



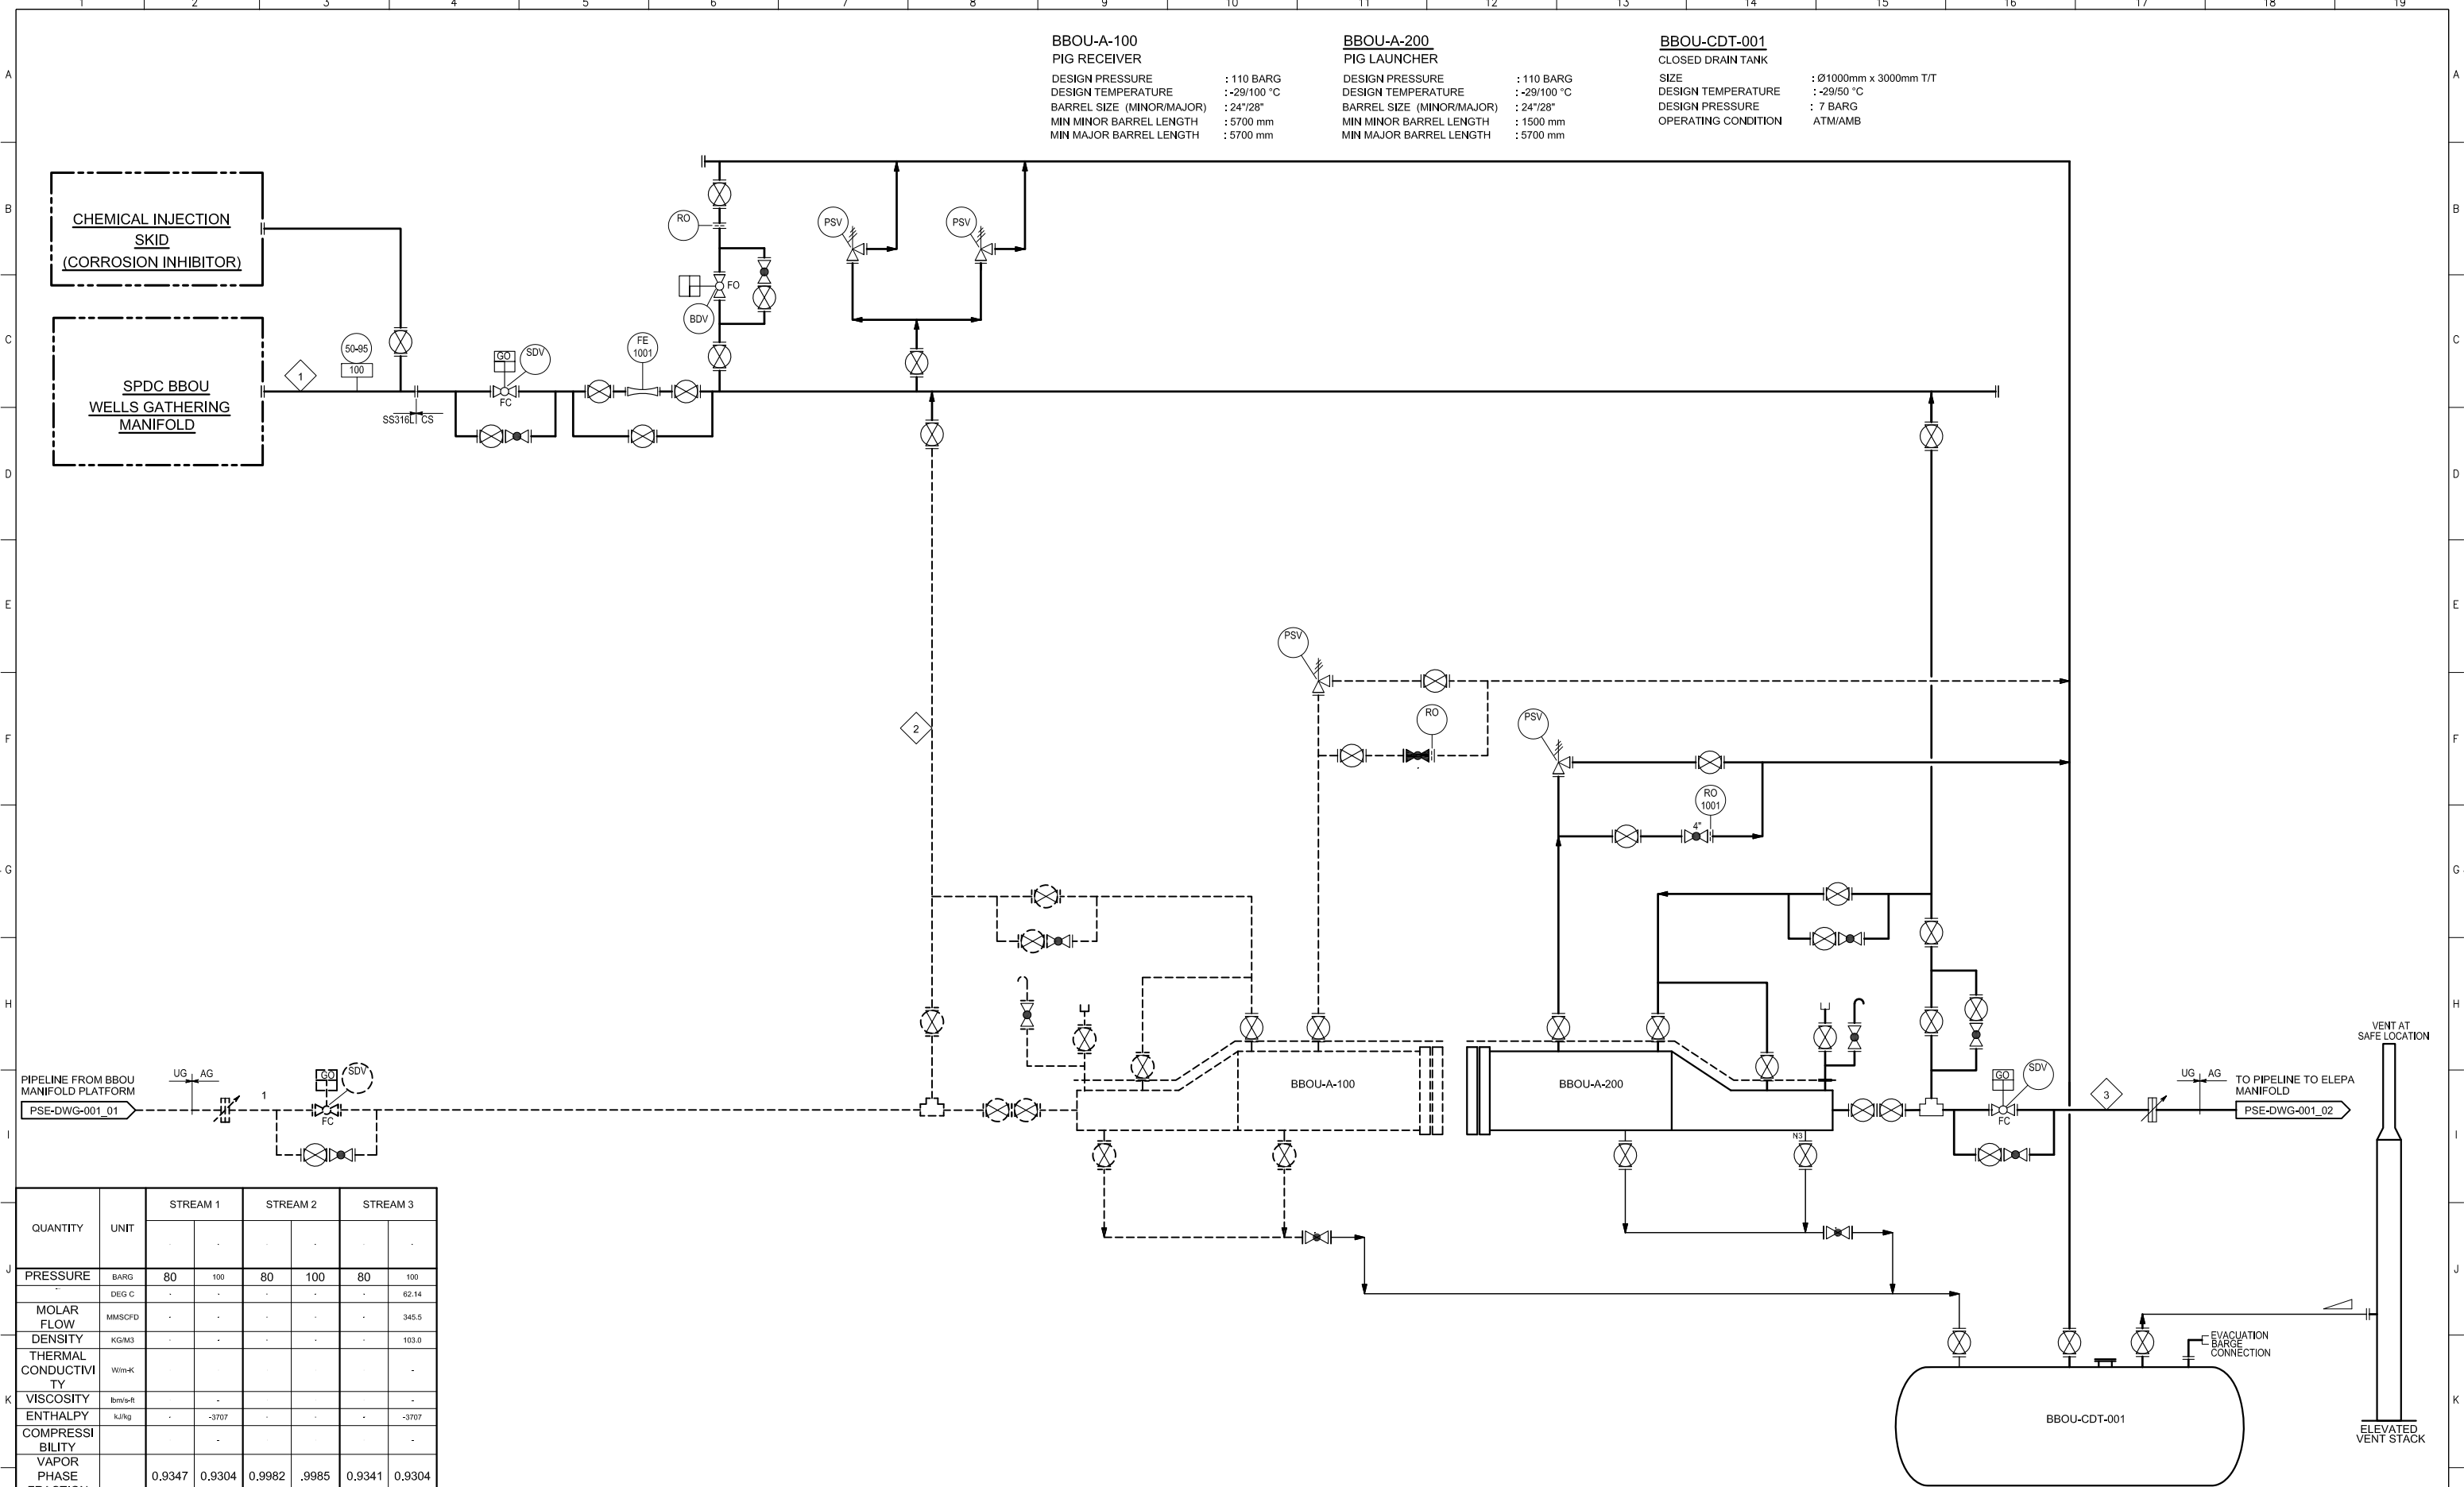

	QUANTITY	UNIT	STREAM 1		STREAM 2		STREAM 3	
J	PRESSURE	BARG	80	100	80	100	80	100
		DEG C	-	-	-	-	-	62.14
	MOLAR FLOW	MMSCFD	-	-	-	-	-	345.5
K	DENSITY	KG/M3	-	-	-	-	-	103.0
	THERMAL CONDUCTIVITY	W/m-K						-
	VISCOSITY	lbm/ft ²		-				-
	ENTHALPY	KJ/kg	-	-3707	-	-	-	-3707
	COMPRESSIBILITY			-				-
	VAPOR PHASE FRACTION		0.9347	0.9304	0.9982	.9985	0.9341	0.9304

[illegible]

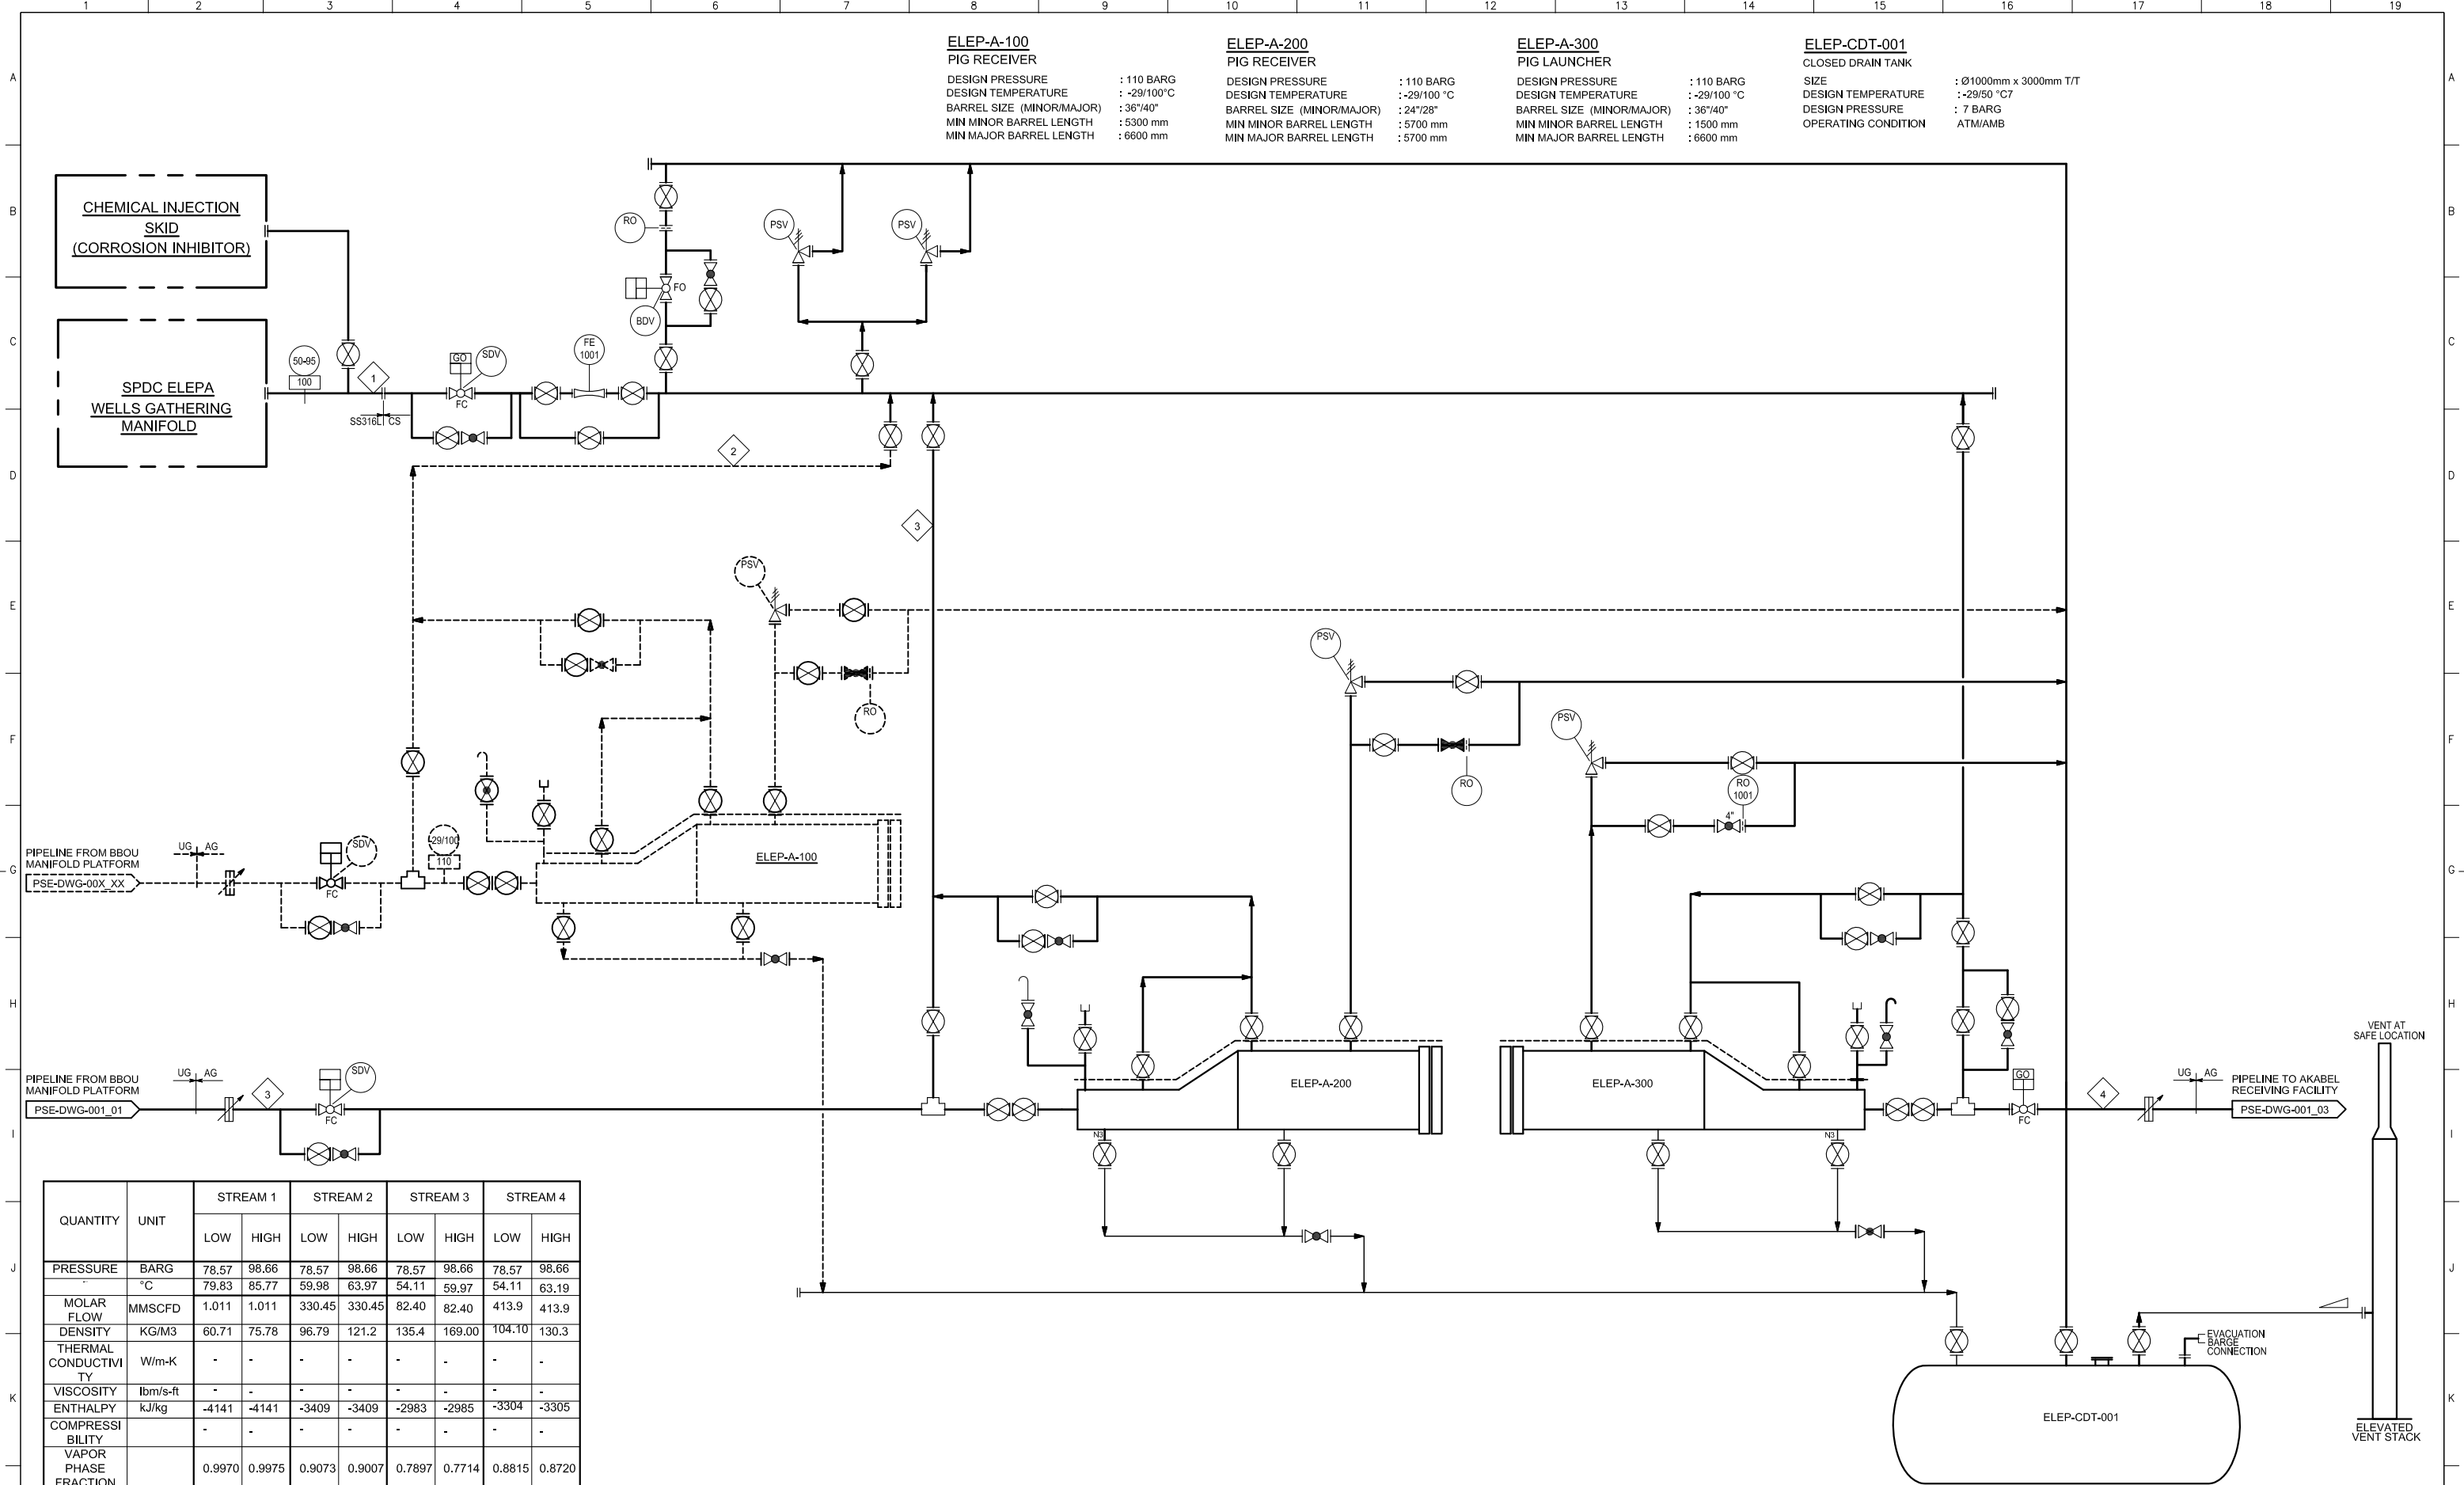

QUANTITY	UNIT	STREAM 1		STREAM 2		STREAM 3		STREAM 4	
		LOW	HIGH	LOW	HIGH	LOW	HIGH	LOW	HIGH
PRESSURE	BARG	78.57	98.66	78.57	98.66	78.57	98.66	78.57	98.66
	°C	79.83	85.77	59.98	63.97	54.11	59.97	54.11	63.19
MOLAR FLOW	MMSCFD	1.011	1.011	330.45	330.45	82.40	82.40	413.9	413.9
DENSITY	KG/M3	60.71	75.78	96.79	121.2	135.4	169.00	104.10	130.3
THERMAL CONDUCTIVITY	W/m-K	-	-	-	-	-	-	-	-
VISCOSITY	lbm/s-ft	-	-	-	-	-	-	-	-
ENTHALPY	kJ/kg	-4141	-4141	-3409	-3409	-2983	-2985	-3304	-3305
COMPRESSIBILITY		-	-	-	-	-	-	-	-
VAPOR PHASE FRACTION		0.9970	0.9975	0.9073	0.9007	0.7897	0.7714	0.8815	0.8720

REFERENCE DRAWINGS

DRAWING No.

NOTES:

CONTRACTOR

BRASS FERTILIZER & PETROCHEMICAL COMPANY LIMITED

GAS PROCESSING AND METHANOL COMPLEX PROJECT
FEED FOR GAS GATHERING PIPELINES

PROCESS SYSTEMS ENGINEERING
PROCESS FLOW SHEETS (PFS)
ELEPA MANIFOLD PLATFORM

DRAWN: RO

DATE: 21.OCT.2022

SHEET: 2 OF 3

CHECKED: KY

DRAWING No. EA-BFPC-L-GPMC-GGPL-FEED-PSE-DWG-001_2

REV. A01

ENDORSED: AD


PROJECT No. 11998A

APP'D DATE: 12.DEC.2022

PROJECT No.

A01	APPROVED FOR DESIGN	FA	OJ	AD	12.12.2022
R03	ISSUED FOR REVIEW	FA	OJ	AD	21.10.2022
R02	ISSUED FOR REVIEW	FA	OJ	AD	08.09.2022
R01	ISSUED FOR REVIEW	BA	KY	AD	17.05.2022
R00	ISSUE FOR IDC	RO	KY	AD	25.04.2022
REV		DRAWN	CHK	END	DATE

COPY RIGHT RESERVED

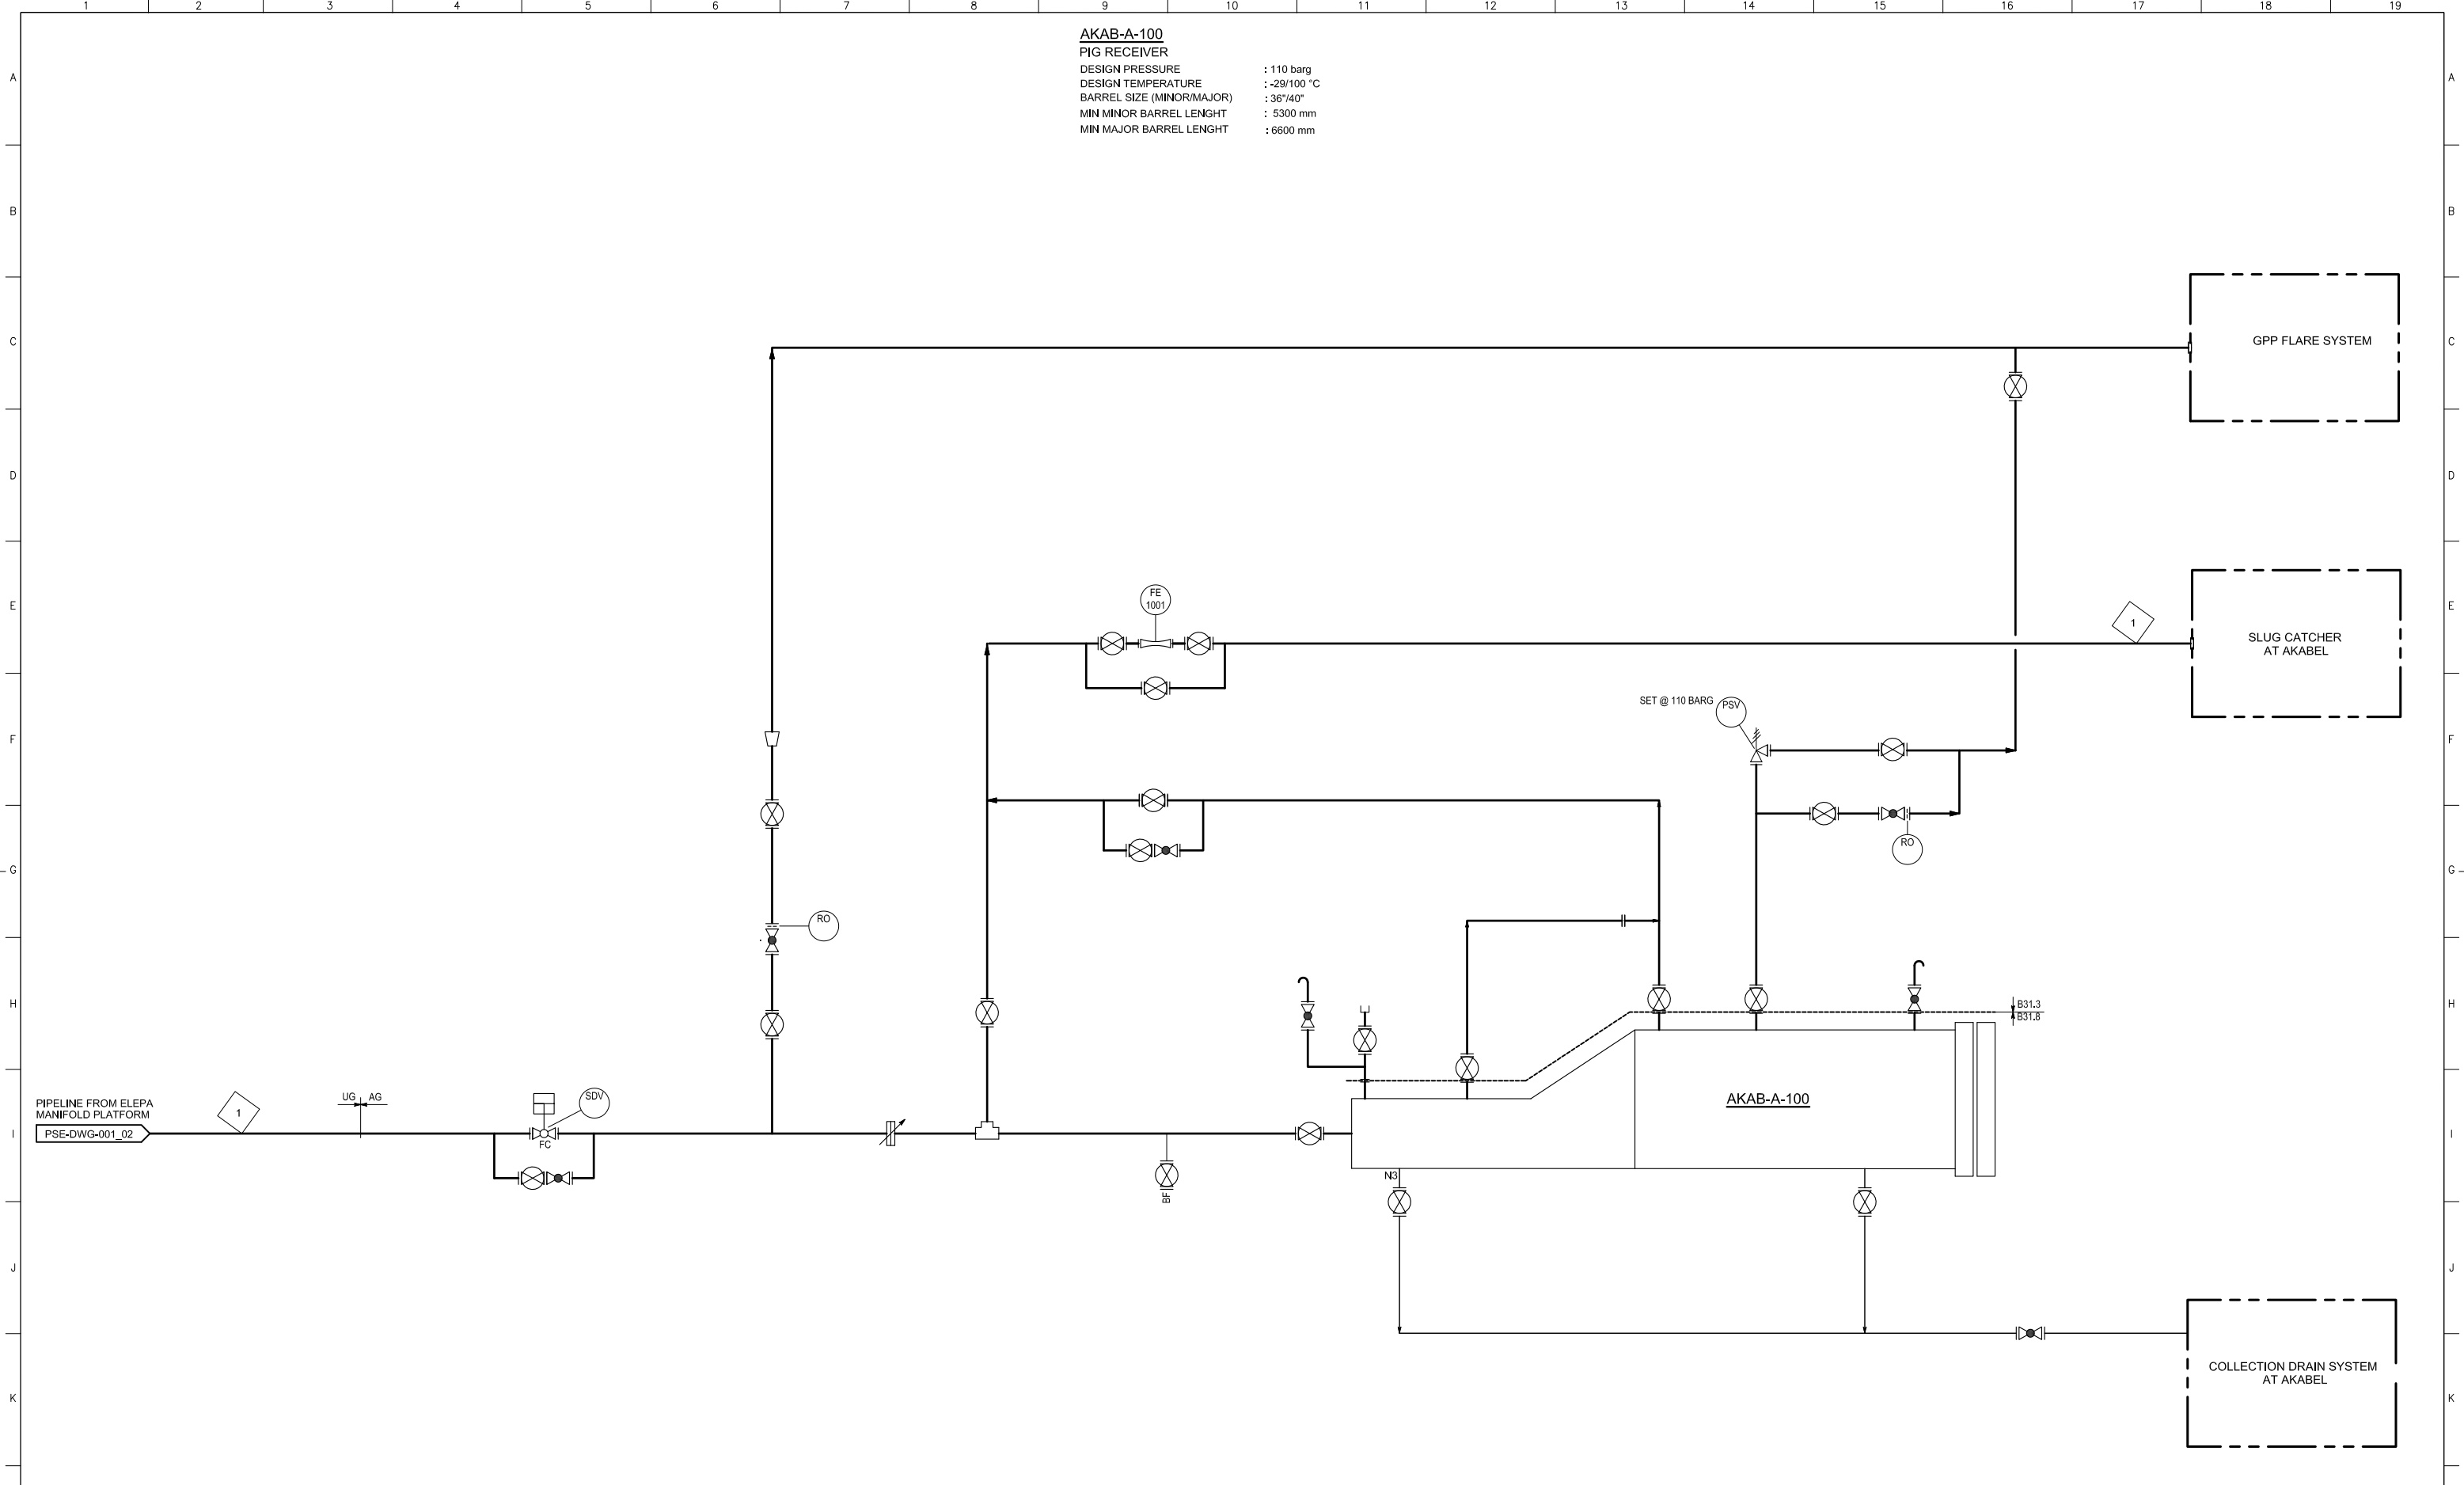

REFERENCE DRAWINGS		DRAWING No.	NOTES:				CONTRACTOR					BRASS FERTILIZER & PETROCHEMICAL COMPANY LIMITED						
												GAS PROCESSING AND METHANOL COMPLEX PROJECT FEED FOR GAS GATHERING PIPELINES						
												PROCESS SYSTEMS ENGINEERING PROCESS FLOW SHEETS (PFS) AKABEL RECEIVING FACILITY						
							ENDORSEMENT					DRAWN: RO						
							RELEASED FOR					CHECKED: KY						
							DESIGN ENGR.					DRAWING No. EA-BFPCL-GPMC-GGPL-FEED-PSE-DWG-001_3						
							BFPCL TECH REP					PROJECT No. 11998A						
							SPDC TECH REP					APP'D DATE: 12.DEC.2022						
							DATE					PROJECT No.						
							REV					A01						
							COPY RIGHT RESERVED											

A01	APPROVED FOR DESIGN	FA	OJ	AD	12.12.2022
R03	ISSUED FOR REVIEW	FA	OJ	AD	21.10.2022
R02	ISSUED FOR REVIEW	FA	OJ	AD	08.09.2022
R01	ISSUED FOR REVIEW	BA	KY	AD	17.05.2022
R00	ISSUE FOR IDC	RO	KY	AD	25.04.2022
REV		DRAWN	CHK	END	DATE

1	2	3	4	5	6	7	8	9	10	11	12	13	14	15	16	17	18	19
---	---	---	---	---	---	---	---	---	----	----	----	----	----	----	----	----	----	----