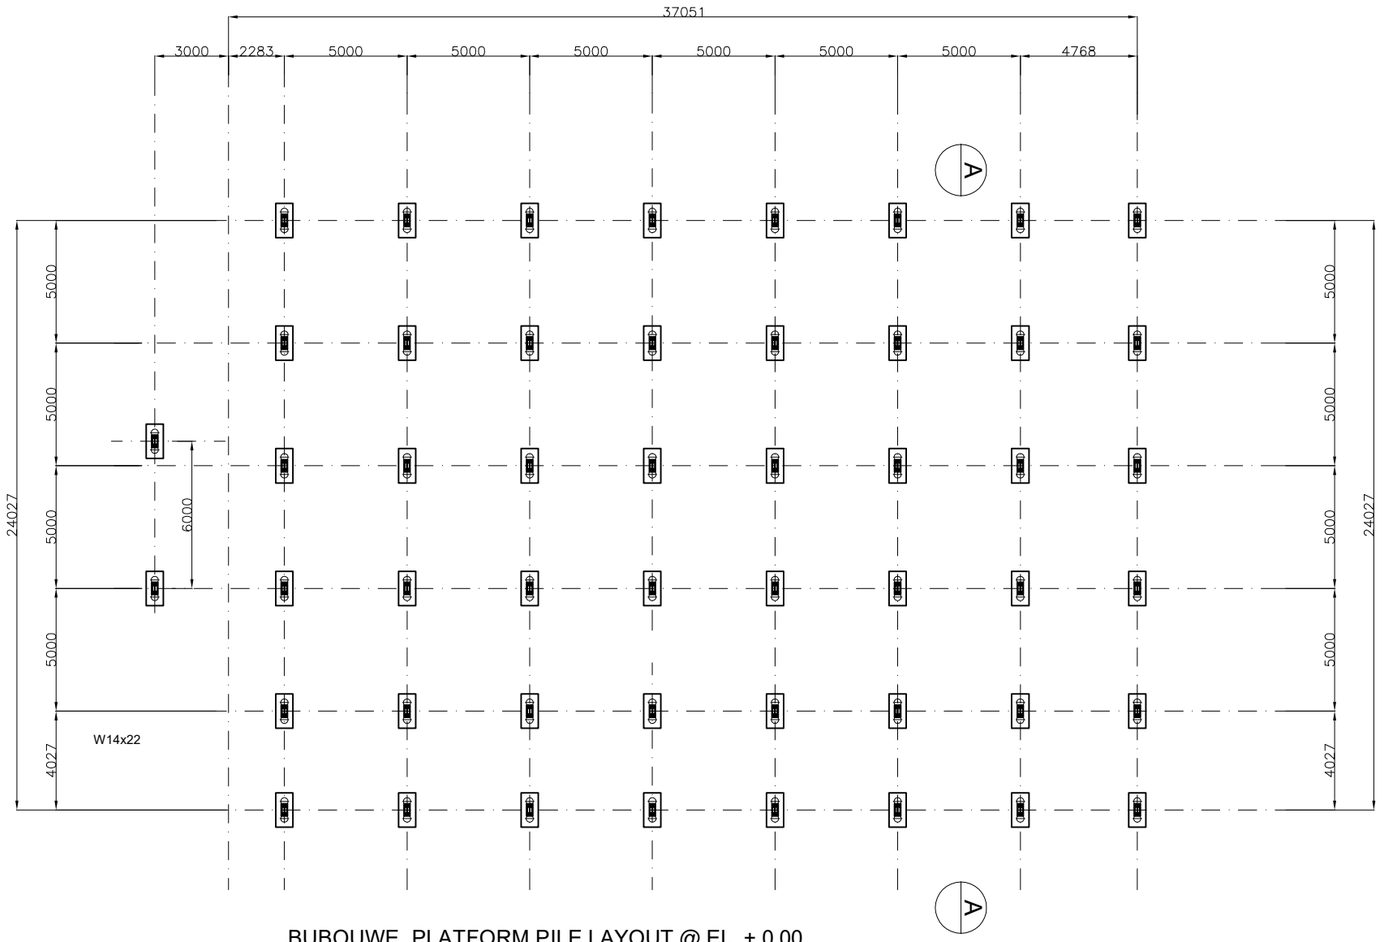

BUBOUWE PLATFORM PILE LAYOUT @ EL. + 0.00

SCALE 1:250

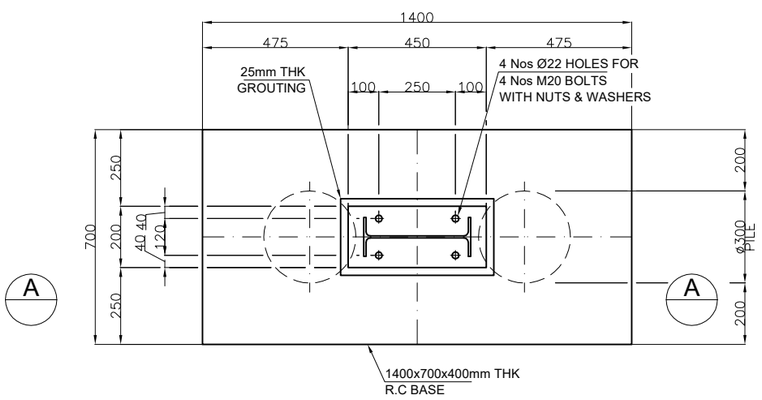

TYPICAL BASE LAYOUT

SCALE 1:20

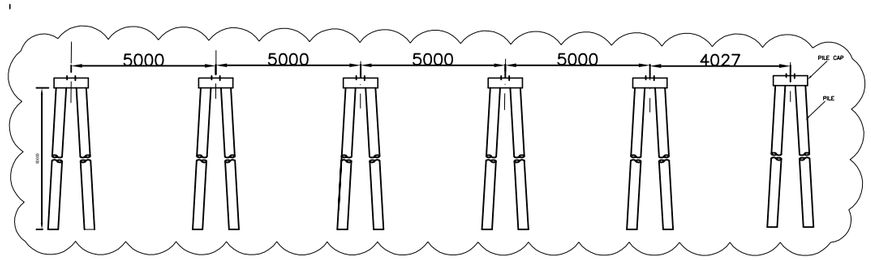

SECTION A - A DETAILS

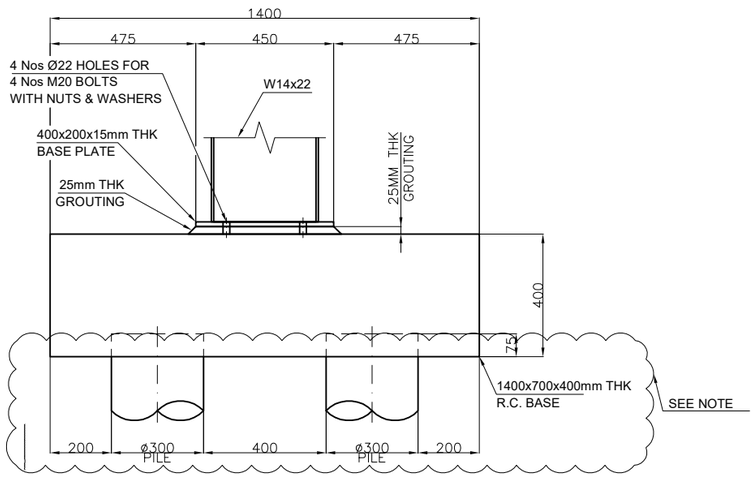

SECTION A- A

SCALE 1:20

ALL DIMENSIONS ARE IN MILLIMETERS UNLESS OTHERWISE STATED.

REFERENCE DRAWINGS	DRAWING No.

NOTES:

1. ALL DIMENSIONS ARE IN MILLIMETERS UNLESS OTHERWISE STATED.
2. PILE DESIGN INFORMATION IN THE SOIL REPORT ISSUED IS NOT ADEQUATE TO CARRY OUT PILE DESIGN.THE DESIGN MAY BE CARRIED OUT AT DED STAGE.

REV		DRAWN	CHK	END	DATE
R01	ISSUED FOR REVIEW	A.O	I.O	I.W	24/06/22

COPY RIGHT RESERVED

CONTRACTOR

epic ATLANTIC

ENDORSEMENT

RELEASED FOR	DESIGN ENGR.	BFPC TECH REP	SPDC TECH REP	DATE
–	–	–	–	–

BRASS FERTILIZER & PETROCHEMICAL COMPANY LIMITED

brass fertilizer

GAS PROCESSING AND METHANOL COMPLEX PROJECT
FEED FOR GAS GATHERING PIPELINES

LOCATION
BUBOUWE
–

DRAWN: A.O	DATE: 06/24/22	SHEET: 1 of 2	
CHECKED: I.O	DRAWING No. EA-BFPCL-GPMC-GGPL-FEED-CIV-DWG-003		REV.
ENDORSED: I.W	PROJECT No. –		–
APP'D DATE: –	PROJECT No. –		

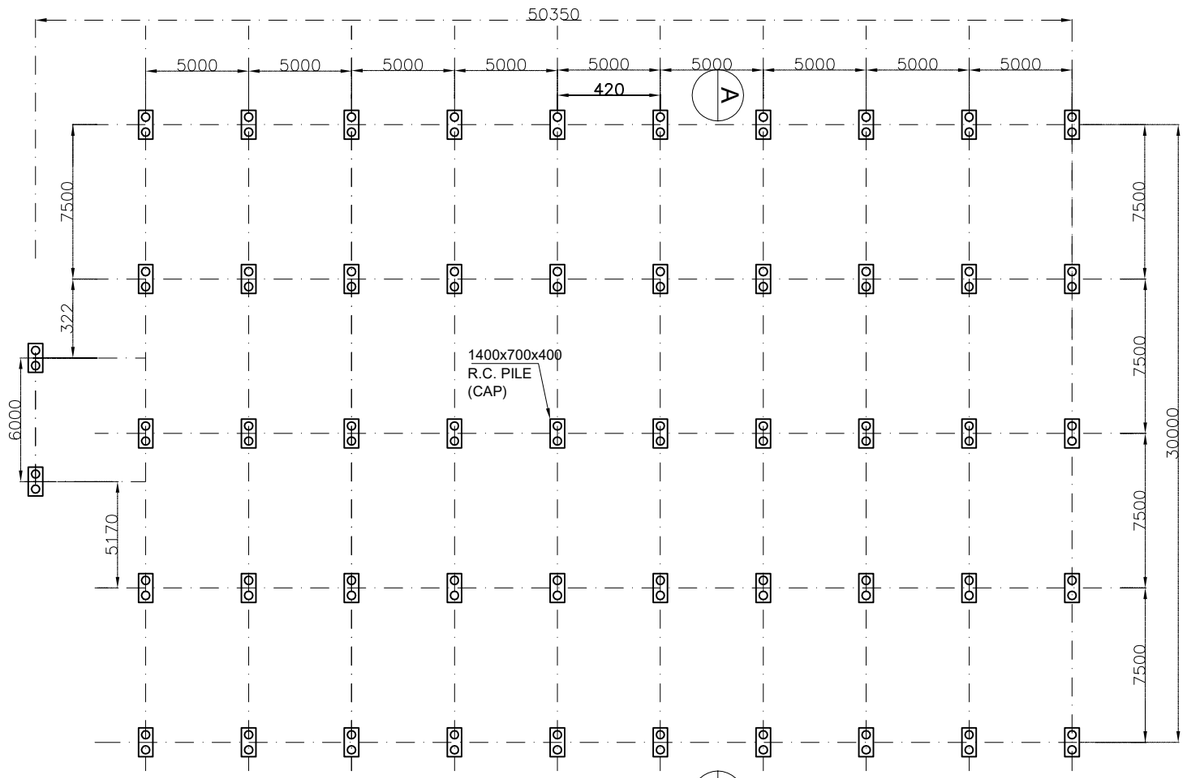

ELEPA PILE ARRANGEMENT @ EL. + 0.00

SCALE 1:150

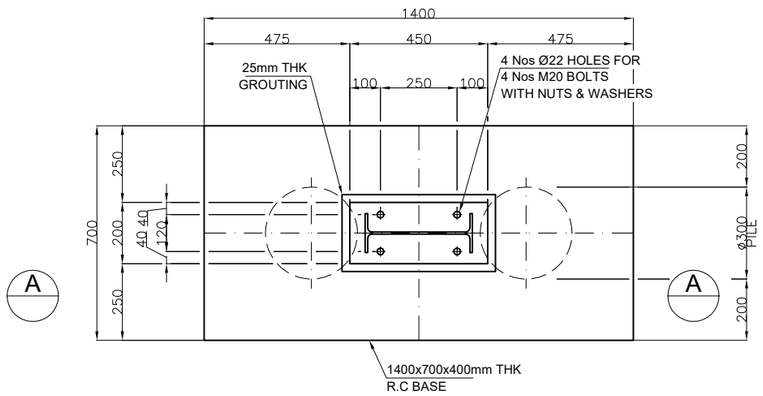

TYPICAL BASE LAYOUT

SCALE 1:20

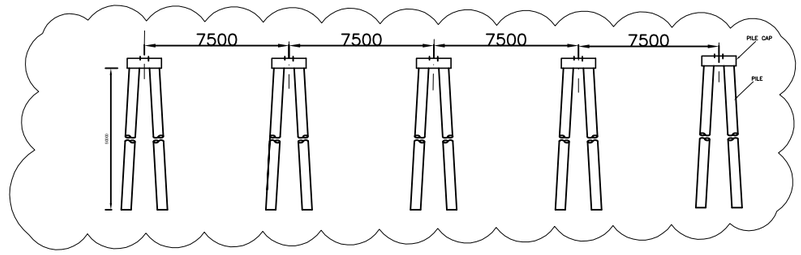

SECTION A - A DETAILS

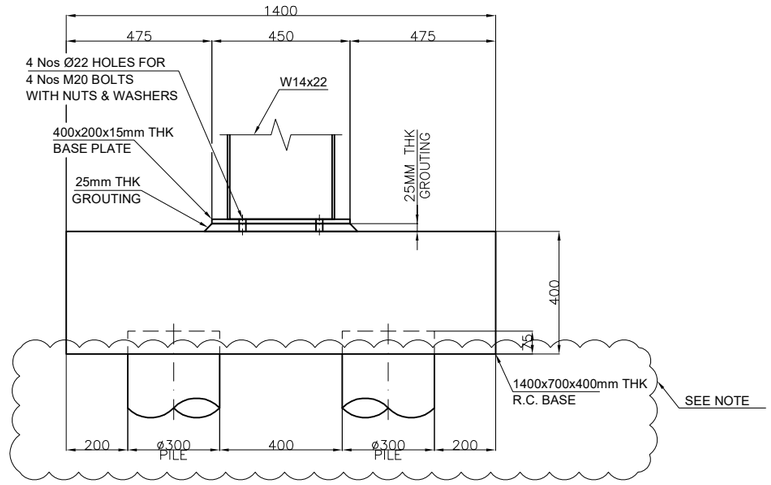

SECTION A- A

SCALE 1:20

REFERENCE DRAWINGS	DRAWING No.

NOTES:

1. ALL DIMENSIONS ARE IN MILLIMETERS UNLESS OTHERWISE STATED.
2. PILE DESIGN INFORMATION IN THE SOIL REPORT ISSUED IS NOT ADEQUATE TO CARRY OUT PILE DESIGN.THE DESIGN MAY BE CARRIED OUT AT DED STAGE.

REV		DRAWN	CHK	END	DATE
R01	ISSUED FOR REVIEW	A.O	I.O	I.W	24/06/22

COPY RIGHT RESERVED

CONTRACTOR

epic ATLANTIC

ENDORSEMENT				
RELEASED FOR	DESIGN ENGR.	BFPC TECH REP	SPDC TECH REP	DATE
–	–	–	–	–

BRASS FERTILIZER & PETROCHEMICAL COMPANY LIMITED

brass fertilizer

GAS PROCESSING AND METHANOL COMPLEX PROJECT
FEED FOR GAS GATHERING PIPELINES

LOCATION
ELEPA
–

DRAWN: A.O	DATE: 06/24/22	SHEET: 2 of 2	
CHECKED: I.O	DRAWING No. EA-BFPCL-GPMC-GGPL-FEED-CIV-DWG-003		REV.
ENDORSED: I.W	PROJECT No. –		–
APP'D DATE: –	PROJECT No. –		