



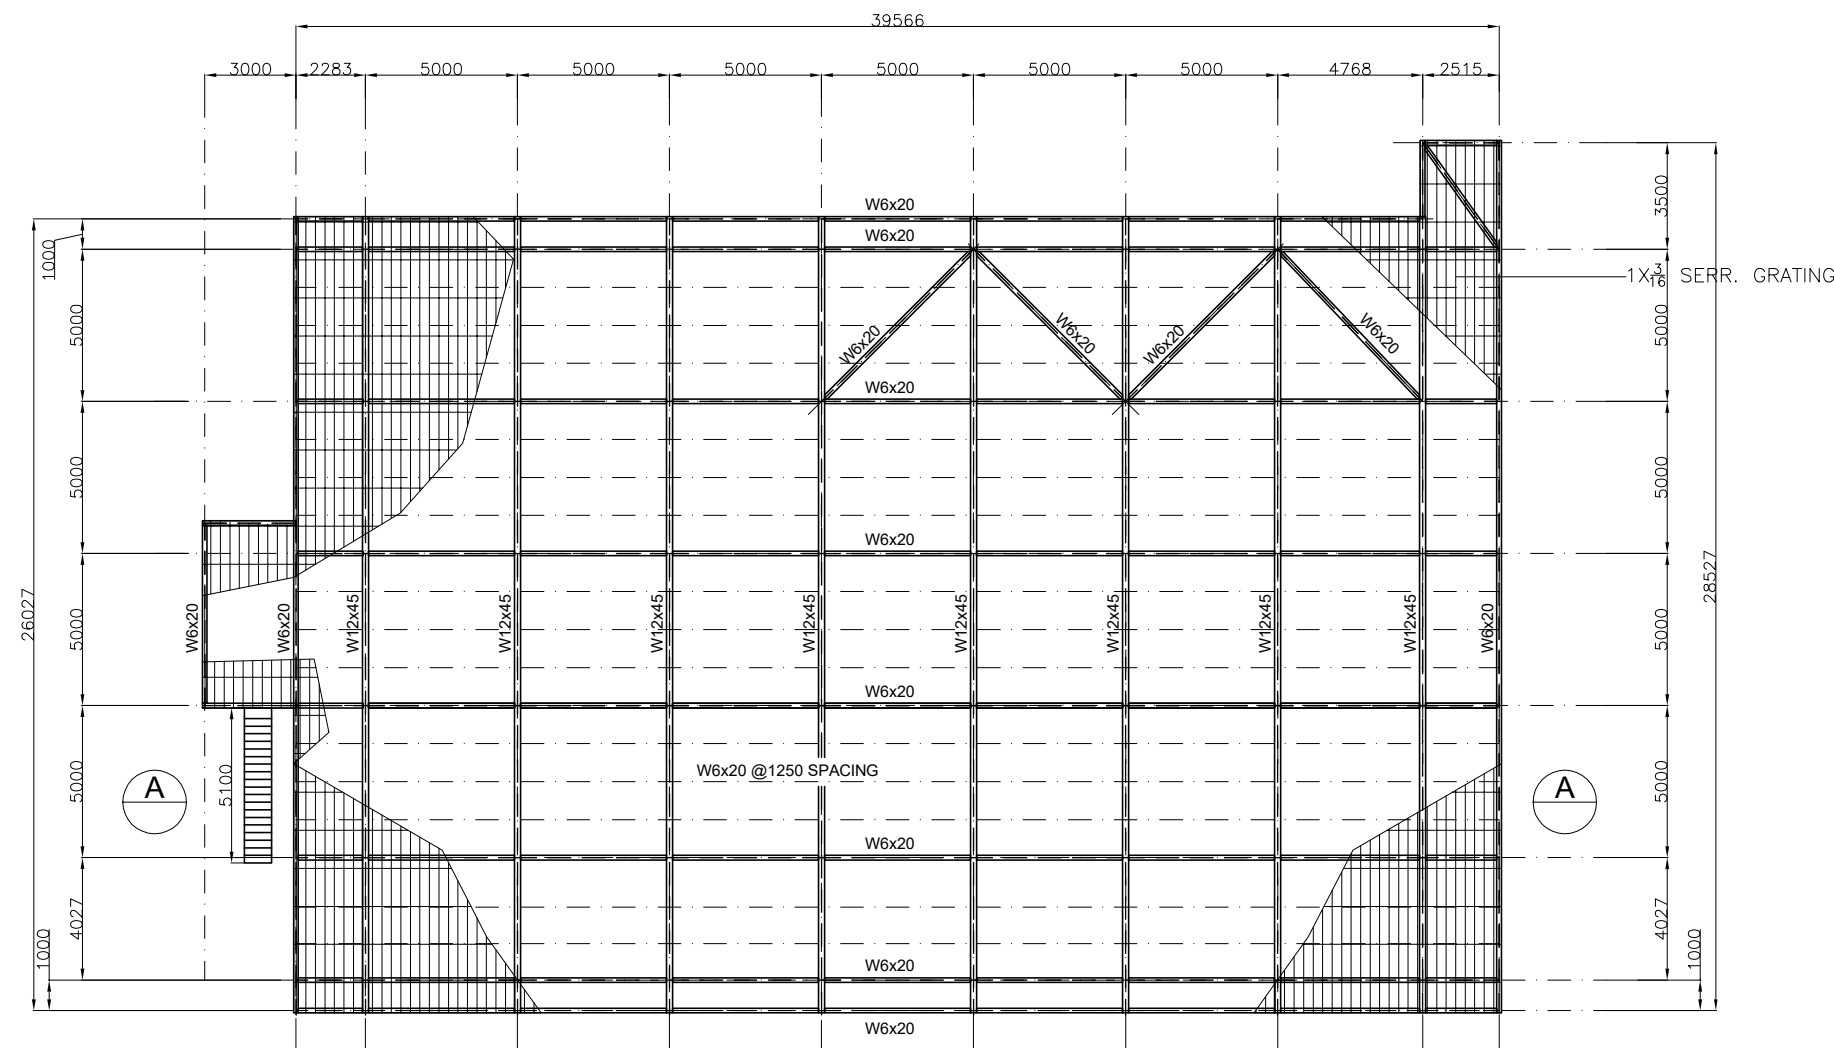


BUBOUWE PLATFORM FRAMING PLAN @ EL. + 3000
SCALE 1:250

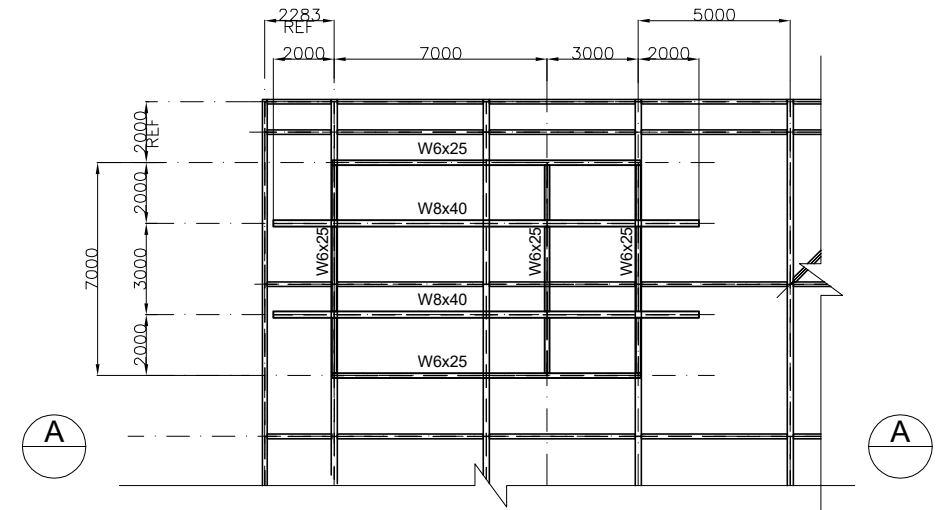

FRAMING PLAN @ EL. + 6000

SCALE 1:250



SECTIONS	TOTAL LENGTH (m)	UNIT WEIGHTH (kg/m) or (kg/m2)	TOTAL WEIGHTH
W6X20	917.8	29.76	27,313.73
W6X25	34.0	37.2	1264.80
W8X40	28.0	59.2	1657.60
W12X45	28.0	66.9	1873.20
W14X22	162.0	59.5	9639.00
C8X13	24.9	19.3	480.57
1X3/16 GRAT	1060.0 m2		

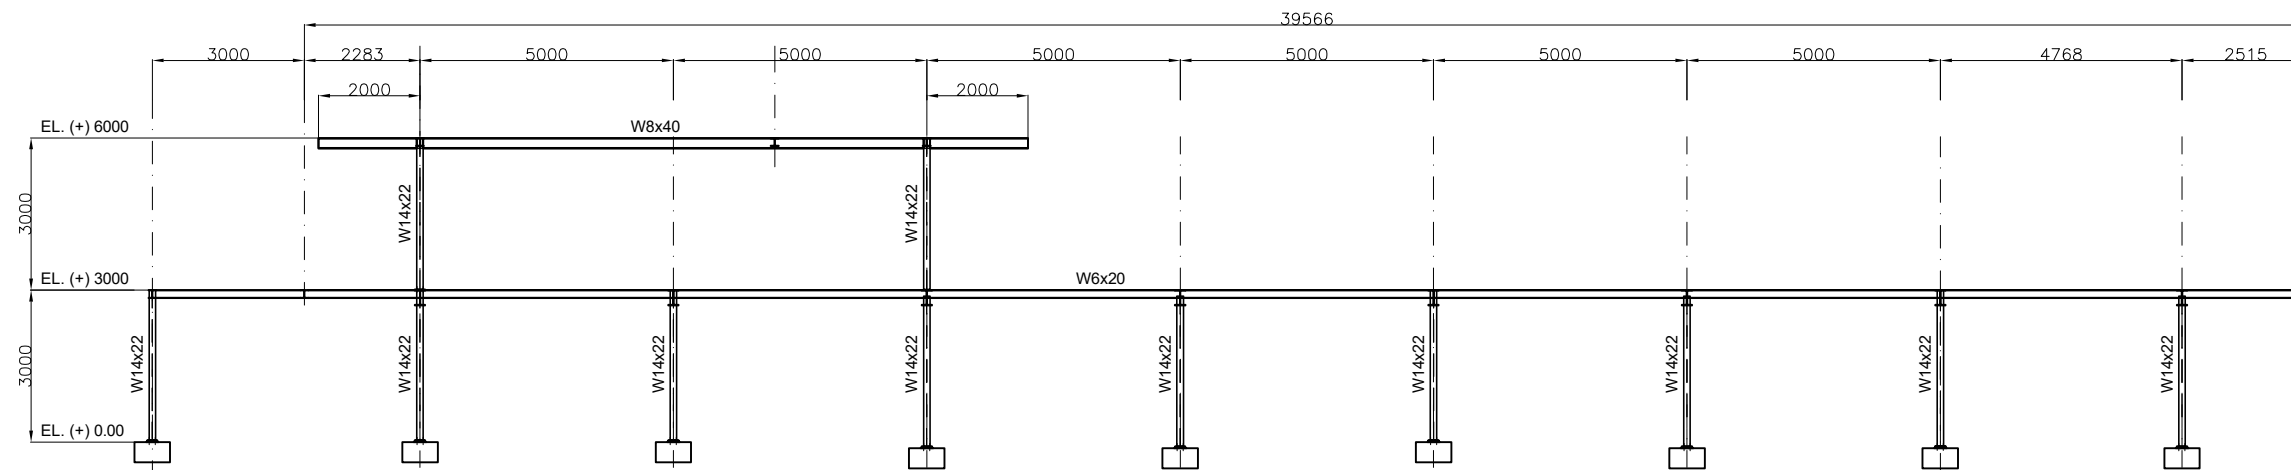


SECTION A- A
SCALE 1:150

ALL DIMENSIONS ARE IN MILLIMETERS UNLESS OTHERWISE STATED.

[illegible]

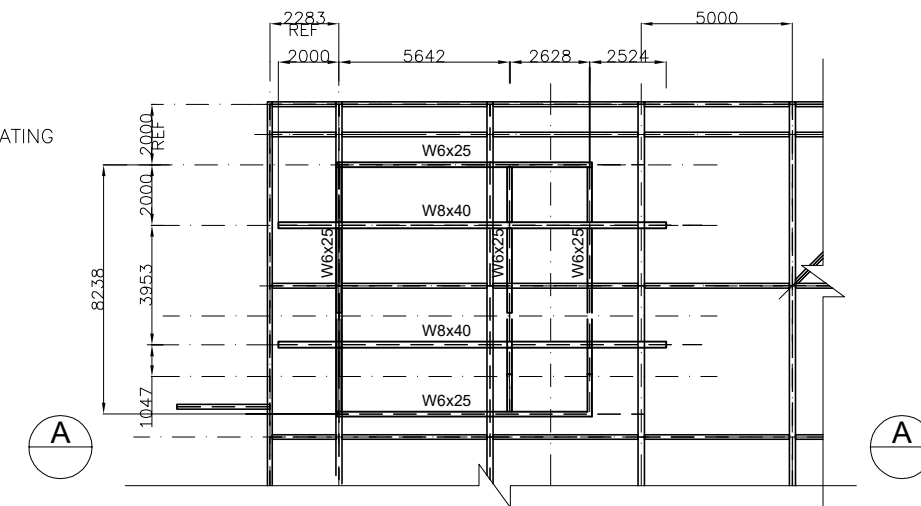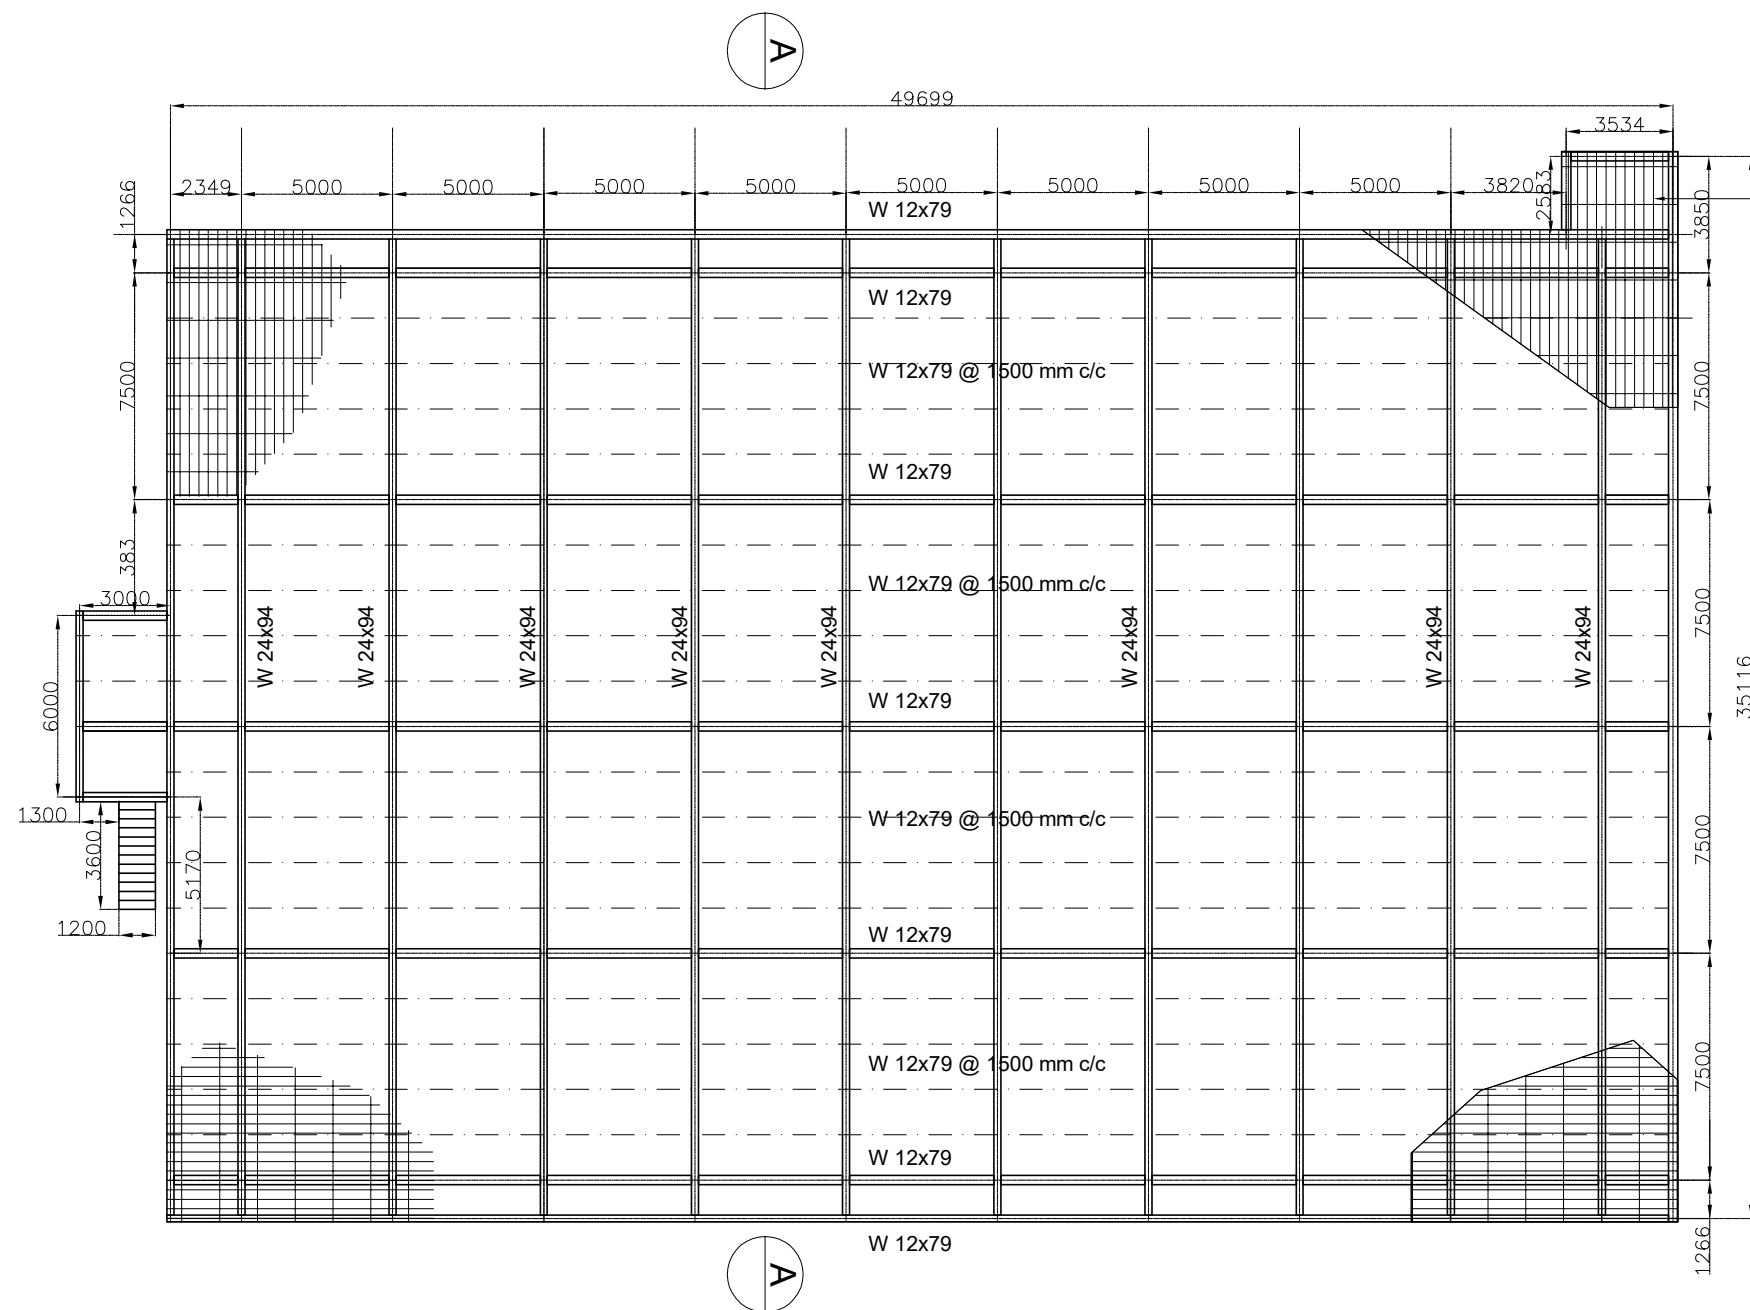

SECTIONS	TOTAL LENGTH (m)	UNIT WEIGHTH (kg/m) or (kg/m2)	TOTAL WEIGHTH
W8X40	42.00	59.20	2486.4
W12X79	1292.80	117.60	152.03
W14X48	168.00	71.43	12000.24
W24X94	325.00	139.80	45435.00
C8X13	24.90	19.30	480.57
1X3/16 GRAT	1673.88m2		

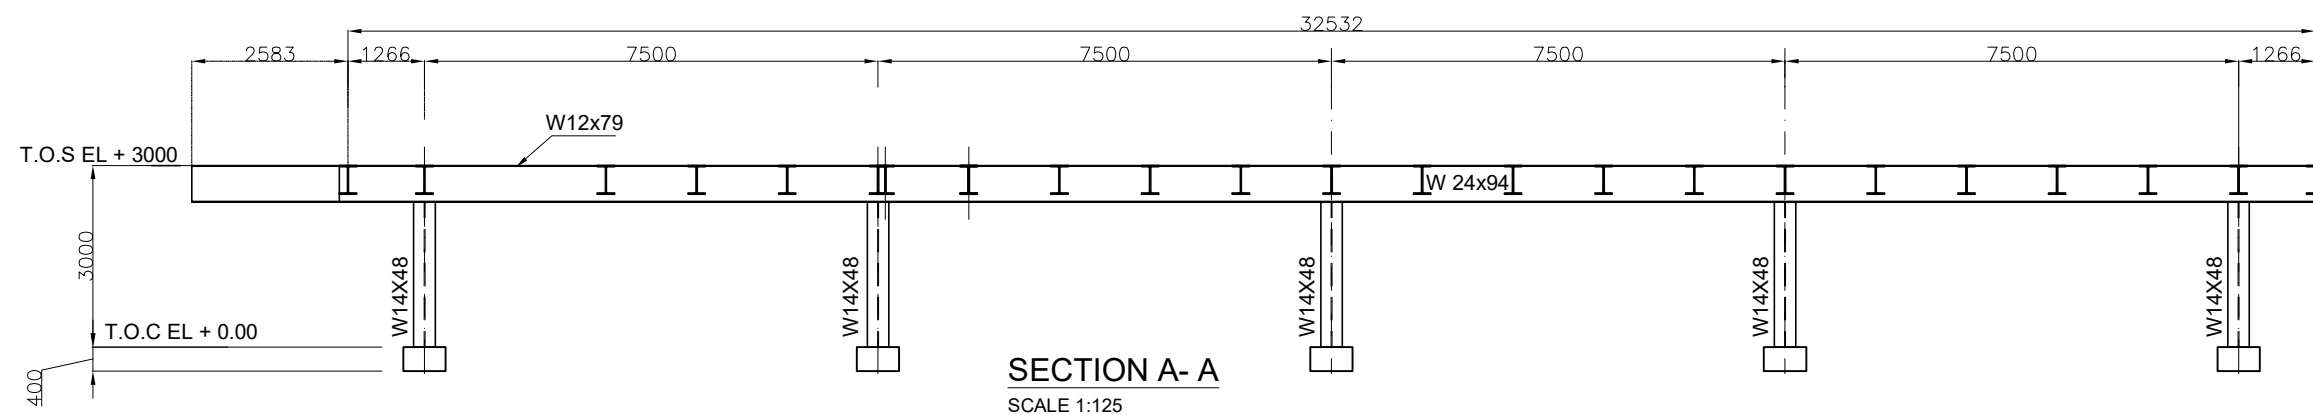[illegible]