


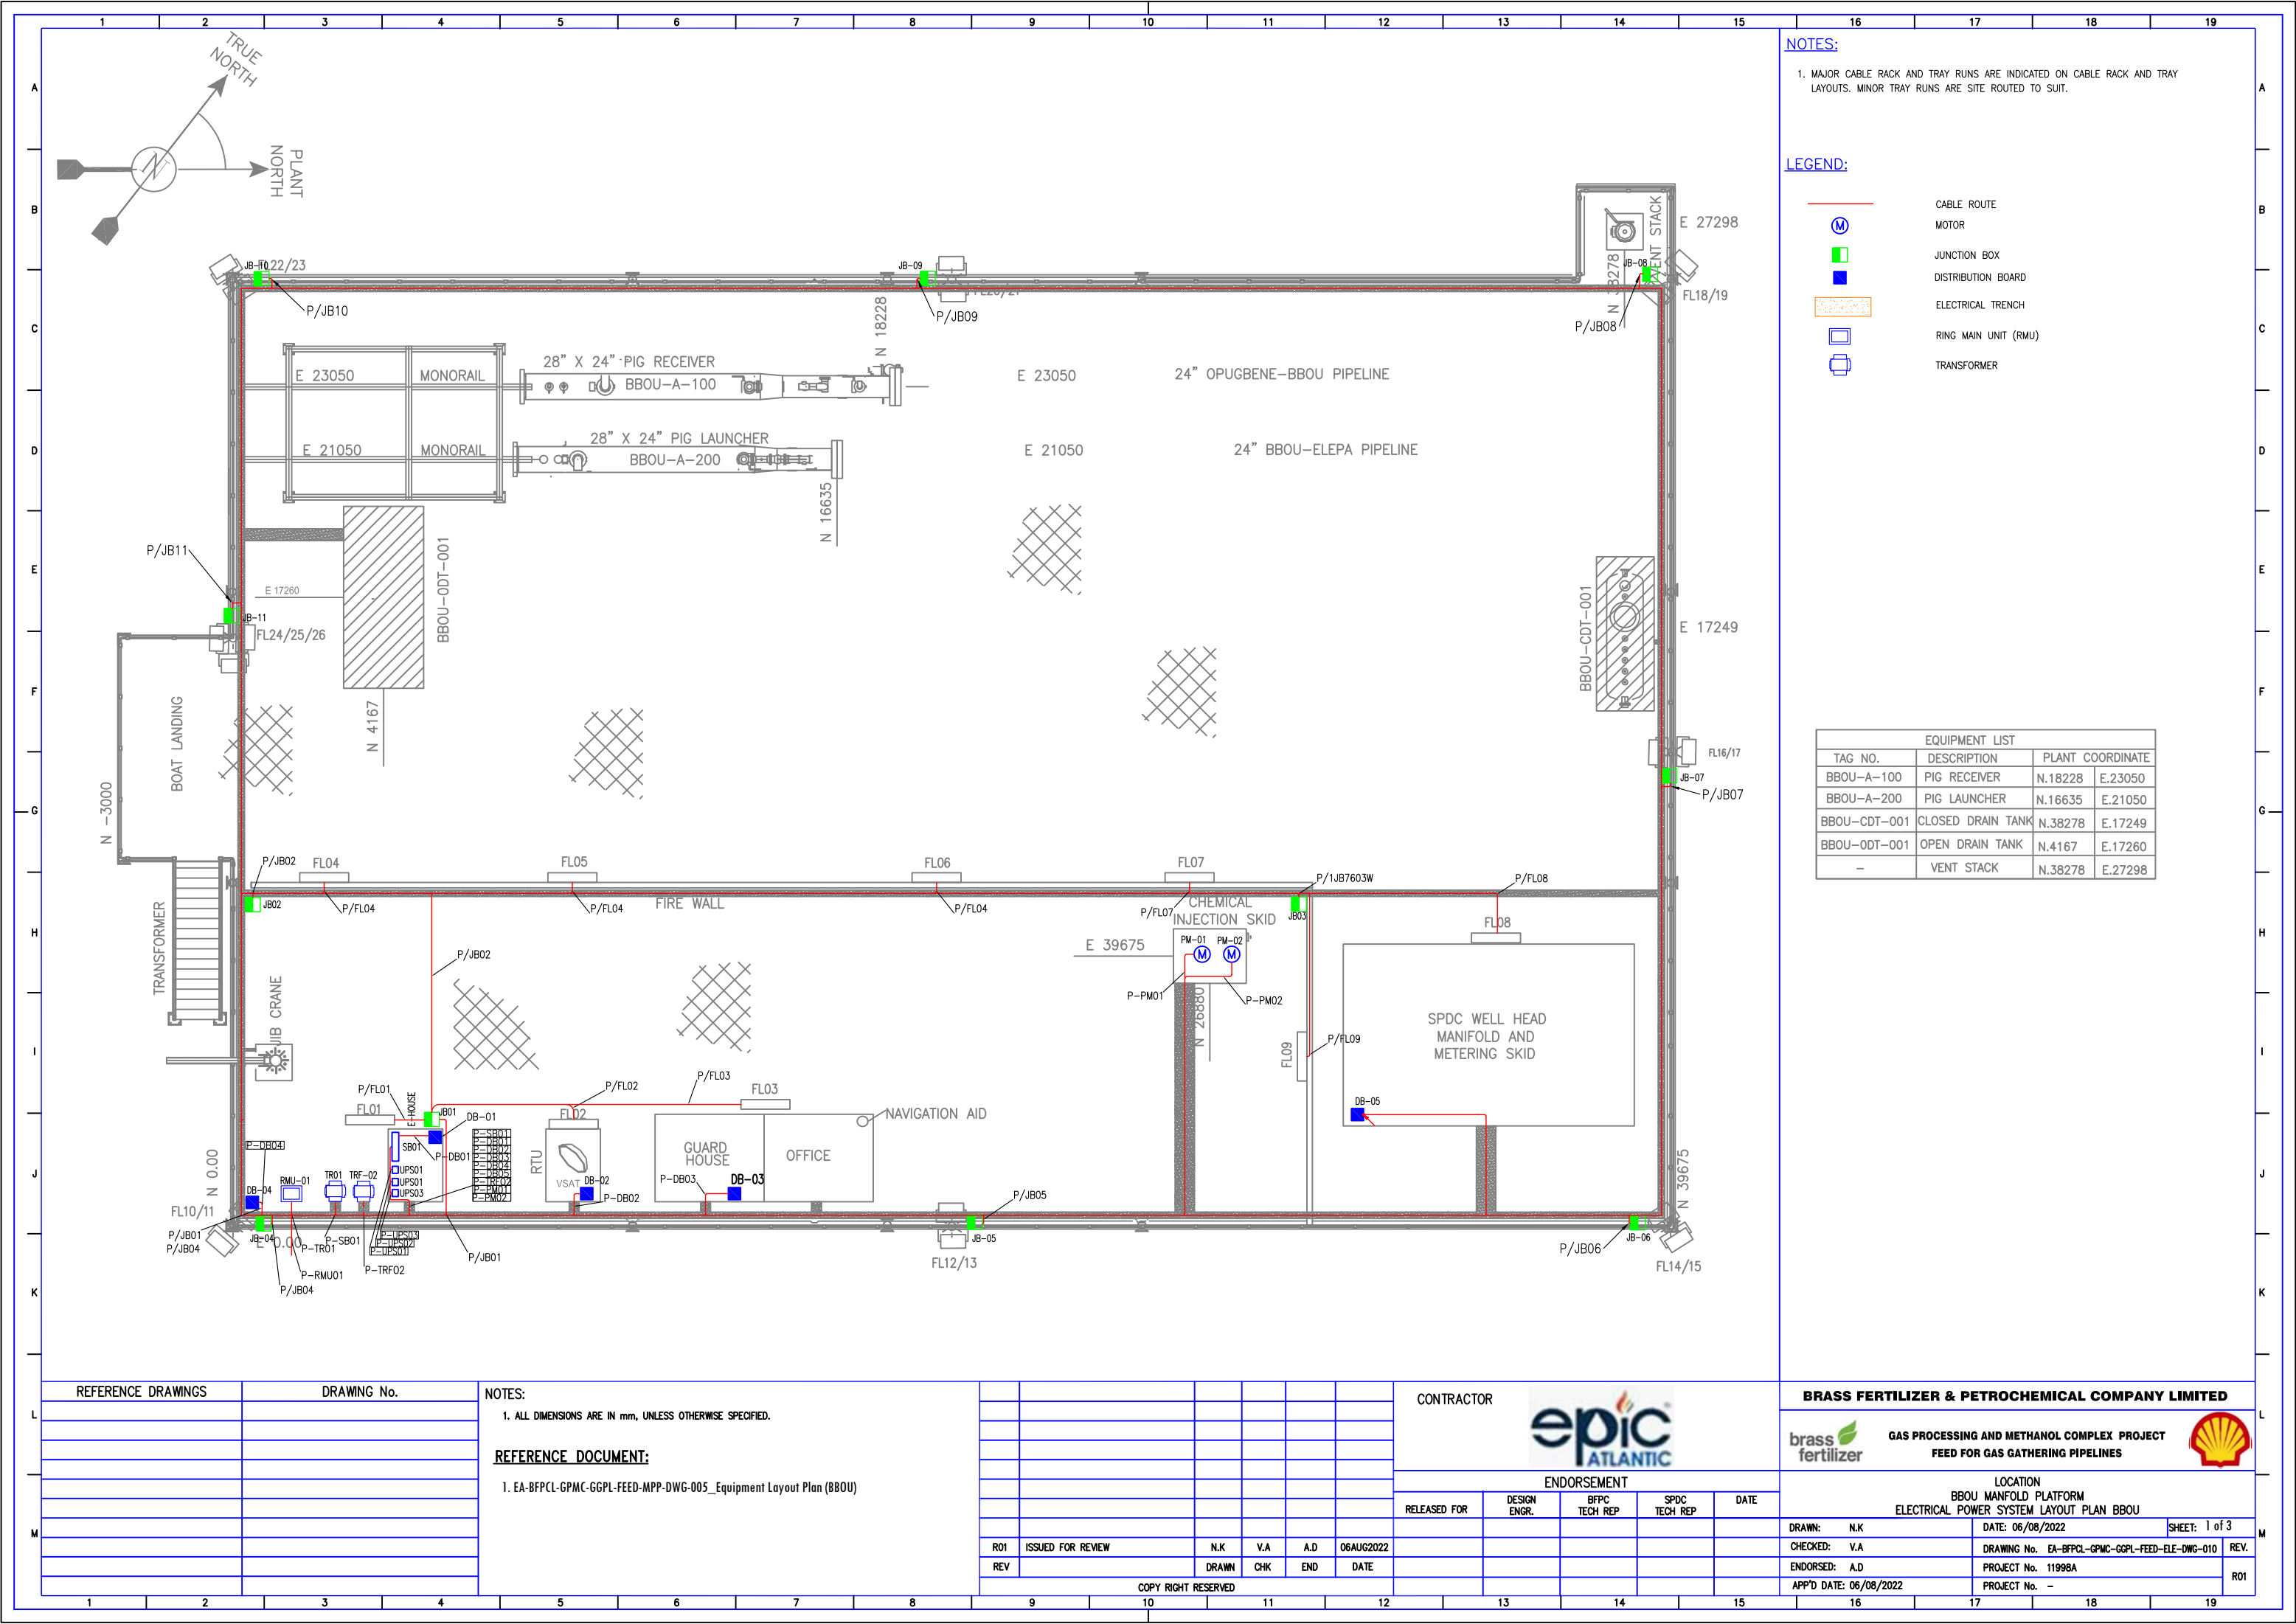

NOTES:

1. MAJOR CABLE RACK AND TRAY RUNS ARE INDICATED ON CABLE RACK AND TRAY LAYOUTS. MINOR TRAY RUNS ARE SITE ROUTED TO SUIT.

- LEGEND:**
- CABLE ROUTE
 - MOTOR
 - JUNCTION BOX
 - DISTRIBUTION BOARD
 - ELECTRICAL TRENCH
 - RING MAIN UNIT (RMU)
 - TRANSFORMER

EQUIPMENT LIST			
TAG NO.	DESCRIPTION	PLANT COORDINATE	
BBOU-A-100	PIG RECEIVER	N.18228	E.23050
BBOU-A-200	PIG LAUNCHER	N.16635	E.21050
BBOU-CDT-001	CLOSED DRAIN TANK	N.38278	E.17249
BBOU-ODT-001	OPEN DRAIN TANK	N.4167	E.17260
-	VENT STACK	N.38278	E.27298

REFERENCE DRAWINGS

DRAWING No.

NOTES:

1. ALL DIMENSIONS ARE IN mm, UNLESS OTHERWISE SPECIFIED.

REFERENCE DOCUMENT:

1. EA-BFPCL-GPMC-GGPL-FEED-MPP-DWG-005_Equipment Layout Plan (BBOU)

CONTRACTOR

ENDORSEMENT

RELEASED FOR	DESIGN ENGR.	BFPC TECH REP	SPDC TECH REP	DATE
R01 ISSUED FOR REVIEW	N.K	V.A	A.D	06AUG2022
REV	DRAWN	CHK	END	DATE


COPY RIGHT RESERVED

BRASS FERTILIZER & PETROCHEMICAL COMPANY LIMITED

GAS PROCESSING AND METHANOL COMPLEX PROJECT
FEED FOR GAS GATHERING PIPELINES

LOCATION
BBOU MANFOLD PLATFORM
ELECTRICAL POWER SYSTEM LAYOUT PLAN BBOU

DRAWN: N.K	DATE: 06/08/2022	SHEET: 1 of 3
CHECKED: V.A	DRAWING No. EA-BFPCL-GPMC-GGPL-FEED-ELE-DWG-010	REV.
ENDORSED: A.D	PROJECT No. 11998A	R01
APP'D DATE: 06/08/2022	PROJECT No. -	

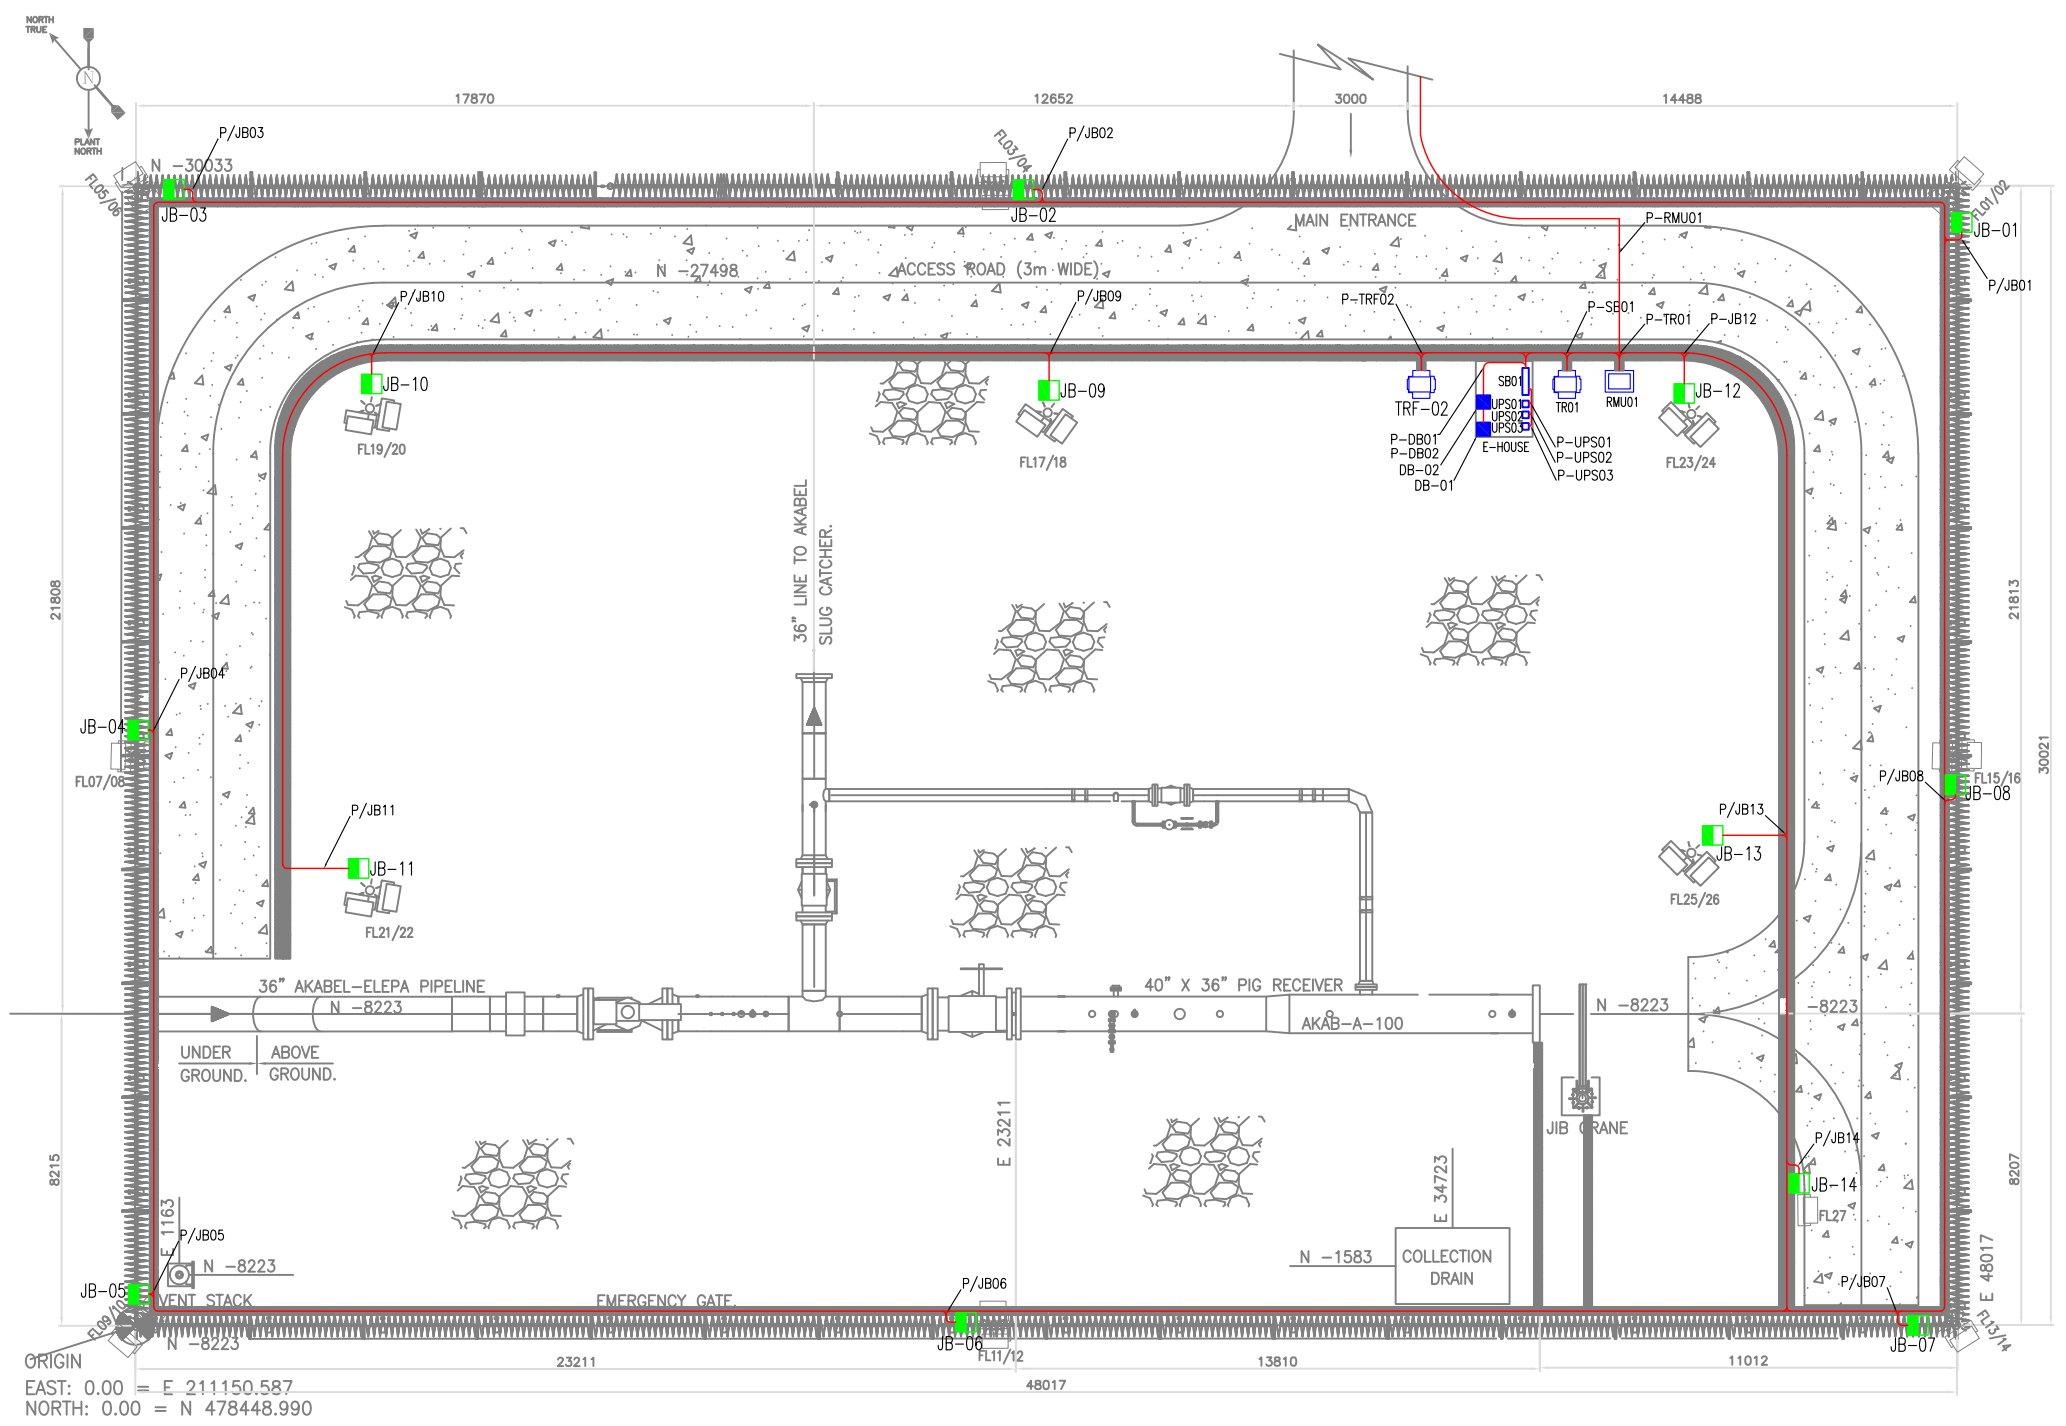

- NOTES:**
1. MAJOR CABLE RACK AND TRAY RUNS ARE INDICATED ON CABLE RACK AND TRAY LAYOUTS. MINOR TRAY RUNS ARE SITE ROUTED TO SUIT.
- LEGEND:**
- CABLE ROUTE
 - JUNCTION BOX
 - DISTRIBUTION BOARD
 - ELECTRICAL TRENCH
 - RING MAIN UNIT (RMU)
 - TRANSFORMER

L	REFERENCE DRAWINGS		DRAWING No.		NOTES: ALL DIMENSIONS ARE IN mm, UNLESS OTHERWISE SPECIFIED. <u>REFERENCE DOCUMENT:</u> 1. EA-BFPCL-GPMC-GGPL-FEED-MPP-DWG-007_Equipment Layout Plan (AKABEL)	
---	--------------------	--	-------------	--	--	