



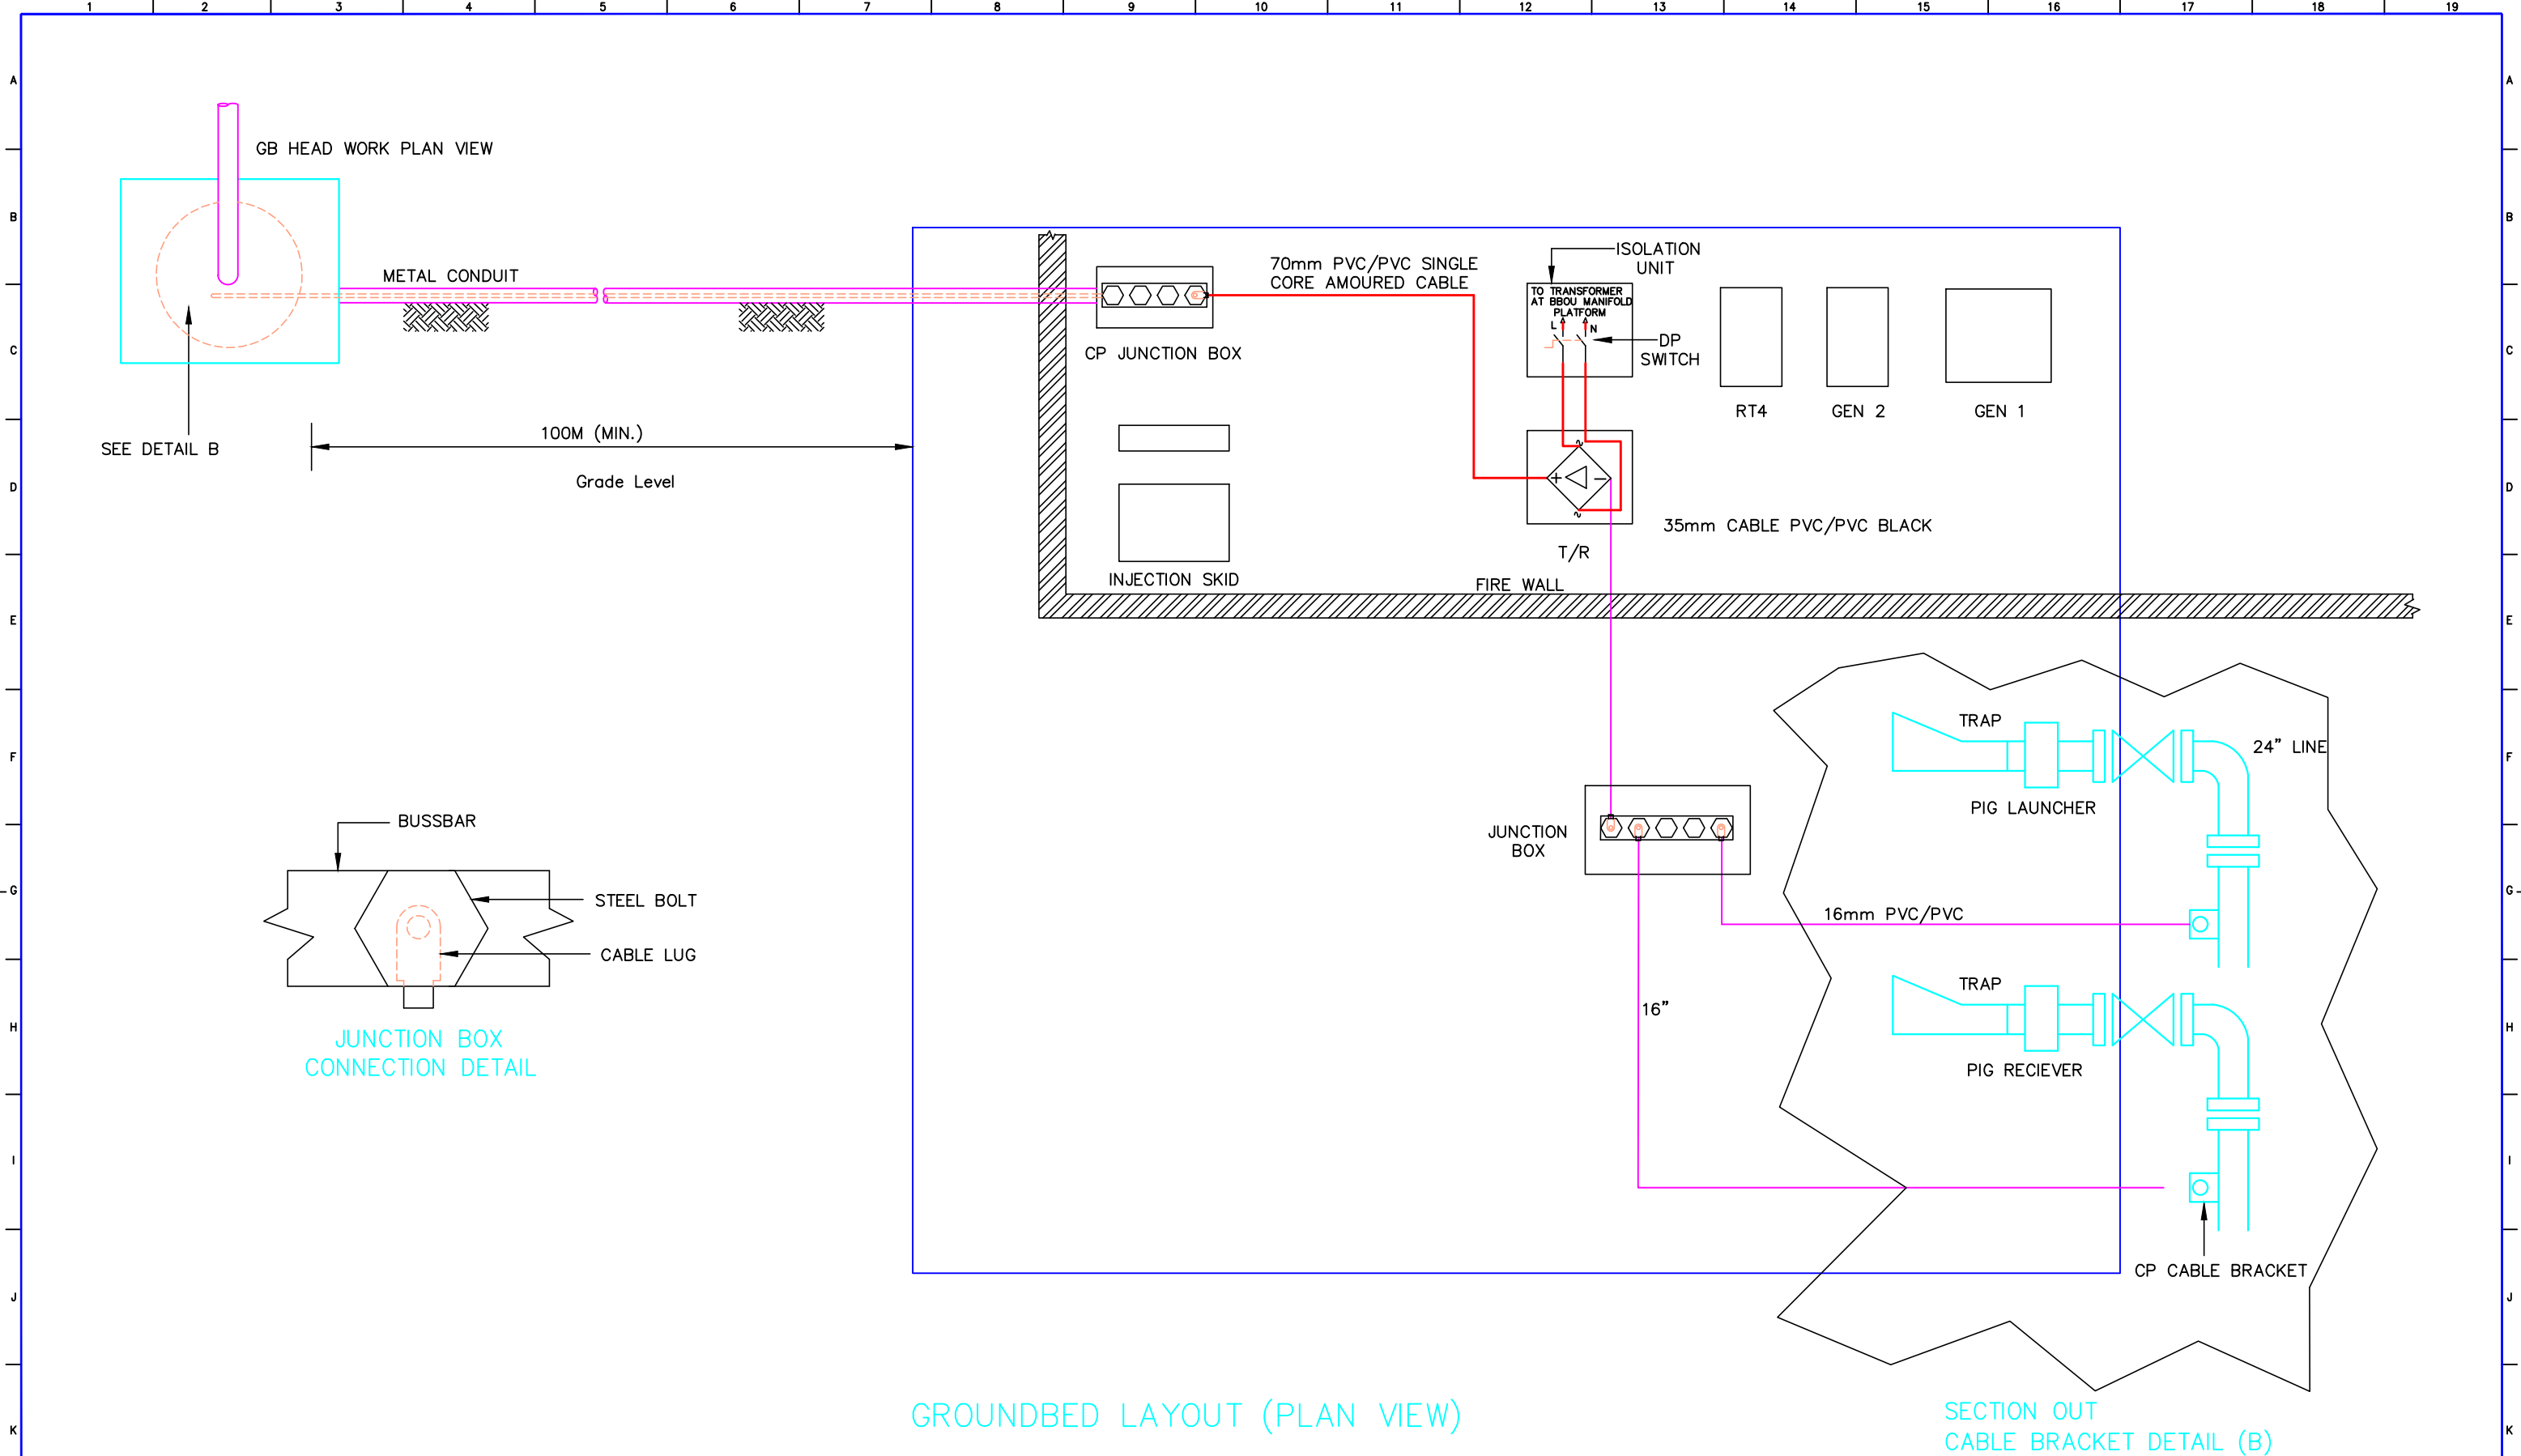

GROUND BED LAYOUT (PLAN VIEW)

SECTION OUT
CABLE BRACKET DETAIL (B)

L	REFERENCE DRAWINGS		DRAWING No.		NOTES: * The transformer indicated on the platform will have to be instrument transformer							CONTRACTOR		BRASS FERTILIZER & PETROCHEMICAL COMPANY LIMITED	
															 GAS PROCESSING AND METHANOL COMPLEX PROJECT FEED FOR GAS GATHERING PIPELINES 	
													LOCATION CP-GB LAYOUT BBOU MANIFOLD PLATFORM	
M	

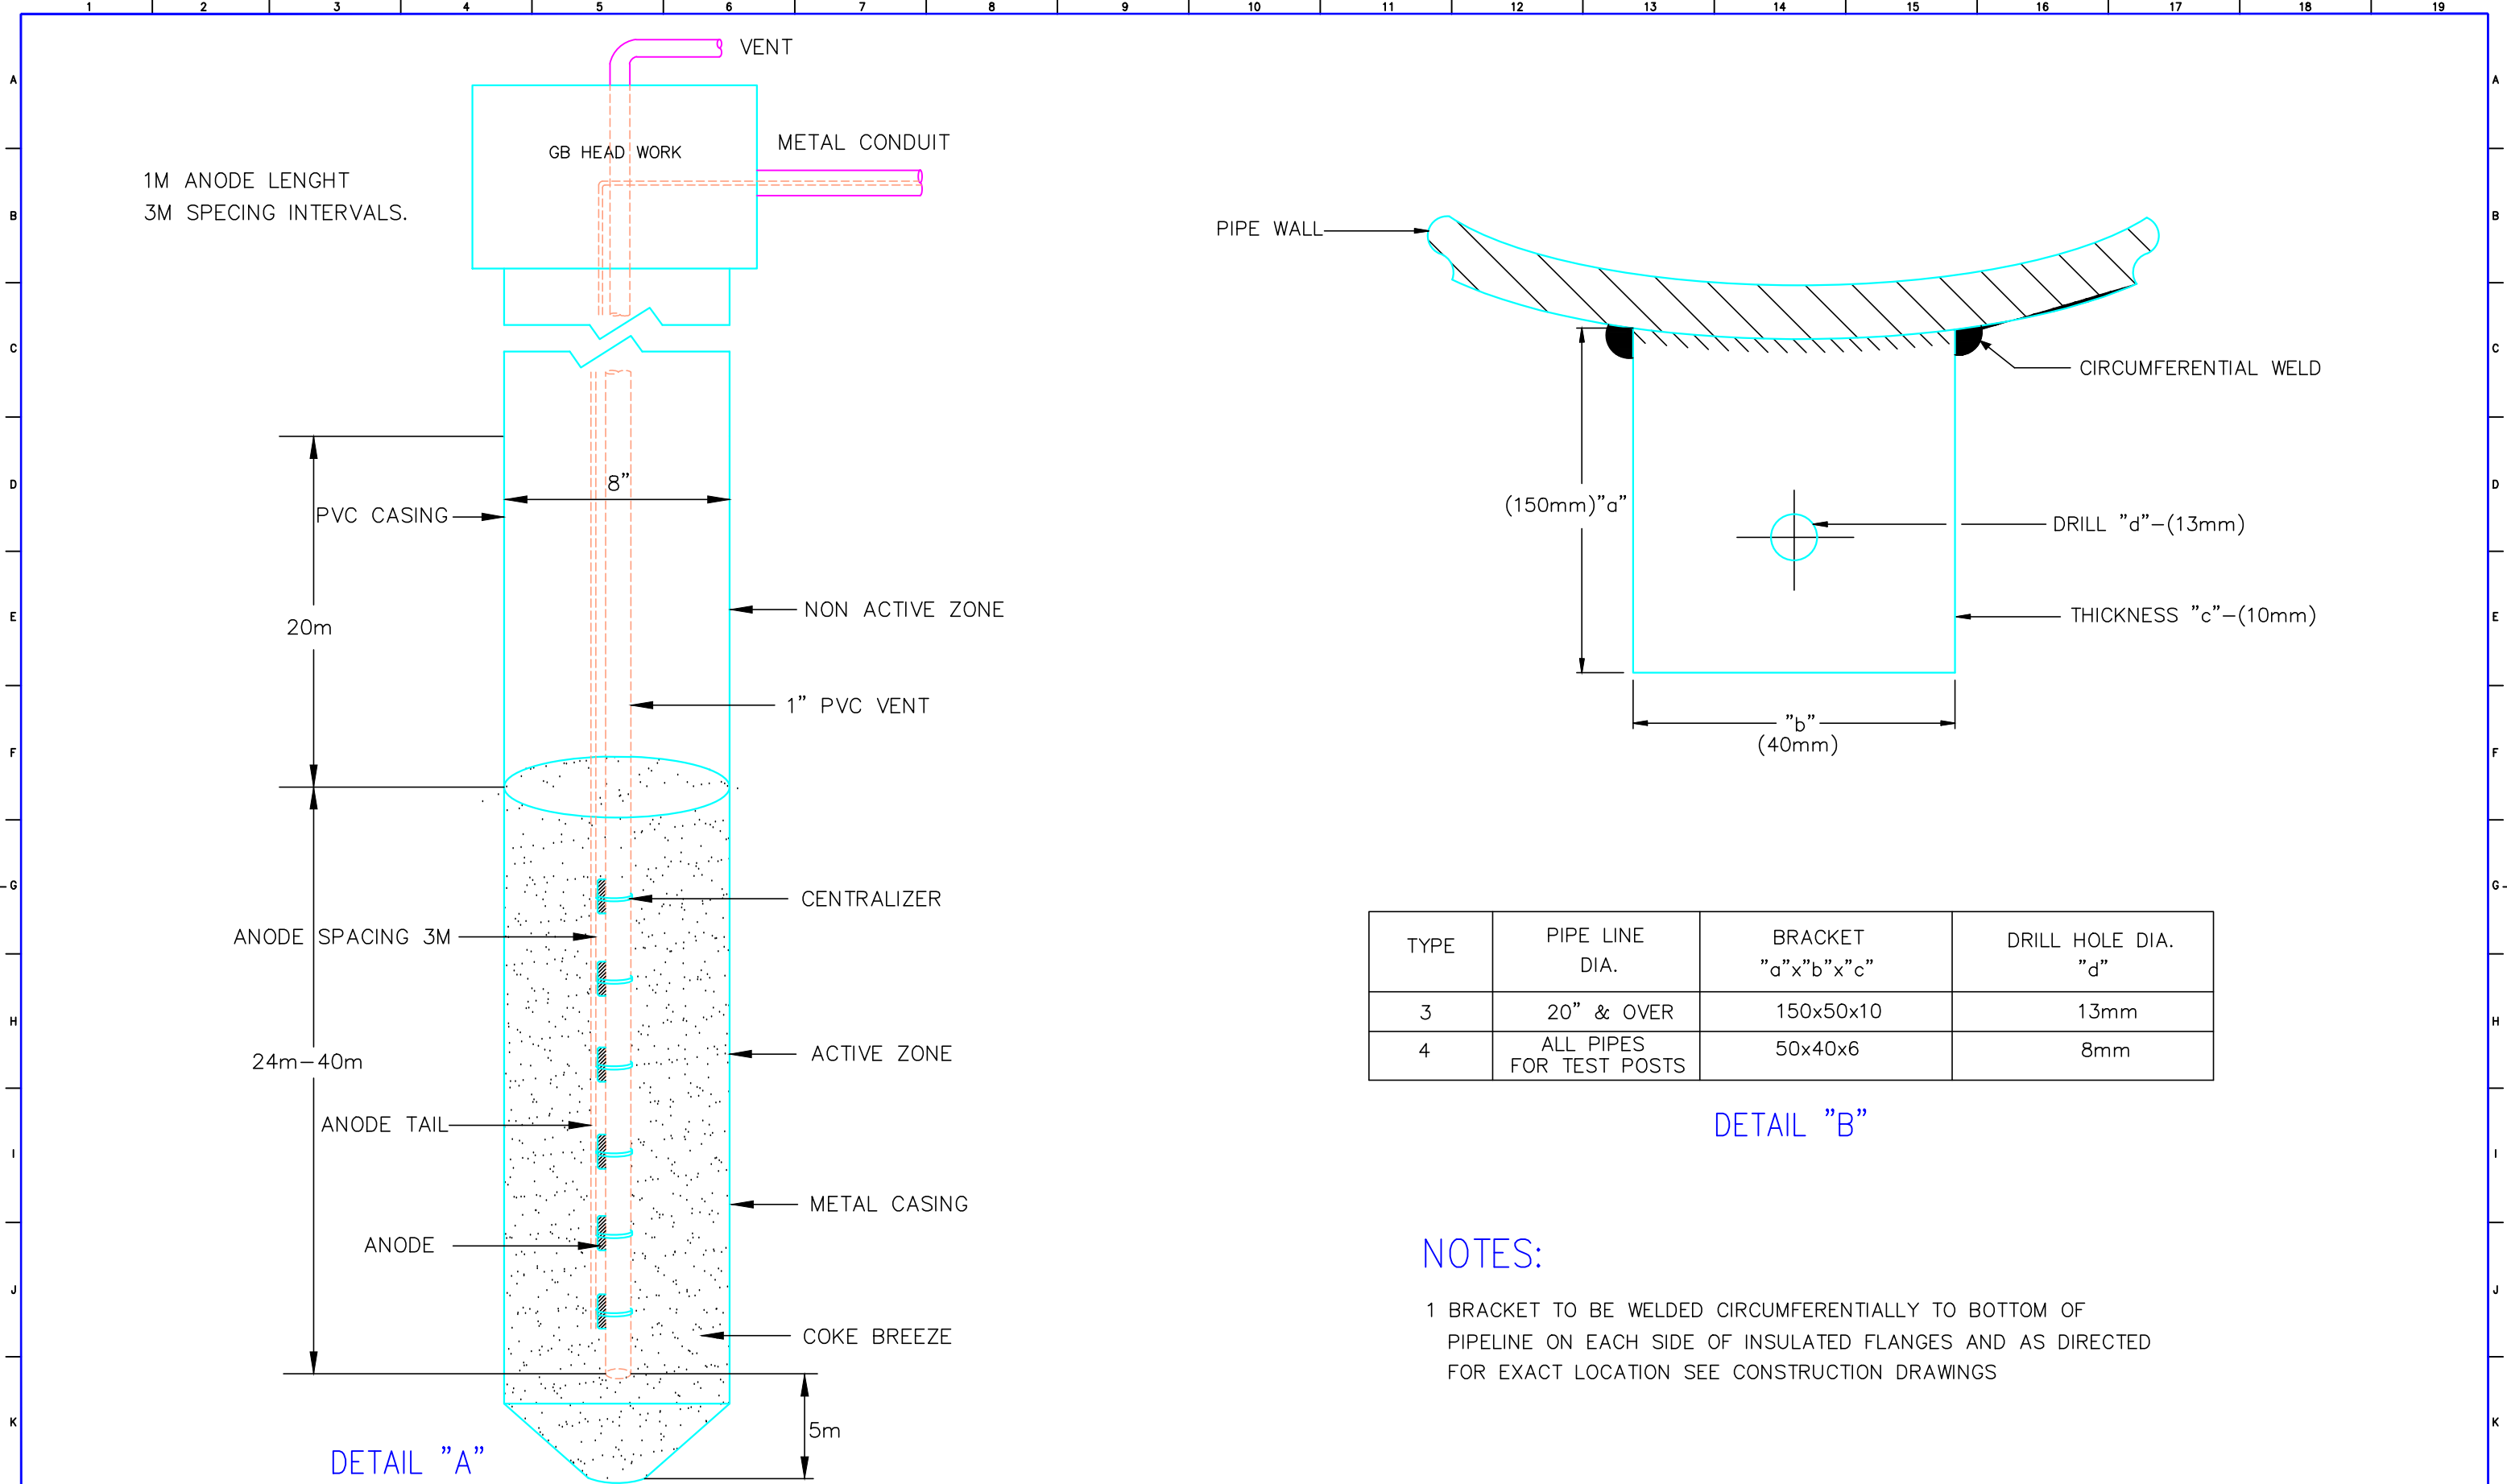


TYPE	PIPE LINE DIA.	BRACKET "a"x"b"x"c"	DRILL HOLE DIA. "d"
3	20" & OVER	150x50x10	13mm
4	ALL PIPES FOR TEST POSTS	50x40x6	8mm

DETAIL "B"

NOTES:

1 BRACKET TO BE WELDED CIRCUMFERENTIALLY TO BOTTOM OF PIPELINE ON EACH SIDE OF INSULATED FLANGES AND AS DIRECTED FOR EXACT LOCATION SEE CONSTRUCTION DRAWINGS

REFERENCE DRAWINGS		DRAWING No.	NOTES:					CONTRACTOR				BRASS FERTILIZER & PETROCHEMICAL COMPANY LIMITED				
								epic ATLANTIC				brass fertilizer GAS PROCESSING AND METHANOL COMPLEX PROJECT FEED FOR GAS GATHERING PIPELINES				
								ENDORSEMENT				CP-GB LAYOUT DRAWING ELEPA MANIFOLD PLATFORM				
								RELEASED FOR	DESIGN ENGR.	BFPC TECH REP	SPDC TECH REP	DATE	DRAWN: -		DATE: -	SHEET: 4 of 6
													CHECKED: -		EA-BFPC-L-GPMC-GGPL-FEED-ELE-DWG-014	REV.
													ENDORSED: -		PROJECT No. -	
													APP'D DATE: -		PROJECT No. -	
								COPY RIGHT RESERVED								

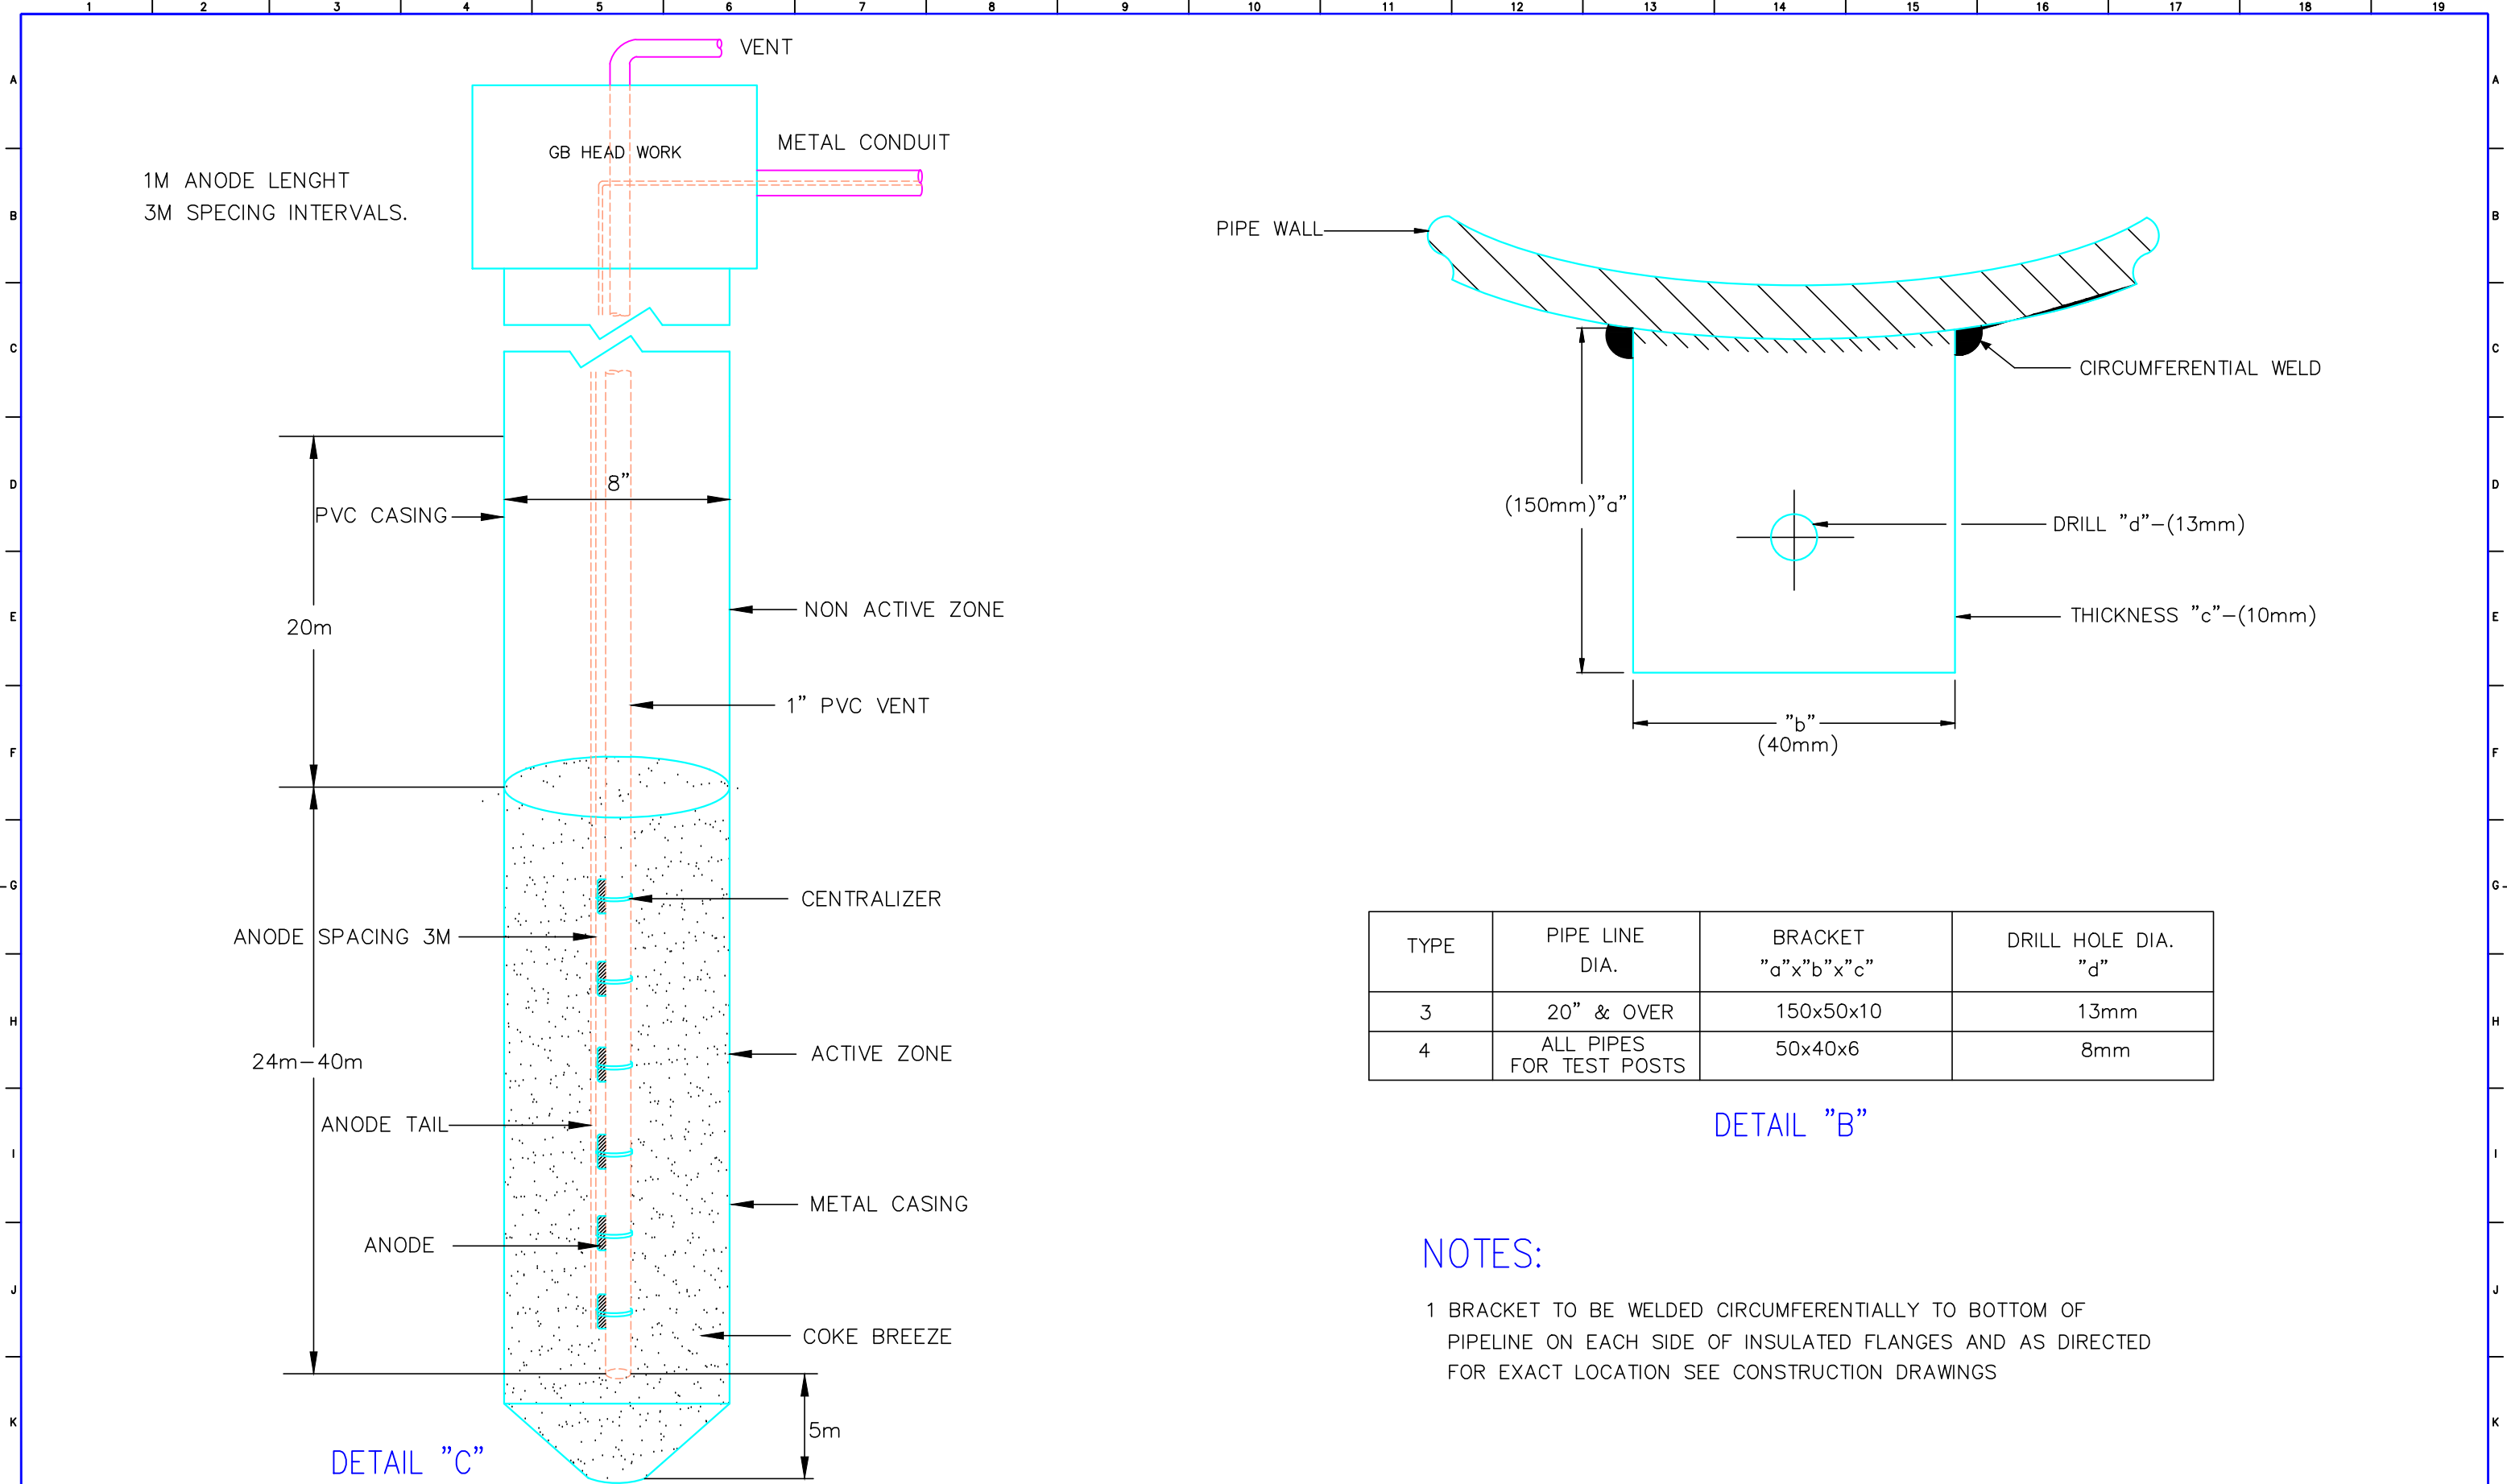

TYPE	PIPE LINE DIA.	BRACKET "a"x"b"x"c"	DRILL HOLE DIA. "d"
3	20" & OVER	150x50x10	13mm
4	ALL PIPES FOR TEST POSTS	50x40x6	8mm

DETAIL "B"

NOTES:

1 BRACKET TO BE WELDED CIRCUMFERENTIALLY TO BOTTOM OF PIPELINE ON EACH SIDE OF INSULATED FLANGES AND AS DIRECTED FOR EXACT LOCATION SEE CONSTRUCTION DRAWINGS

REFERENCE DRAWINGS		DRAWING No.	NOTES:						CONTRACTOR					BRASS FERTILIZER & PETROCHEMICAL COMPANY LIMITED				
									epic ATLANTIC					brass fertilizer GAS PROCESSING AND METHANOL COMPLEX PROJECT FEED FOR GAS GATHERING PIPELINES				
									ENDORSEMENT					CP-GB LAYOUT DRAWING AKABEL				
									RELEASED FOR					DRAWN: - DATE: - SHEET: 6 of 6				
									DESIGN ENGR.					CHECKED: - DRAWING No. A-BFPC-L-GPMC-GGPL-FEED-ELE-DWG-014 REV.				
									BFPCL TECH REP					ENDORSED: - PROJECT No. -				
									SPDC TECH REP					APP'D DATE: - PROJECT No. -				
									DATE									
									R01 ISSUED FOR REVIEW									
									CAA LBJ WEI 08/08/2022									
									DRAWN CHK END DATE									
									COPY RIGHT RESERVED									