



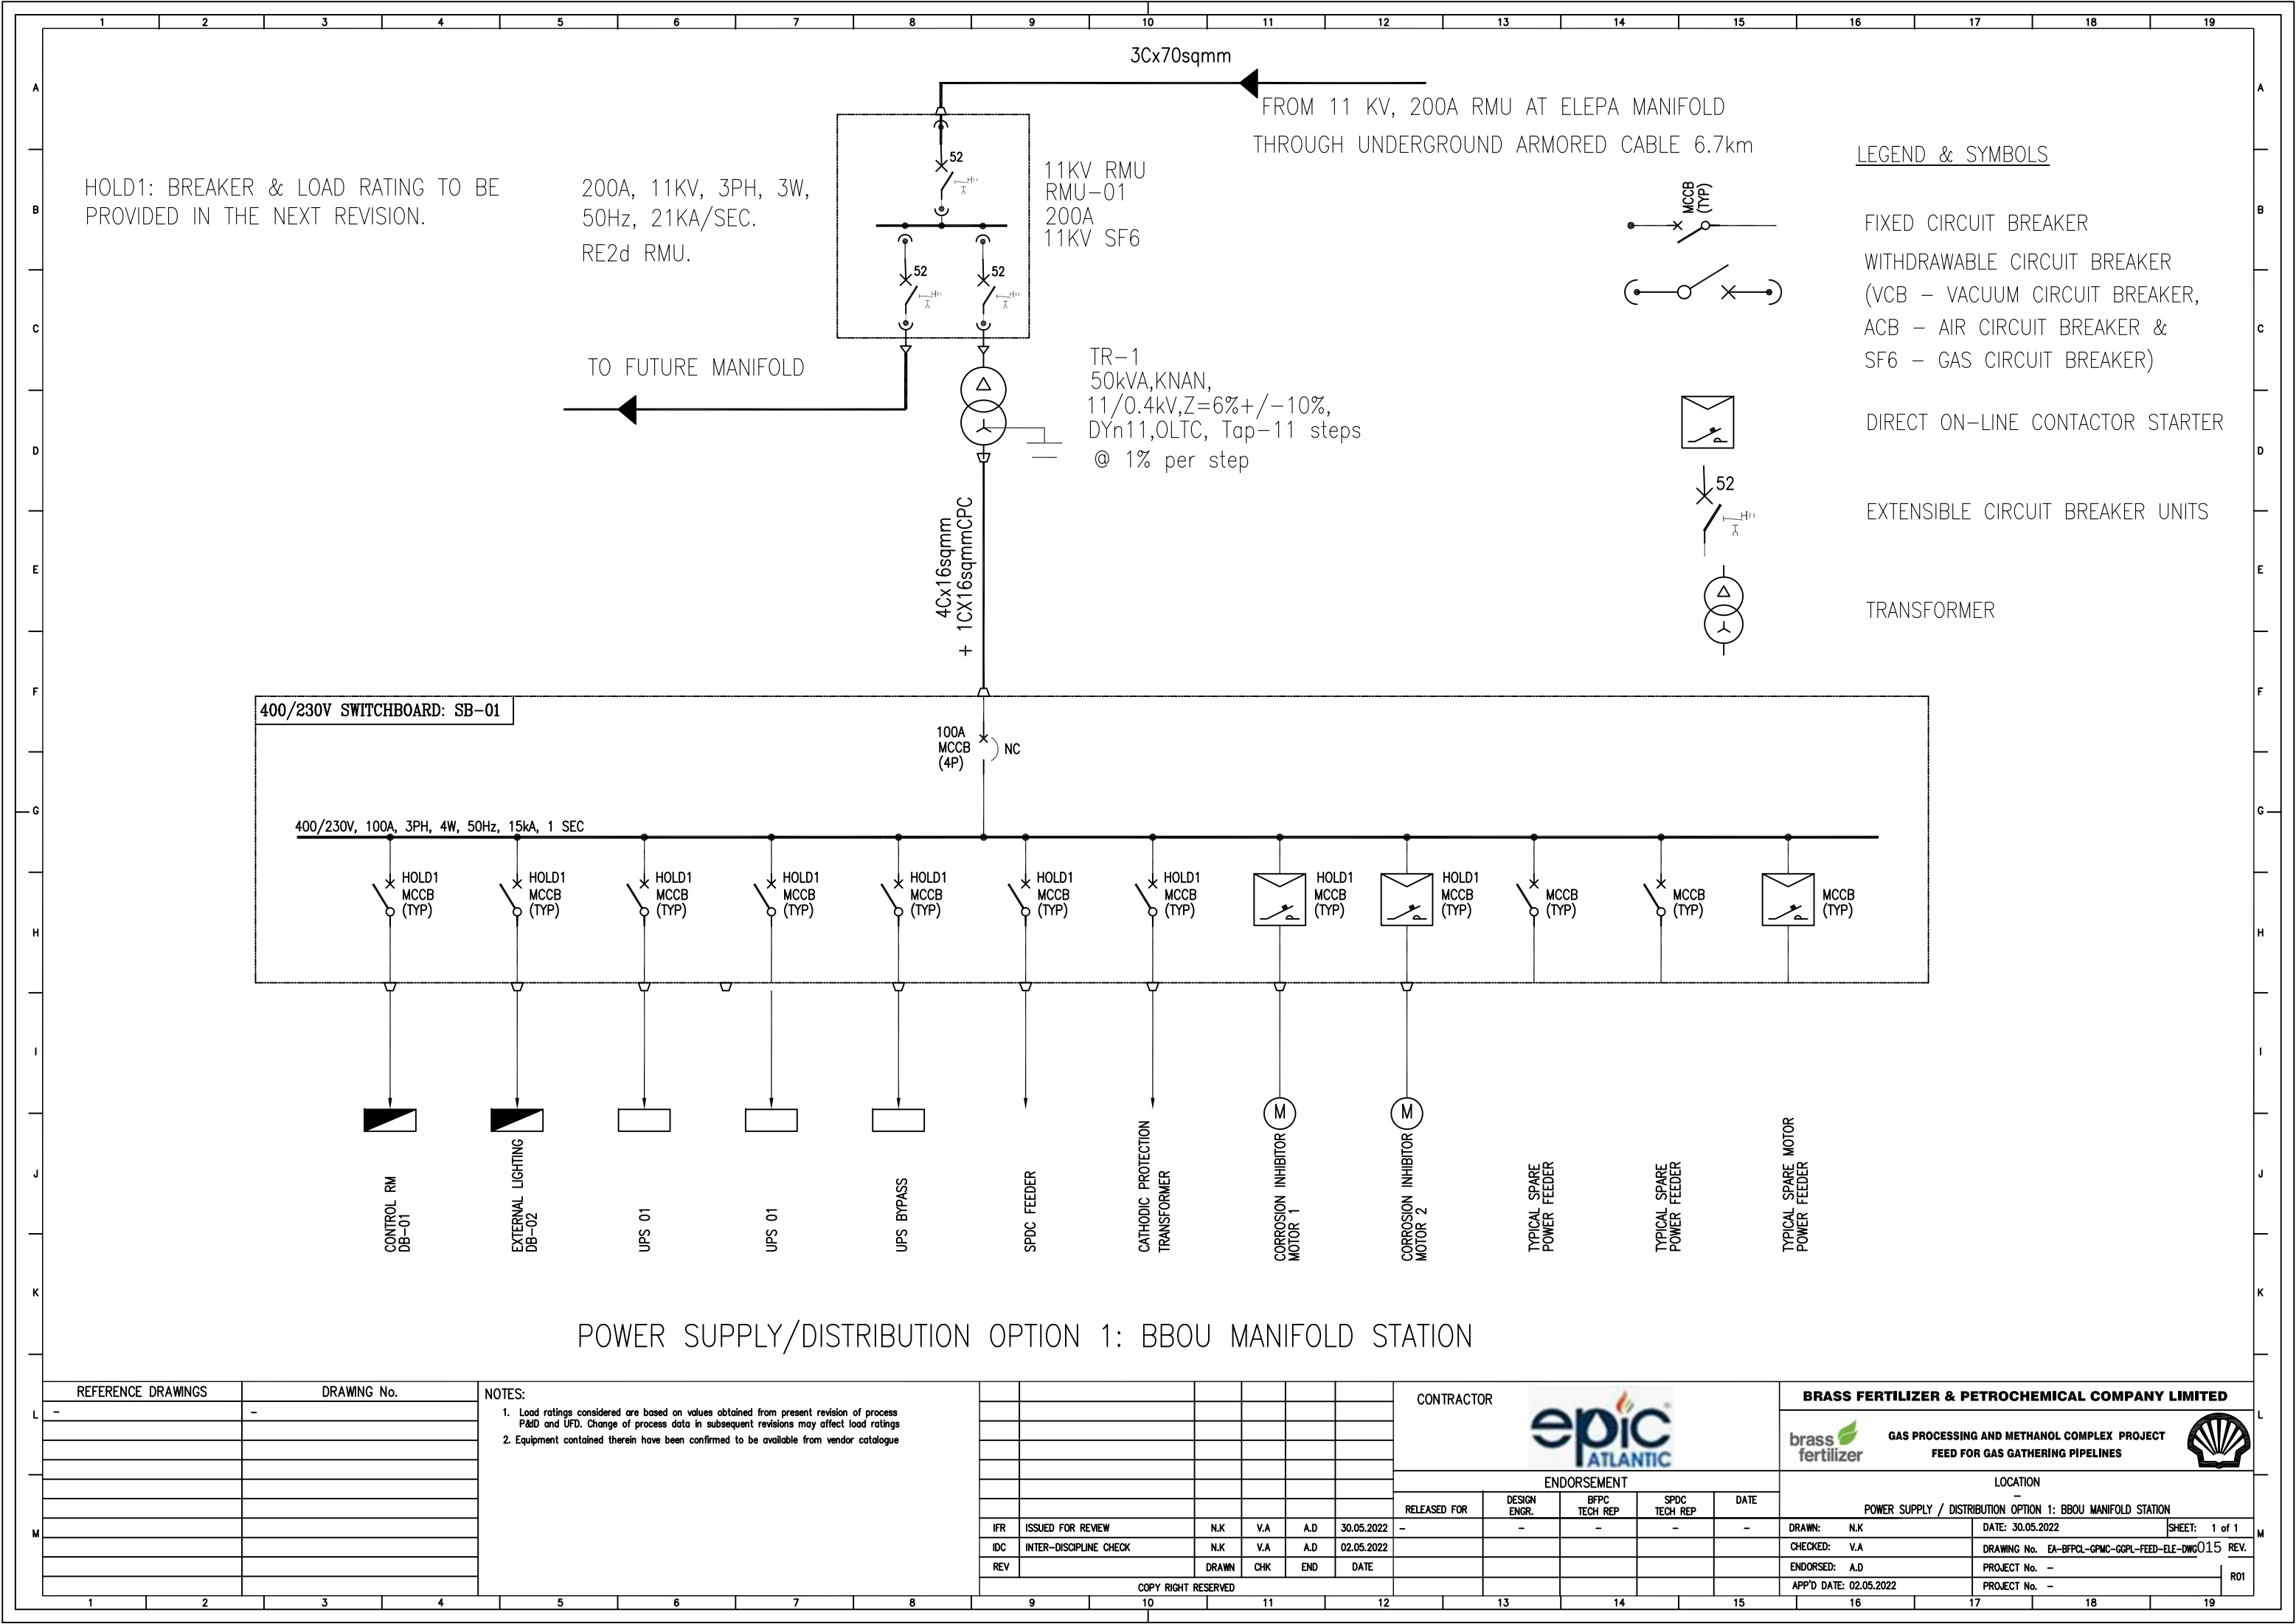

POWER SUPPLY/DISTRIBUTION OPTION 1: BBOU MANIFOLD STATION

REFERENCE DRAWINGS		DRAWING No.		NOTES: 1. Load ratings considered are based on values obtained from present revision of process P&ID and UFD. Change of process data in subsequent revisions may affect load ratings 2. Equipment contained therein have been confirmed to be available from vendor catalogue										CONTRACTOR 					BRASS FERTILIZER & PETROCHEMICAL COMPANY LIMITED											
																			brass fertilizer					GAS PROCESSING AND METHANOL COMPLEX PROJECT FEED FOR GAS GATHERING PIPELINES						
									LOCATION -					POWER SUPPLY / DISTRIBUTION OPTION 1: BBOU MANIFOLD STATION																
									ENDORSEMENT																					
									RELEASED FOR	DESIGN ENGR.	BFPC TECH REP	SPDC TECH REP	DATE																	
									IFR	ISSUED FOR REVIEW	N.K	V.A	A.D	30.05.2022	-	-	-	-	-	DRAWN: N.K					DATE: 30.05.2022		SHEET: 1 of 1			
									IDC	INTER-DISCIPLINE CHECK	N.K	V.A	A.D	02.05.2022						CHECKED: V.A					DRAWING No. EA-BFPCL-GPMC-GGPL-FEED-ELE-DWG015					REV.
									REV		DRAWN	CHK	END	DATE						ENDORSED: A.D					PROJECT No. -					R01
									COPY RIGHT RESERVED										APP'D DATE: 02.05.2022					PROJECT No. -						

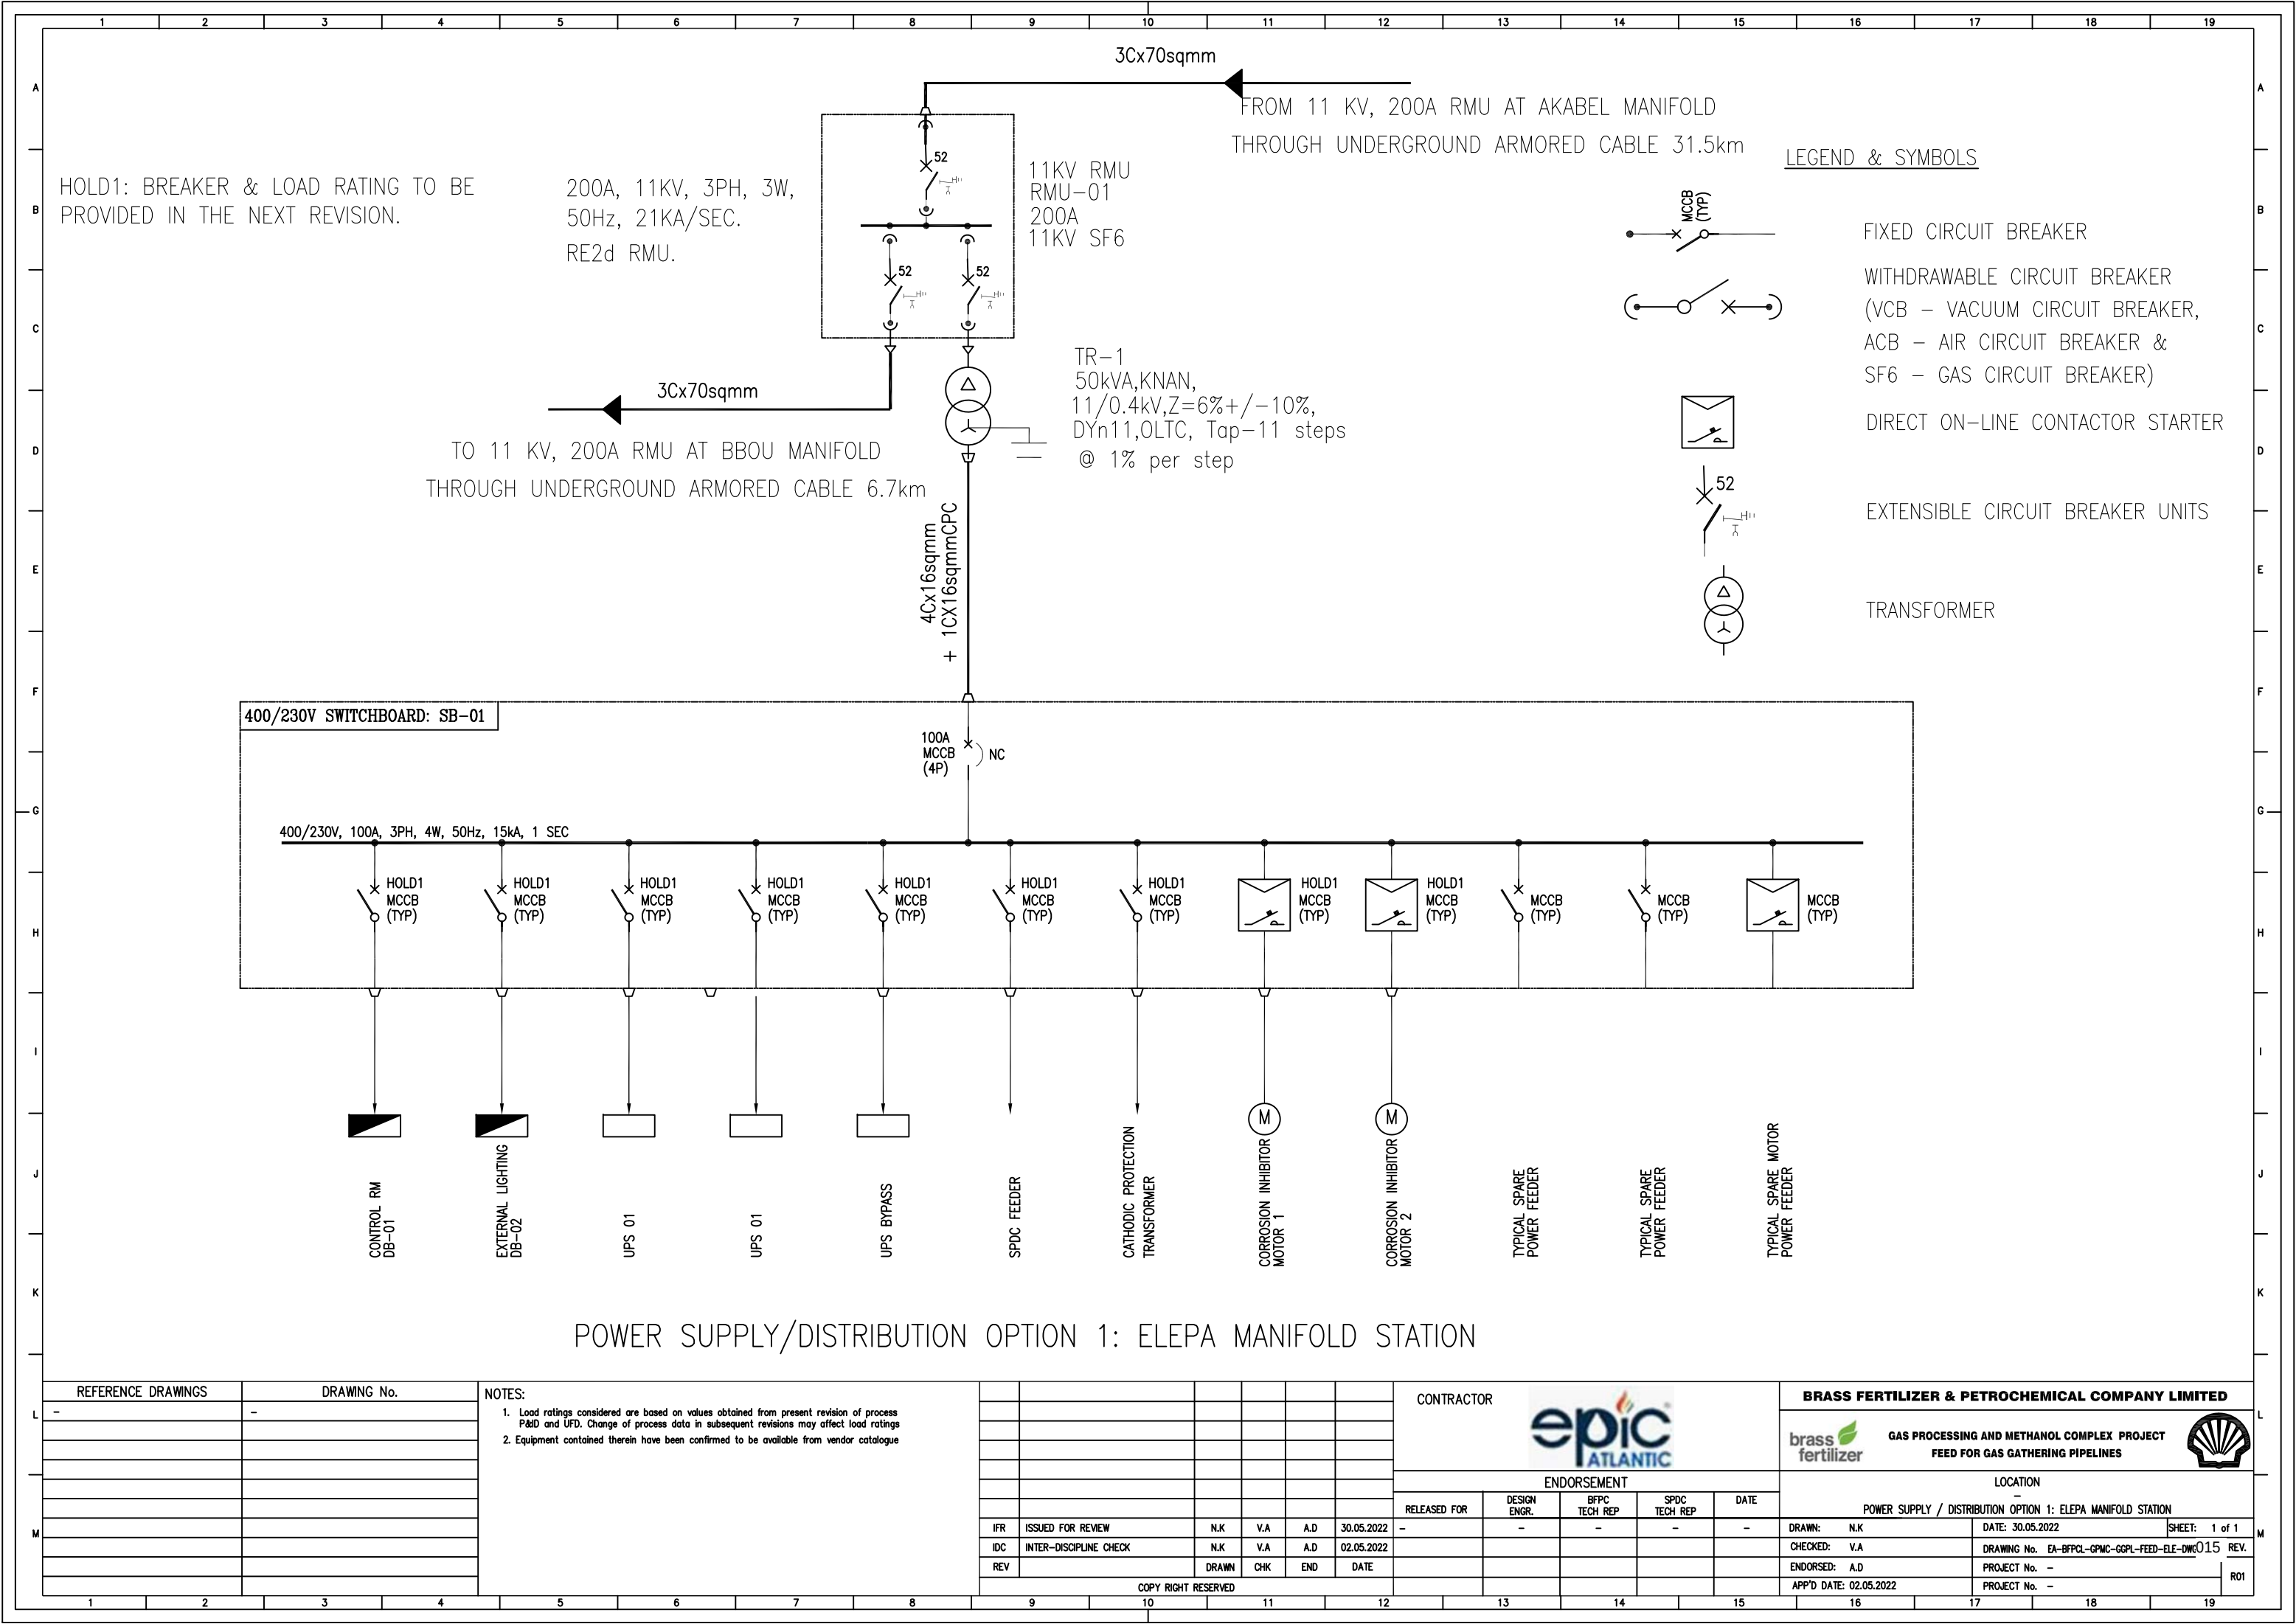

POWER SUPPLY/DISTRIBUTION OPTION 1: ELEPA MANIFOLD STATION

REFERENCE DRAWINGS		DRAWING No.	NOTES: 1. Load ratings considered are based on values obtained from present revision of process P&ID and UFD. Change of process data in subsequent revisions may affect load ratings 2. Equipment contained therein have been confirmed to be available from vendor catalogue							CONTRACTOR					BRASS FERTILIZER & PETROCHEMICAL COMPANY LIMITED								
-		-													 GAS PROCESSING AND METHANOL COMPLEX PROJECT FEED FOR GAS GATHERING PIPELINES 								
										ENDORSEMENT					LOCATION								
															POWER SUPPLY / DISTRIBUTION OPTION 1: ELEPA MANIFOLD STATION								
										RELEASED FOR	DESIGN ENGR.	BFPC TECH REP	SPDC TECH REP	DATE									
										IFR	ISSUED FOR REVIEW	N.K	V.A	A.D	30.05.2022	-	-	-	-	-	DRAWN: N.K	DATE: 30.05.2022	SHEET: 1 of 1
										IDC	INTER-DISCIPLINE CHECK	N.K	V.A	A.D	02.05.2022						CHECKED: V.A	DRAWING No. EA-BFPC-L-GPMC-GGPL-FEED-ELE-DWG015	REV.
										REV		DRAWN	CHK	END	DATE						ENDORSED: A.D	PROJECT No. -	R01
										COPY RIGHT RESERVED													
																APP'D DATE: 02.05.2022							

