

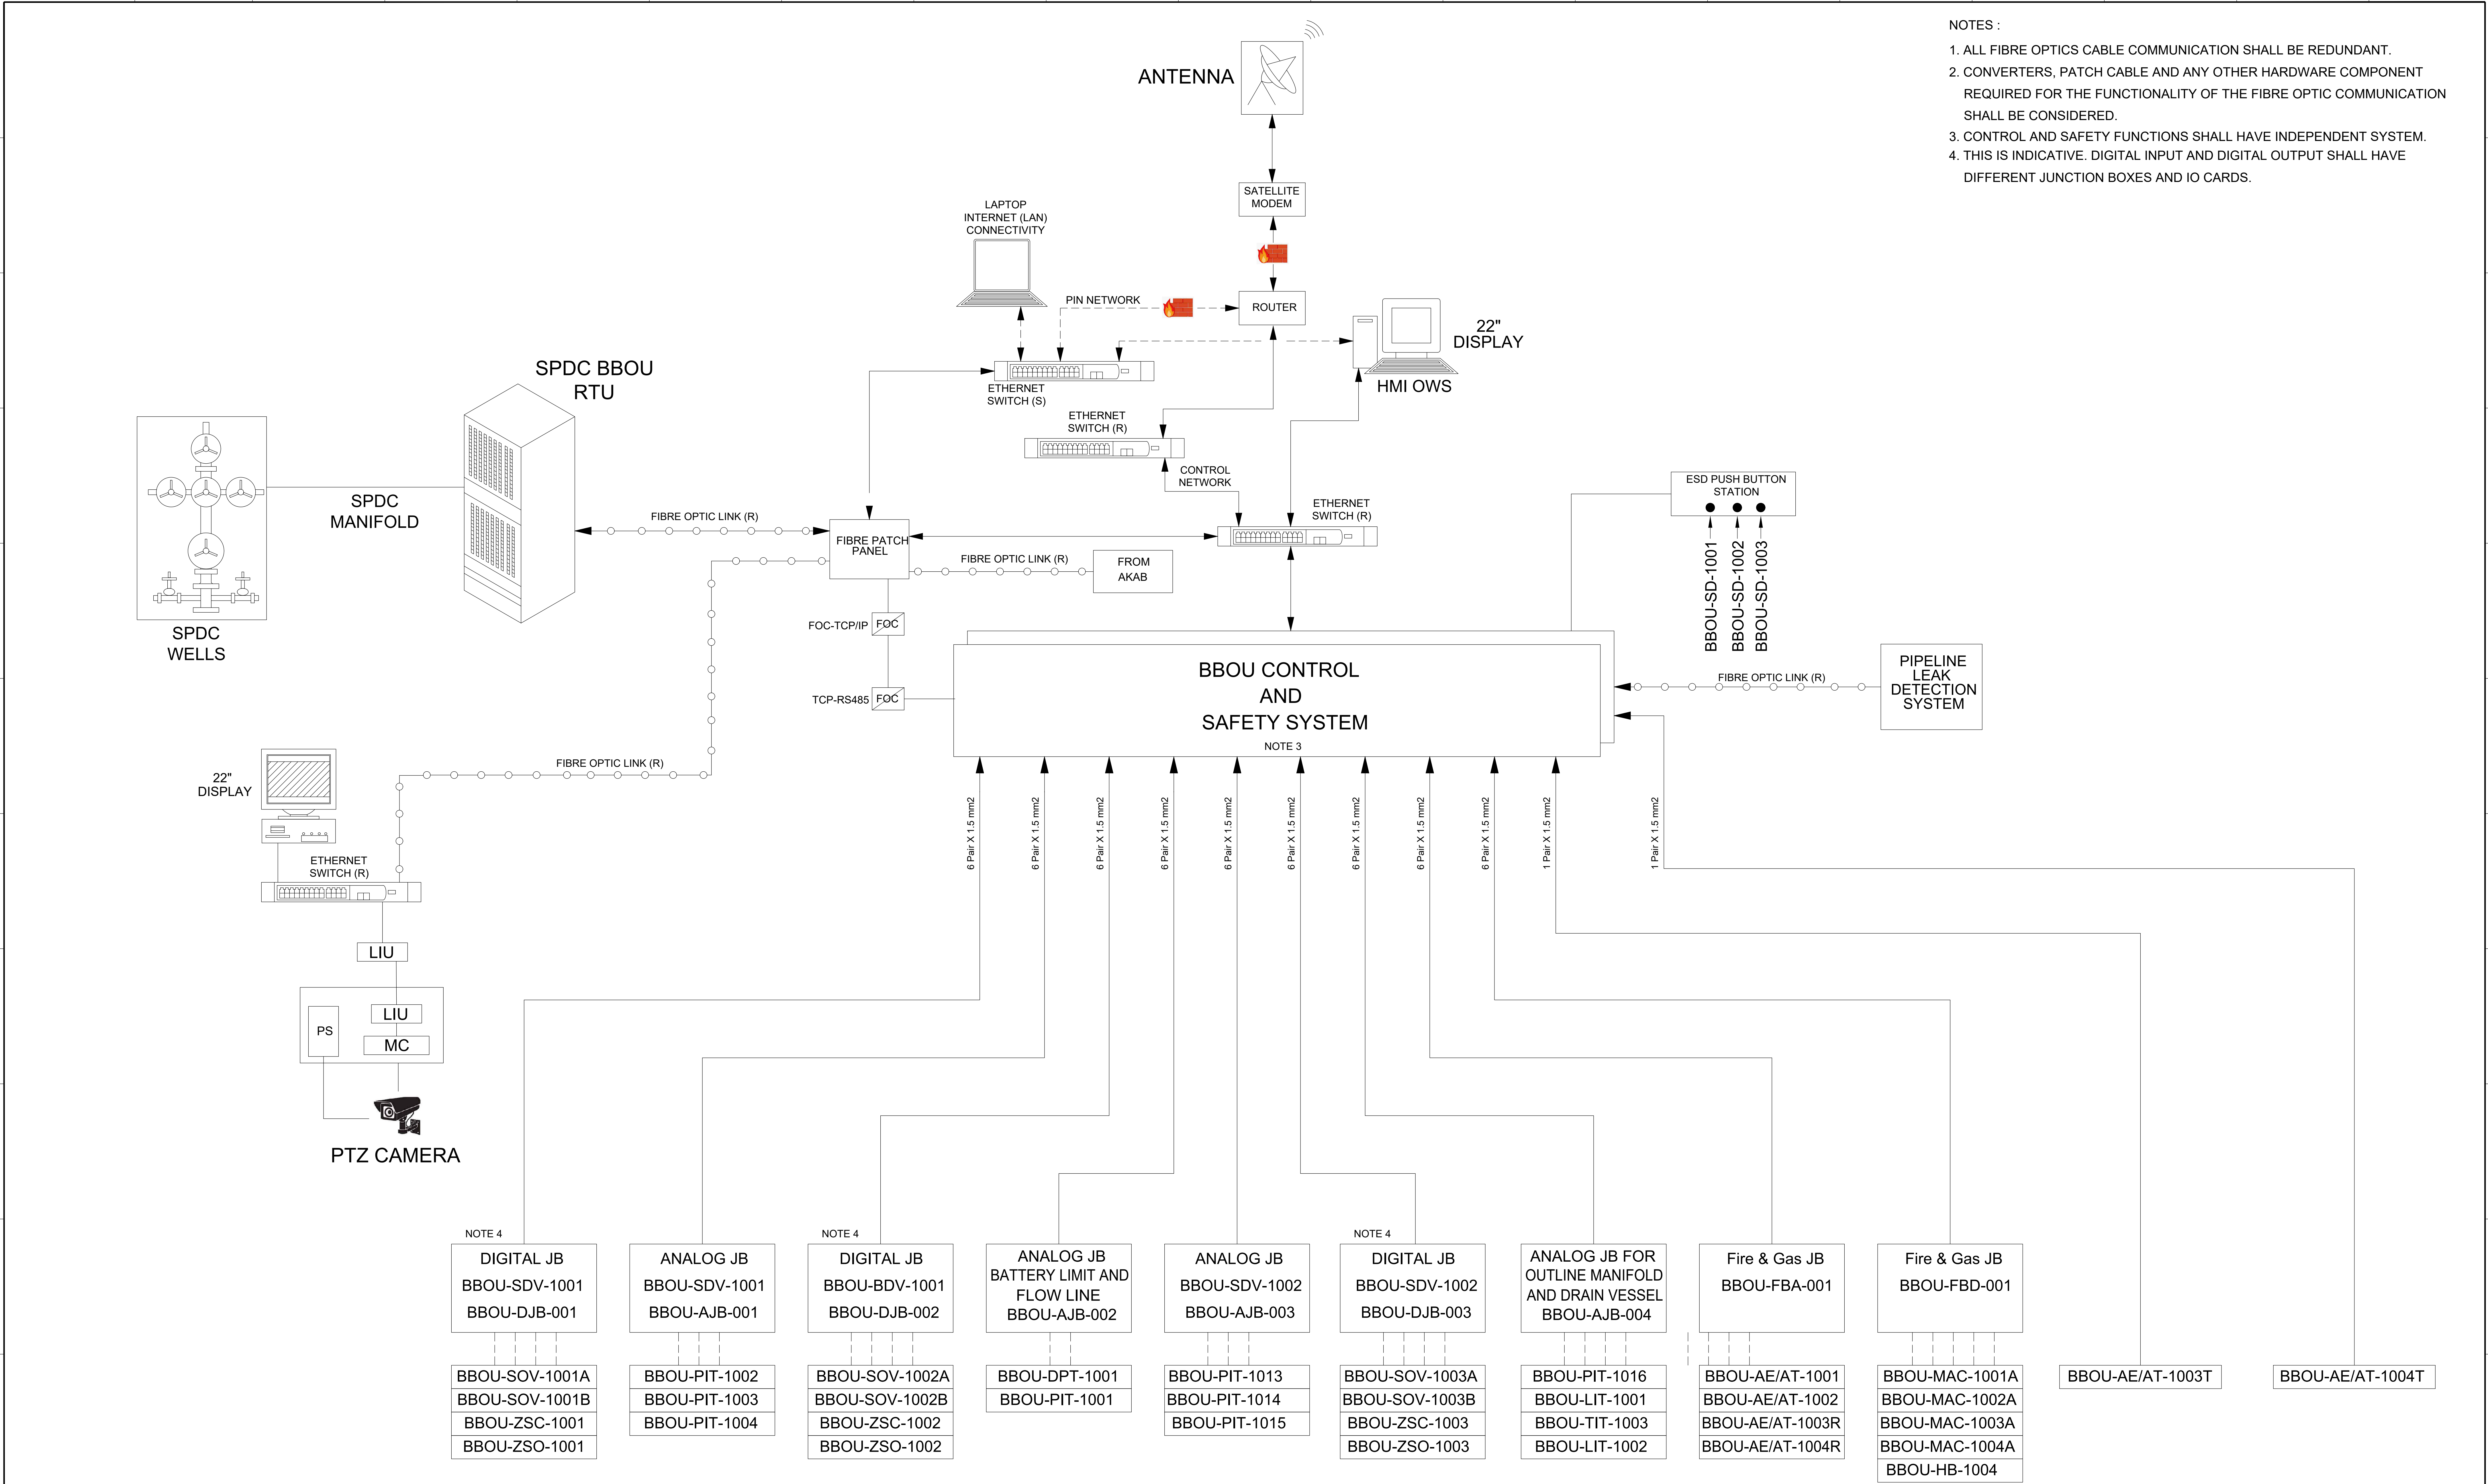


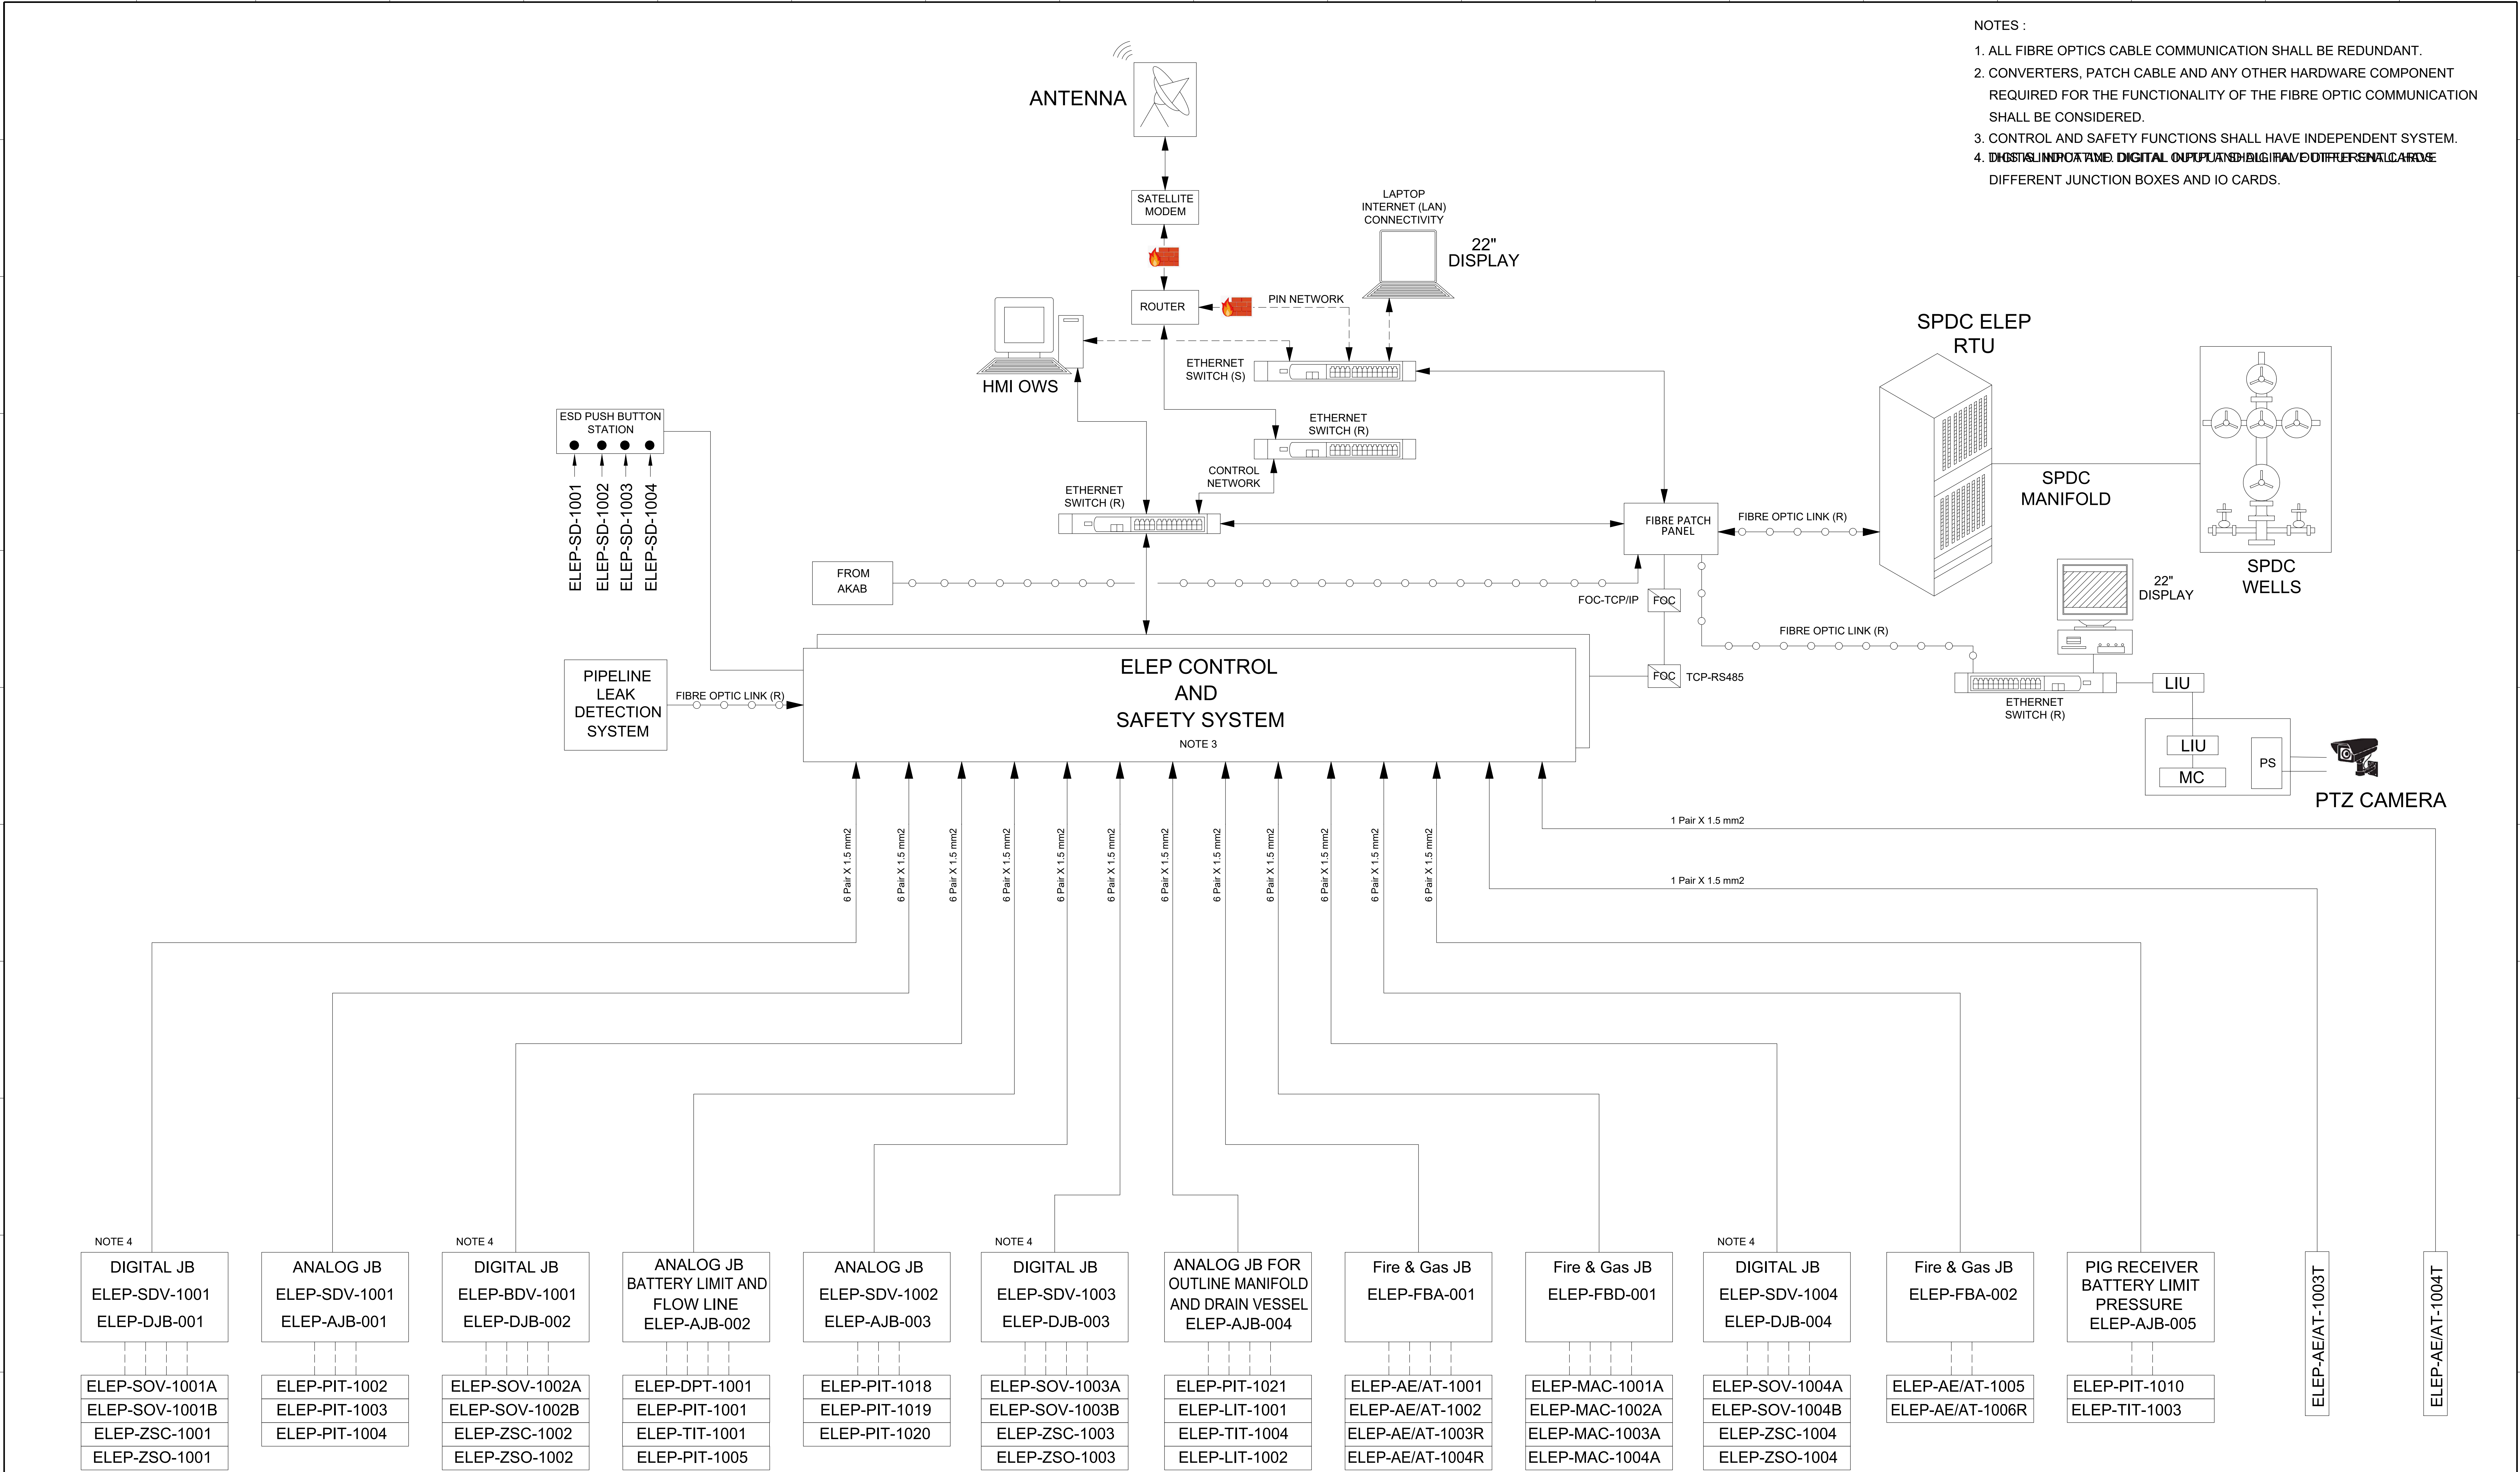

REFERENCE DRAWINGS		DRAWING No.	NOTES: -						CONTRACTOR		BRASS FERTILIZER & PETROCHEMICAL COMPANY LIMITED			
-	-	-											 GAS PROCESSING AND METHANOL COMPLEX PROJECT  FEED FOR GAS GATHERING PIPELINES	
											BLOCK DIAGRAM BBOU			

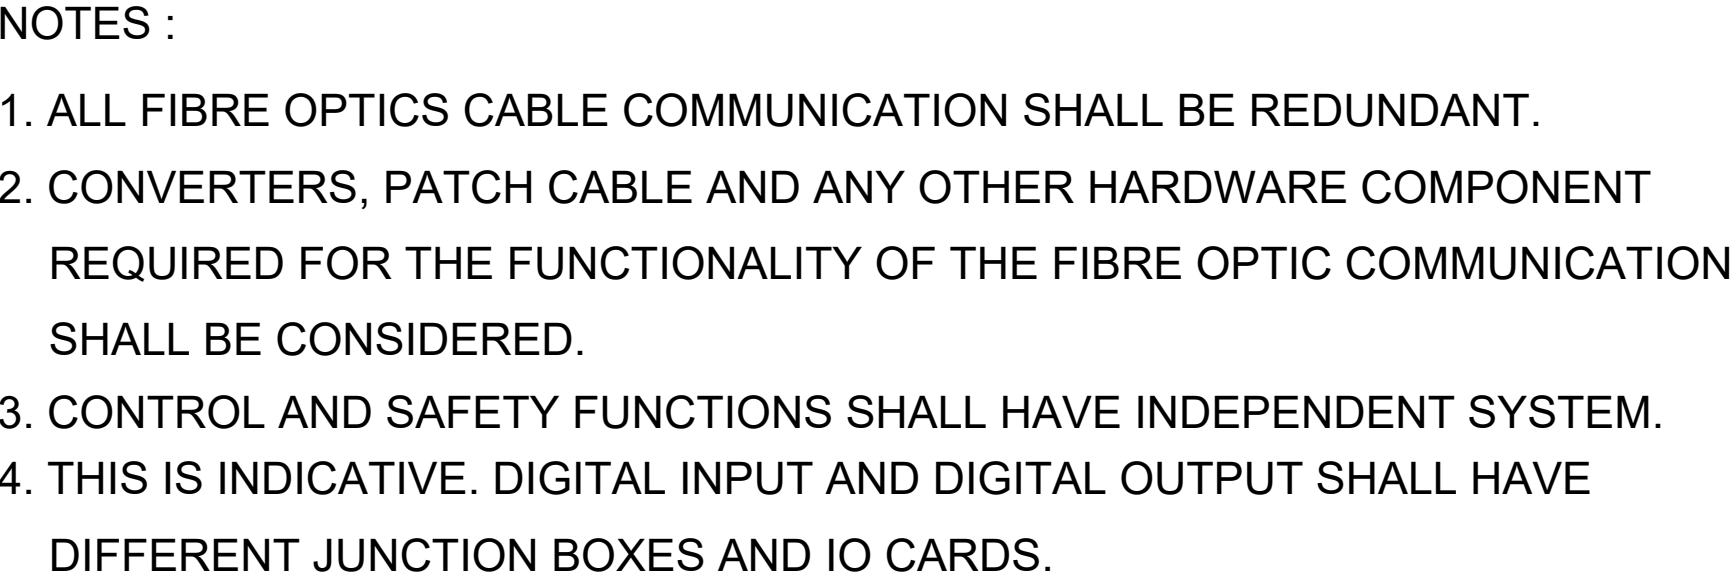

REFERENCE DRAWINGS		DRAWING No.	NOTES:						CONTRACTOR					BRASS FERTILIZER & PETROCHEMICAL COMPANY LIMITED							
														 GAS PROCESSING AND METHANOL COMPLEX PROJECT  FEED FOR GAS GATHERING PIPELINES							
									ENDORSEMENT					BLOCK DIAGRAM ELEP							
									RELEASED FOR		DESIGN ENGR.	BFPC TECH REP	SPDC TECH REP	DATE							
									R03		ISSUED FOR REVIEW	KIRAN P.	PRINCE O.	KINGSLEY A.	26-07-22	DRAWN: KIRAN P.		DATE: 01-07-2022		SHEET: 1 of 1	
									R02		ISSUED FOR REVIEW	KIRAN P.	PRINCE O.	KINGSLEY A.	01-07-22	CHECKED: PRINCE O.		DRAWING No. EA-BFPC-L-GPMC-GGPL-FEED-ICS-DWG-004-02		REV.	
									R01		ISSUED FOR REVIEW	KIRAN P.	PRINCE O.	KINGSLEY A.	14-06-22	ENDORSED: KINGSLEY. A.		PROJECT No. -		R03	
									REV		DRAWN		CHK	END	DATE	APP'D DATE: -		PROJECT No.			
									COPY RIGHT RESERVED												

[illegible]