

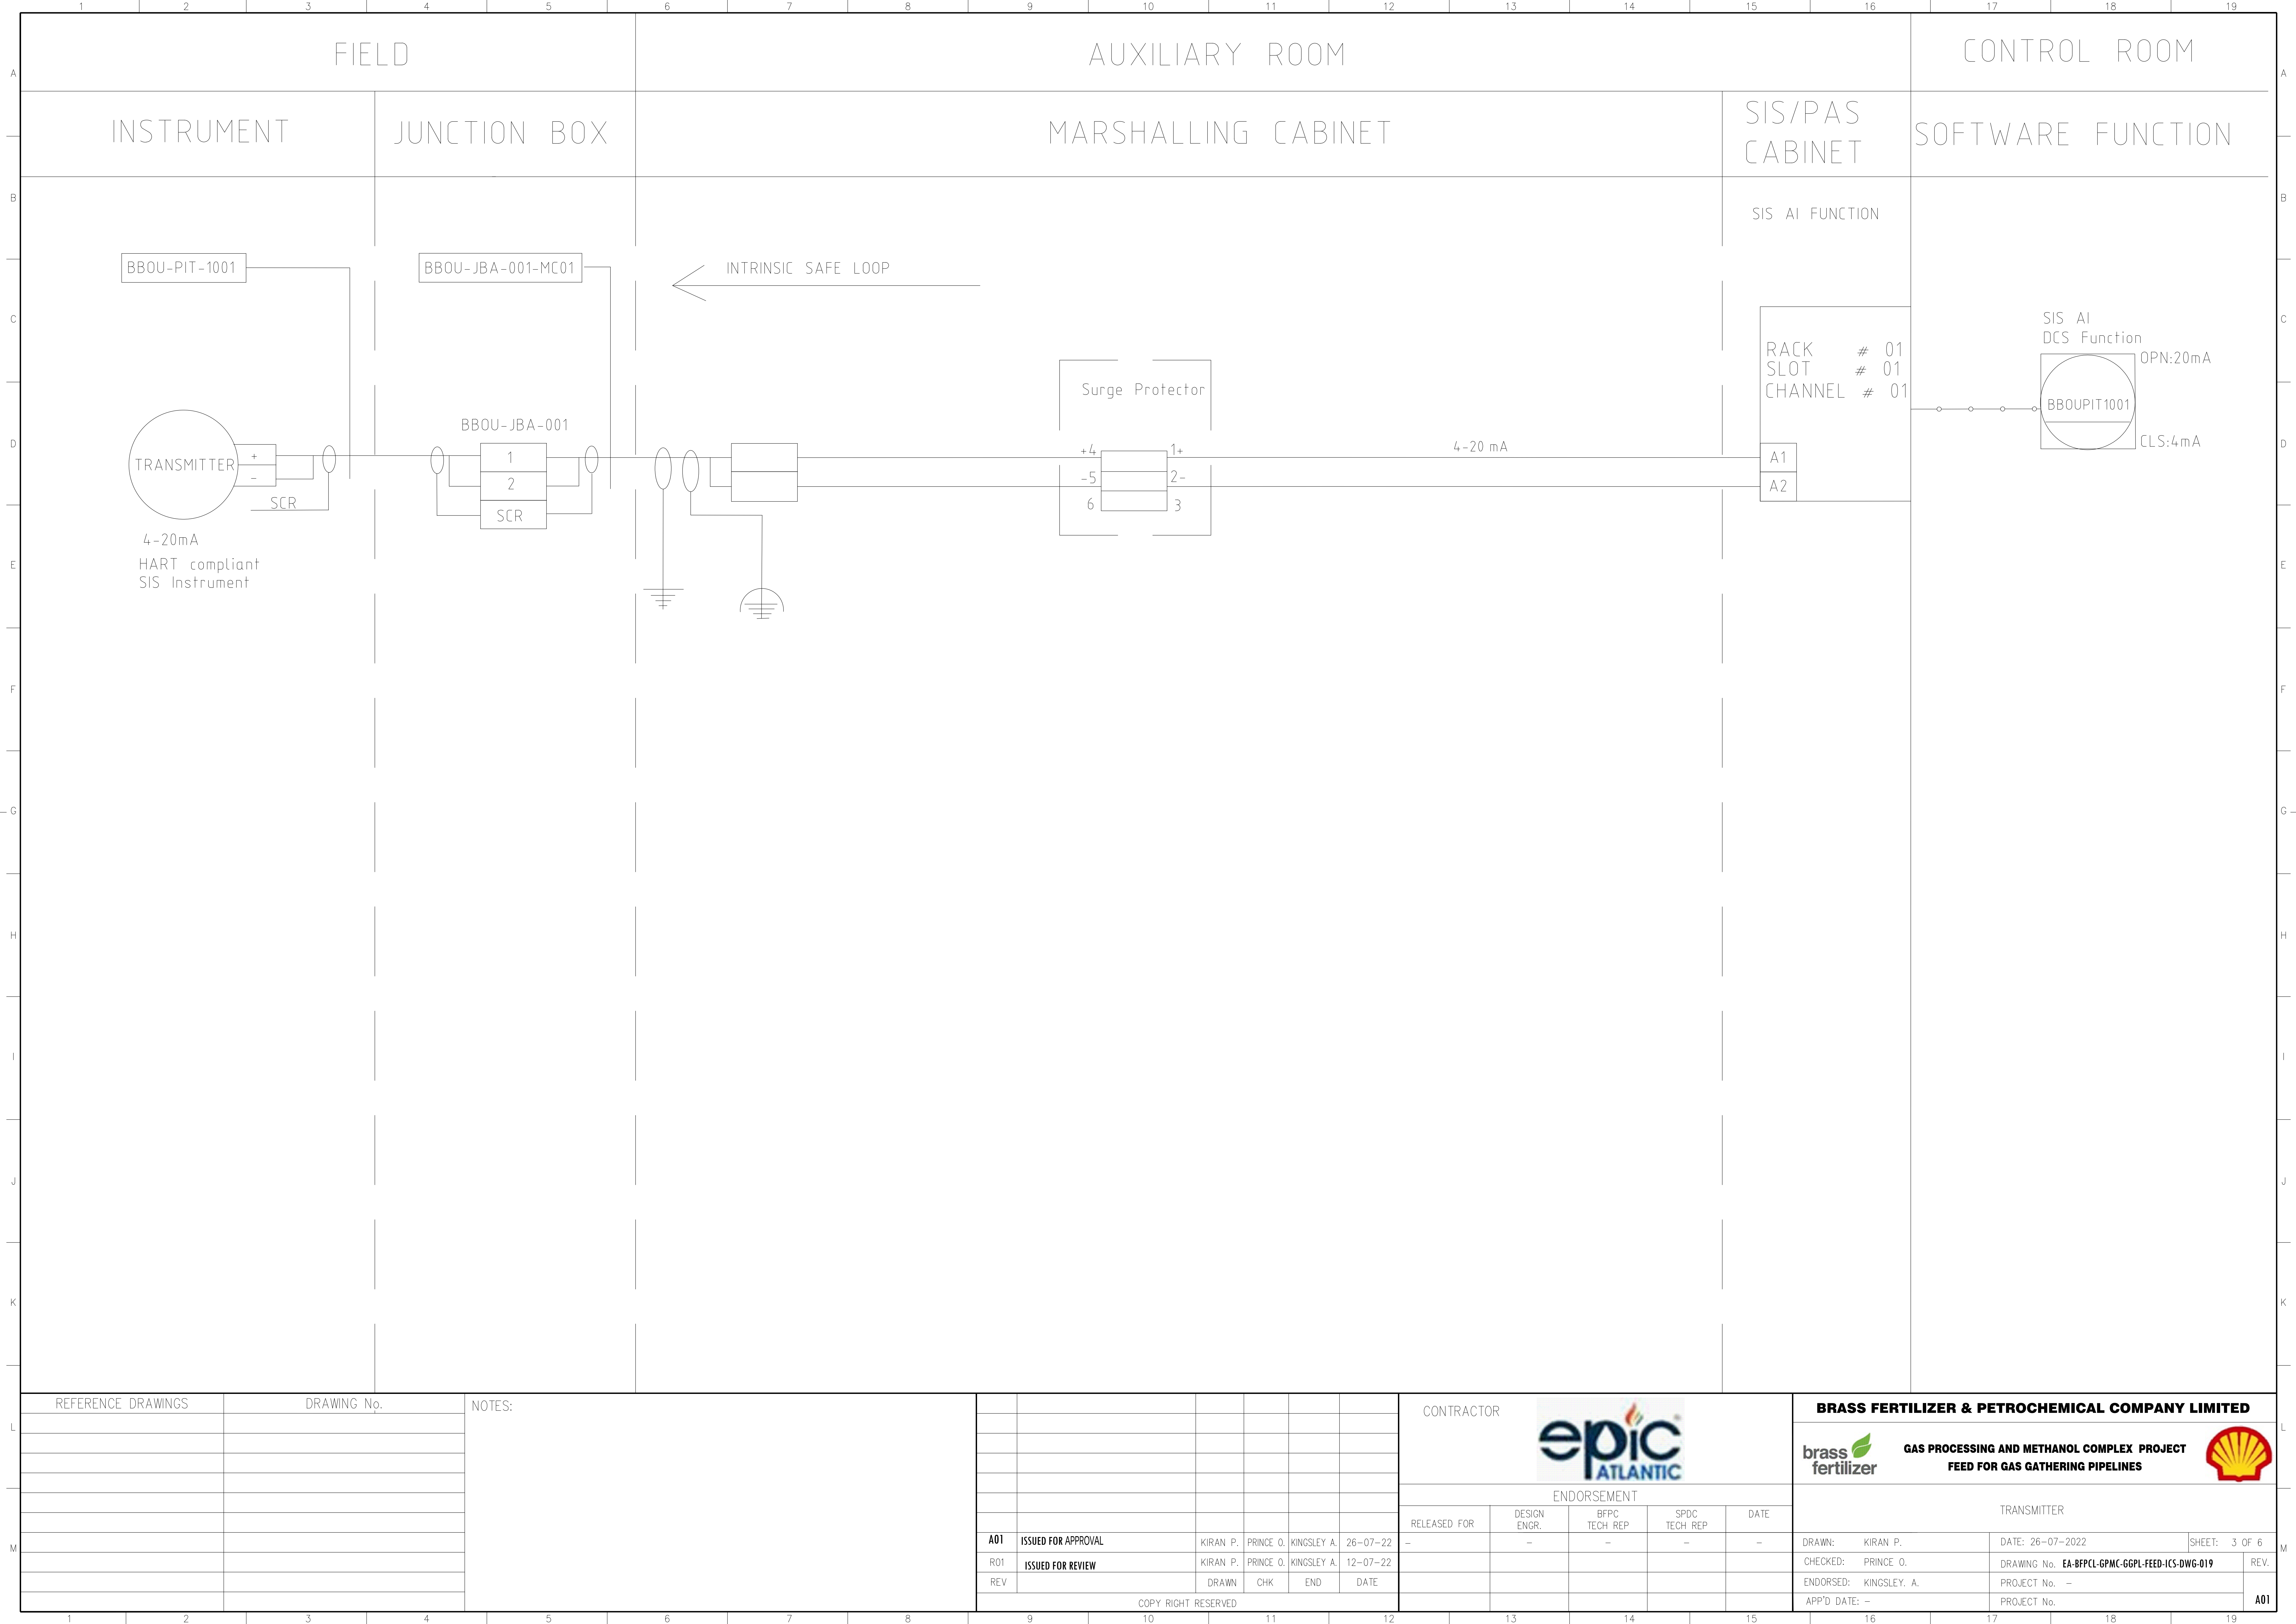



1	2	3	4	5	6	7	8	9	10	11	12	13	14	15	16	17	18	19
A	SHT.NO.	DESCRIPTION	REV.	R01	REV.	A01			SHT.NO.	DESCRIPTION								
B	01	COVER SHEET	12-07-22		26-07-22													
C	02	INDEX SHEET																
D	03	TRANSMITTER																
E	04	DI DEVICE																
F	05	DO DEVICE																
G	06	GAS DETECTOR																
H																		
I																		
J																		
K																		
L																		
M																		

REFERENCE DRAWINGS	DRAWING No.	NOTES:								CONTRACTOR					BRASS FERTILIZER & PETROCHEMICAL COMPANY LIMITED				
																 GAS PROCESSING AND METHANOL COMPLEX PROJECT FEED FOR GAS GATHERING PIPELINES 			
											ENDORSEMENT					COOVER SHEET			
											RELEASED FOR	DESIGN ENGR.	BFPc TECH REP	SPDC TECH REP	DATE				

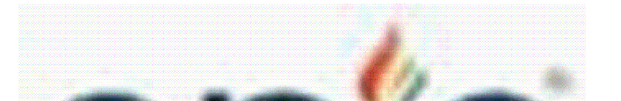

L	REFERENCE DRAWINGS	DRAWING No.	NOTES:							CONTRACTOR		BRASS FERTILIZER & PETROCHEMICAL COMPANY LIMITED								
													GAS PROCESSING AND METHANOL COMPLEX PROJECT							
													FEED FOR GAS GATHERING PIPELINES							
M											ENDORSEMENT				TRANSMITTER					
											RELEASED FOR	DESIGN ENGR.	BFPC TECH. REP	SPDC TECH. REP	DATE	DRAWN: KIRAN P.		DATE: 26-07-2022	SHEET: 3 OF 6	
											A01	ISSUED FOR APPROVAL	KIRAN P.	PRINCE O.	KINGSLEY A.	26-07-22				
											R01	ISSUED FOR REVIEW	KIRAN P.	PRINCE O.	KINGSLEY A.	12-07-22	CHECKED: PRINCE O.	DRAWING No. EA-BFPC-L-GPMC-GGPL-FEED-ICS-DWG-019	REV.	
											REV		DRAWN	CHK	END	DATE	ENDORSED: KINGSLEY. A.	PROJECT No. --		
											COPY RIGHT RESERVED									

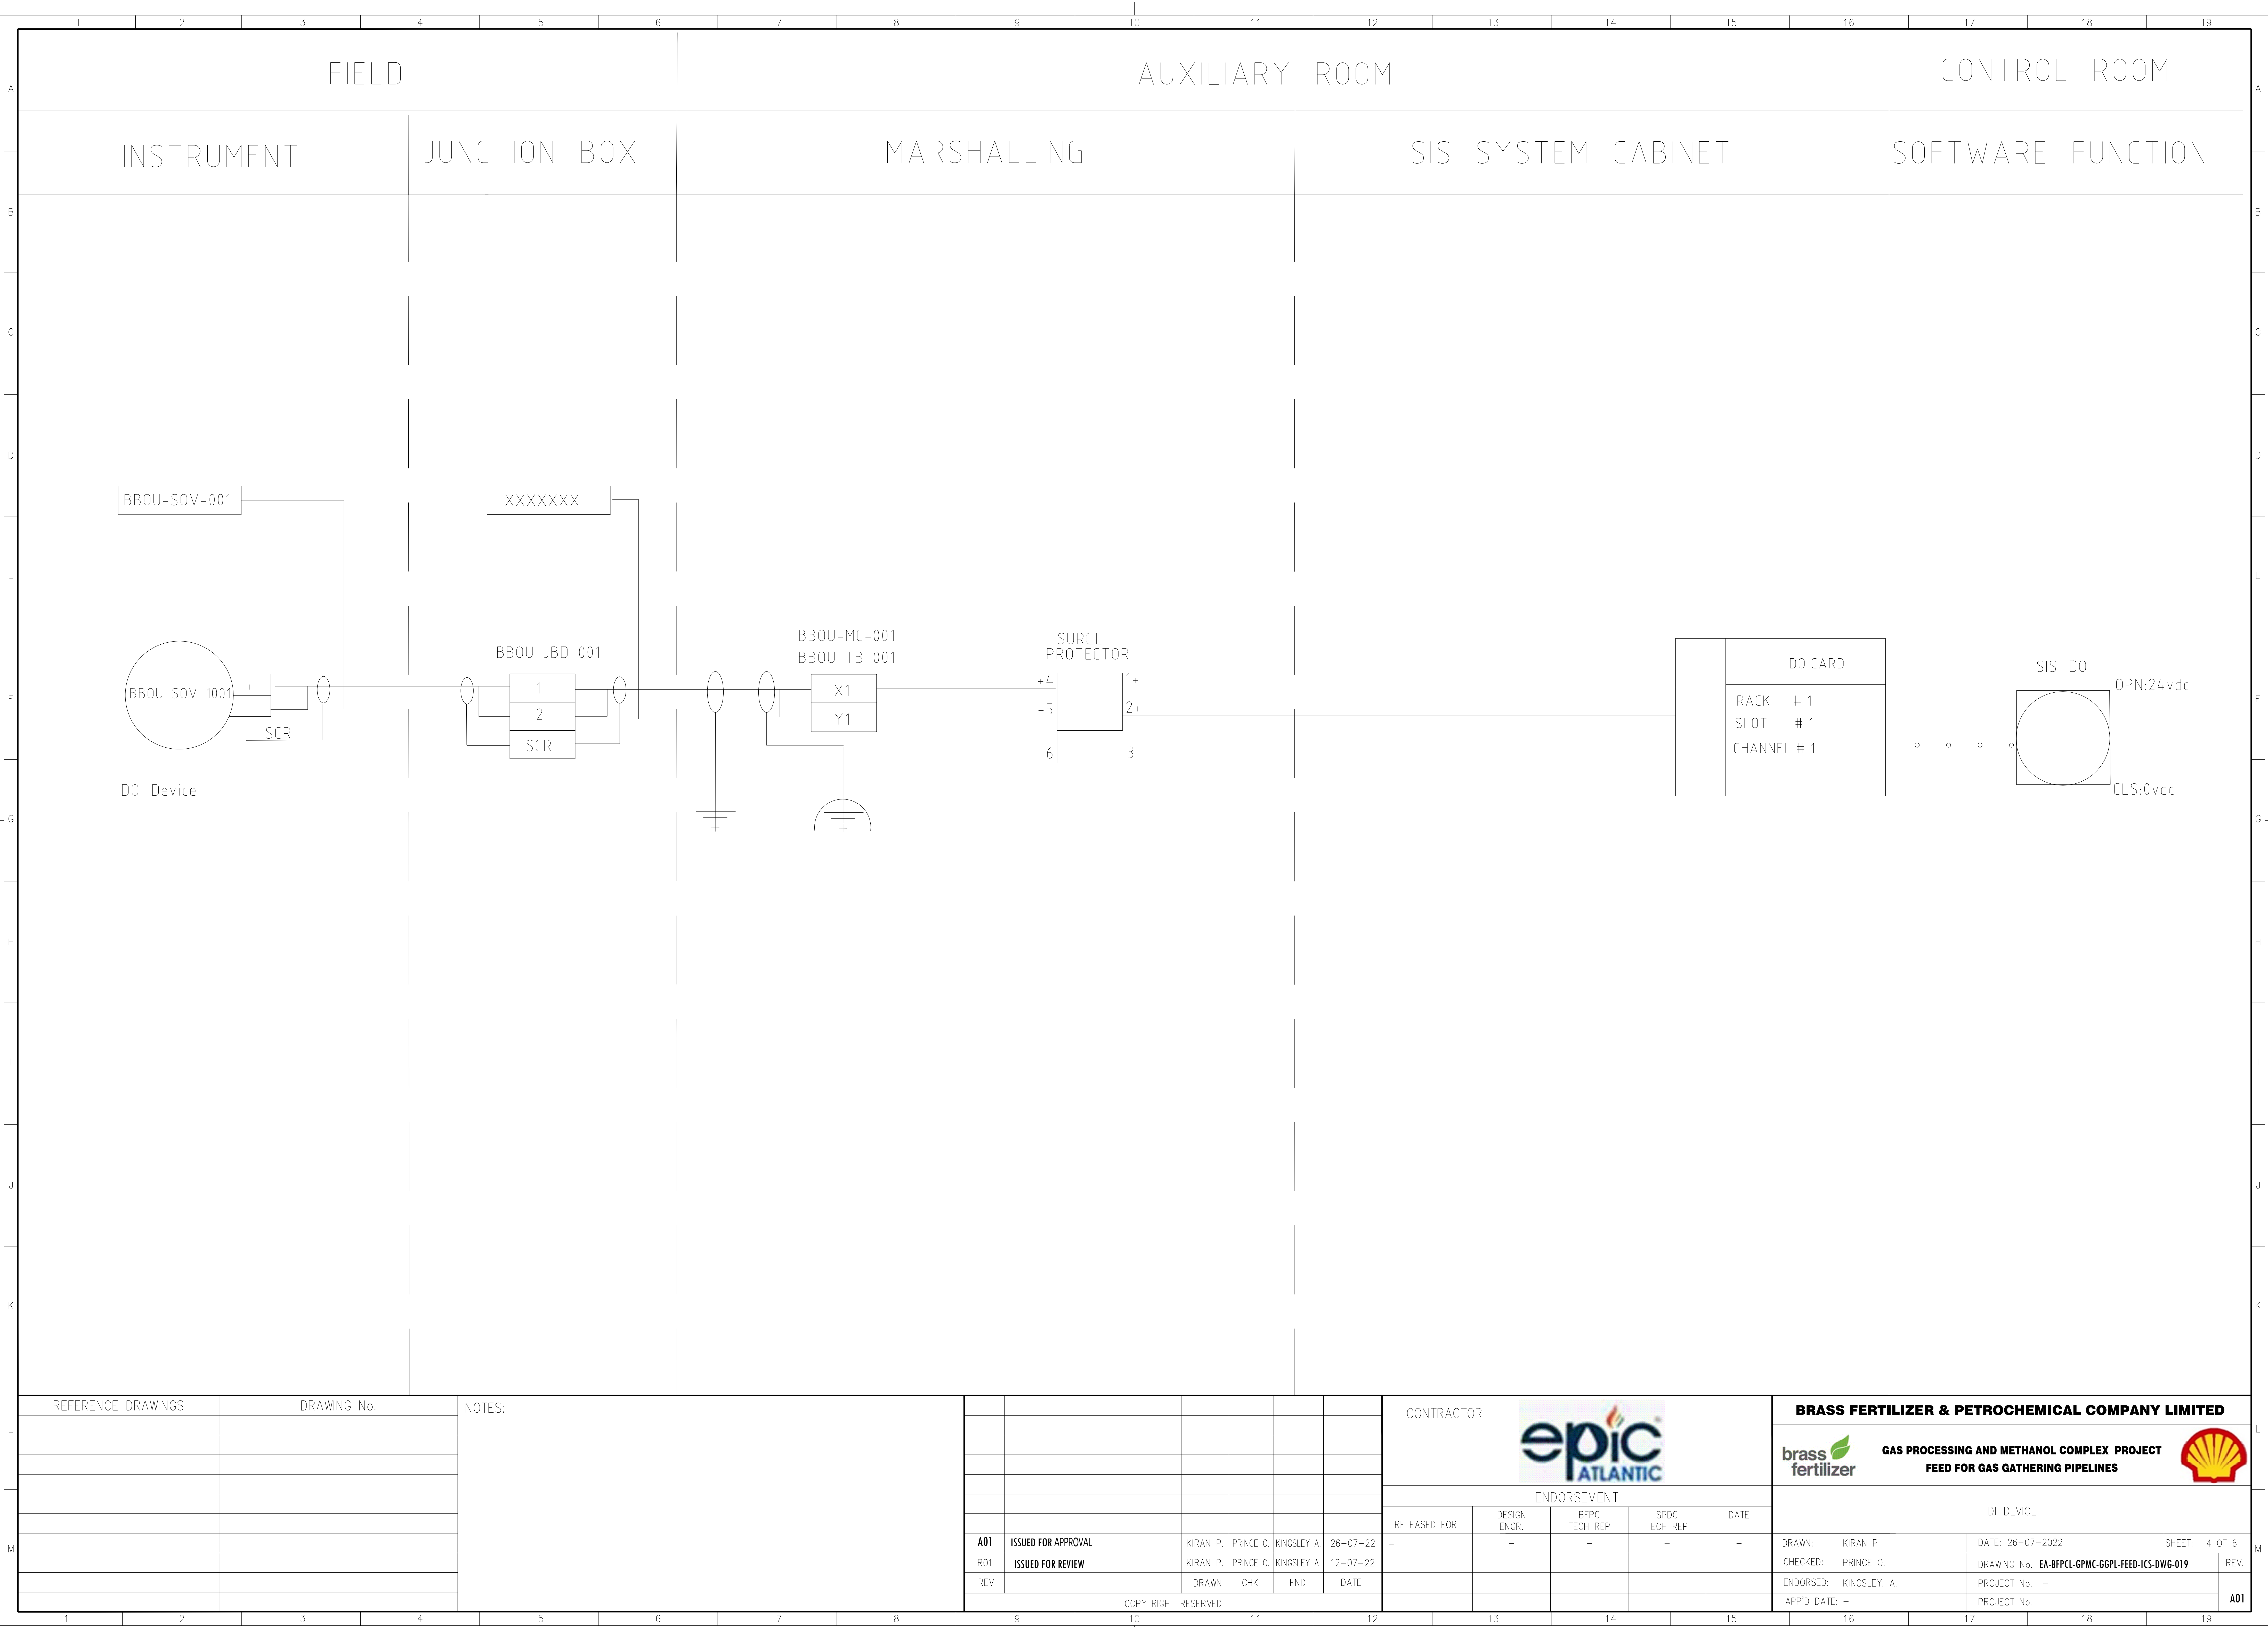

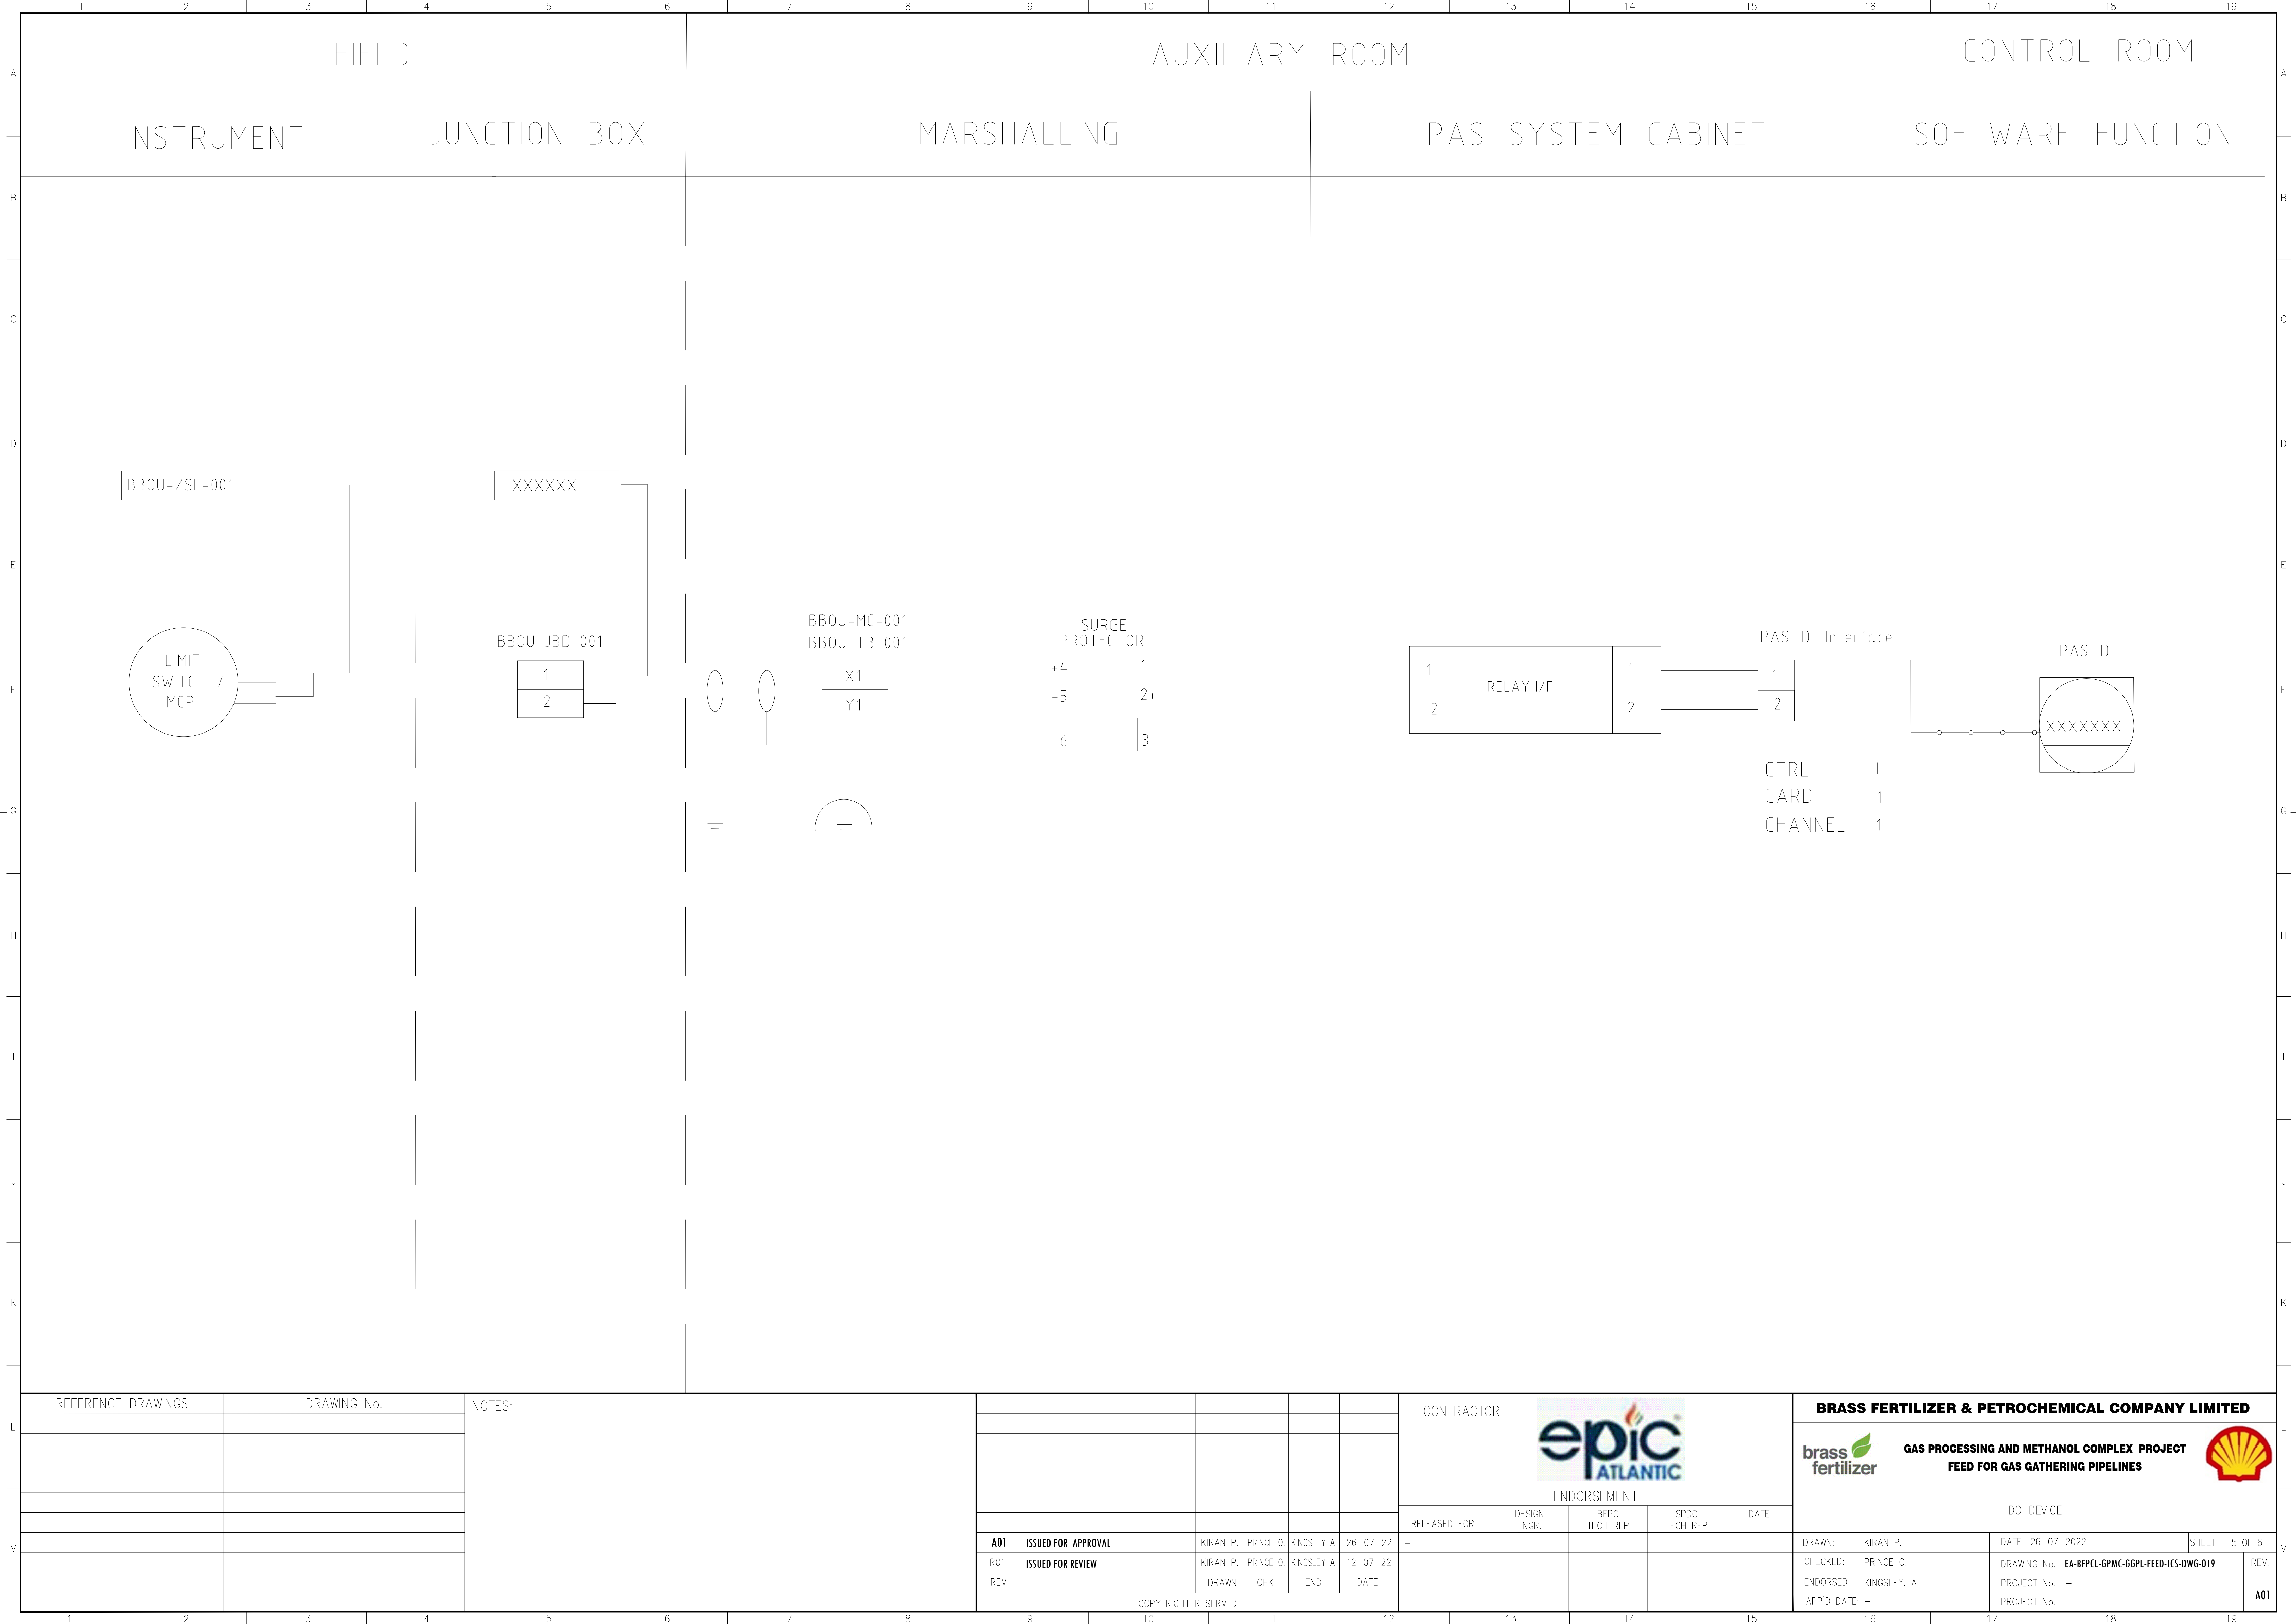

L	REFERENCE DRAWINGS		DRAWING No.		NOTES:	
---	--------------------	--	-------------	--	--------	--	--	

