


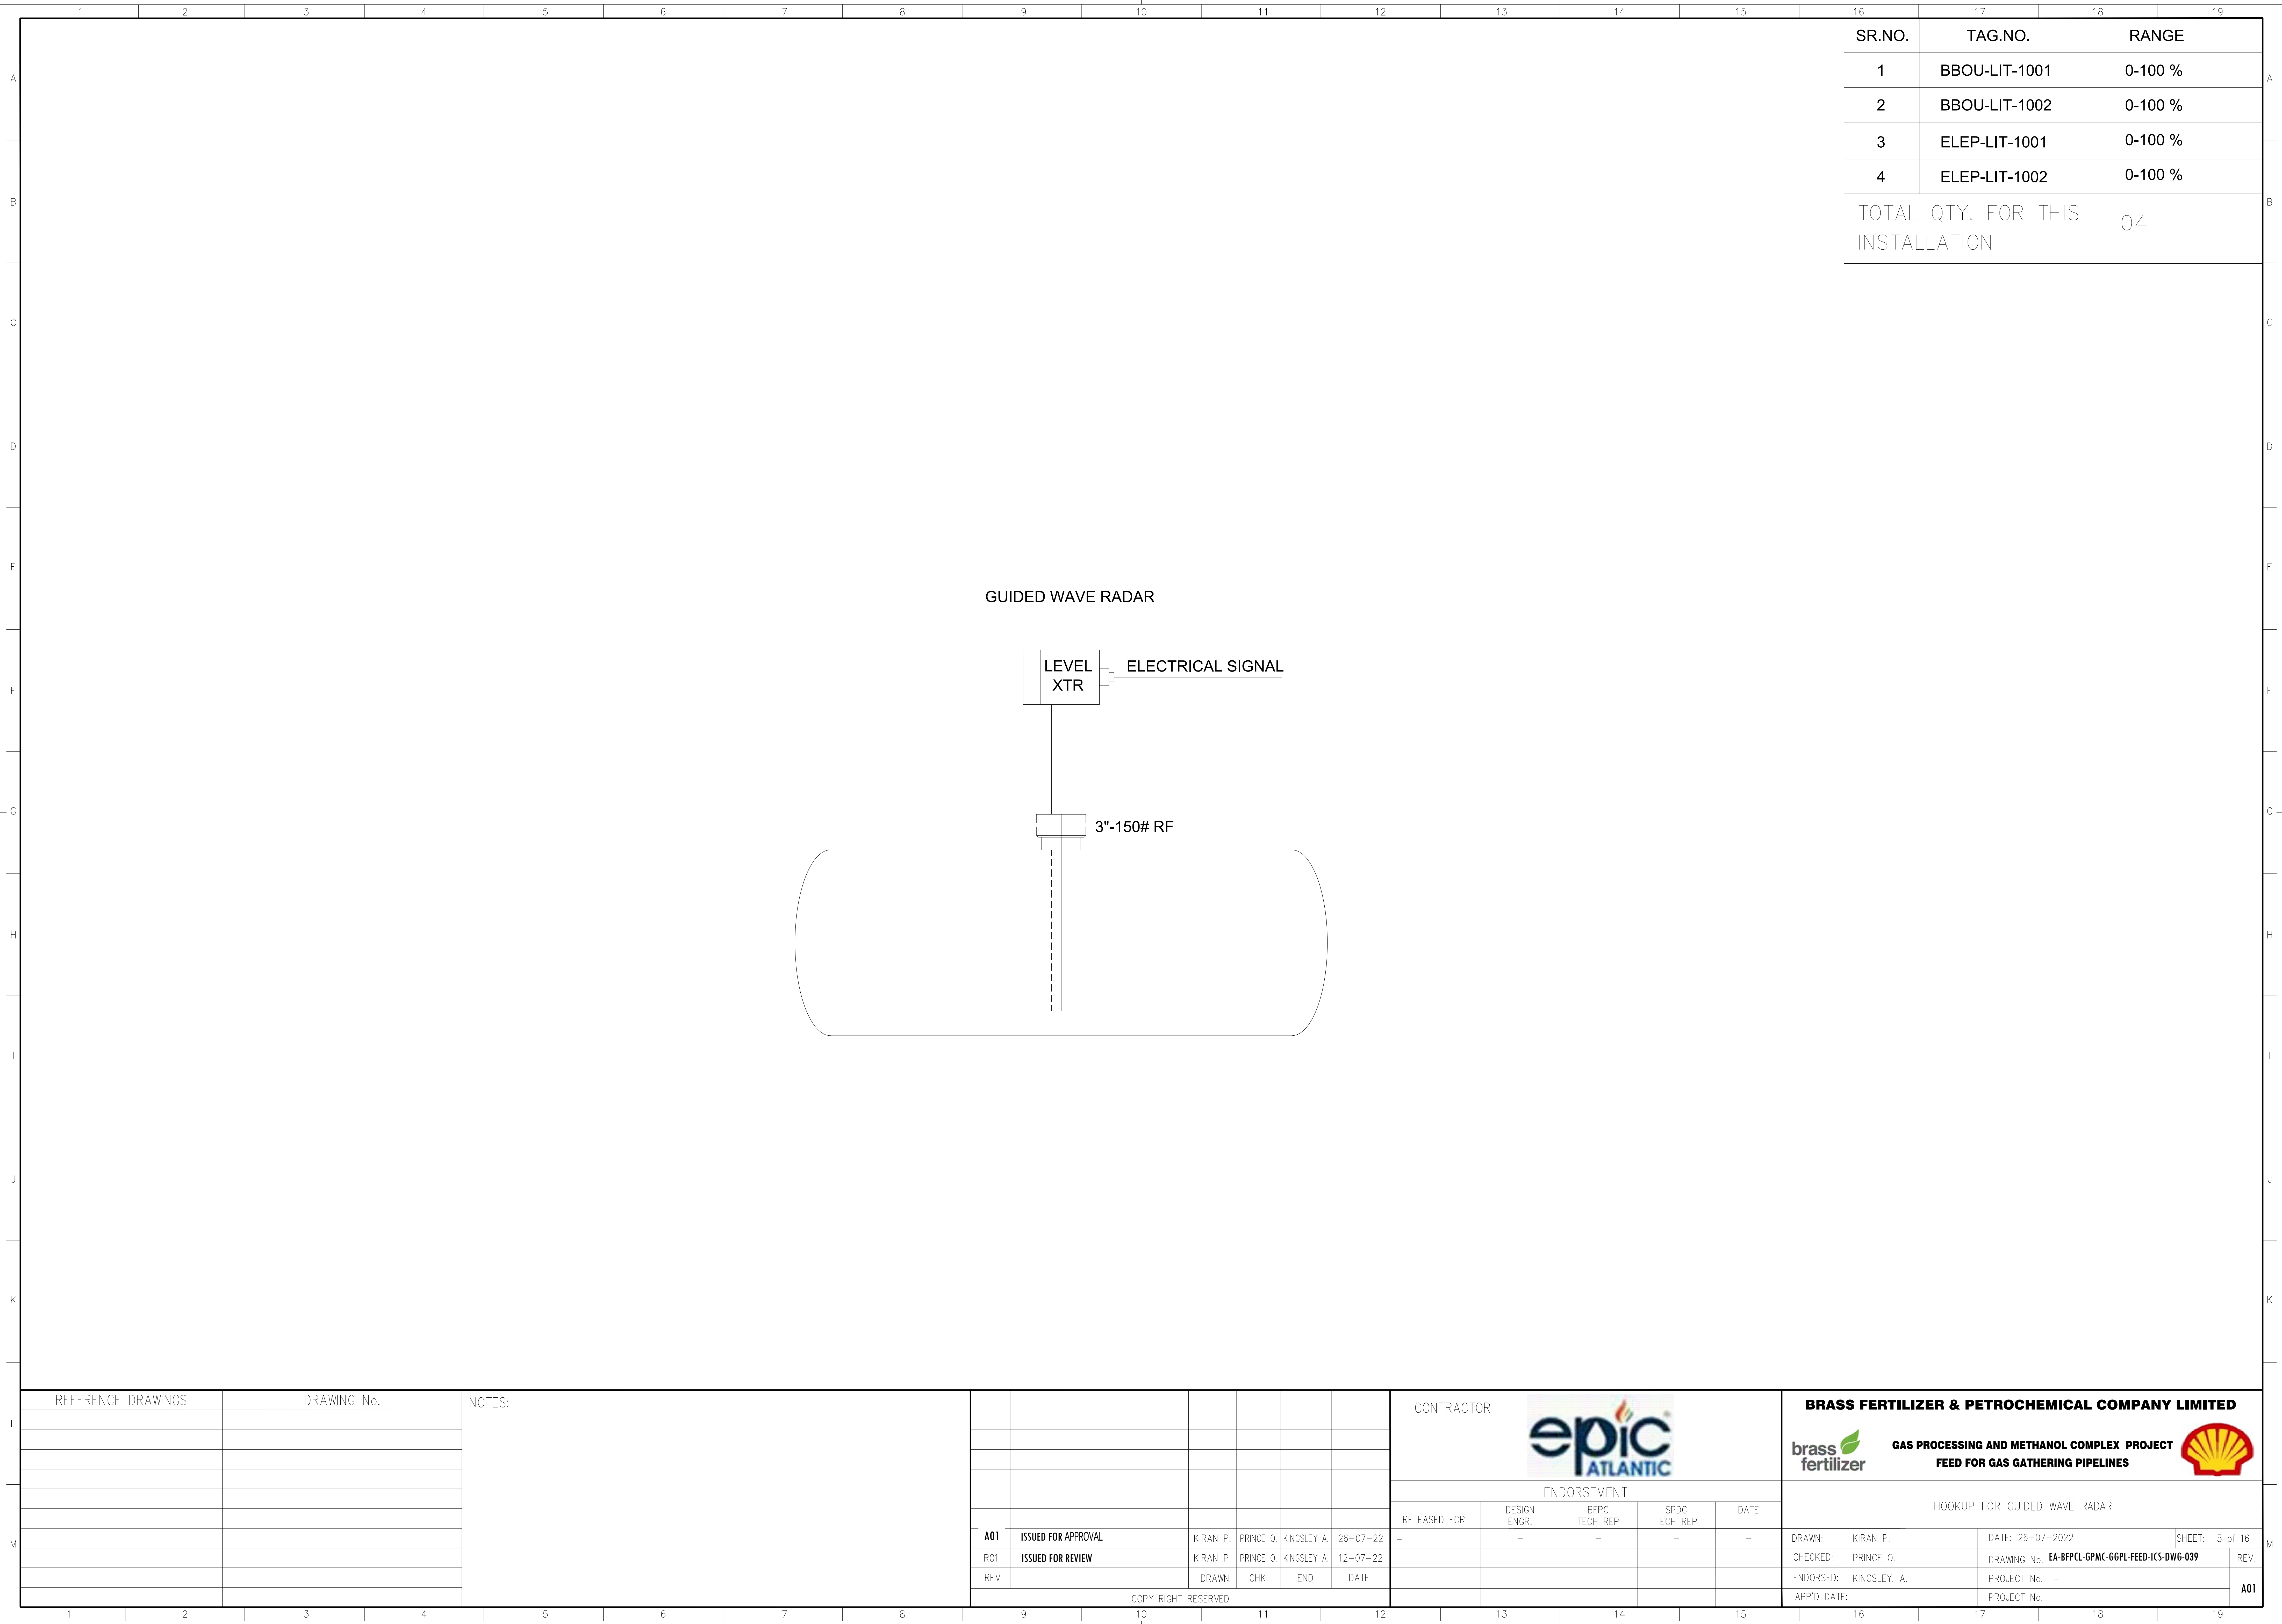

1

2

3

4

5

6

7

8

9

10

11

12

13

14


15

16

17

18







19

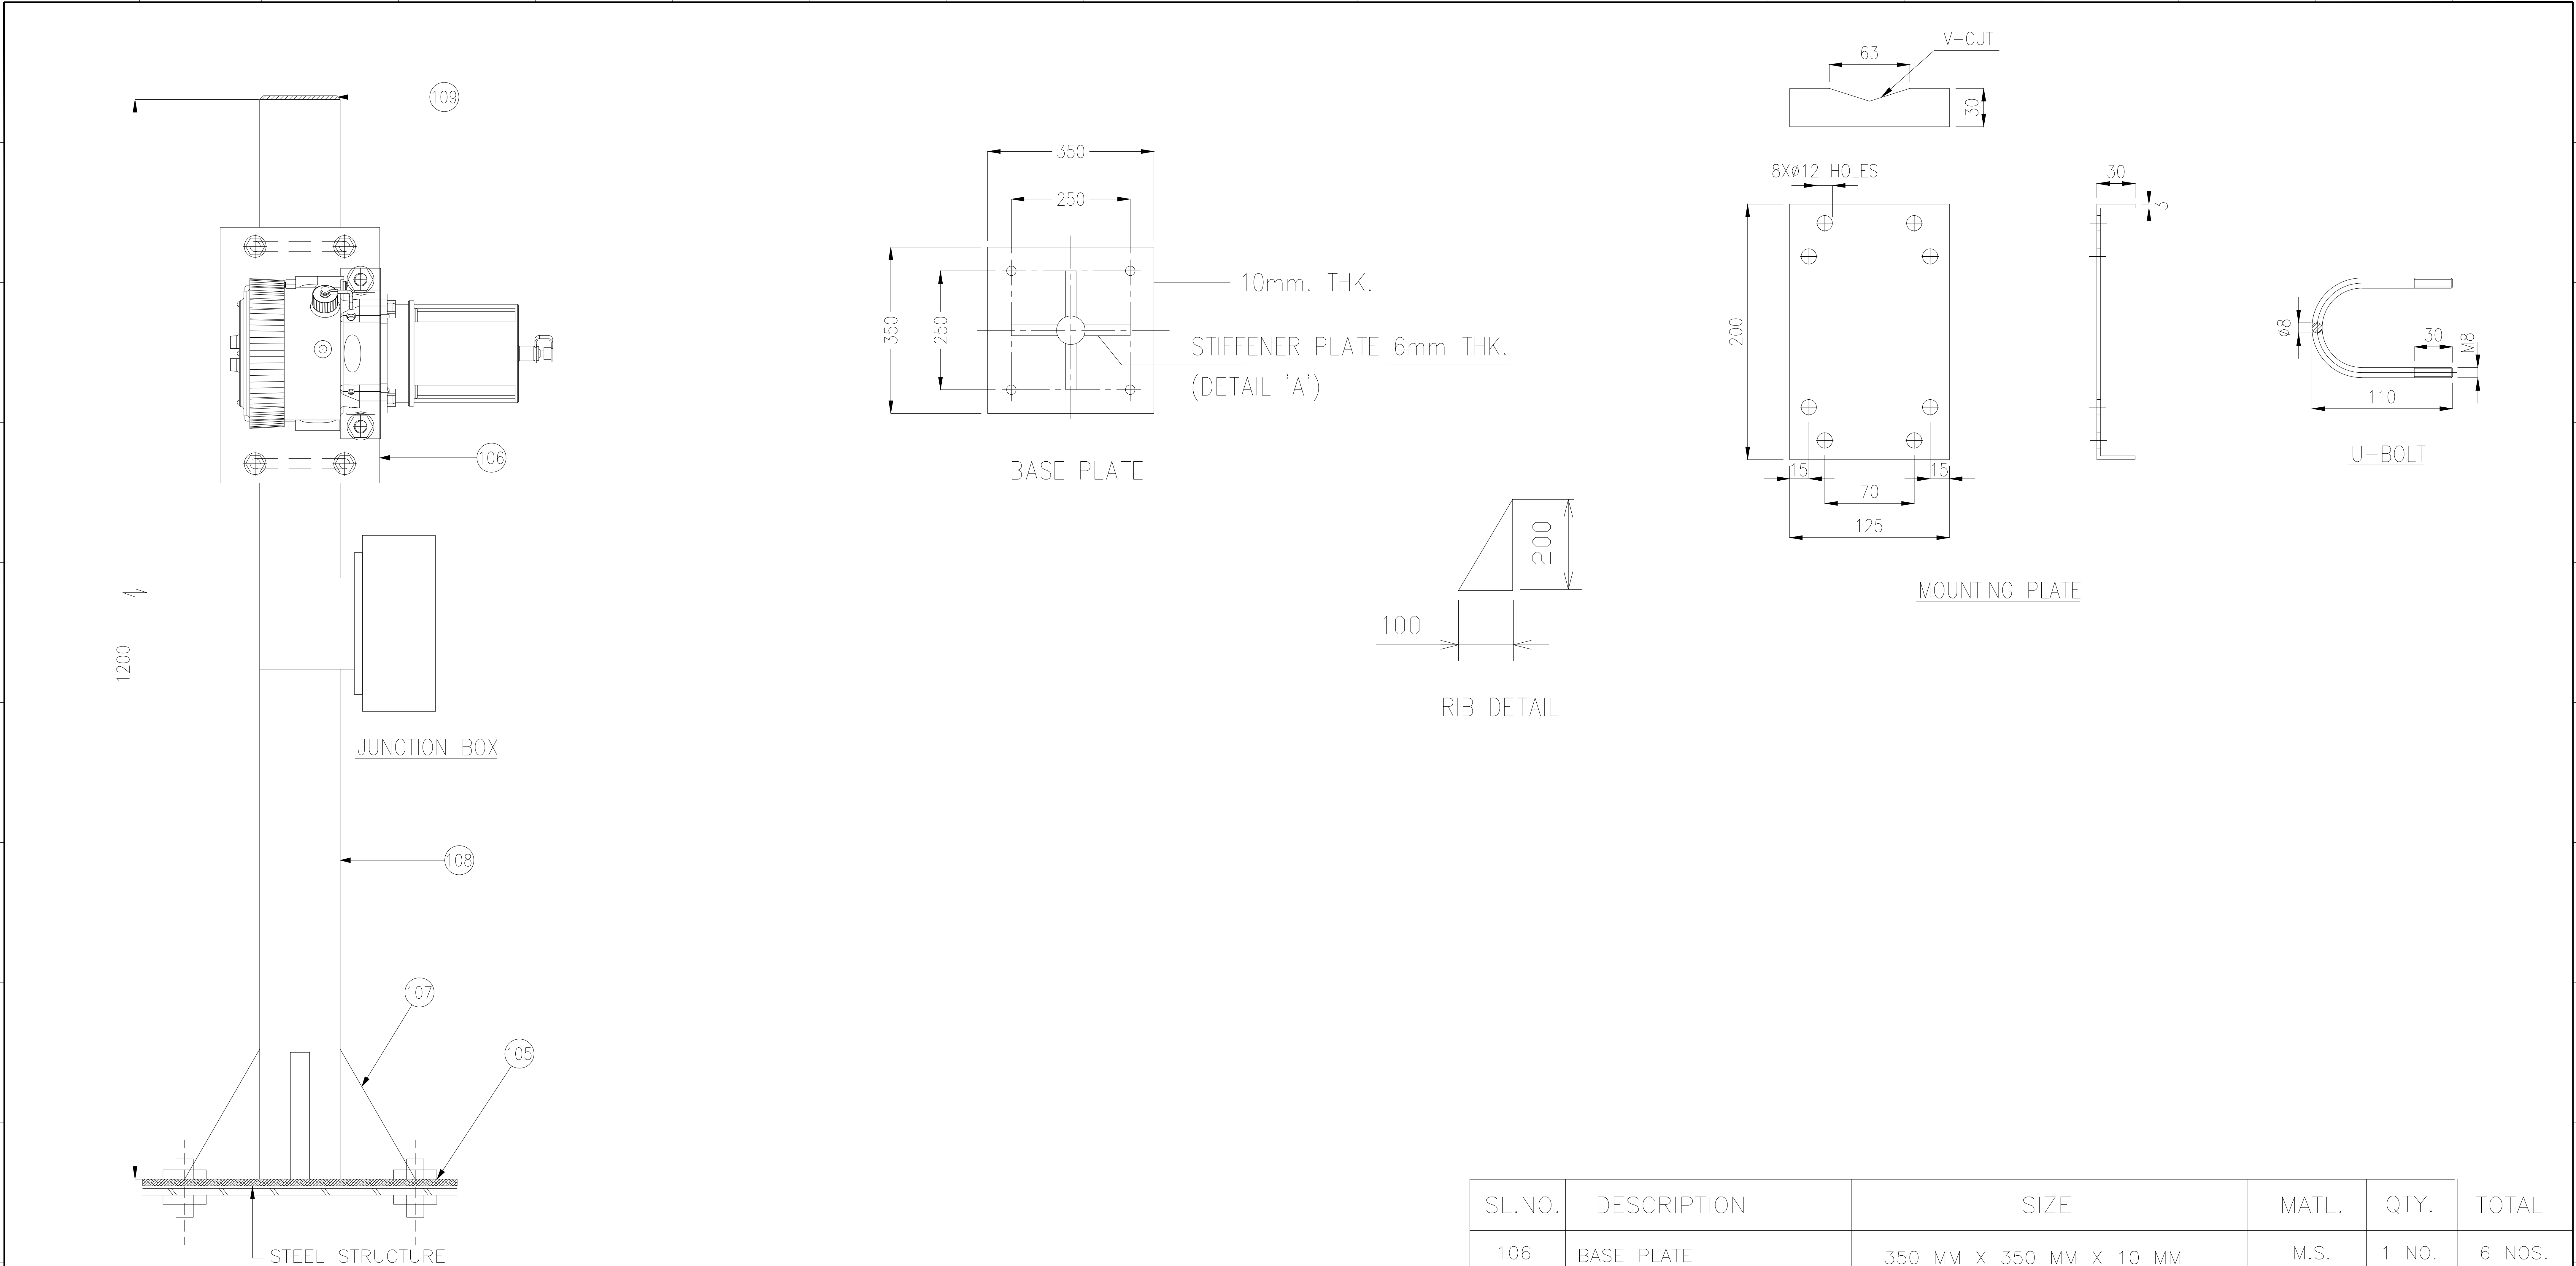

SL.NO.	DESCRIPTION	SIZE	MATL.	QTY.	TOTAL
106	BASE PLATE	350 MM X 350 MM X 10 MM	M.S.	1 NO.	6 NOS.
107	MOUNTING PLATE	200 MM X 125 MM X 3 MM	M.S.	1 NO.	6 NOS.
108	RIB PLATE	140 MM X 70 MM X 6 MM	M.S.	3 NOS.	18 NOS.
109	PIPE	2" NB	M.S.	1.2M	7.2M
110	TOP PLATE	ø63 X 3MM	M.S.	1 NO.	6 NOS.
111	U-BOLT,NUTS & WASHERS	M8	SS 304	2 SETS	12 SETS
112	BOLT, NUTS, WASHERS & SPRING WASHERS	M16x110 LONG	SS 304	2 SETS	12 SETS
113	BOLT, NUTS, WASHERS & SPRING WASHERS	M6	SS 304	2 SETS	12 SETS


TAG NO.	BBOU-AE/AT-1001	BBOU-AE/AT-1002	ELEP-AE/AT-1001	ELEP-AE/AT-1002	ELEP-AE/AT-1005	AKAB-AE/AT-1001
---------	-----------------	-----------------	-----------------	-----------------	-----------------	-----------------

REFERENCE DRAWINGS	DRAWING No.	NOTES:	
--------------------	-------------	--------	--	--	

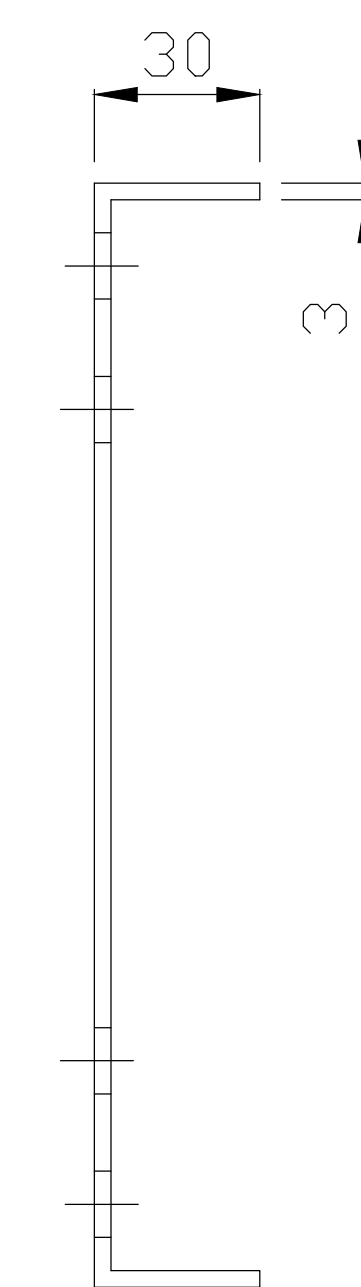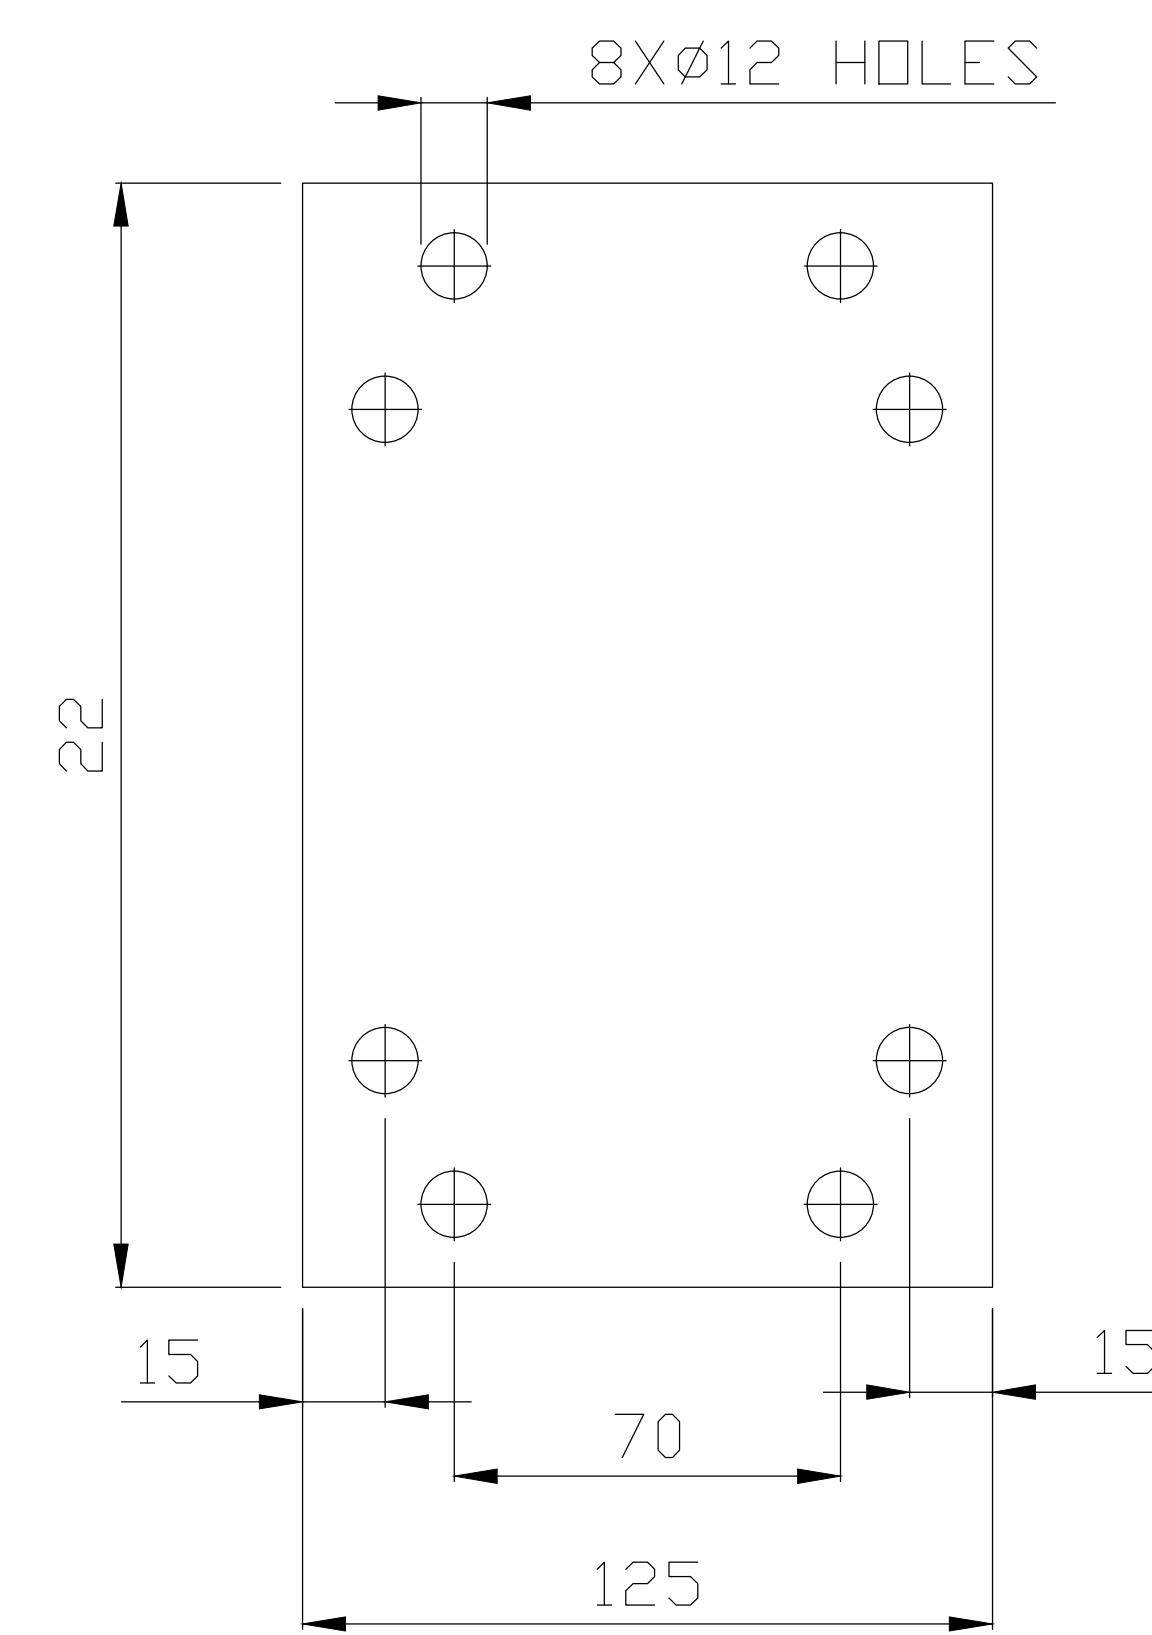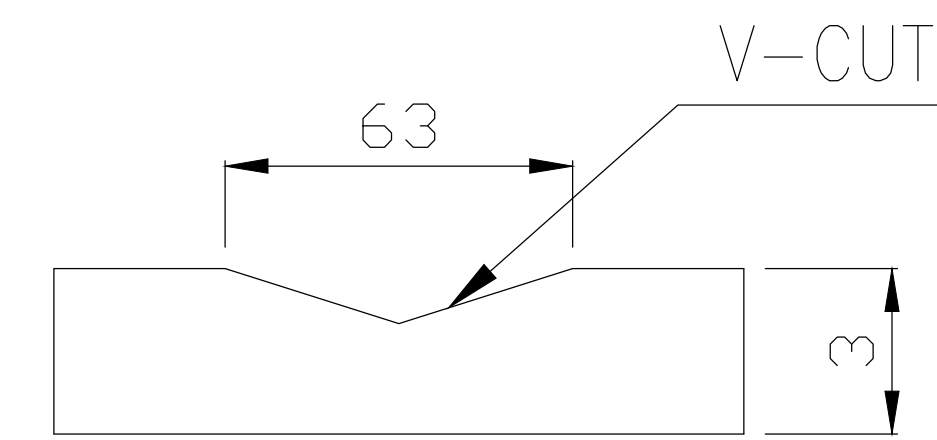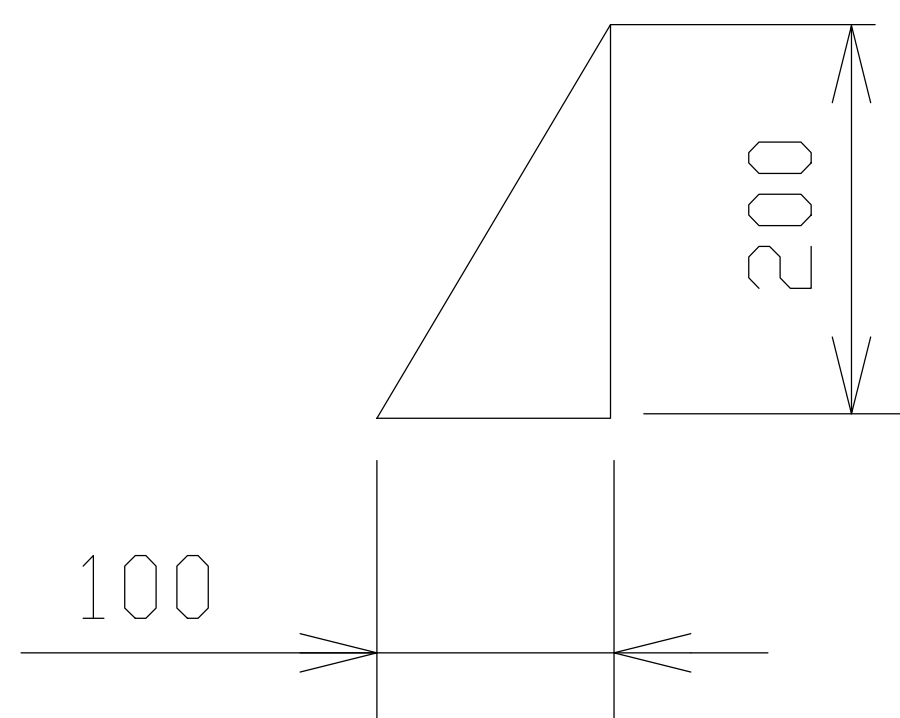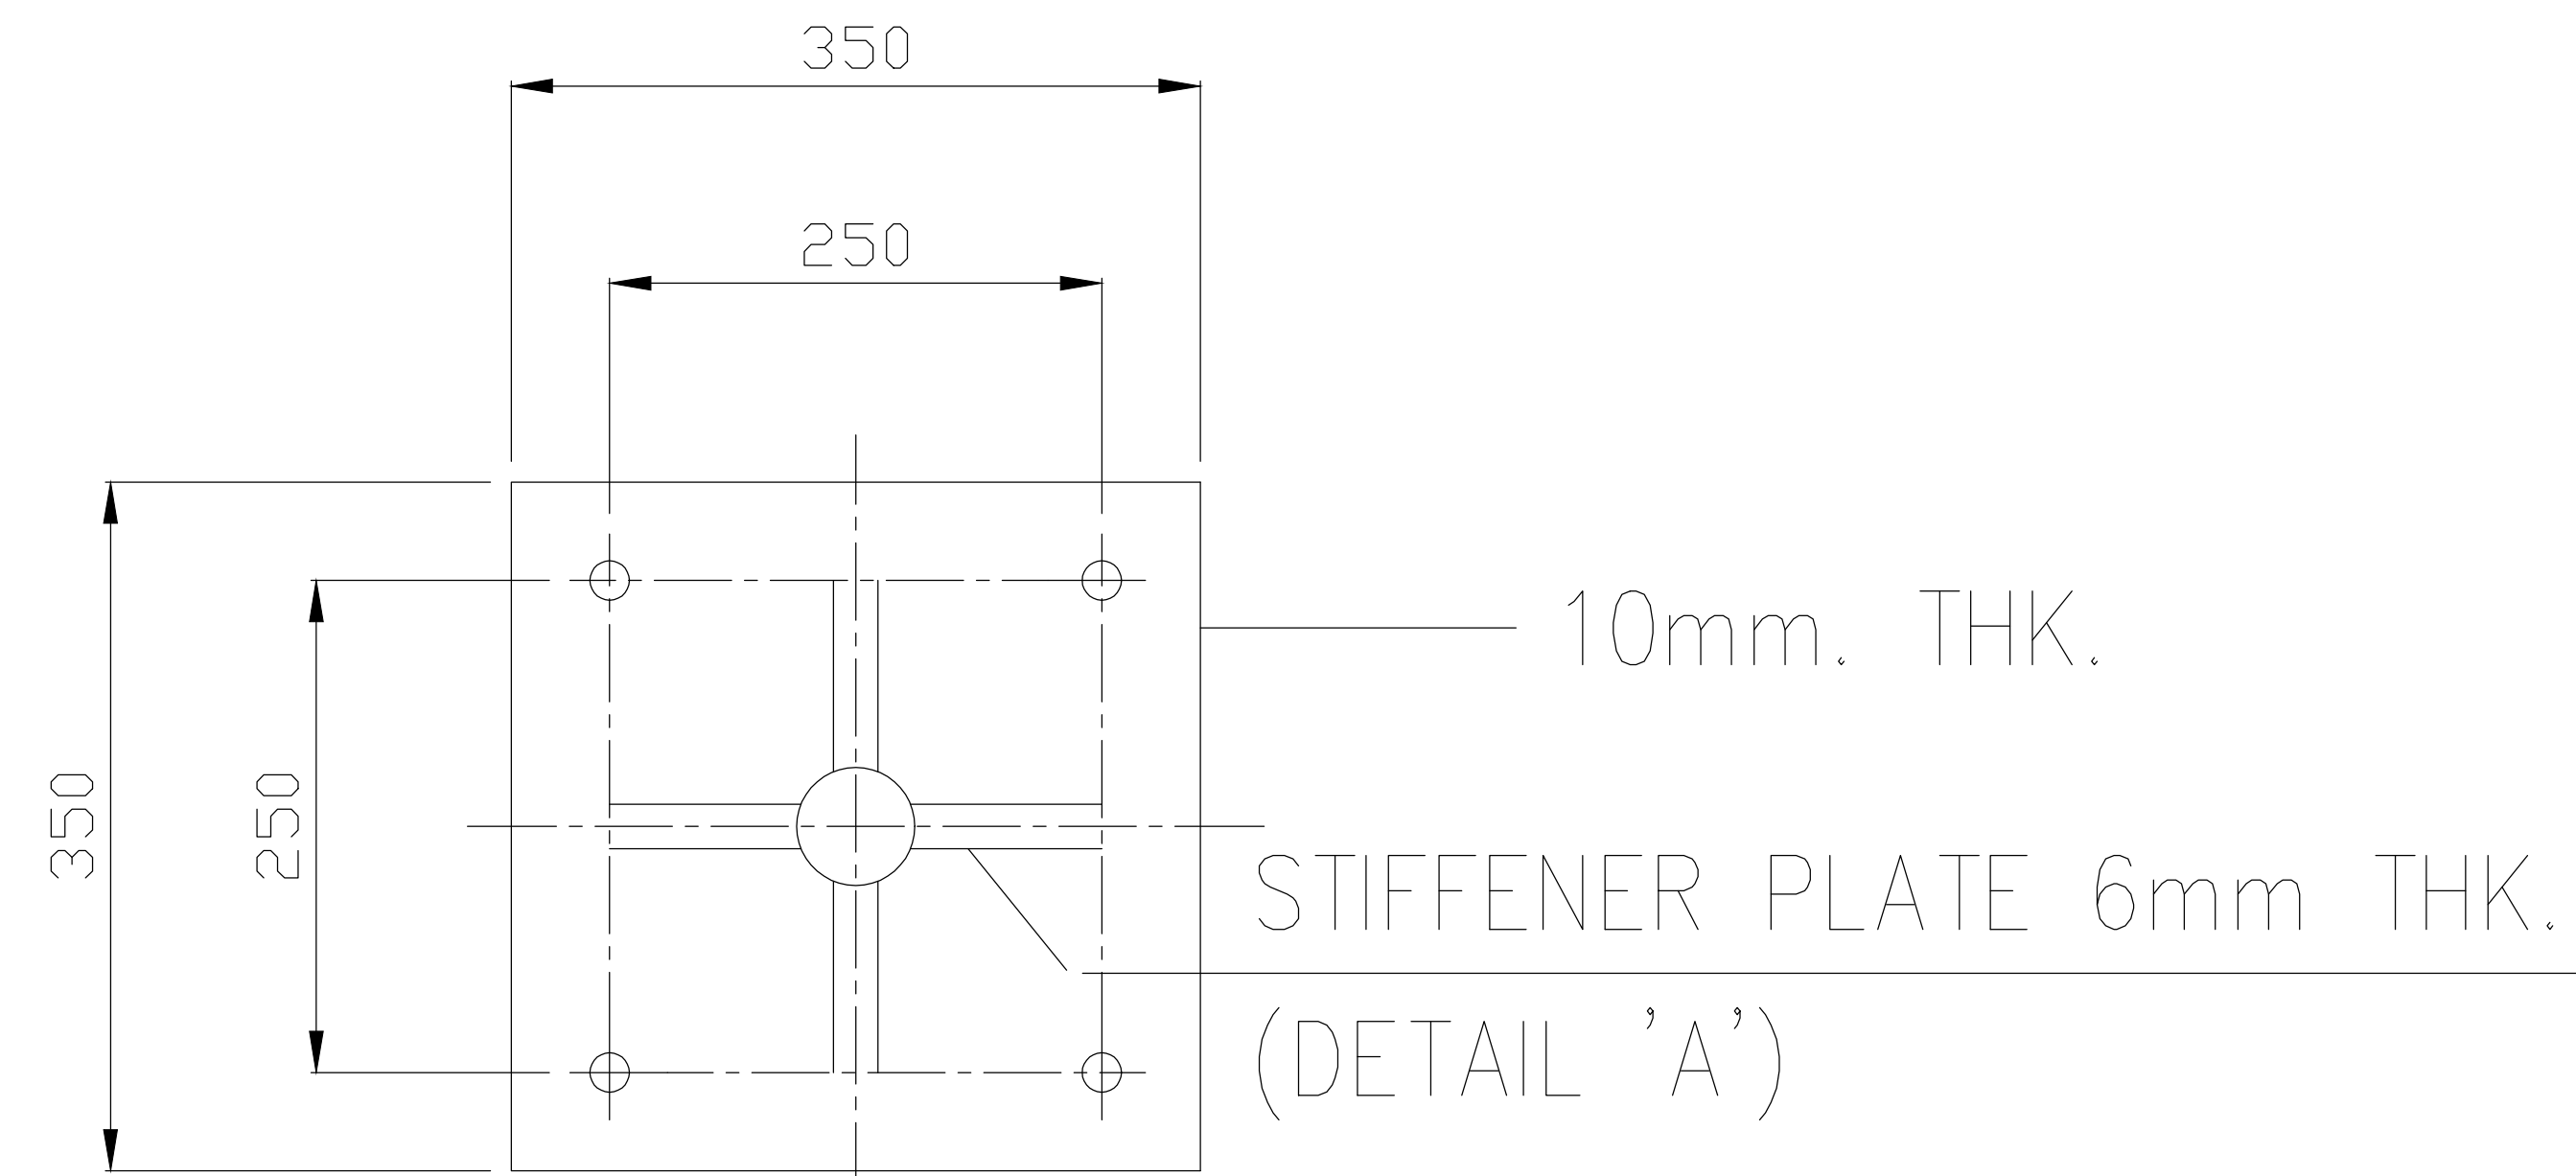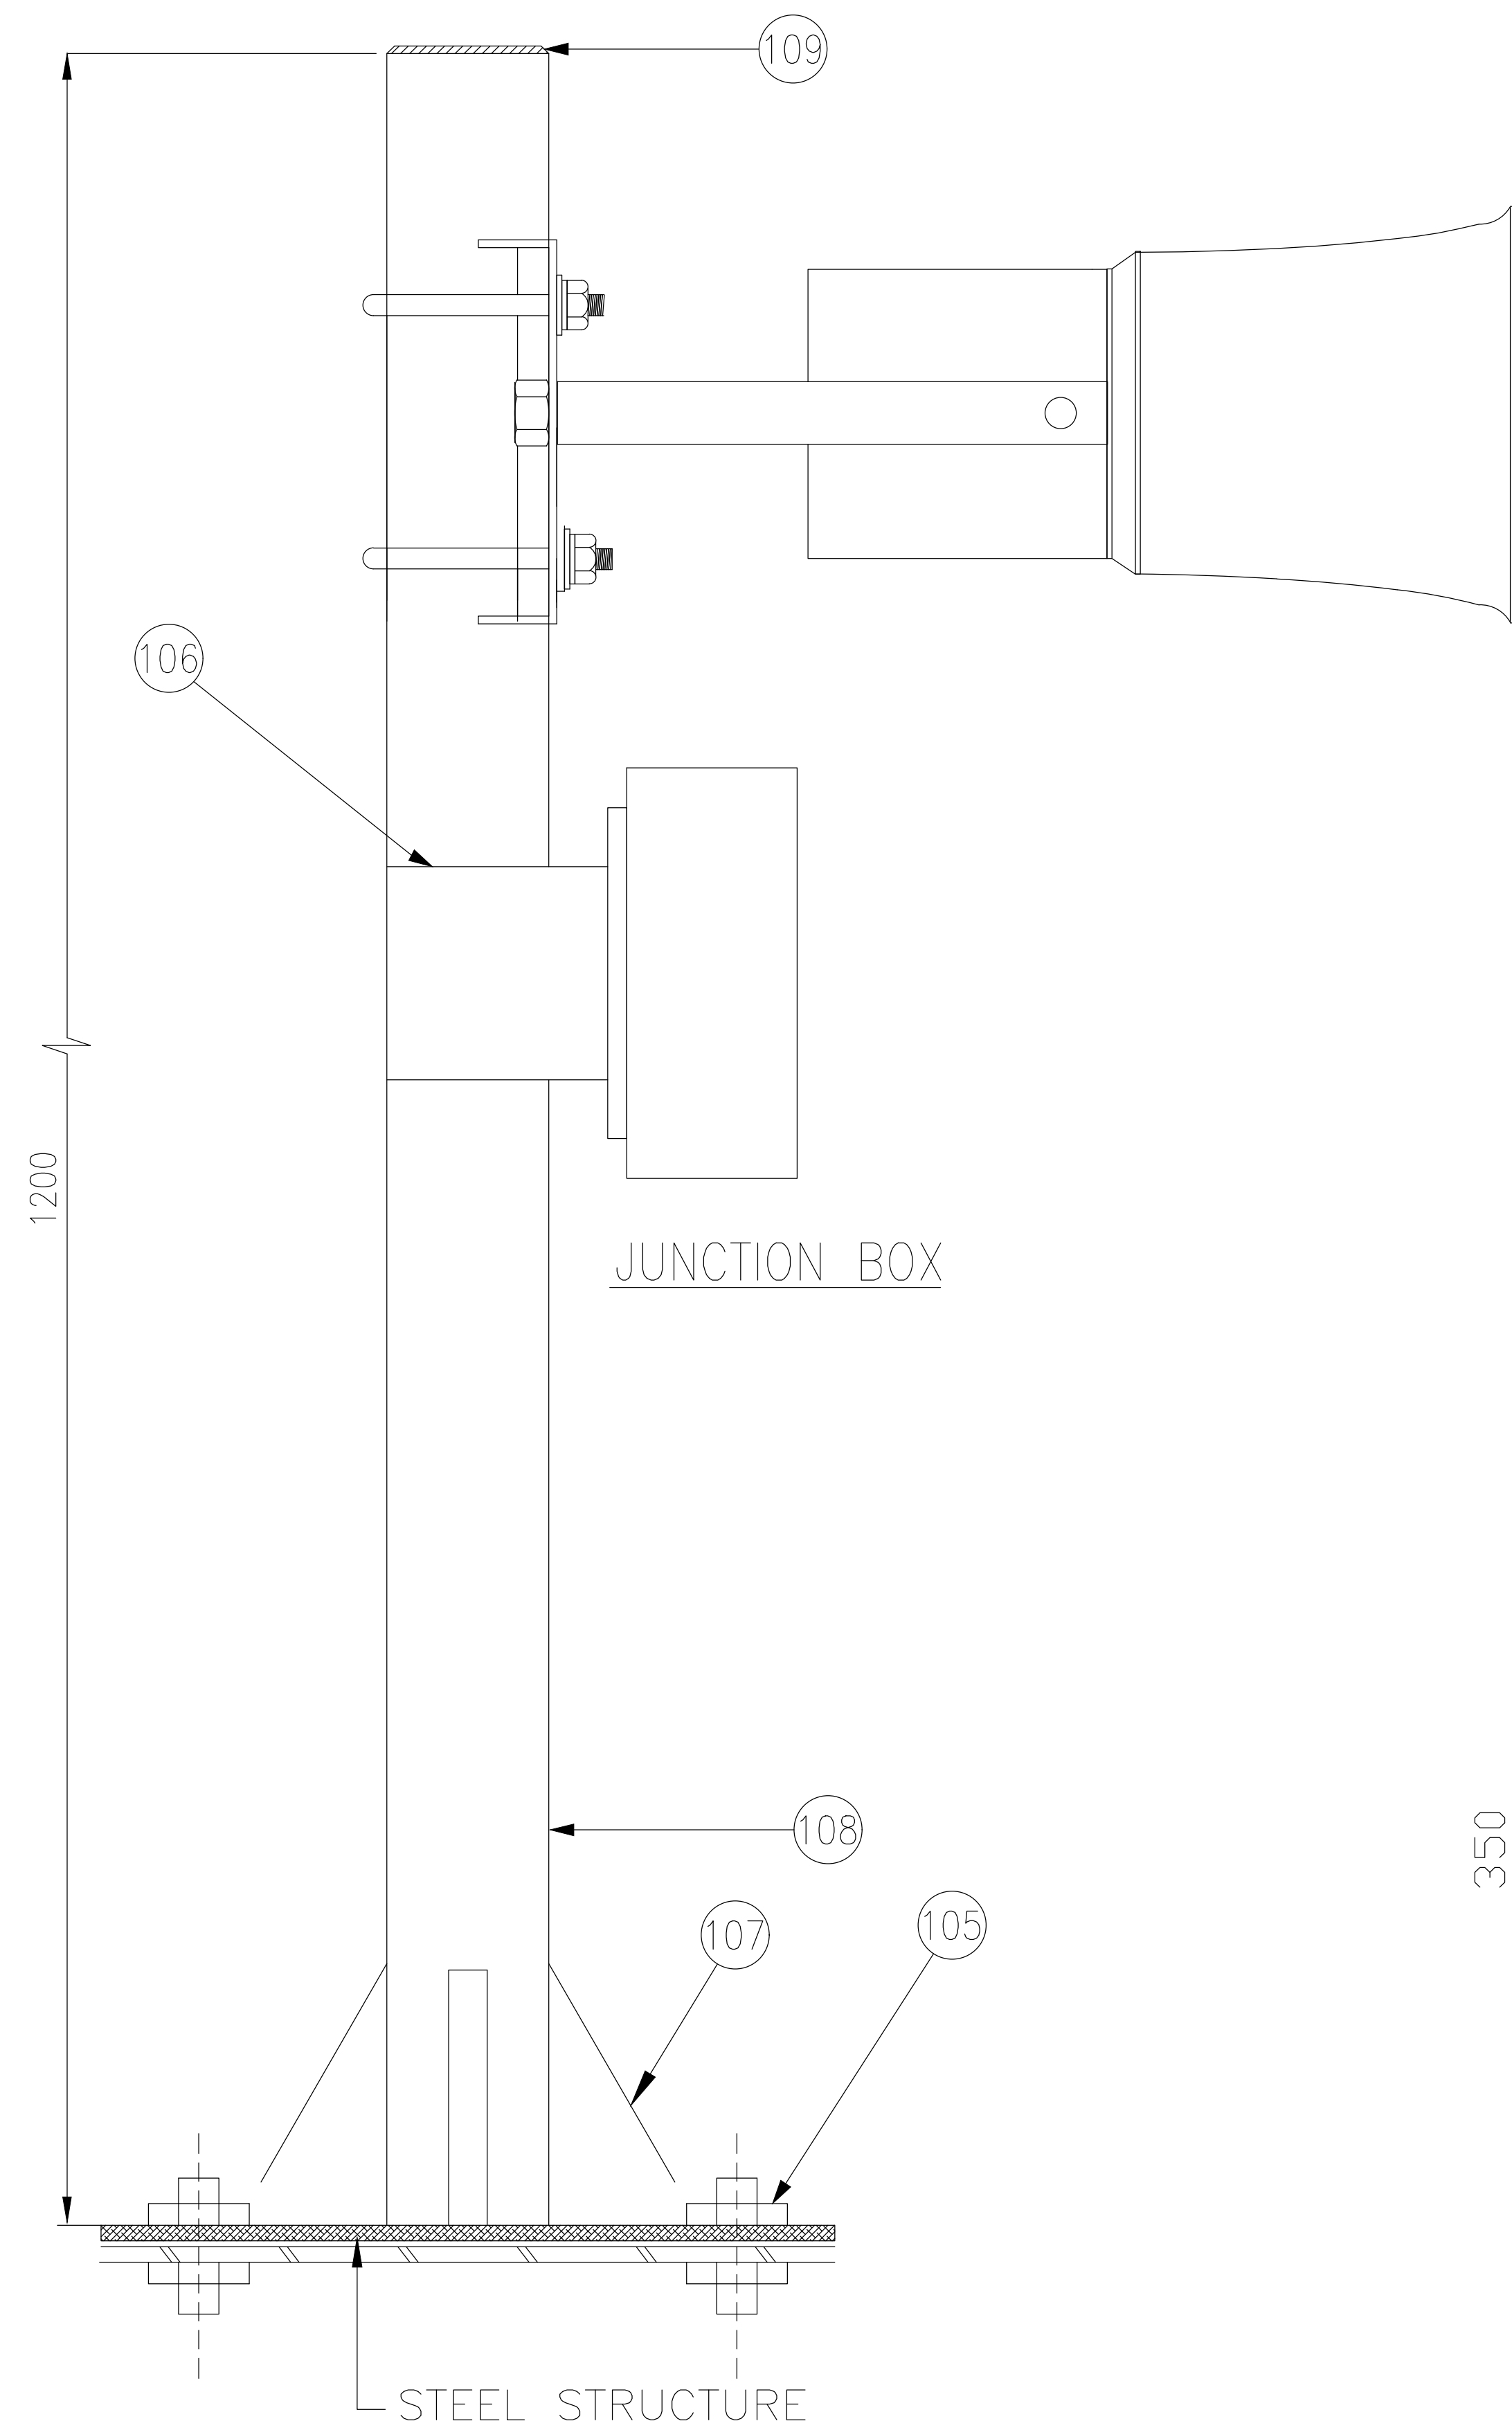

ITEM No.	TAG No.	
1	BBOU-HB-1004	
2	ELEP-HB-1004	
3	AKAB-HB-1003	
TOTAL QTY. FOR THIS		03
INSTALLATION		

REFERENCE DRAWINGS	DRAWING No.	NOTES:						CONTRACTOR					BRASS FERTILIZER & PETROCHEMICAL COMPANY LIMITED				
													 GAS PROCESSING AND METHANOL COMPLEX PROJECT 				
								ENDORSEMENT					INSTALLATION DIAGRAM FOR HOOTER & BEACON				
								RELEASED FOR	DESIGN ENGR.	BFPC TECH. REP	SPDC TECH. REP	DATE					
			A01	ISSUED FOR APPROVAL	KIRAN P.	PRINCE O.	KINGSLEY A.	26-07-22	-	-	-	-	-	DRAWN: KIRAN P.		DATE: 26-07-2022	SHEET: 7 of 16
			R01	ISSUED FOR REVIEW	KIRAN P.	PRINCE O.	KINGSLEY A.	12-07-22						CHECKED: PRINCE O.		DRAWING No. EA-BFPC-L-GPMC-GGPL-FEED-ICS-DWG-039	REV.
			REV		DRAWN	CHK	END	DATE						ENDORSED: KINGSLEY. A.		PROJECT No. -	A01
			COPY RIGHT RESERVED										APP'D DATE: -		PROJECT No.		

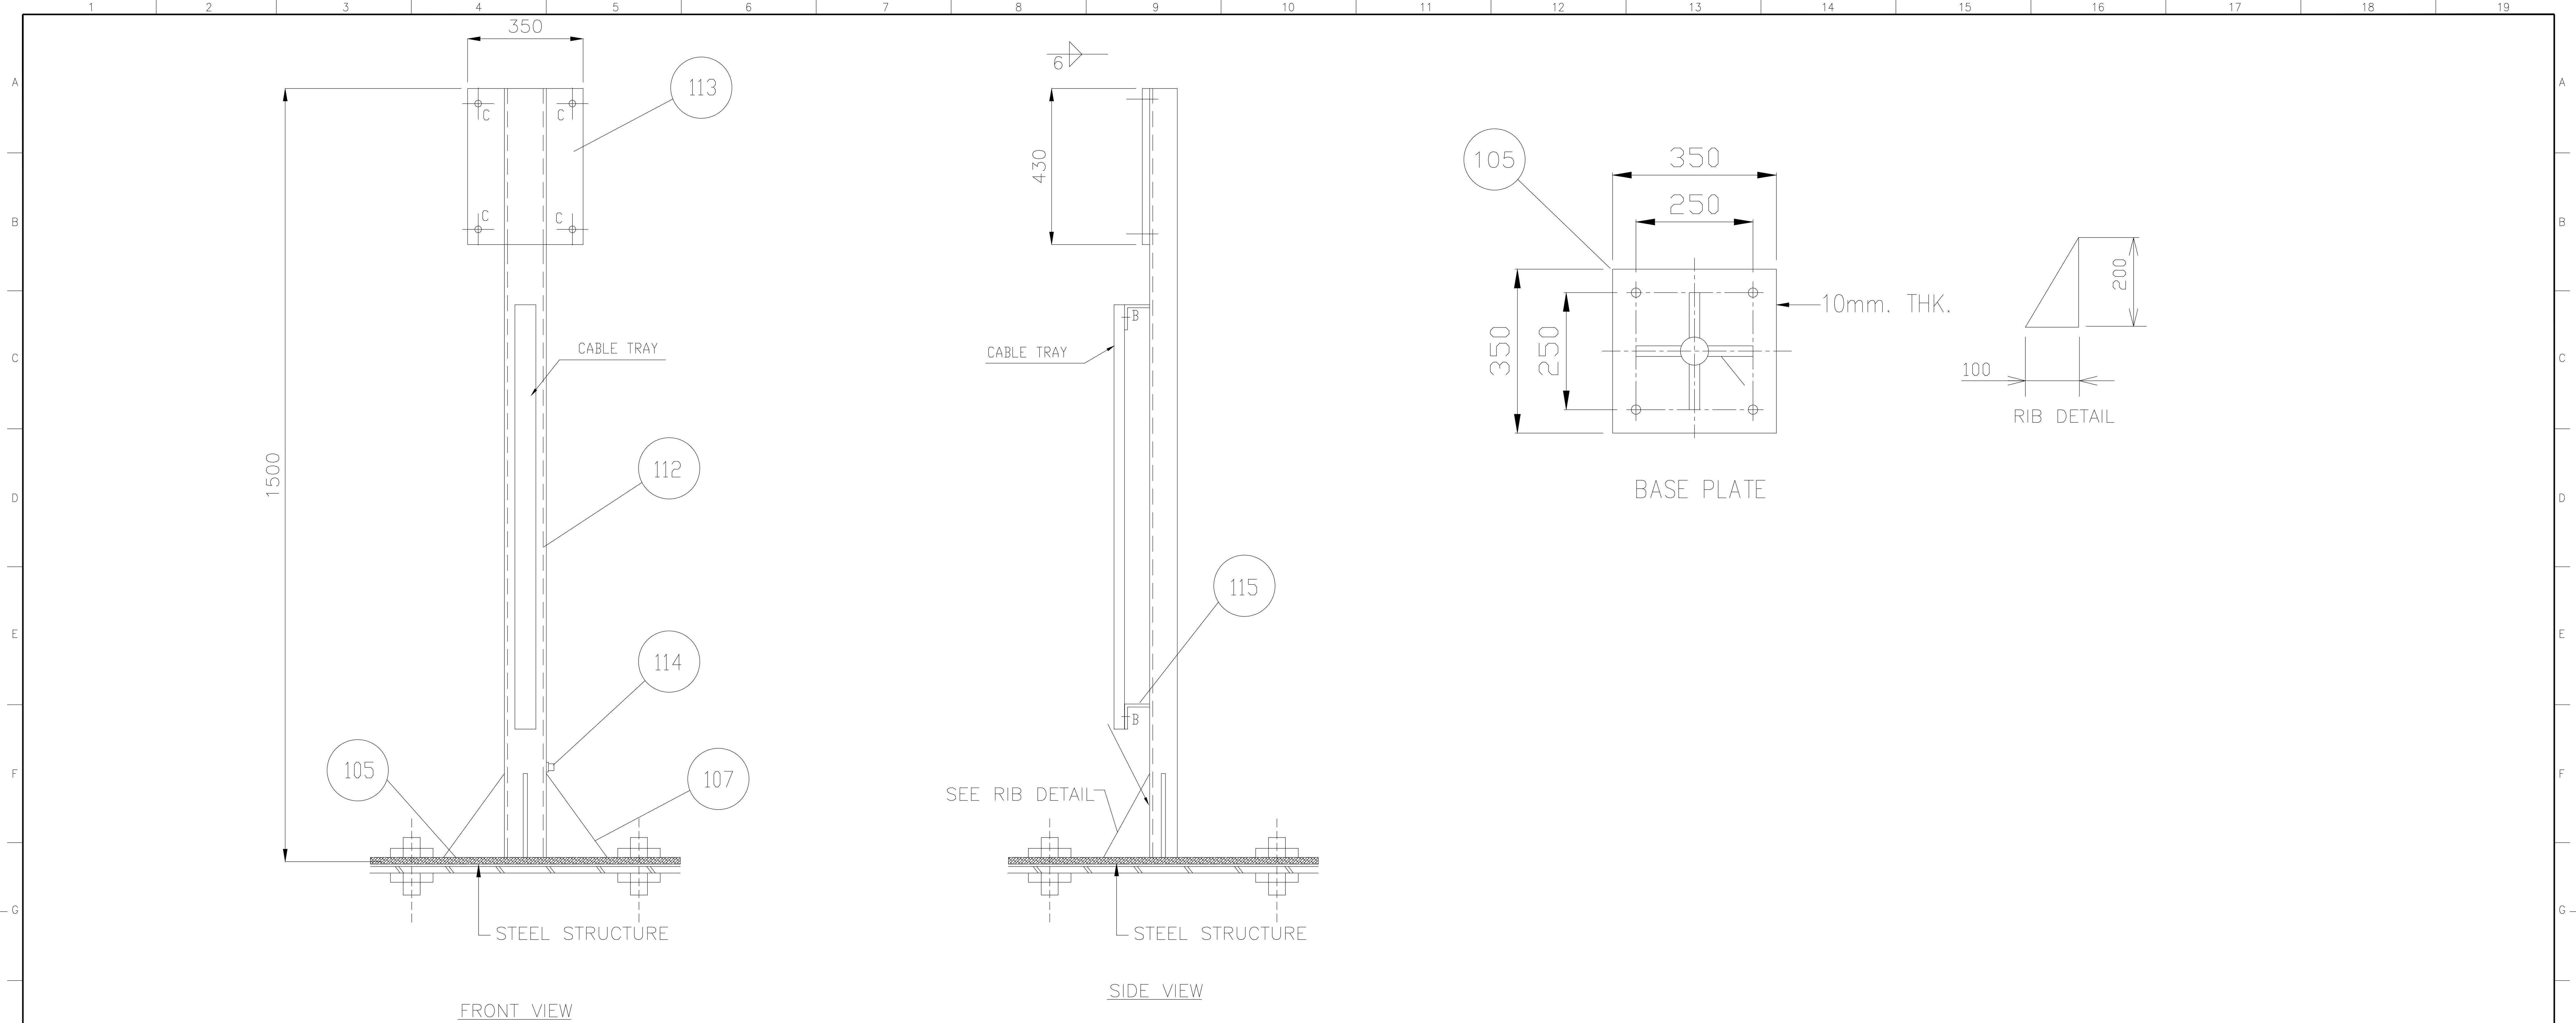


TOTAL STEEL STRUCTURE WEIGHT = 216.12 Kg.

NOTES :
HOLE SIZE 'A' – 8 NOS. 14mm DIA. FOR MOUNTING OF INSTRUMENT STAND.
8 NOS M10 BOLT C/W NUTS AND WASHERS.
HOLE SIZE 'B' – 8 NOS. 8mm DIA. FOR MOUNTING JUNCTION BOX.
8 NOS. M6 BOLT C/W NUTS AND WASHERS.

MATERIAL DESCRIPTION

SL.NO.	DESCRIPTION	SIZE	MATL	QTY.	TOTAL QTY.	UNIT WT.	TOTAL WT.
112	1.5M LG MS CHANNEL	100mm x 50mm x 6mm THK	M.S.	1	8	13.8 Kg	110.4 Kg
105	BASE PLATE	350mm x 350mm x 10mm THK	M.S.	1	8	0.49 Kg	3.92 Kg
115	1100mm LG ANGLE IRON	50mm x 50mm x 6mm THK	M.S.	2	16	4.95 Kg	79.2 Kg
107	RIB PLATE	75mm x 200mm x 6mm THK	M.S.	3	24	0.7065 Kg	16.95 Kg
113	STEEL PLATE	350mm X 430mm X 10mm THK.	M.S.	1	8	0.7065 Kg	5.65 Kg
114	EARTH BOSS c/w EARTH STUD & ACCESSORIES	M10	S.S	1	8	–	–
111	BOLT, NUTS, WASHERS & SPRING WASHERS	M16x110 LONG	S.S	4	32	–	–

L	REFERENCE DRAWINGS	DRAWING No.	NOTES:							CONTRACTOR		BRASS FERTILIZER & PETROCHEMICAL COMPANY LIMITED													
													GAS PROCESSING AND METHANOL COMPLEX PROJECT												
													FEED FOR GAS GATHERING PIPELINES												
													INSTALLATION DRAWING JUNCTION BOX (SINGLE) MOUNTING STAND												
M												ENDORSEMENT													
												RELEASED FOR	DESIGN ENGR.	BFPC TECH REP	SPDC TECH REP	DATE									
												A01	ISSUED FOR APPROVAL	KIRAN P.	PRINCE O.	KINGSLEY A.	26-07-22	-	-	-	-	-	DRAWN: KIRAN P.	DATE: 26-07-2022	SHEET: 8 of 16
												R01	ISSUED FOR REVIEW	KIRAN P.	PRINCE O.	KINGSLEY A.	12-07-22						CHECKED: PRINCE O.	DRAWING No. EA-BFPCL-GPMC-GGPL-FEED-ICS-DWG-039	REV.
												REV		DRAWN	CHK	END	DATE						ENDORSED: KINGSLEY. A.	PROJECT No. -	
												COPY RIGHT RESERVED											APP'D DATE: -	PROJECT No.	A01

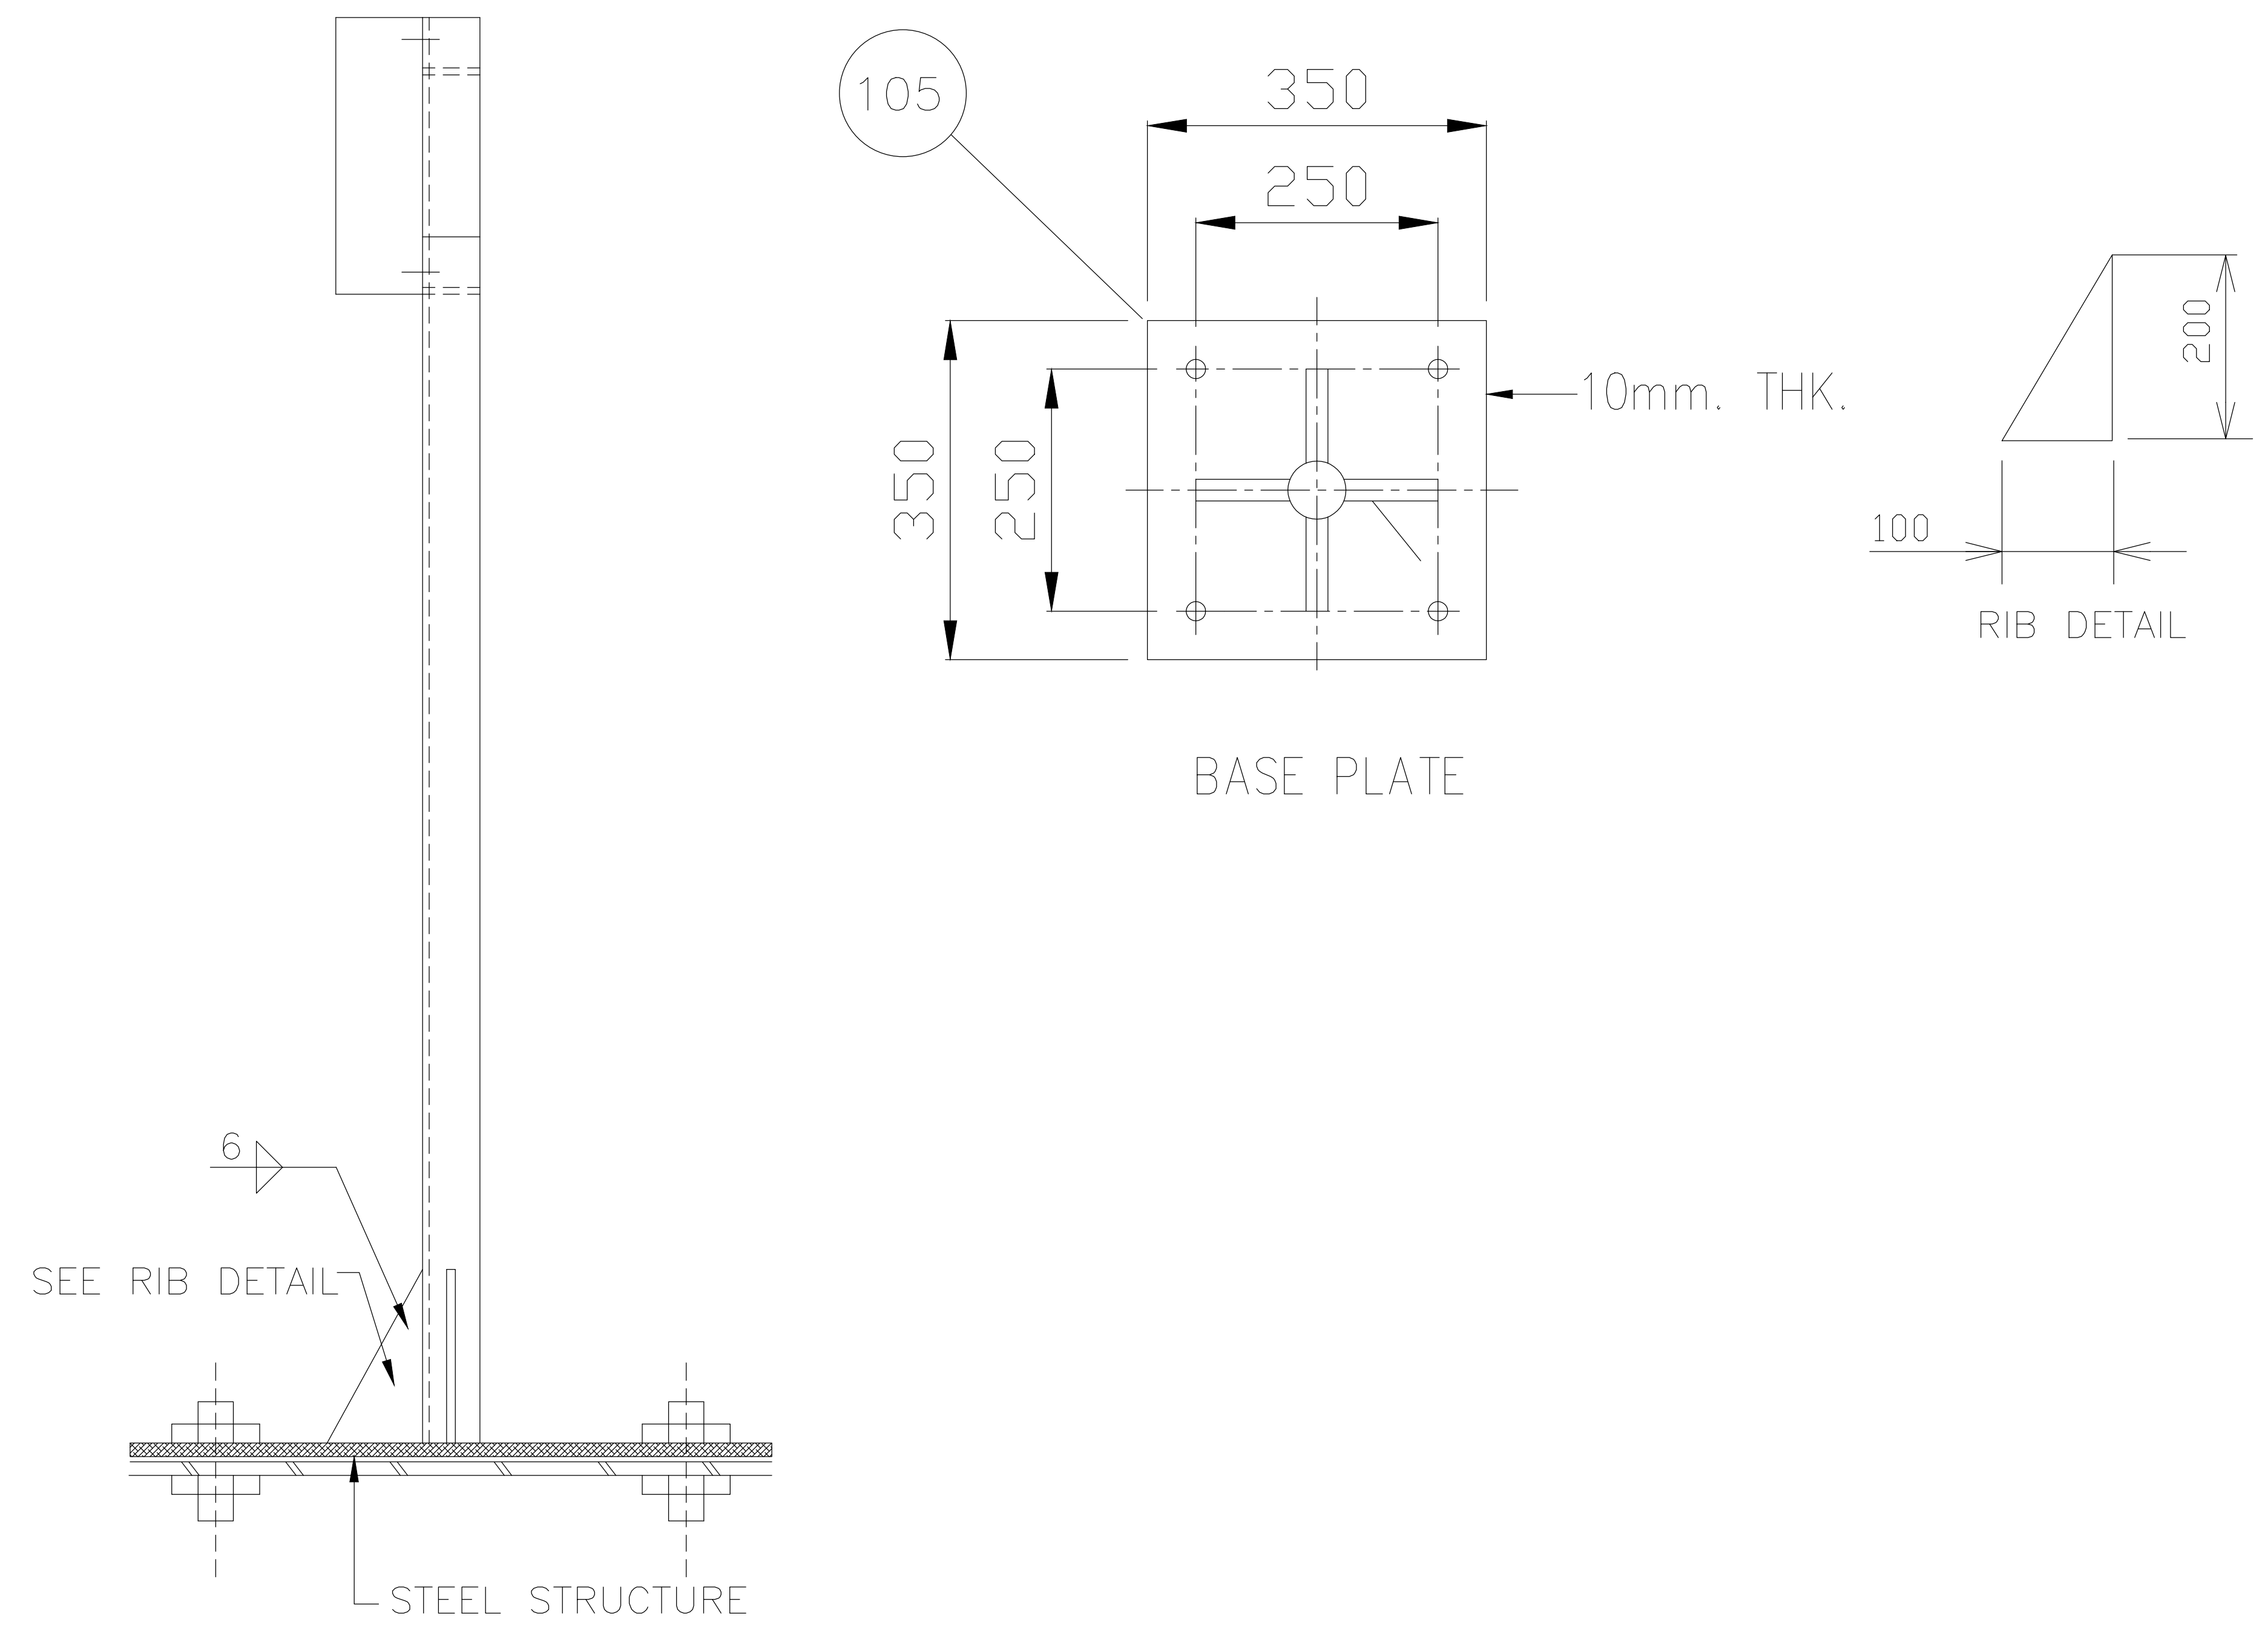

SIDE VIEW


MATERIAL DESCRIPTION

SL.NO.	DESCRIPTION	SIZE	MATL	QTY.	TOTAL QTY.	UNIT WT.	TOTAL WT.
112	1.5M LG MS CHANNEL	100mm x 50mm x 6mm THK	M.S.	2	74	13.8 Kg	510.6 Kg
105	BASE PLATE	350mm x 350mm x 10mm THK	M.S.	2	74	0.49 Kg	18.13 Kg
115	1100mm LG ANGLE IRON	50mm x 50mm x 6mm THK	M.S.	2	74	4.95 Kg	183.15 Kg
107	RIB PLATE	75mm x 200mm x 6mm THK	M.S.	6	222	0.7065 Kg	26.14 Kg
114	EARTH BOSS c/w EARTH STUD & ACCESSORIES	M10	S.S	2	74	—	—
111	BOLT, NUTS, WASHERS & SPRING WASHERS	M16x110 LONG	S.S	4	32	—	—

HOLE SIZE 'A' - 8 NOS. 14mm DIA. FOR MOUNTING OF INSTRUMENT STAND.
8 NOS M10 BOLT C/W NUTS AND WASHERS.


HOLE SIZE 'B' - 8 NOS. 8mm DIA. FOR MOUNTING JUNCTION BOX.
8 NOS. M6 BOLT C/W NUTS AND WASHERS.

[illegible]

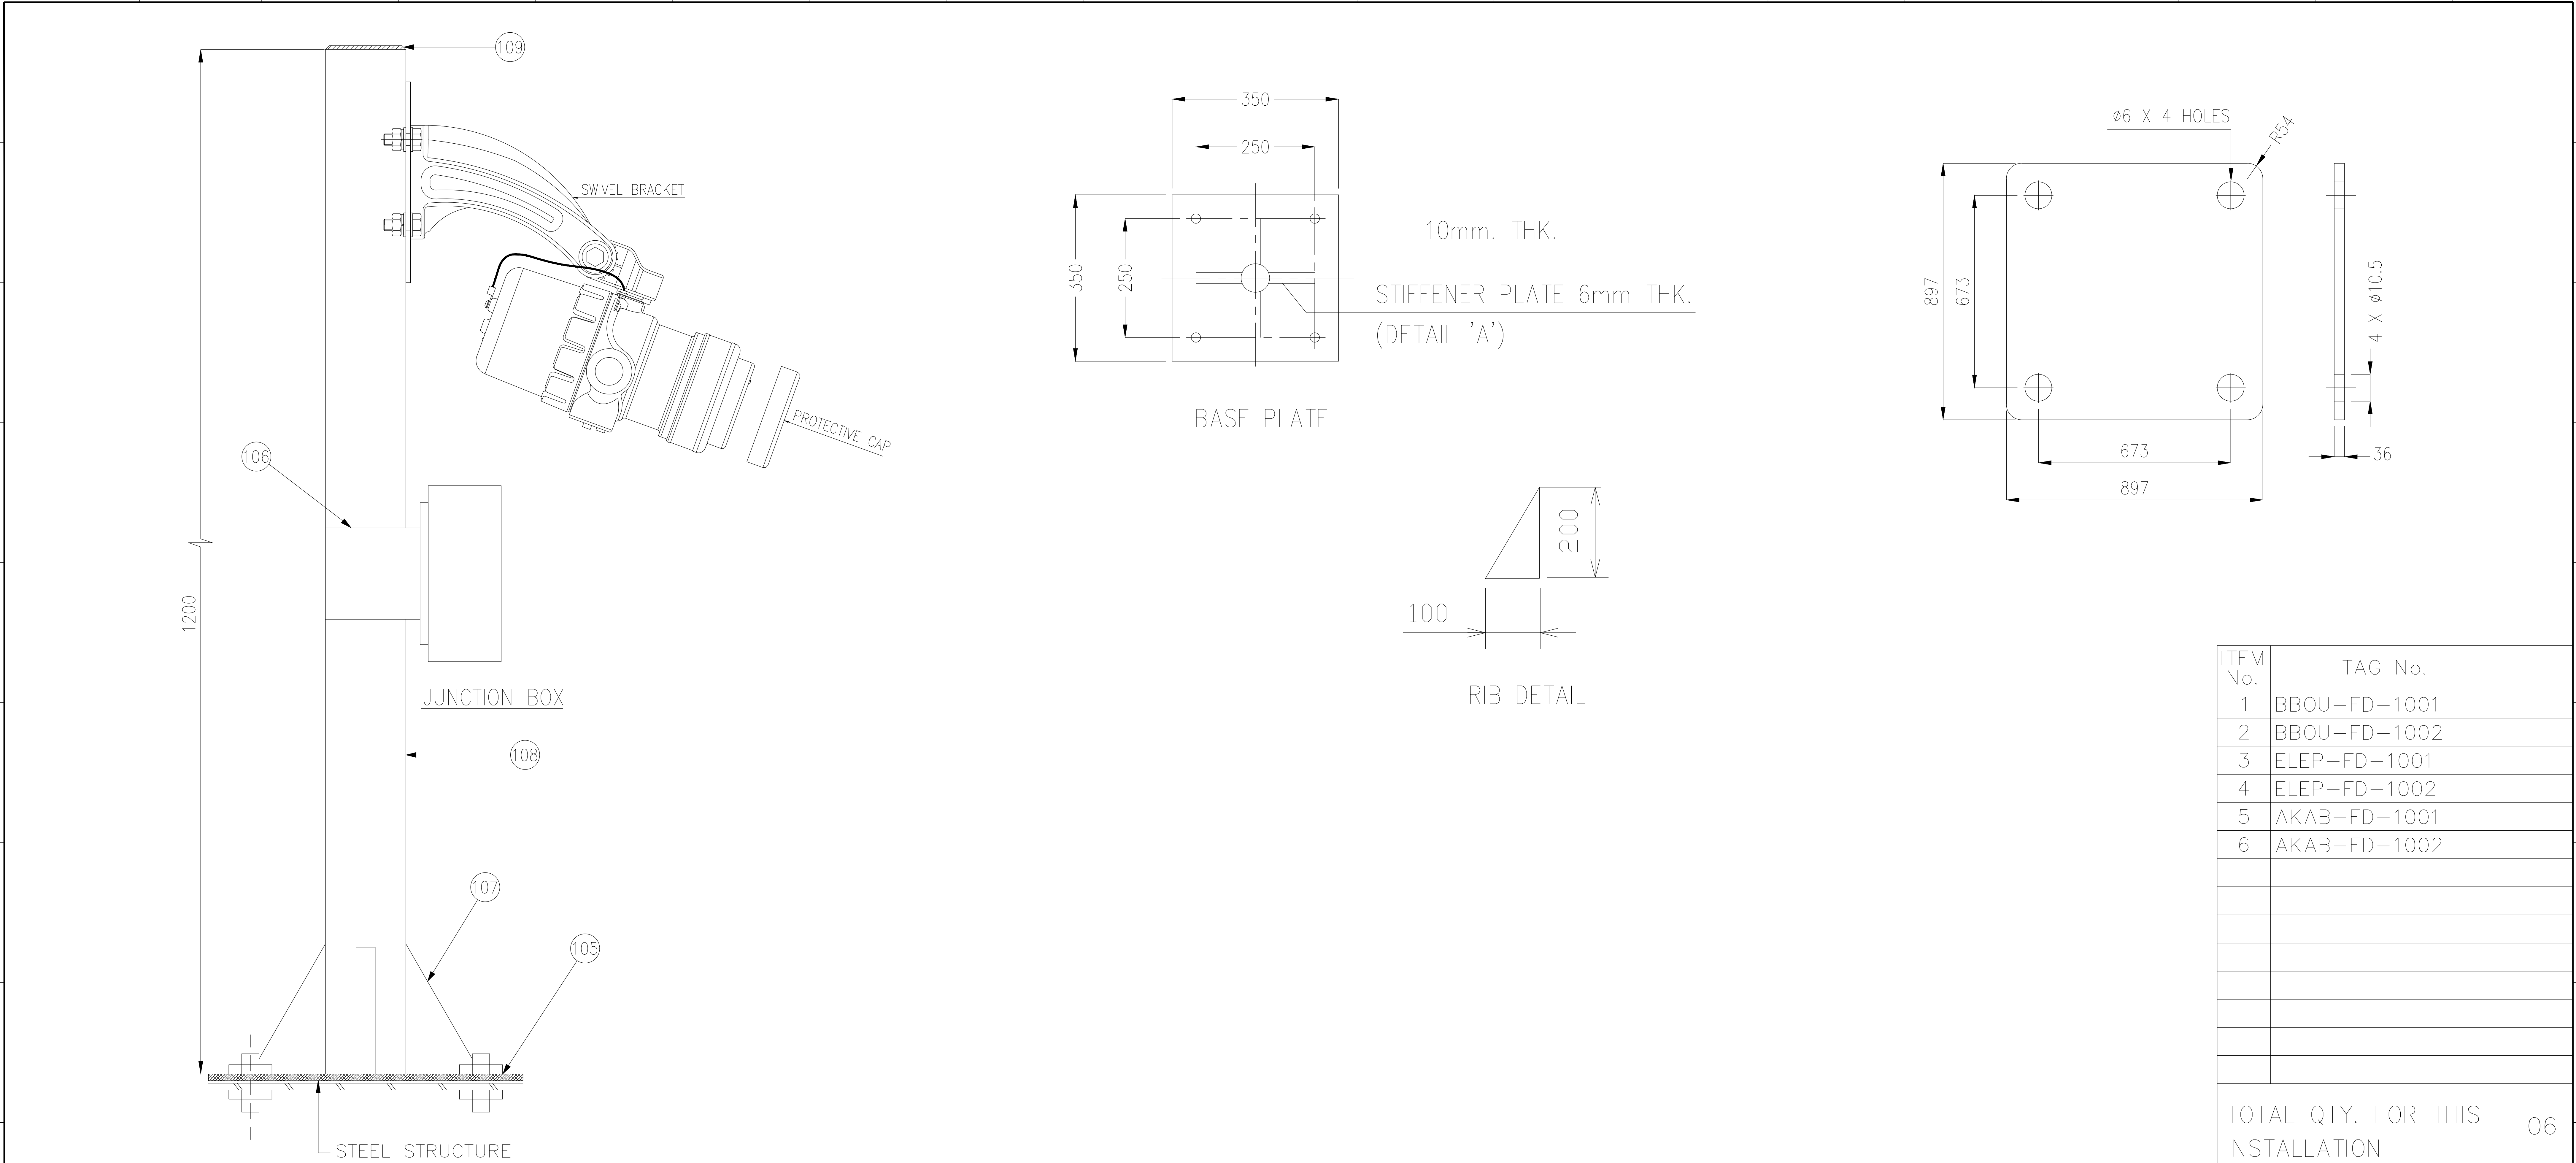



1. SPECTRON WILL SUPPLY MATERIAL AS INDICATED ABOVE ALONG WITH THE BRACKETS.

REFERENCE DRAWINGS		DRAWING No.	NOTES:							CONTRACTOR					BRASS FERTILIZER & PETROCHEMICAL COMPANY LIMITED			
										epicATLANTIC					brass fertilizer GAS PROCESSING AND METHANOL COMPLEX PROJECT FEED FOR GAS GATHERING PIPELINES SHELL			
										ENDORSEMENT					MULTI SPECTRUM FLAME DETECTOR			
										RELEASED FOR	DESIGN ENGR.	BFPC TECH REP	SPDC TECH REP	DATE				
															DRAWN: KIRAN P. DATE: 26-07-2022 SHEET: 10 of 16			
															CHECKED: PRINCE O. DRAWING No. EA-BFPC-L-GPMC-GGPL-FEED-ICS-DWG-039 REV.			
															ENDORSED: KINGSLEY. A. PROJECT No. --			
															APP'D DATE: -- PROJECT No.			
															A01			

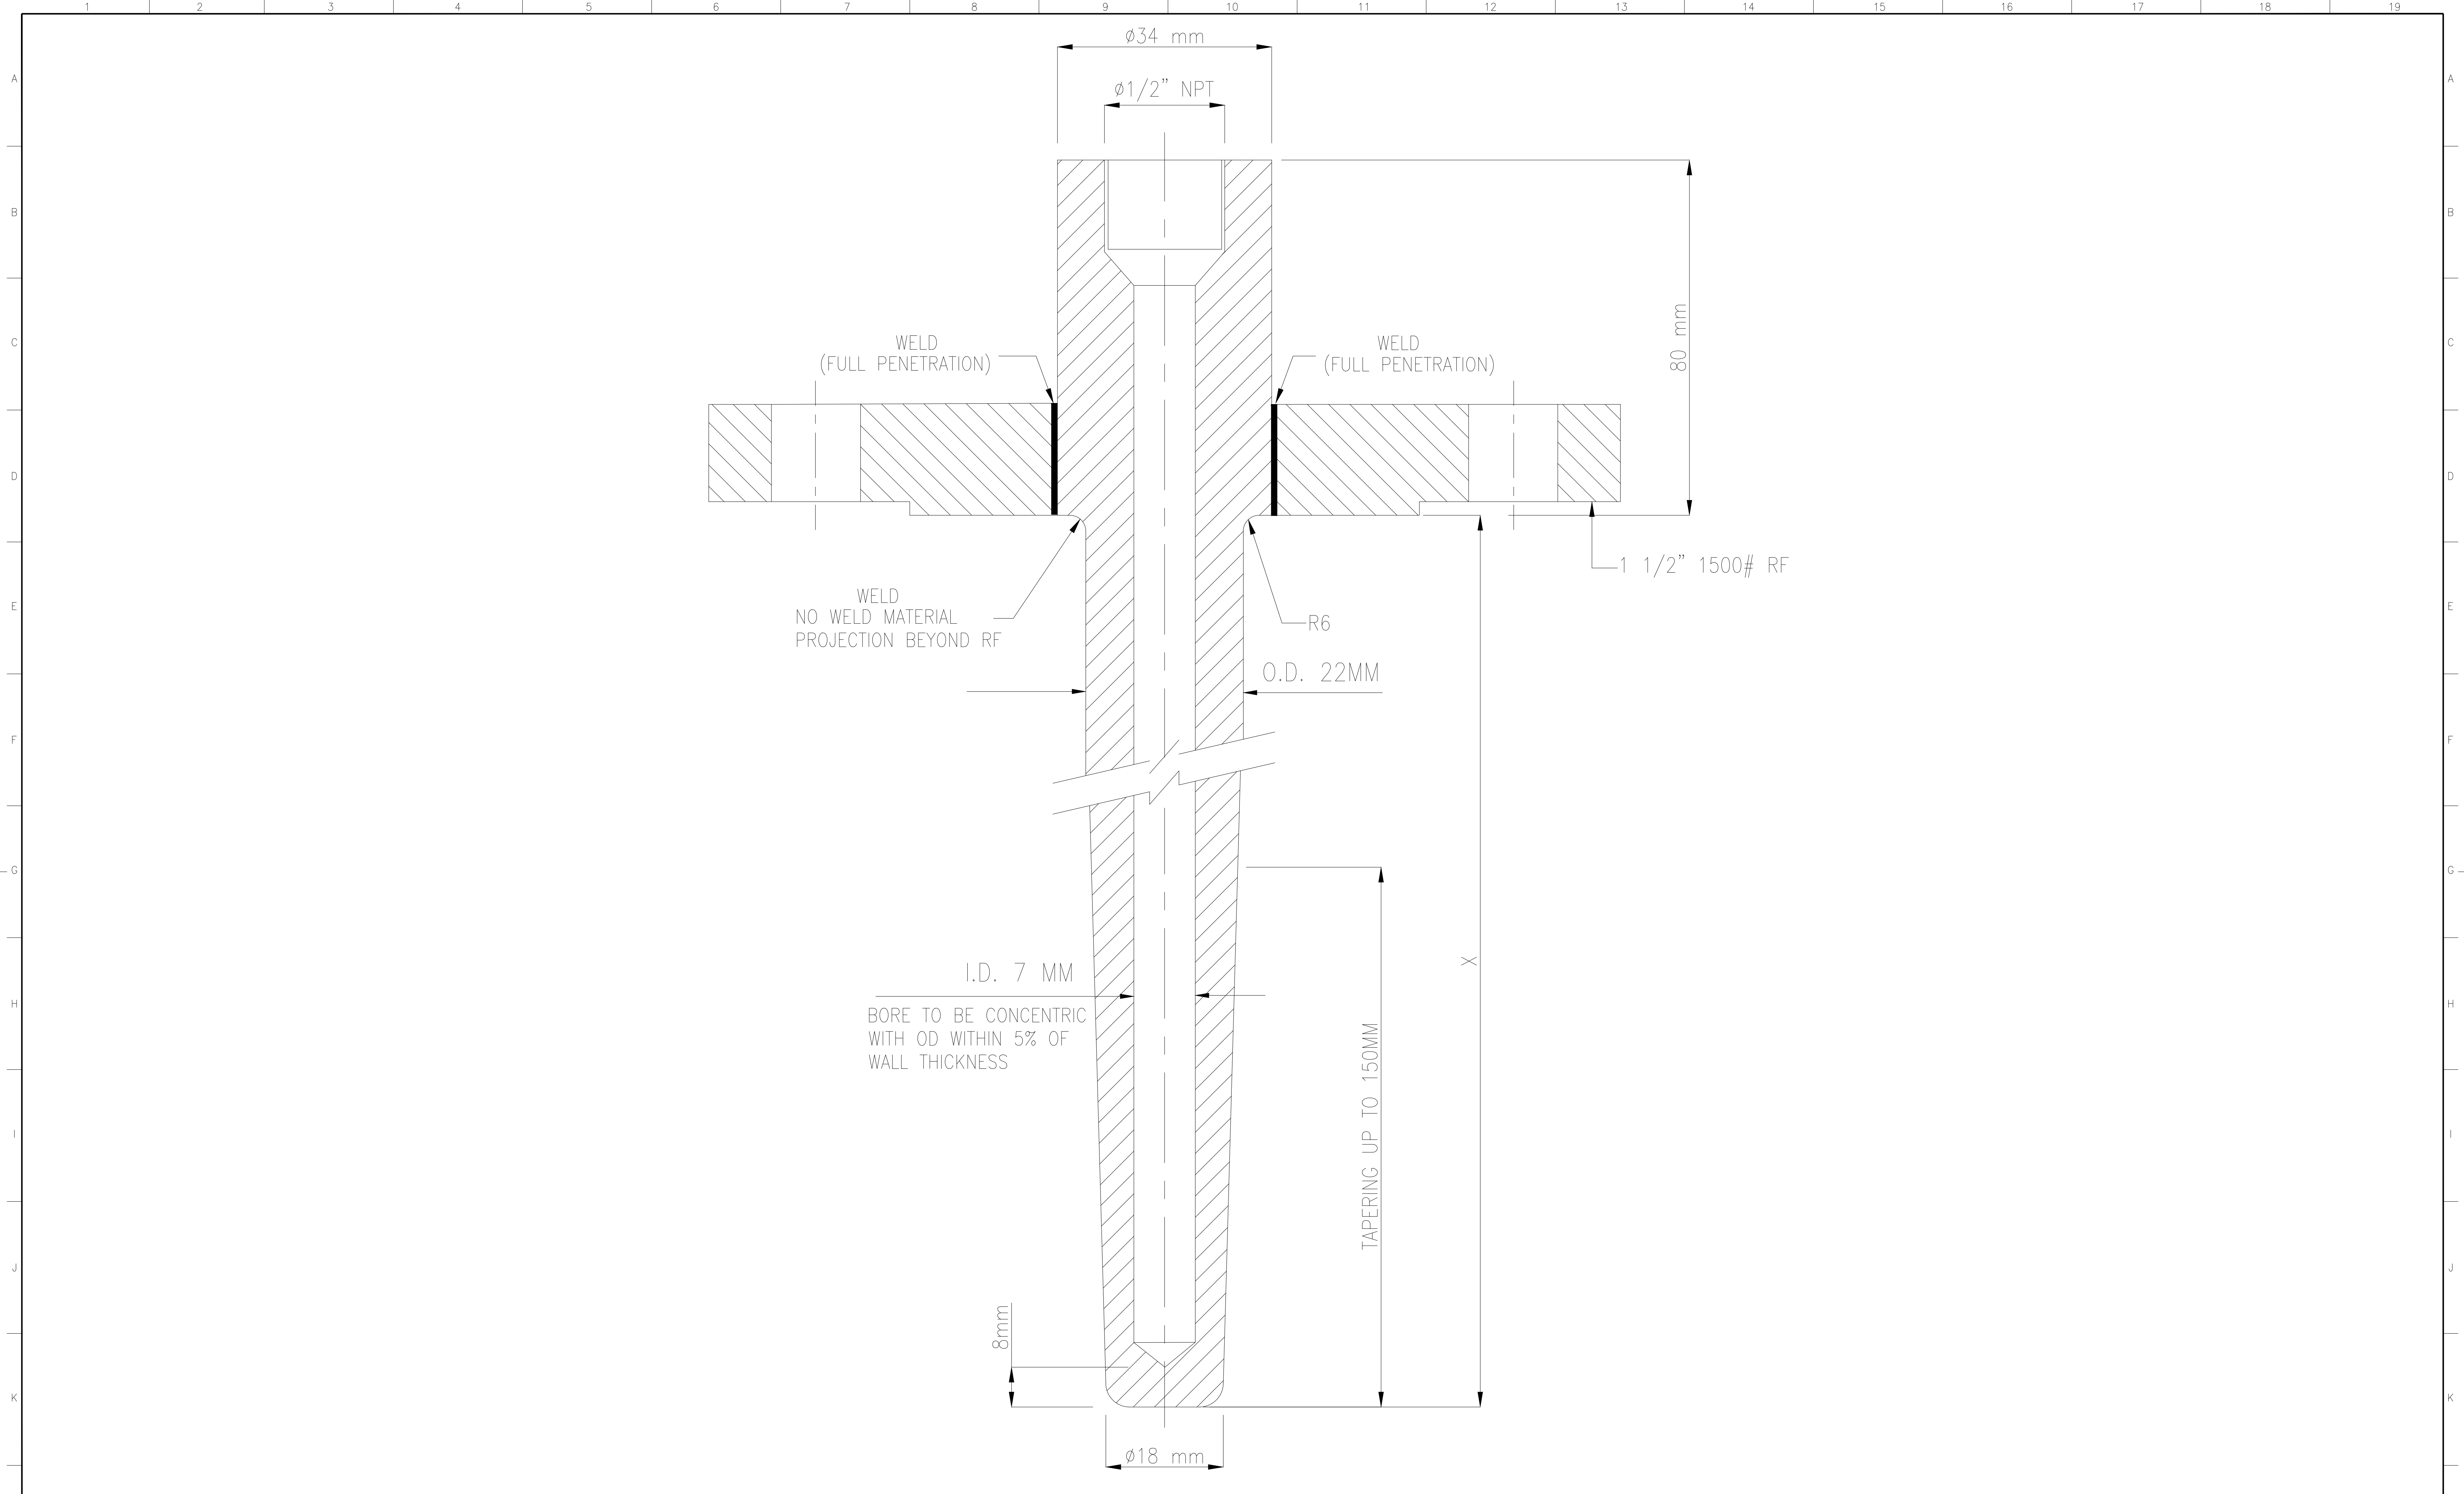

REFERENCE DRAWINGS		DRAWING No.	NOTES:							CONTRACTOR					BRASS FERTILIZER & PETROCHEMICAL COMPANY LIMITED			
										epicATLANTIC					brassfertilizer GAS PROCESSING AND METHANOL COMPLEX PROJECT FEED FOR GAS GATHERING PIPELINES Shell			
										ENDORSEMENT					THERMOWELL			
										RELEASED FOR	DESIGN ENGR.	BFPC TECH. REP	SPDC TECH. REP	DATE				
															DRAWN: KIRAN P.	DATE: 26-07-2022	SHEET: 11 of 16	
															CHECKED: PRINCE O.	DRAWING No. EA-BFPCL-GPMC-GGPL-FEED-ICS-DWG-039	REV.	
															ENDORSED: KINGSLEY. A.	PROJECT No. --	A01	
															APP'D DATE: --	PROJECT No.		
										COPY RIGHT RESERVED								




INFRARED HYDROCARBON GAS DETECTOR
OPEN PATH ECLIPSE,OPECL
TRANSMITTER WITH PAN TILT PN: 007914-001
RECEIVER WITH PAN TILT PN: 007915-001
MATERIAL: STAINLESS STEEL
APPROVALS: CSA, ATEX

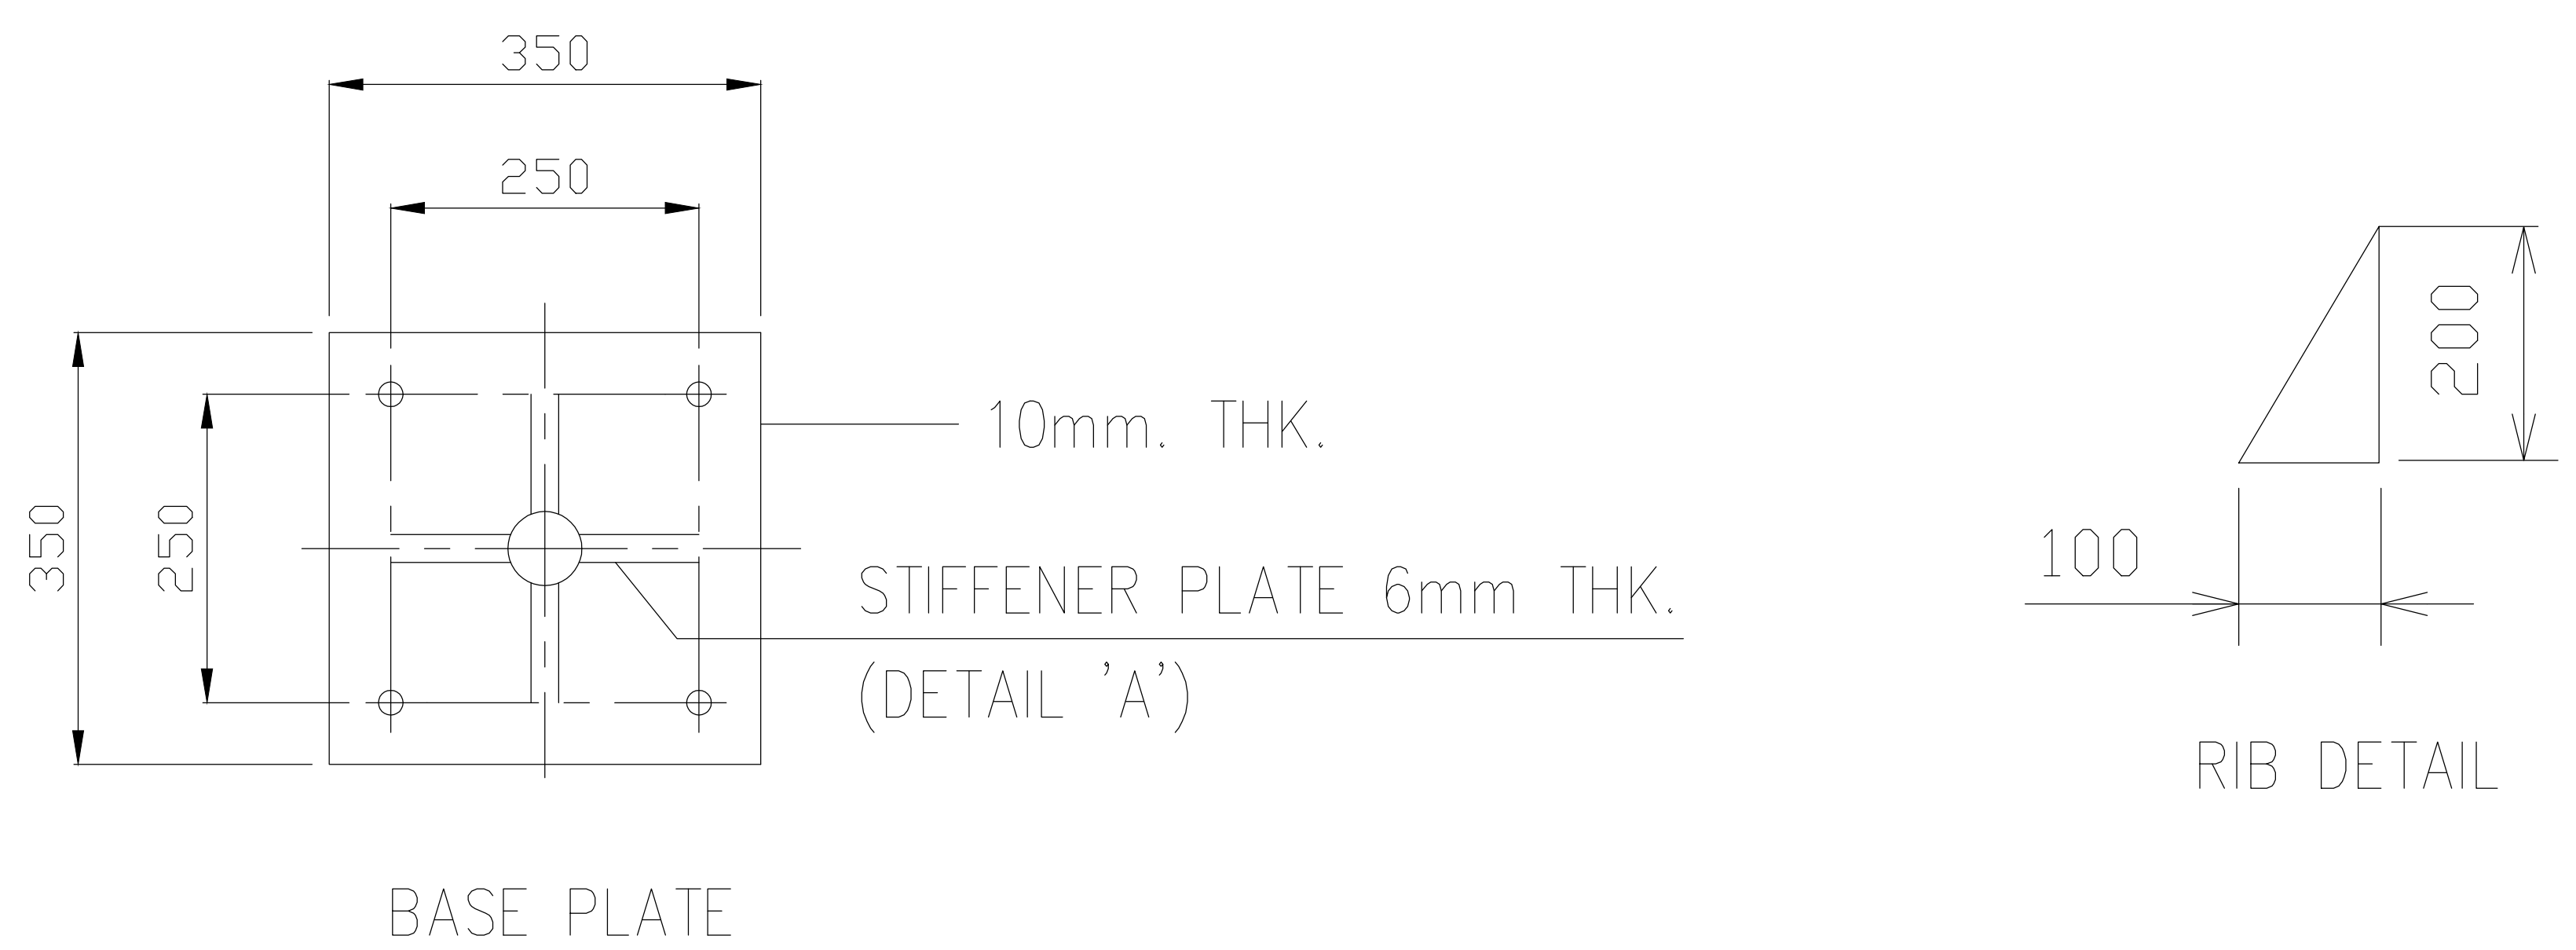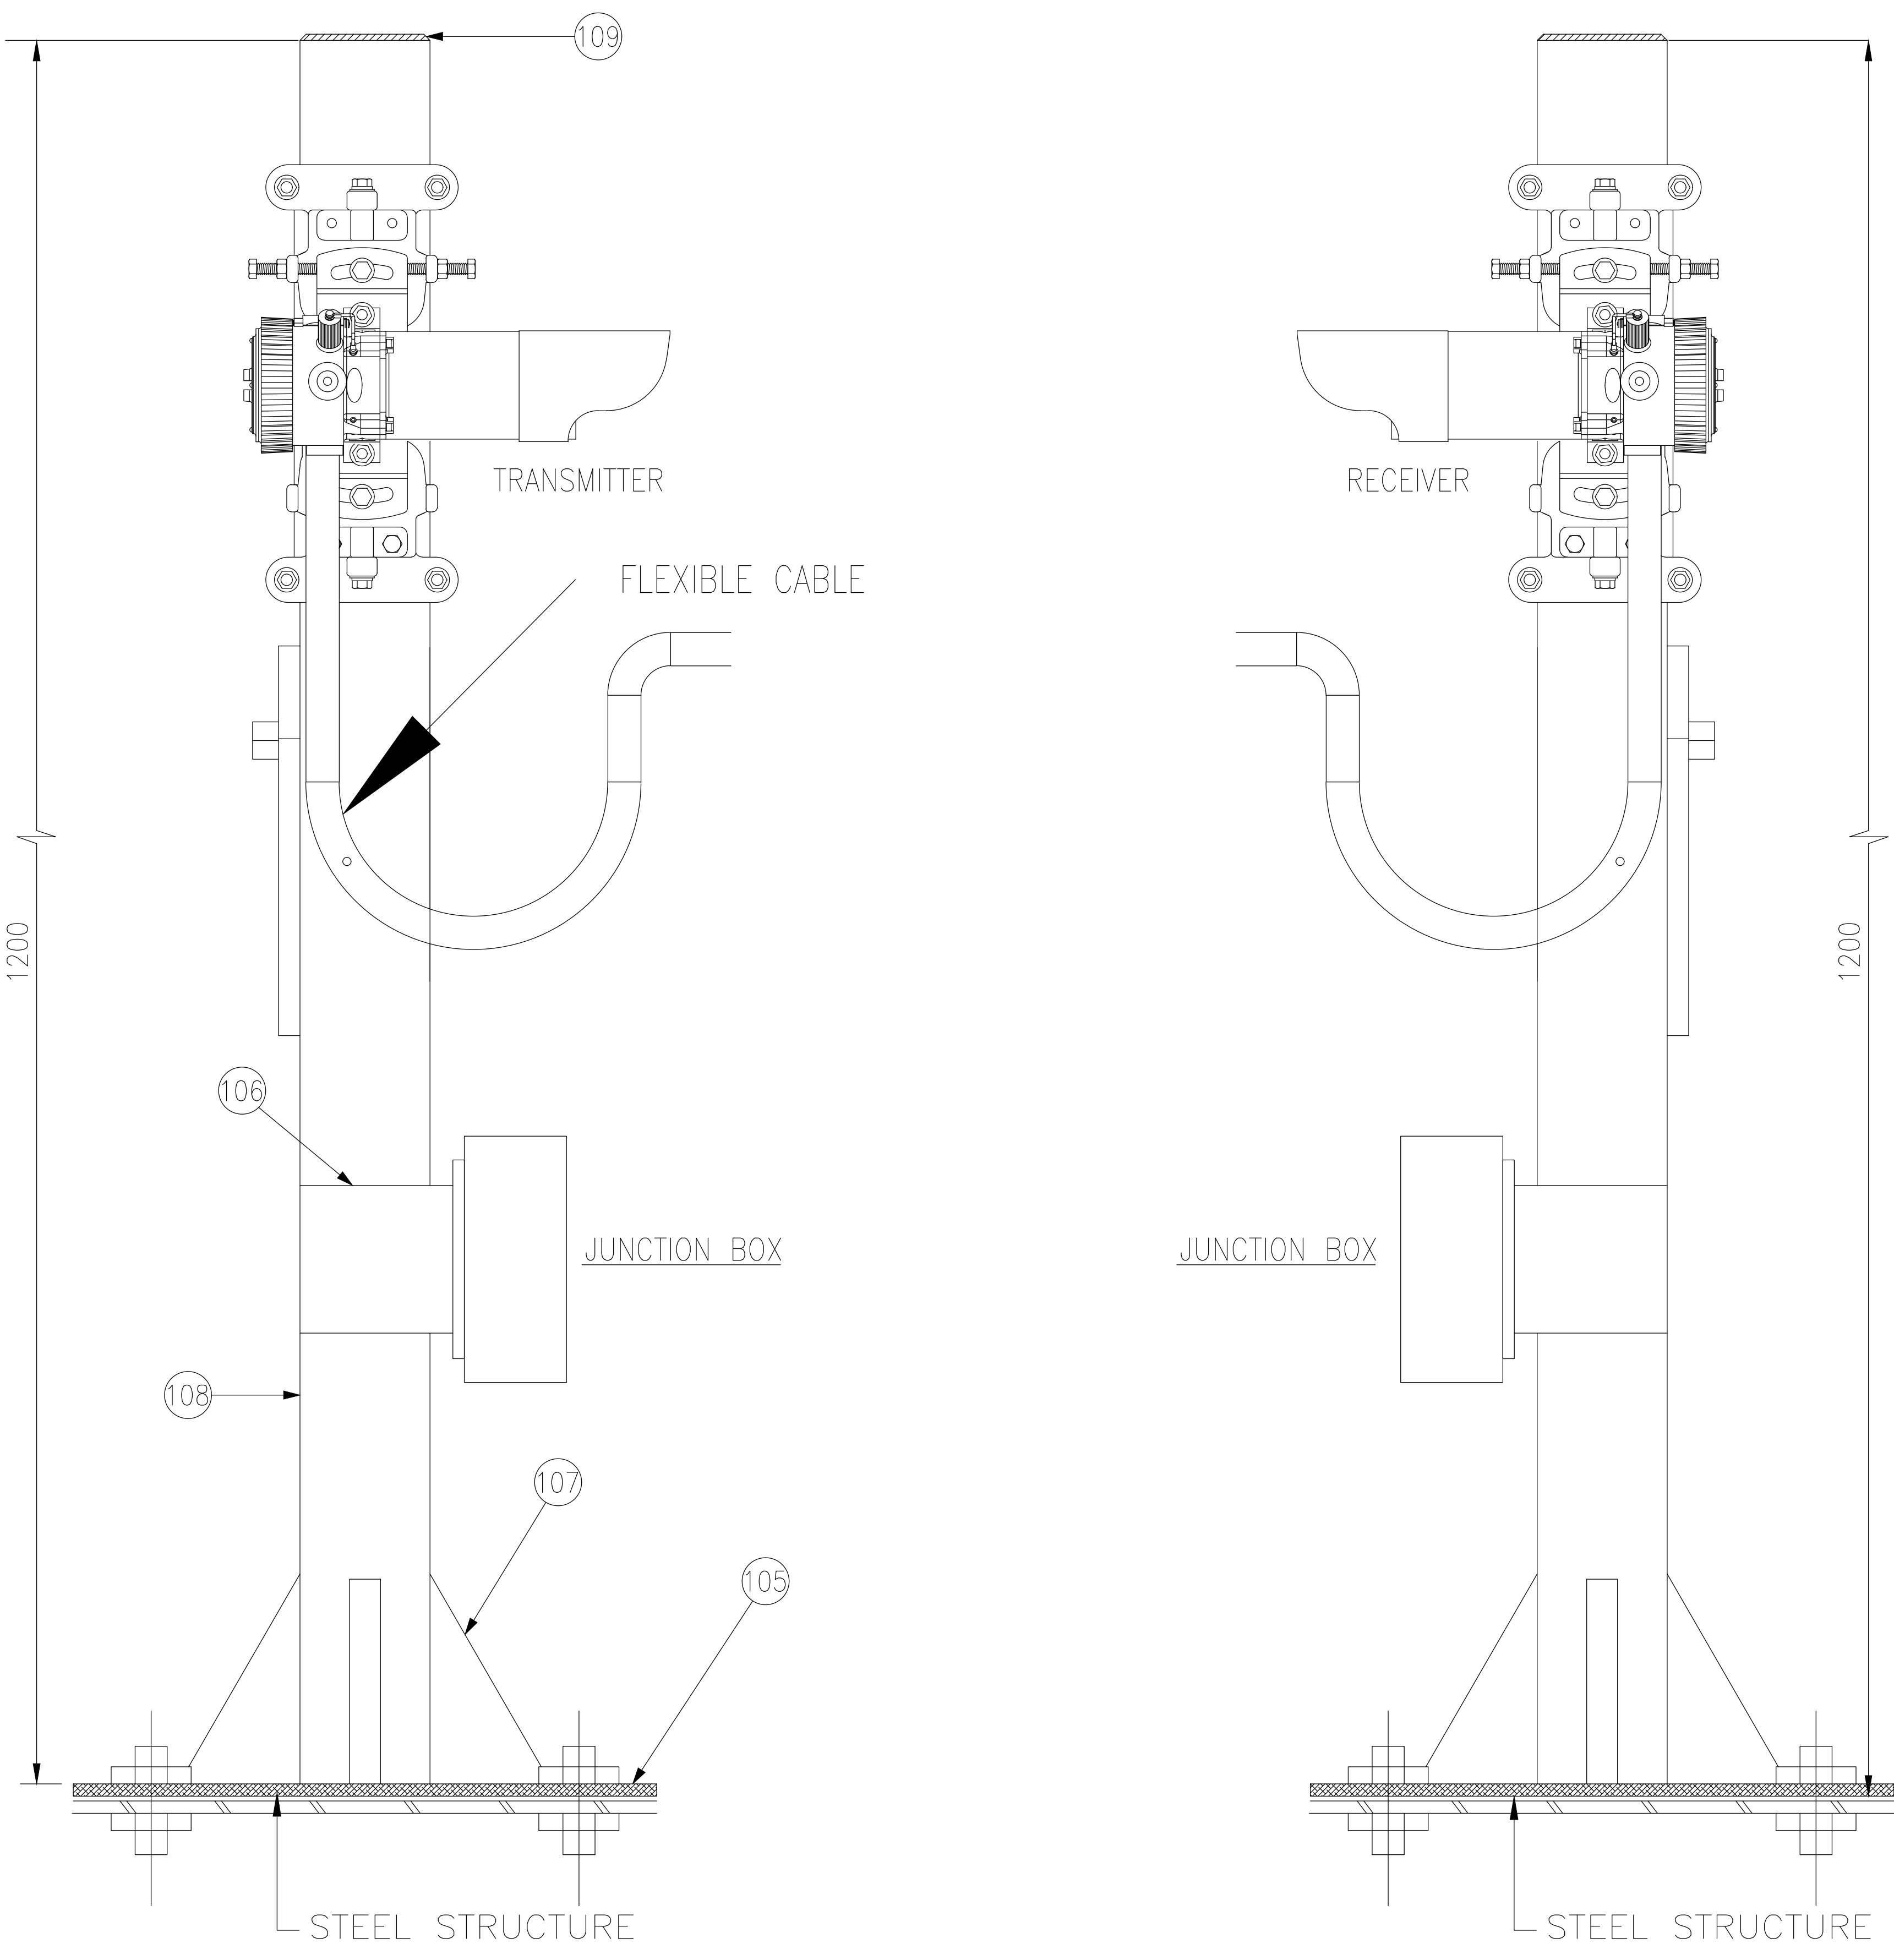

TAG NO.
BBOU-AE/AT-1003T
BBOU-AE/AT-1003R
BBOU-AE/AT-1004T
BBOU-AE/AT-1004R
ELEP-AE/AT-1003T
ELEP-AE/AT-1003R
ELEP-AE/AT-1004T
ELEP-AE/AT-1004R
ELEP-AE/AT-1006T
ELEP-AE/AT-1006R
AKAB-AE/AT-1002T
AKAB-AE/AT-1002R

SL.NO.	DESCRIPTION	SIZE	MATL.	QTY.	TOTAL
105	BASE PLATE	350 MM X 350 MM X 10 MM	M.S.	2 NOS.	12 NOS.
106	MOUNTING PLATE	200 MM X 125 MM X 3 MM	M.S.	2 NOS.	12 NOS.
107	RIB PLATE	140 MM X 70 MM X 6 MM	M.S.	6 NOS.	36 NOS.
108	PIPE	2" NB	M.S.	2.4M	14.4M
109	TOP PLATE	ø63 X 3MM	M.S.	2 NO.	12 NOS.
110	U-BOLT,NUTS & WASHERS	M8	SS 304	4 SETS	4 SETS
111	BOLT, NUTS, WASHERS & SPRING WASHERS	M16x110 LONG	SS 304	4 SETS	24 SETS
116	BOLT, NUTS, WASHERS & SPRING WASHERS	M6	SS 304	4 SETS	24 SETS


REFERENCE DRAWINGS	DRAWING No.	NOTES:				CONTRACTOR					BRASS FERTILIZER & PETROCHEMICAL COMPANY LIMITED						
											GAS PROCESSING AND METHANOL COMPLEX PROJECT						
						ENDORSEMENT					INSTALLATION DIAGRAM						
						RELEASED FOR	DESIGN ENGR.	BFPC TECH REP	SPDC TECH REP	DATE	DRAWN: KIRAN P. DATE: 26-07-2022 SHEET: 12 of 16						
											CHECKED: PRINCE O. DRAWING No. EA-BFPC-L-GPMC-GGPL-FEED-ICS-DWG-039 REV.						
											ENDORSED: KINGSLEY. A. PROJECT No. --						
											APP'D DATE: -- PROJECT No. A01						
COPY RIGHT RESERVED																	

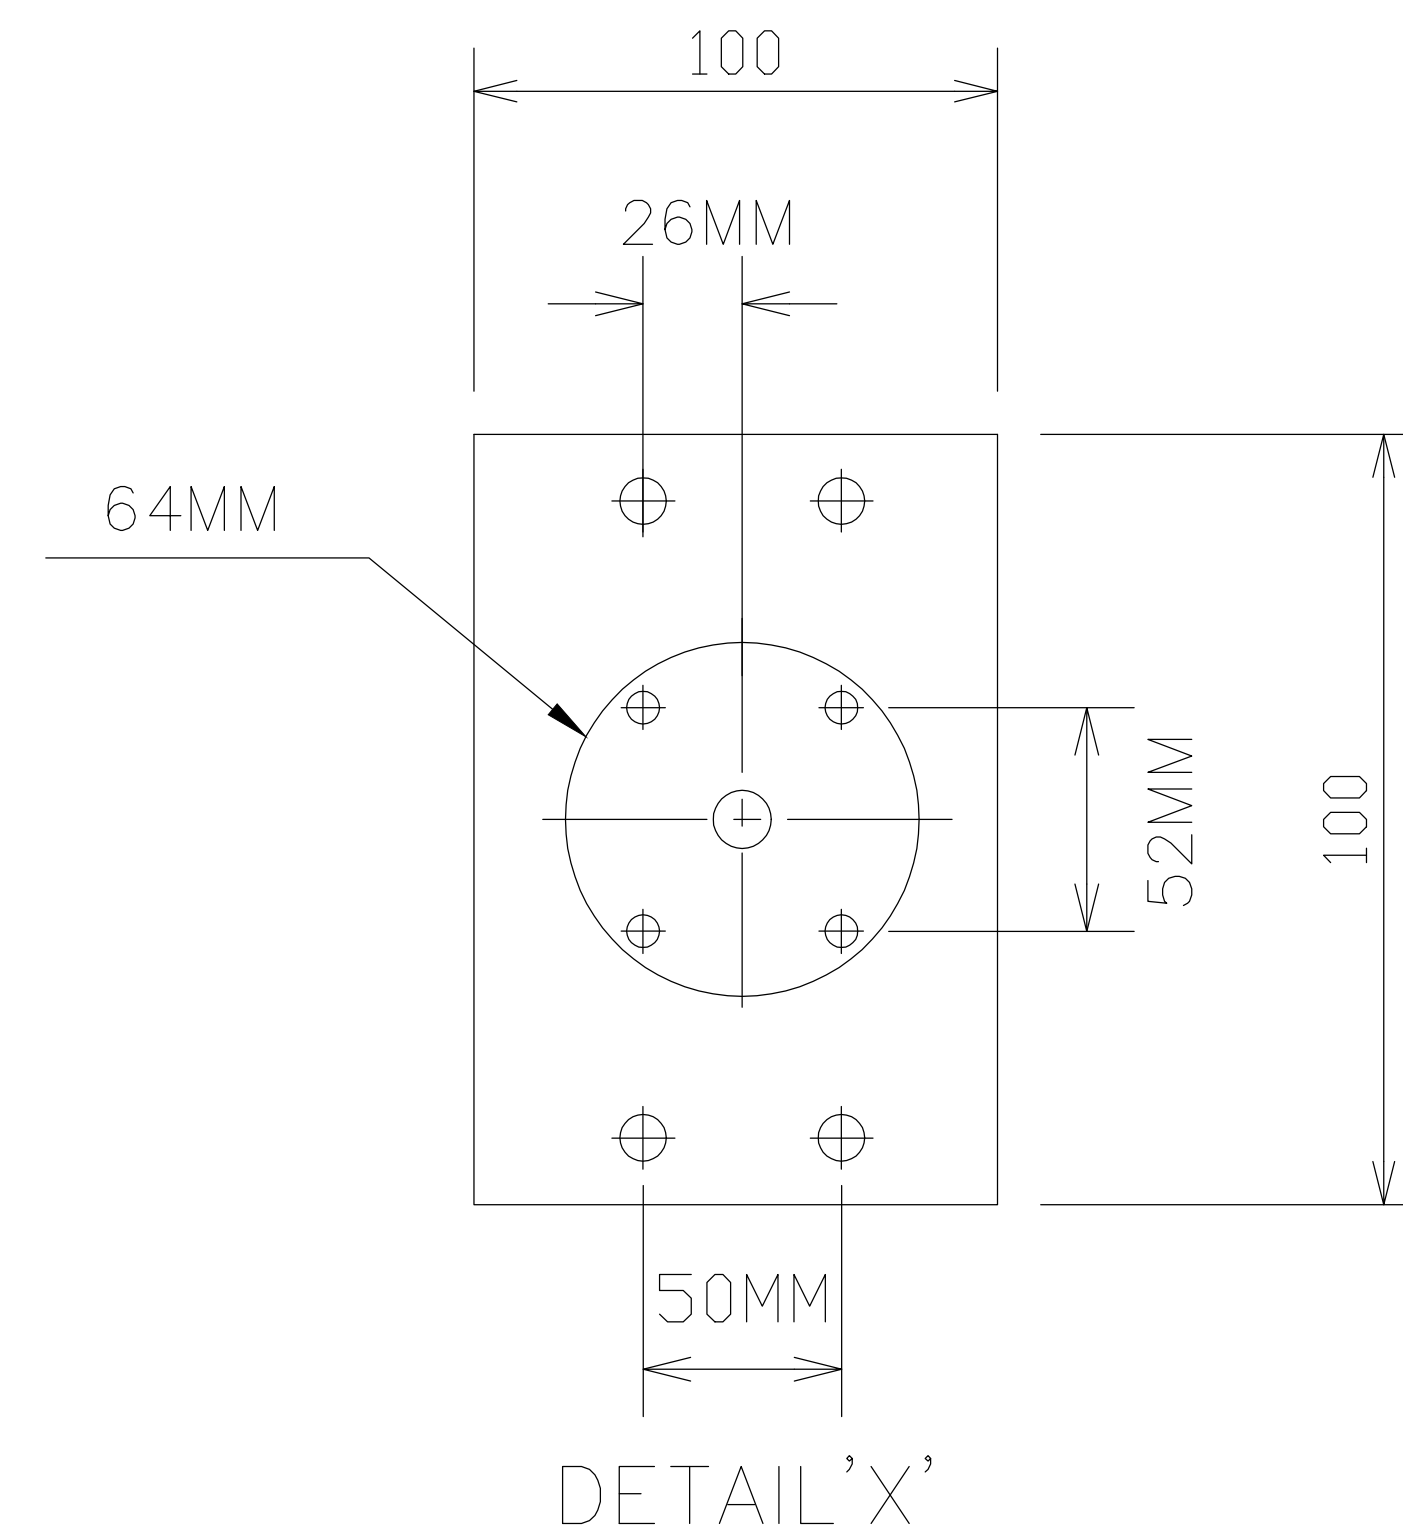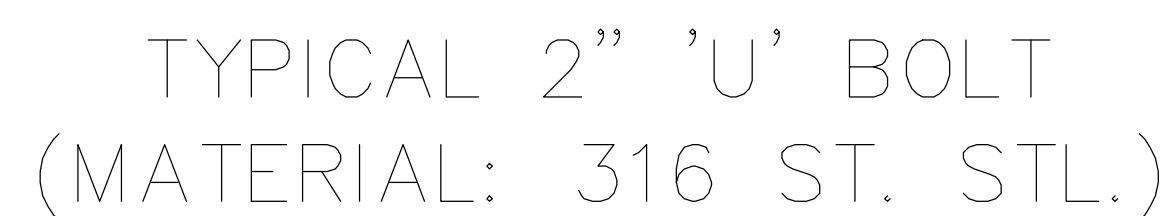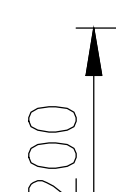


4 SETS	24 SETS
0.86	0.97
0.87	0.98
0.88	0.99
0.89	1.00
0.90	1.00
0.91	1.00
0.92	1.00
0.93	1.00
0.94	1.00
0.95	1.00
0.96	1.00
0.97	1.00
0.98	1.00
0.99	1.00
1.00	1.00

3) NAME PLATE SHALL BE BOLTED AT GAS DETECTOR MOUNTING PLATE.

19

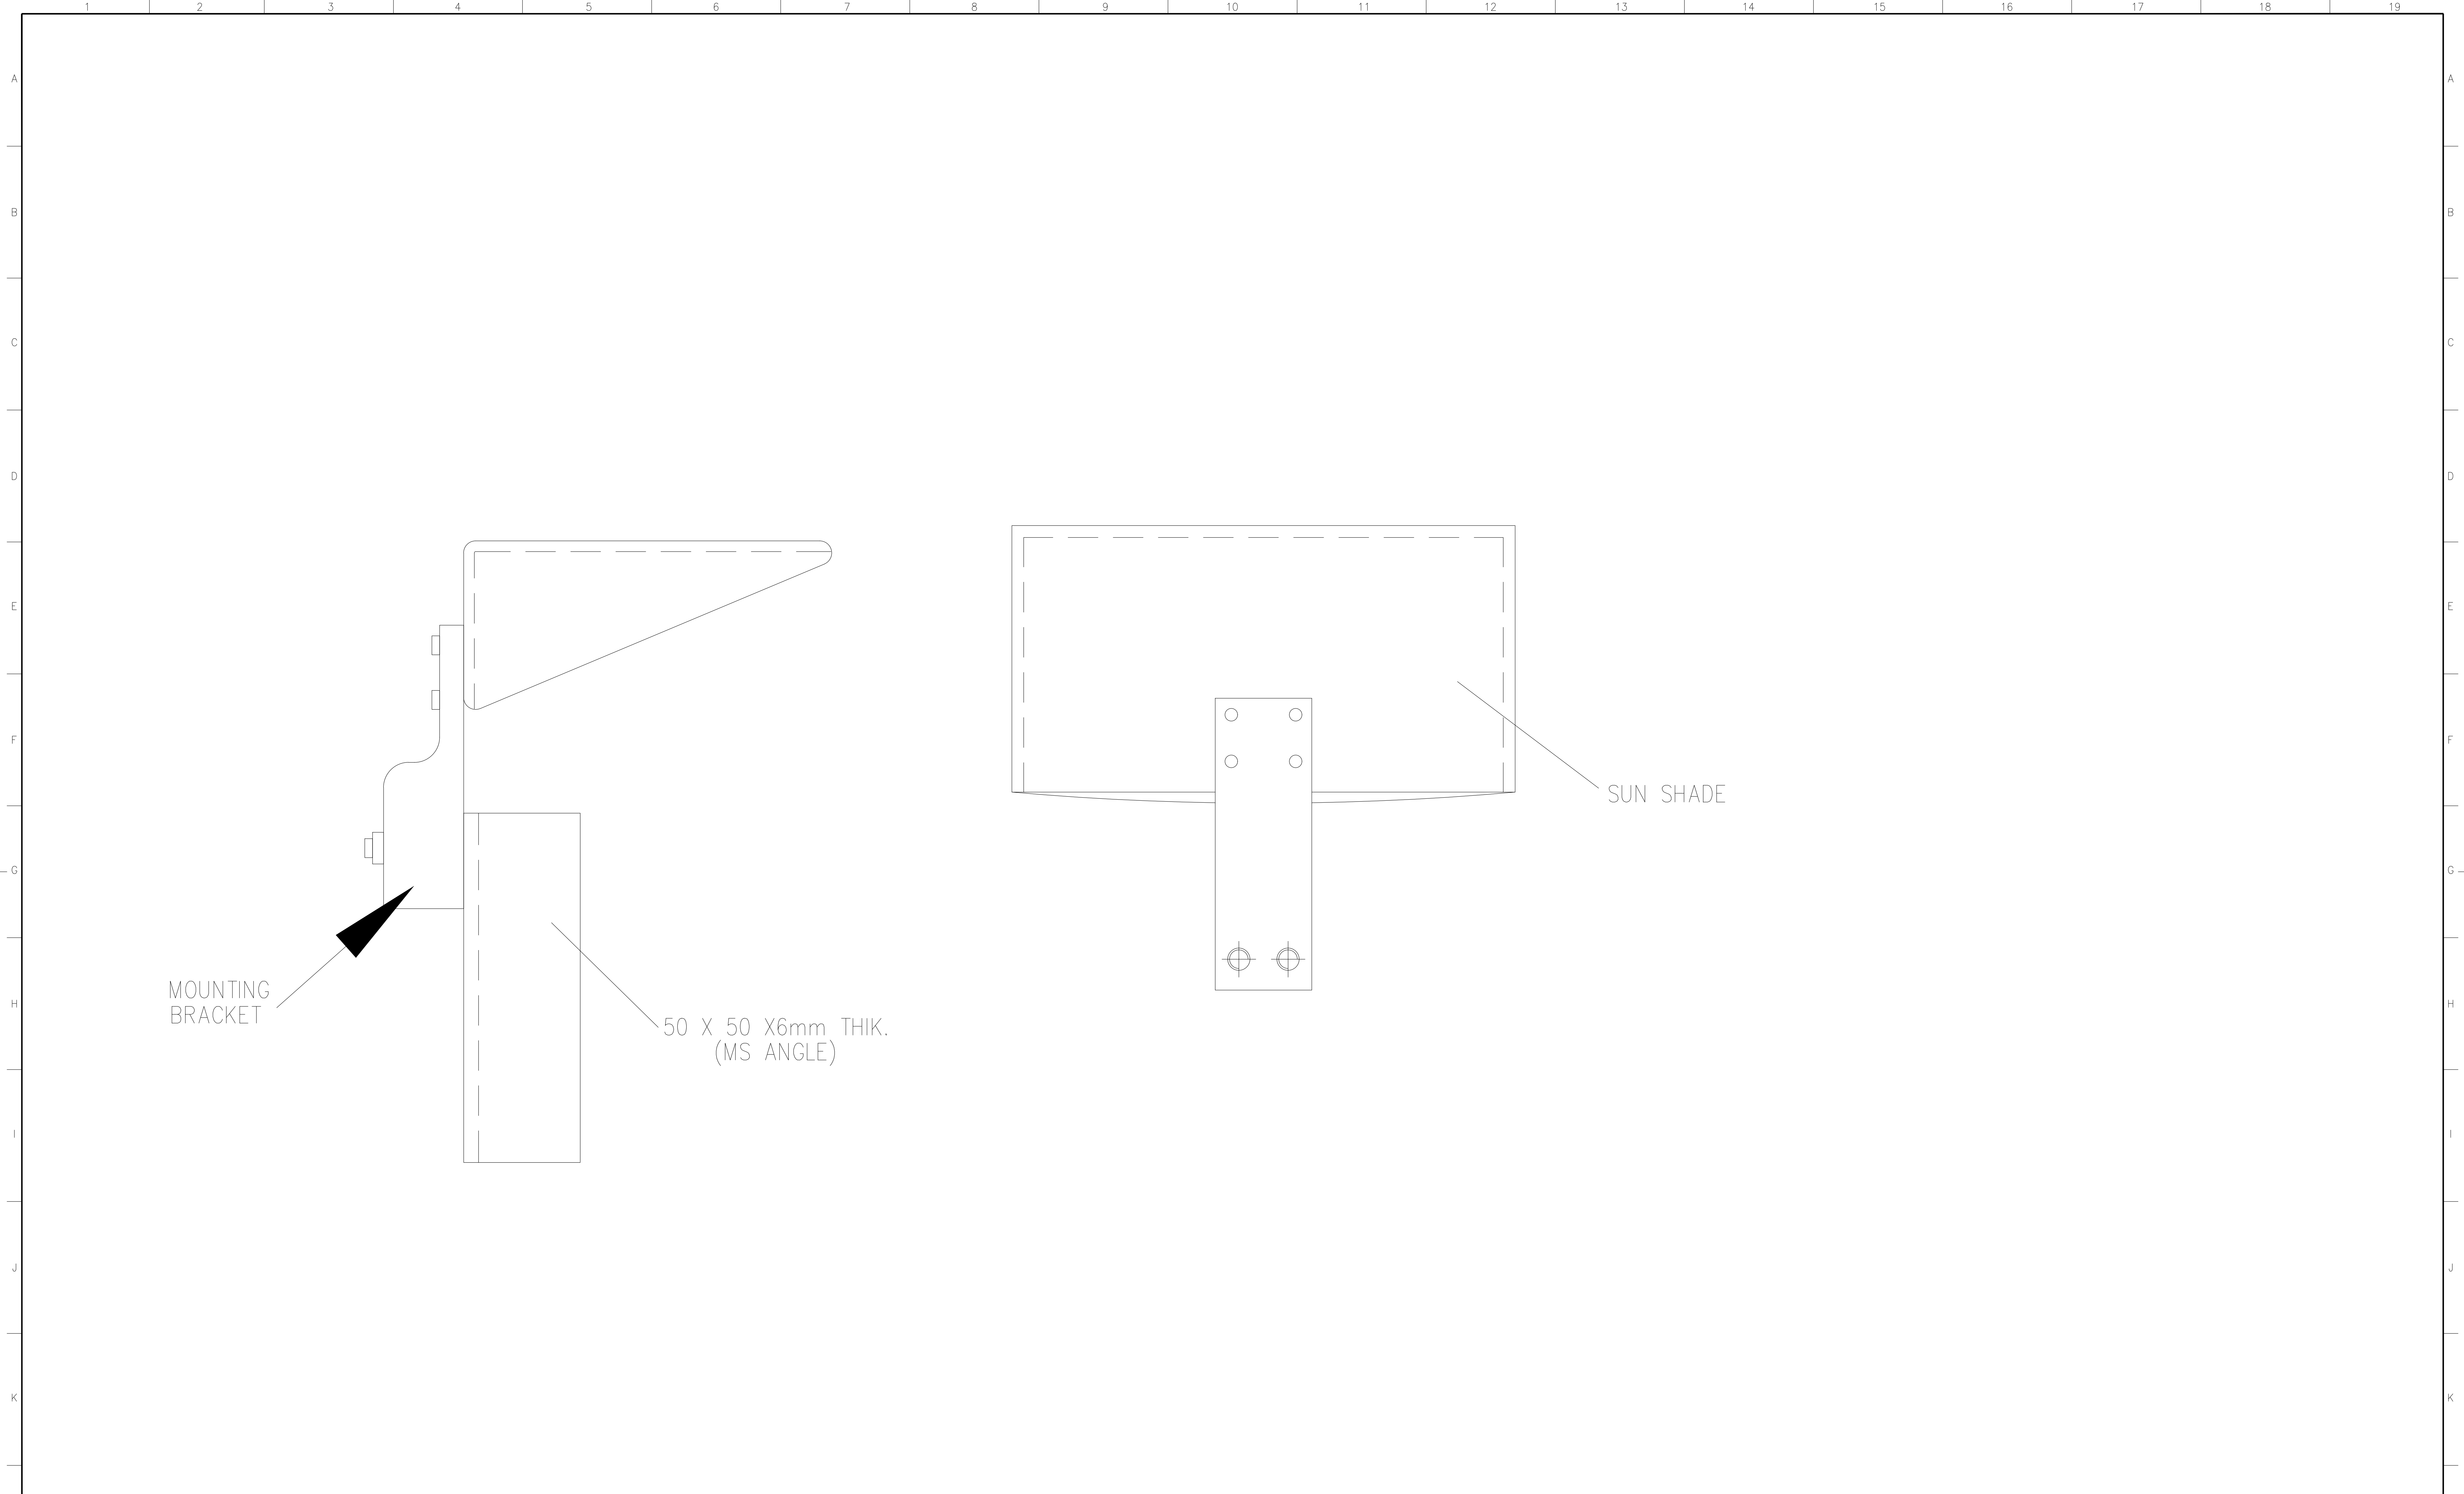

L	REFERENCE DRAWINGS	DRAWING No.	NOTES:							CONTRACTOR epicATLANTIC	BRASS FERTILIZER & PETROCHEMICAL COMPANY LIMITED						
											brassfertilizer	GAS PROCESSING AND METHANOL COMPLEX PROJECT FEED FOR GAS GATHERING PIPELINES		Shell			
											INSTALLATION DIAGRAM FOR CANOPY						
M											ENDORSEMENT						
	A01	ISSUED FOR APPROVAL		KIRAN P.	PRINCE O.	KINGSLEY A.	26-07-22	—	—	—	—	—	DRAWN: KIRAN P.		DATE: 26-07-2022		SHEET: 15 of 16
	R01	ISSUED FOR REVIEW		KIRAN P.	PRINCE O.	KINGSLEY A.	12-07-22						CHECKED: PRINCE O.		DRAWING No. EA-BFPCL-GPMC-GGPL-FEED-ICS-DWG-039		REV.
	REV			DRAWN	CHK	END	DATE						ENDORSED: KINGSLEY. A.		PROJECT No. —		A01
	COPY RIGHT RESERVED											APP'D DATE: —		PROJECT No.			

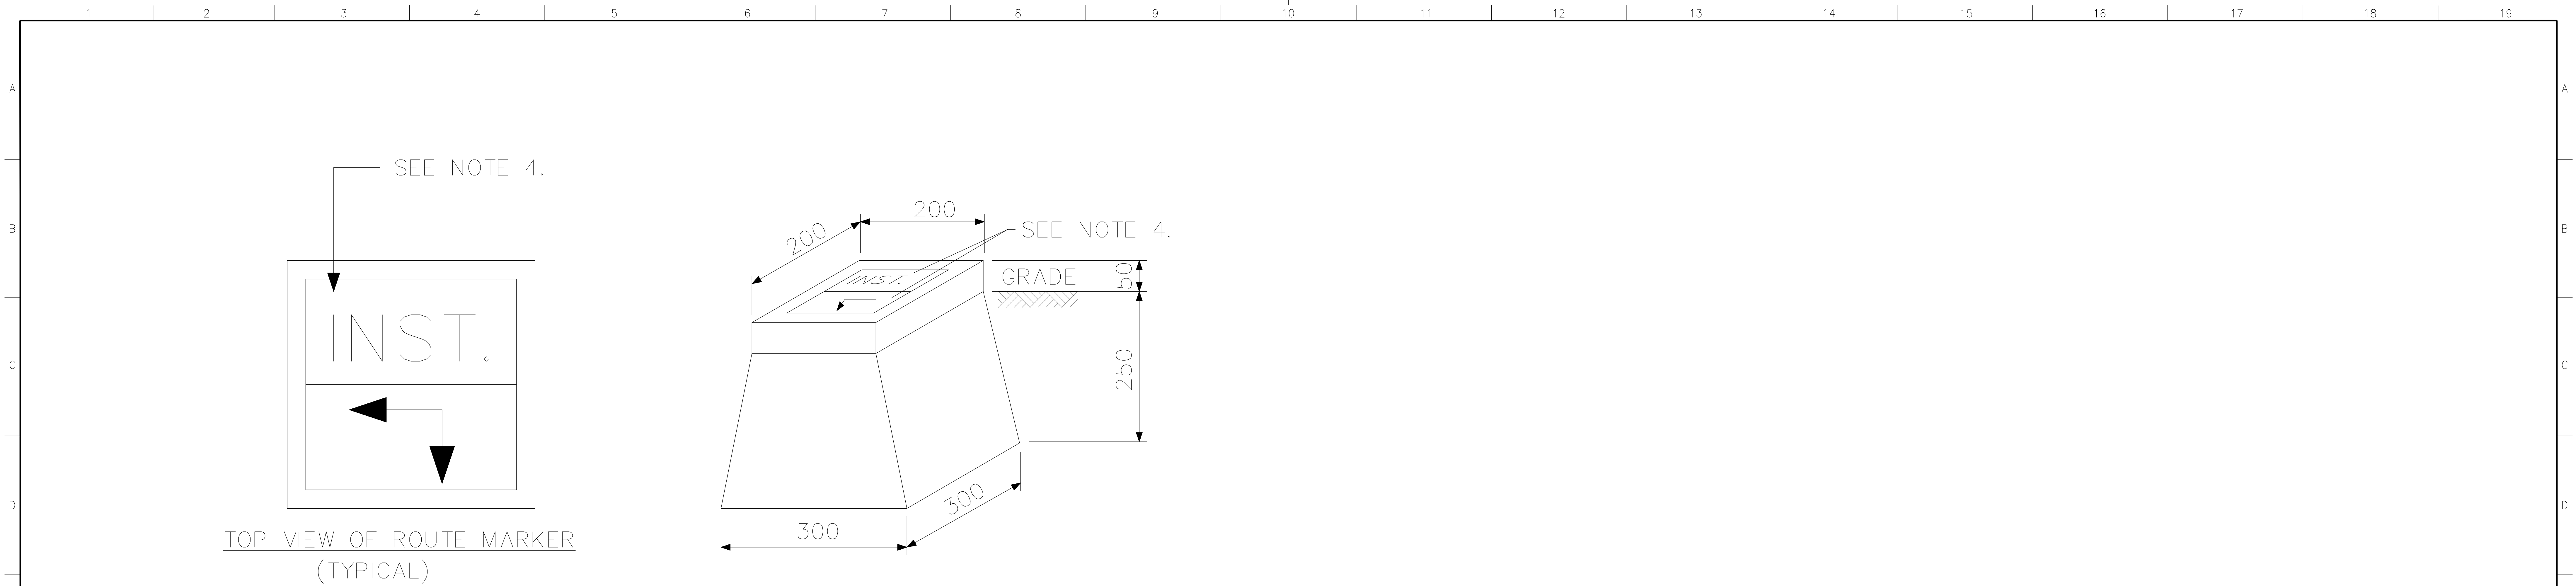

NOTES

1. ALL DIMENSIONS ARE IN mm.
2. CONCRETE USED FOR FABRICATING MARKERS SHALL HAVE CRUSHING STRENGTH OF 20 MPa AT 28 DAYS.
3. CONCRETE CABLE ROUTE MARKERS SHALL BE USED WHEN SPECIFIED FOR TRENCHES CARRYING INSTRUMENT CABLES :

i) ON CONTINUOUS STRAIGHT RUNS AT INTERVALS OF 100m. MARKED

ii) BEFORE & AFTER ROADWAY CROSSINGS.

iii) WHERE TRENCH CHANGES DIRECTION MARKED
4. TOP OF CABLE MARKERS SHALL BE MARKED AS FOLLOWS
UPPER SPACE SHALL INDICATE SERVICE, VOLTAGE ADOPTING FOLLOWING ABBREVIATIONS:
INST. – FOR INSTRUMENT CABLE.
CABLE MARKING ON TOP OF THE CABLE MARKER SHALL BE ENGRAVED (NOT PAINTED) IN THE CONCRETE.
5. ROUTE MARKERS SHALL BE BURIED OVER THE CABLE PROTECTION TILES.

REFERENCE DRAWINGS		DRAWING No.	NOTES:							CONTRACTOR					BRASS FERTILIZER & PETROCHEMICAL COMPANY LIMITED					
																 GAS PROCESSING AND METHANOL COMPLEX PROJECT  FEED FOR GAS GATHERING PIPELINES				
											ENDORSEMENT					INSTALLATION DIAGRAM FOR CABLE ROUTE MARKER				
											RELEASED FOR	DESIGN ENGR.	BFPC TECH. REP	SPDC TECH. REP	DATE	DRAWN: KIRAN P.		DATE: 26-07-2022	SHEET: 16 of 16	
											A01	ISSUED FOR APPROVAL	KIRAN P.	PRINCE O.	KINGSLEY A.	26-07-22	CHECKED: PRINCE O.		DRAWING No. EA-BFPCL-GPMC-GGPL-FEED-ICS-DWG-039	REV.
											R01	ISSUED FOR REVIEW	KIRAN P.	PRINCE O.	KINGSLEY A.	12-07-22	ENDORSED: KINGSLEY. A.		PROJECT No. --	A01
											REV		DRAWN	CHK	END	DATE	APP'D DATE: --		PROJECT No.	
											COPY RIGHT RESERVED									