
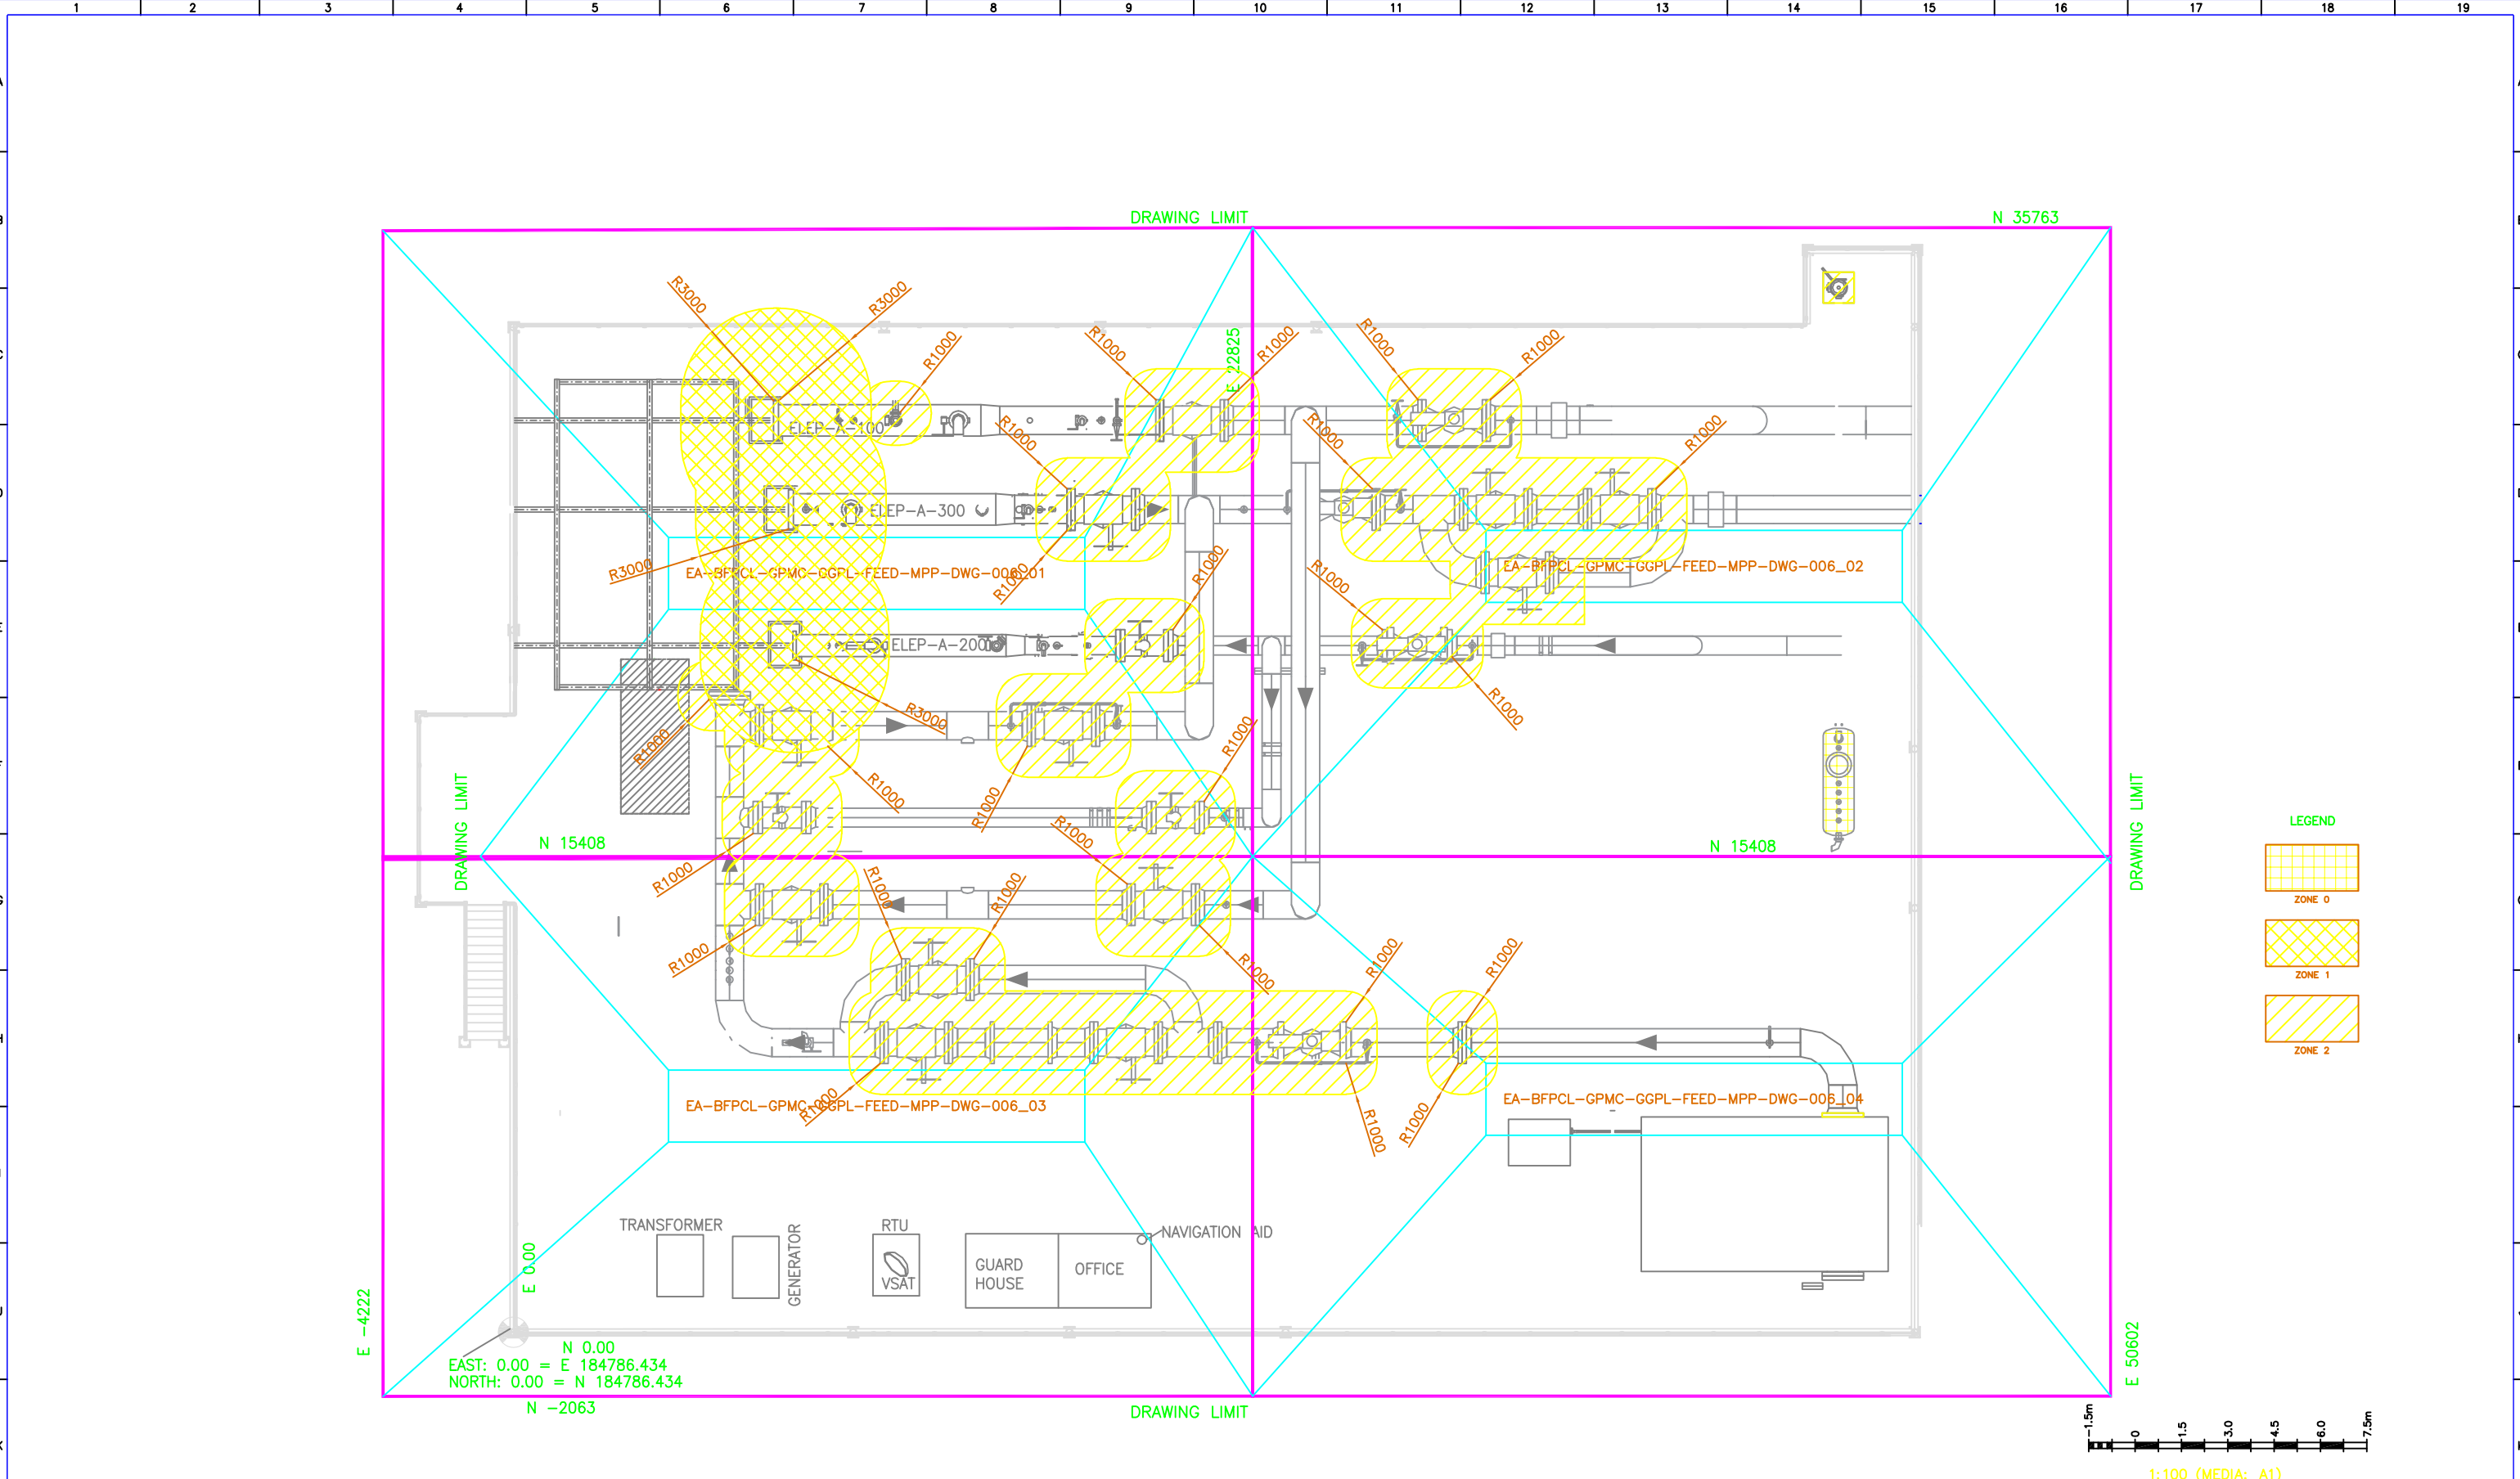


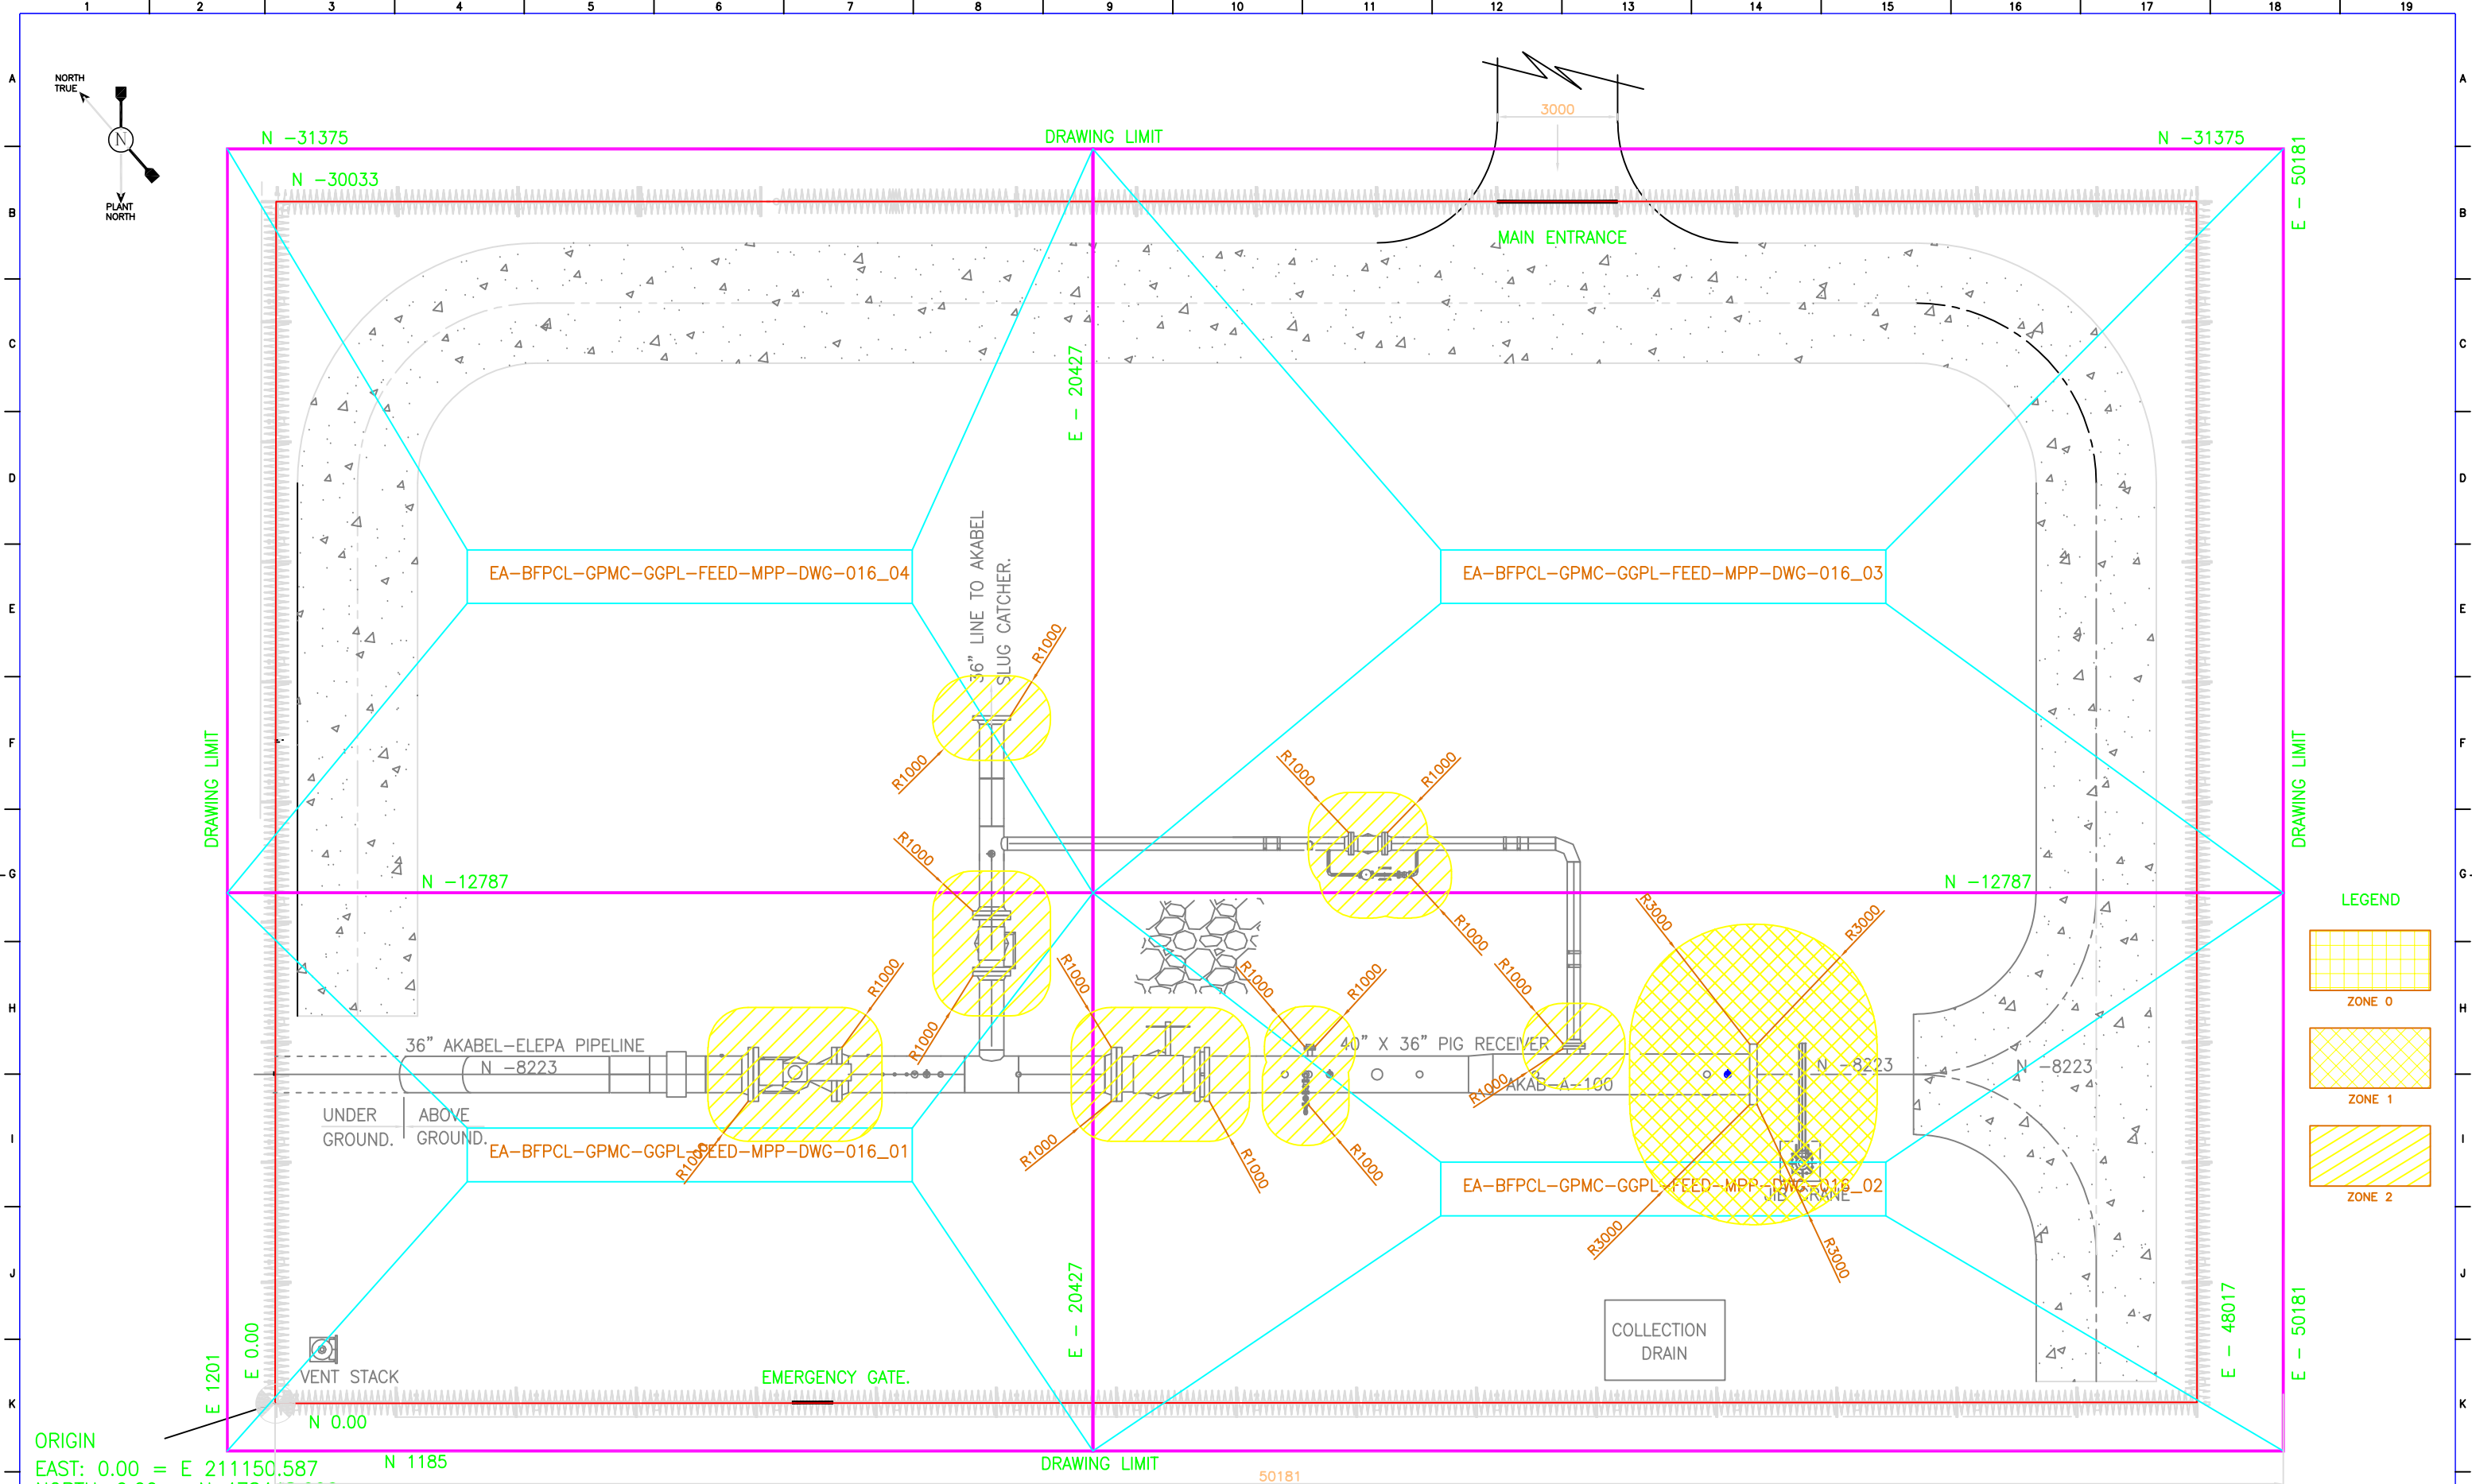

REFERENCE DRAWINGS		DRAWING No.		NOTES: 1. ALL DIMENSIONS ARE IN MILLIMETER UNLESS OTHERWISE STATED. 2. THIS DRAWING IS PRODUCED EXCLUSIVELY FOR THIS PROJECT SCOPE, AND SHOULD NOT BE USED FOR ANY OTHER PURPOSE. 3. THE HAC DRAWING IS BASED ON HAC SCHEDULE No. XXX 4. FOR ANY PROPOSED ELECTRICAL EQUIPMENT INSTALLATIONS WITHIN THE FACILITY, SUCH EQUIPMENT SHALL BE SUITABLE FOR NOT LESS THAN ZONE 2 AREA. 5. IN CASE OF ANY FUTURE ELECTRICAL INSTALLATIONS, INSTALLATION OF POTENTIAL IGNITION SOURCES, OR HOT WORK WITHIN THE FACILITY, CAUTION SHOULD BE TAKEN TO ESTABLISH THE HAC FOR SUCH LOCATION BEFORE EXECUTION.						CONTRACTOR 					BRASS FERTILIZER & PETROCHEMICAL COMPANY LIMITED				
										 GAS PROCESSING AND METHANOL COMPLEX PROJECT FEED FOR GAS GATHERING PIPELINES 									
										LOCATION ELEPA MANFOLD PLATFORM HAZARDOUS AREA CLASSIFICATION – ELEPA									
										DRAWN: CAN DATE: 15/05/2022 SHEET: 2 of 3									
										CHECKED: ENW DRAWING No. EA-BFPCL-GPMC-GGPL-FEED-TMS-DWG-001 REV.									
										ENDORSED: ADR PROJECT No. 11998A R01									
										APP'D DATE: – PROJECT No. –									

[illegible]