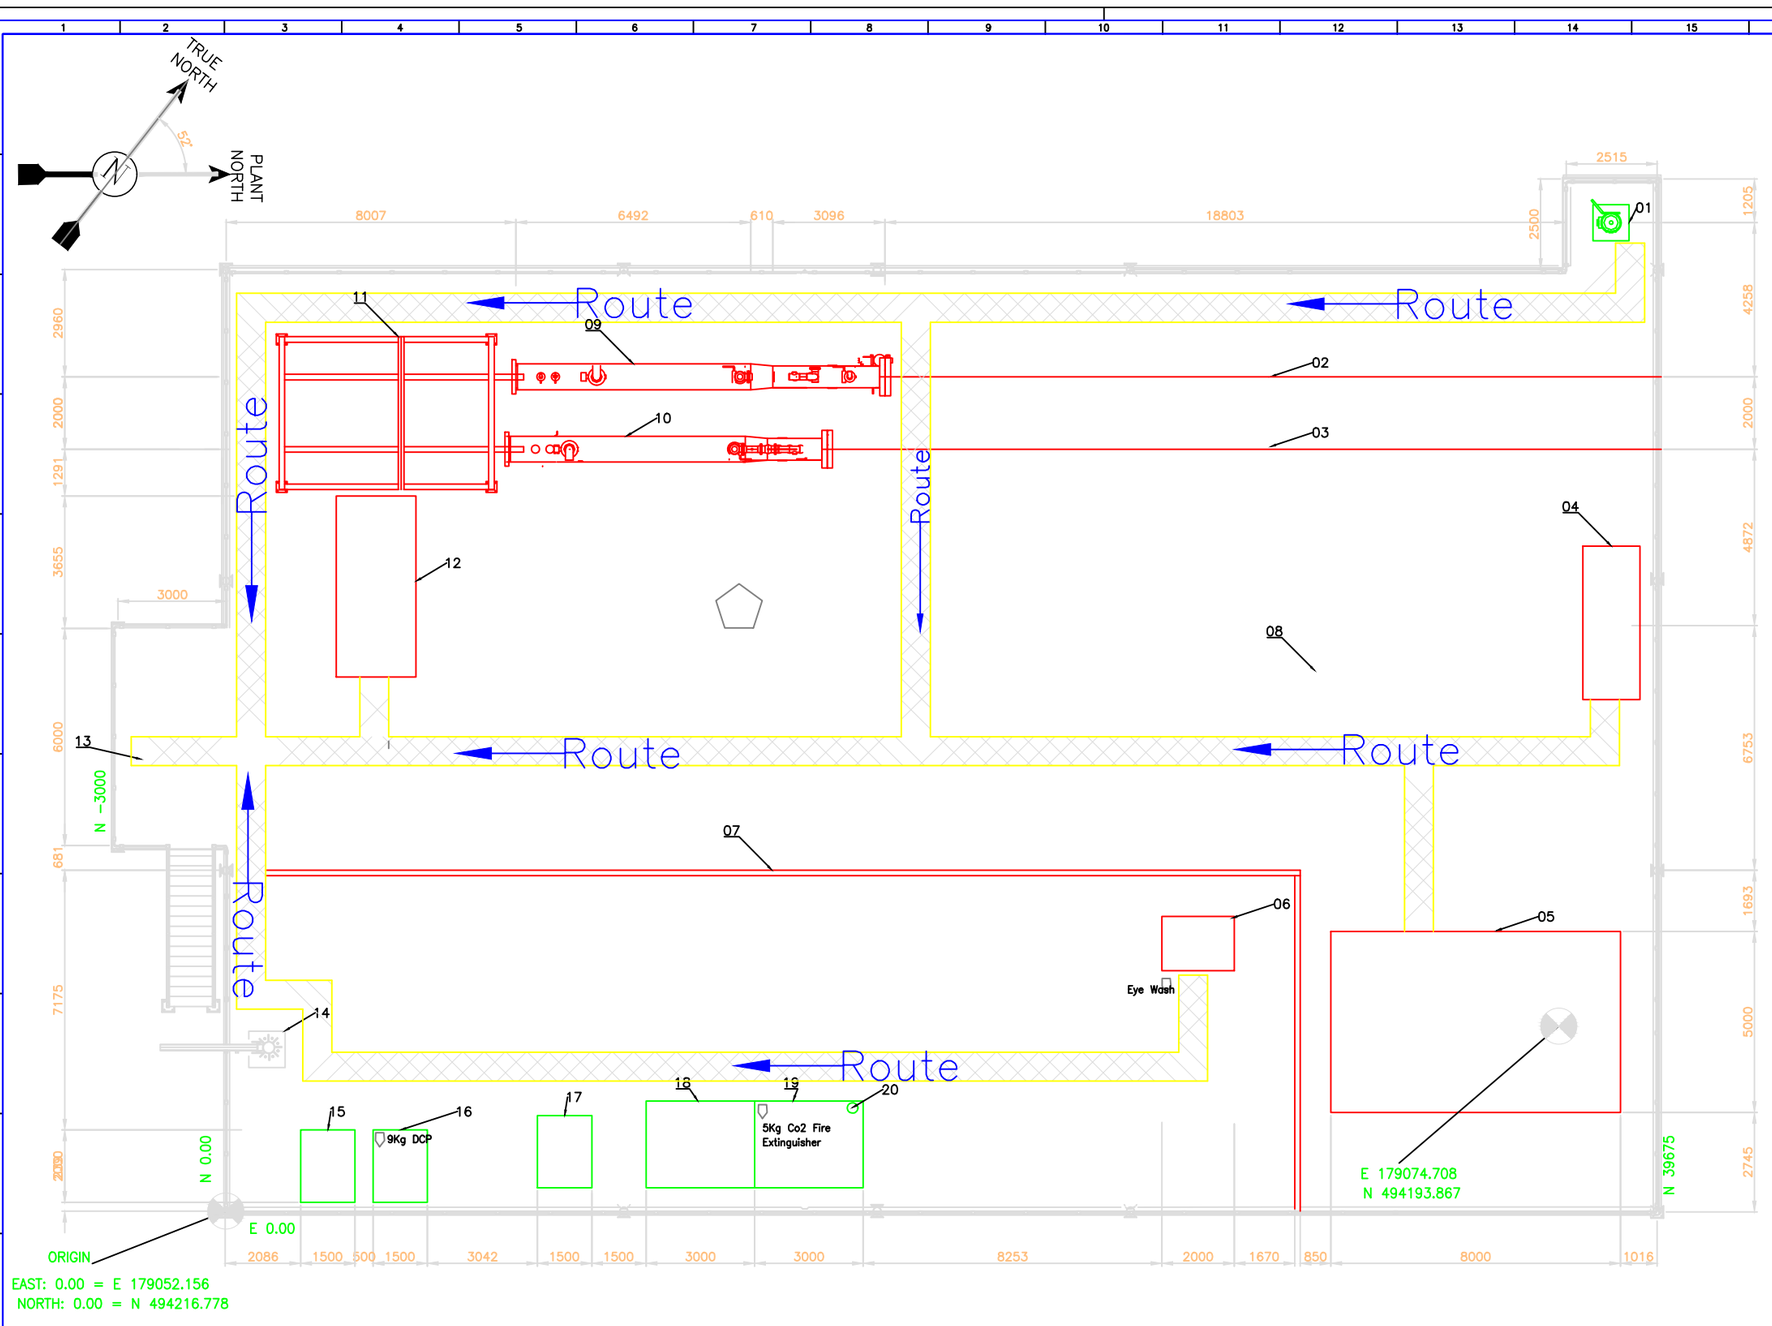

S/N	LEGEND
01	VENT STACK
02	24" OPUGBENE–BBOU PIPELINE
03	24" BBOU–ELEPA PIPELINE
04	BBOU–CLOSED DRAIN TANK–001
05	SPDC WELL HEAD MANIFOLD AND METERING SKID
06	CHEMICAL INJECTION SKID
07	FIRE WALL
08	HD GRATING
09	28" X 24" PIG RECEIVER
10	28" X 24" PIG LAUNCHER
11	MONORAIL
12	BBOU–OPEN DRAIN TANK–001
13	BOAT LANDING
14	JIB CRANE
15	TRANSFORMER
16	GENERATOR
17	RTU
18	GUARD HOUSE
19	OFFICE
05	NAVIGATION AID

REFERENCE DRAWINGS	DRAWING No.

NOTES:

REV					
01	ISSUED FOR REVIEW	CAA	ENW	WEI	10-08-2022
REV		DRAWN	CHK	END	DATE

COPY RIGHT RESERVED

CONTRACTOR epic ATLANTIC

ENDORSEMENT

RELEASED FOR	DESIGN ENGR.	BFPC TECH REP	SPDC TECH REP	DATE

BRASS FERTILIZER & PETROCHEMICAL COMPANY LIMITED

brass fertilizer

GAS PROCESSING AND METHANOL COMPLEX PROJECT
FEED FOR GAS GATHERING PIPELINES

LOCATION
BBOU & ELEPA MANFOLD PLATFORM
SAFETY EQUIPMENT & ESCAPE ROUTE LAYOUT

DRAWN: CAA	DATE: 10-08-2022	SHEET: 1 of 2	
CHECKED: ENW	DRAWING No. EA-BFPCL-GPMC-GGPL-FEED-THS-DWG-002	REV.	
ENDORSED: WEI	PROJECT No. 11998A	01	
APP'D DATE: –	PROJECT No. –		