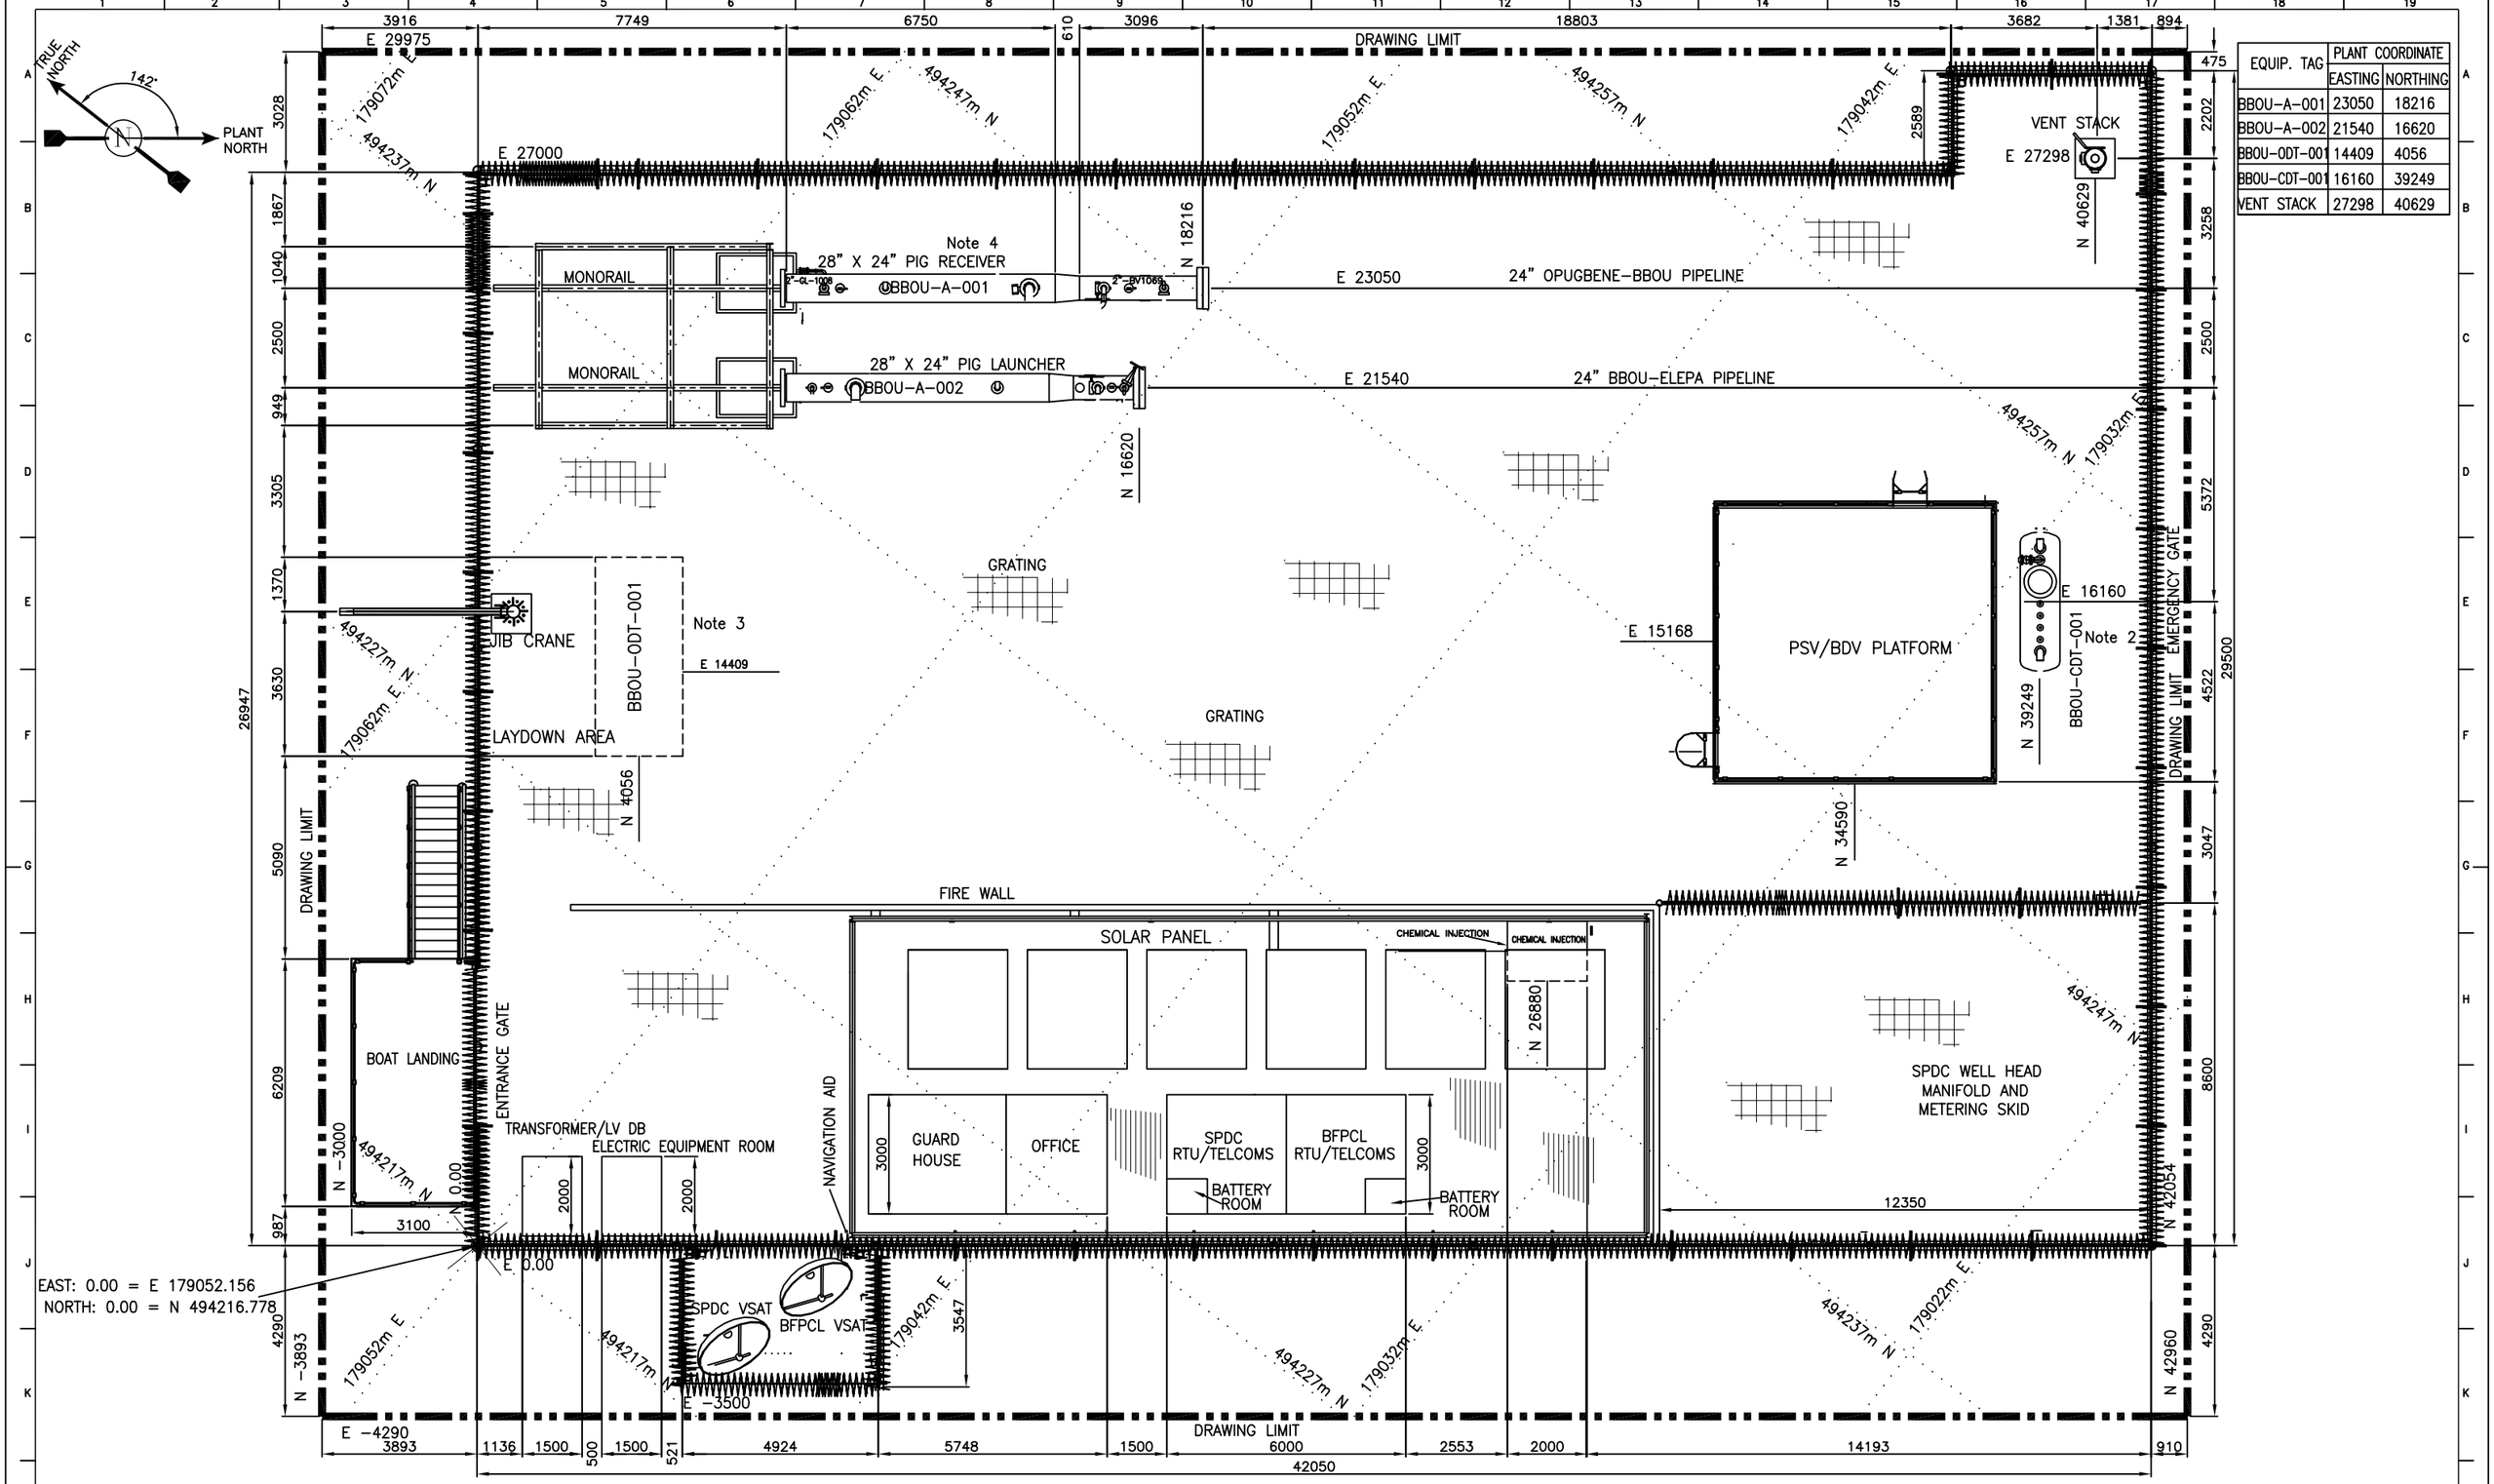

EQUIP. TAG	PLANT COORDINATE	
	EASTING	NORTHING
BBOU-A-001	23050	18216
BBOU-A-002	21540	16620
BBOU-ODT-001	14409	4056
BBOU-CDT-001	16160	39249
VENT STACK	27298	40629

REFERENCE DRAWINGS	DRAWING No.

NOTES:

1. ALL DIMENSIONS ARE IN MM UNLESS OTHERWISE STATED.
2. CLOSE DRAIN TANK TO BE INSTALLED BELOW PLATFORM GRADE.
3. OPEN DRAIN TANK TO BE INSTALLED BELOW PLATFORM GRADE.
4. OPUG PIG RECEIVER BBOU-A-001 IS FOR FUTURE INSTALLATION.
5. PLANT REFERENCE COORDINATE EAST: 0.00, NORTH 0.00 EQUIVALENT COORDINATE 179052mE, 494217mN UTM ZONE 32 WGS 84 DATUM.

REV		DRAWN	CHK	END	DATE
A01	ISSUED FOR APPROVAL	CAN	ENW	ADR	11/12/2022
R01	ISSUED FOR REVIEW	CAN	ENW	ADR	19/06/2022

COPY RIGHT RESERVED

CONTRACTOR

epic ATLANTIC

ENDORSEMENT

RELEASED FOR	DESIGN ENGR.	BFPC TECH REP	SPDC TECH REP	DATE

BRASS FERTILIZER & PETROCHEMICAL COMPANY LIMITED

brass fertilizer

GAS PROCESSING AND METHANOL COMPLEX PROJECT
FEED FOR GAS GATHERING PIPELINES

LOCATION
BBOU MANFOLD PLATFORM
EQUIPMENT LAYOUT PLAN –BBOU

DRAWN: CAN	DATE: 11/12/2022	SHEET: 1 of 1	
CHECKED: ENW	DRAWING No. EA-BFPCL-GPMC-GGPL-FEED-MPP-DWG-005	REV.	
ENDORSED: ADR	PROJECT No. 11998A	A01	
APP'D DATE: –	PROJECT No. –		