


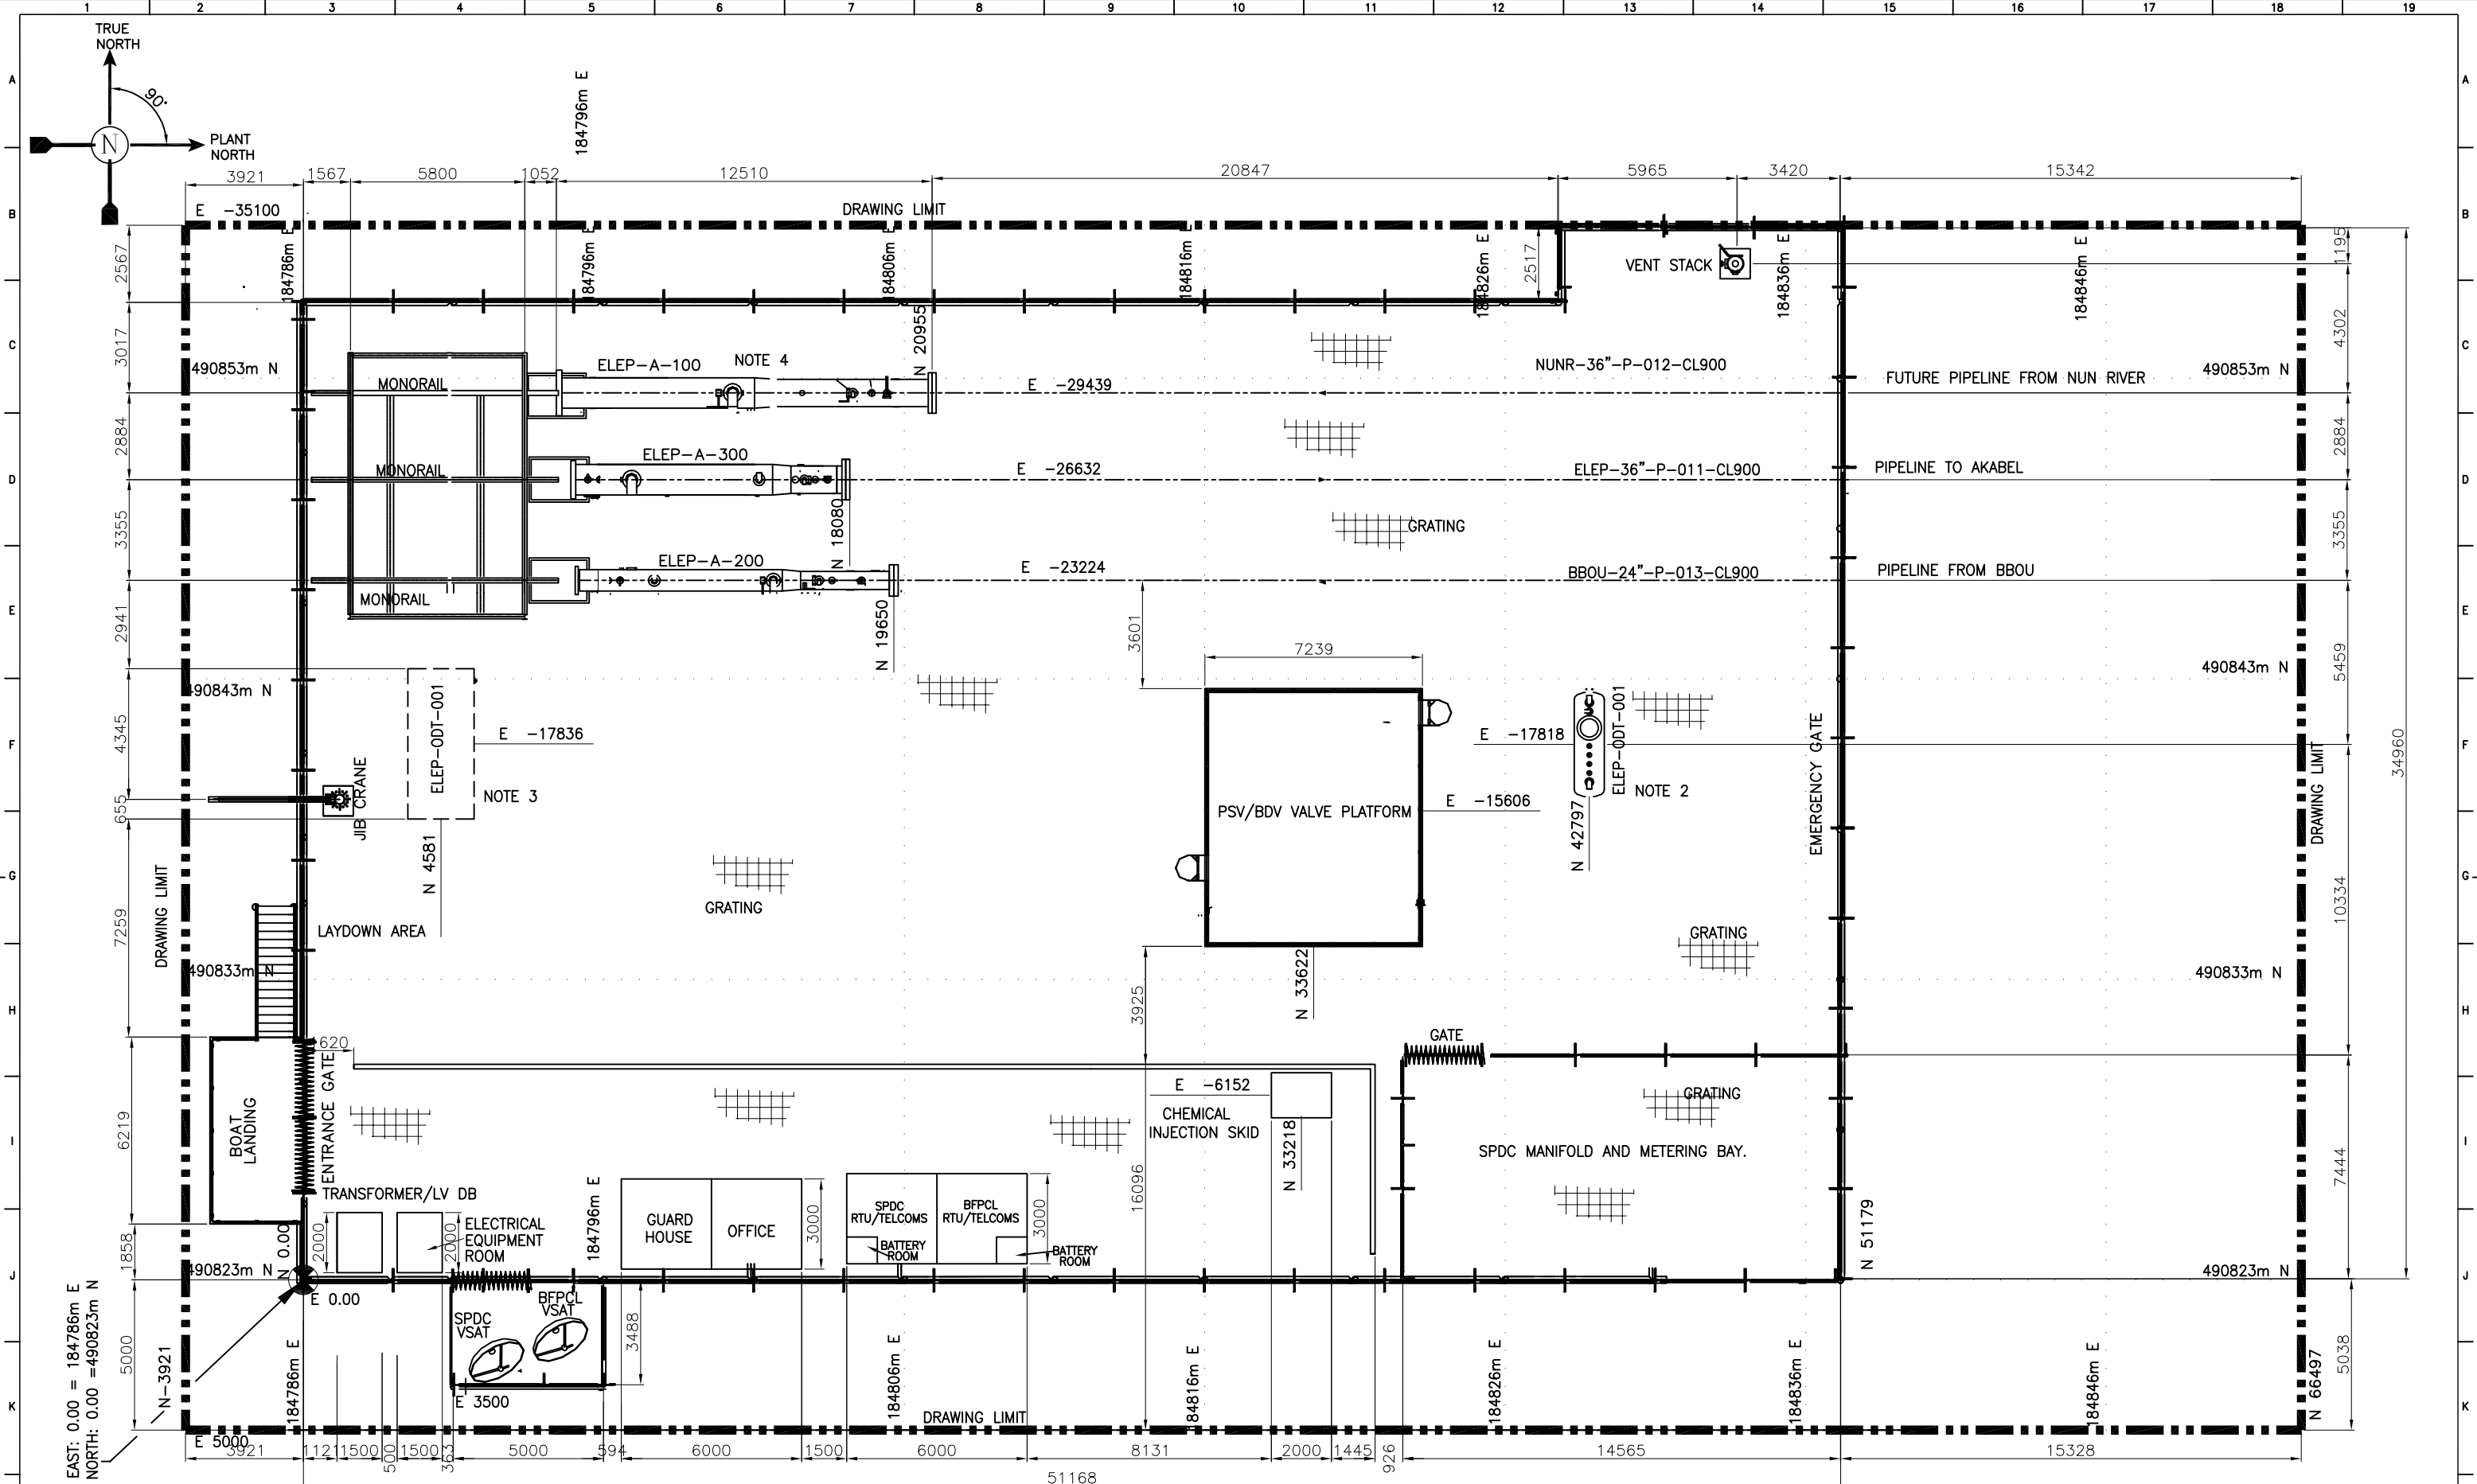

L	REFERENCE DRAWINGS		DRAWING No.		NOTES: 1. ALL DIMENSIONS ARE IN MM UNLESS OTHERWISE STATED. 2. CLOSE DRAIN TANK TO BE INSTALLED BELOW PLATFORM GRADE. 3. OPEN DRAIN TANK TO BE INSTALLED BELOW PLATFORM GRADE. 4. NUNR PIG RECEIVER ELEP-A-001/PIPING IS FOR FUTURE INSTALLATION. 5. PLANT REFERENCE COORDINATE EAST: 0.00, NORTH 0.00 IS EQUIVALENT COORDINATE 184786mE, 490823mN UTM ZONE 32 WGS 84 DATUM.	
---	--------------------	--	-------------	--	---	--	--	