


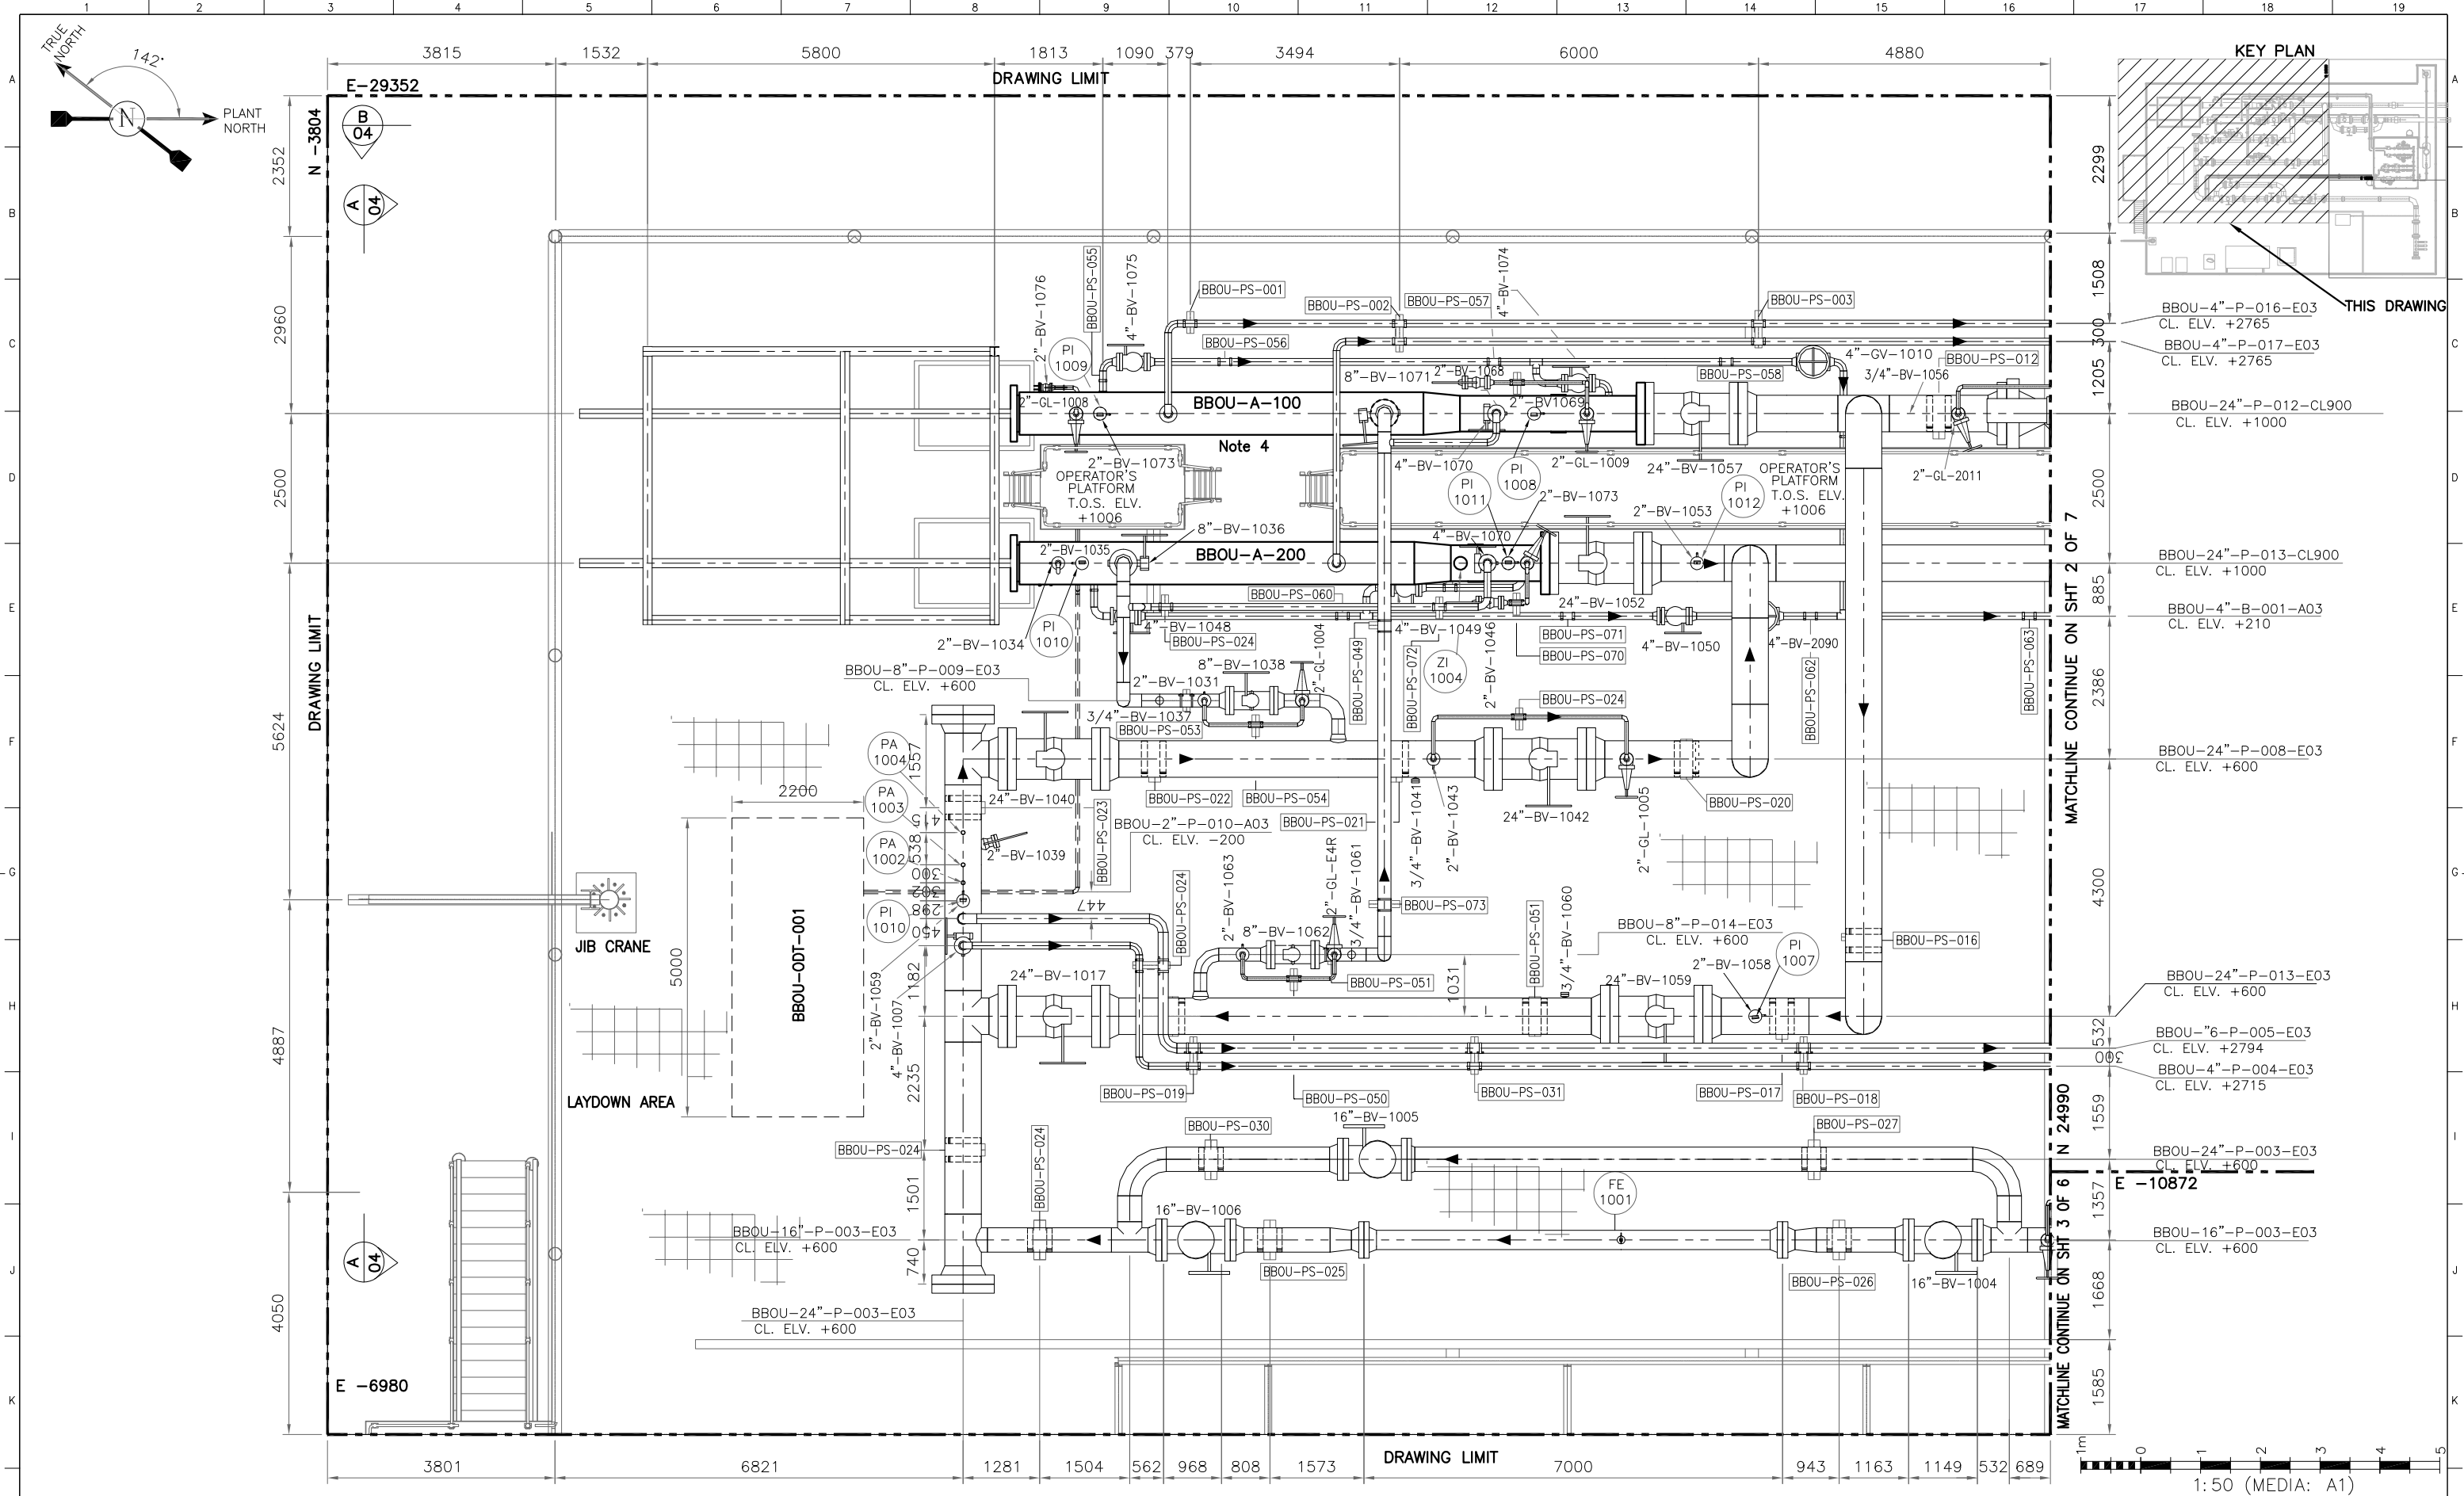


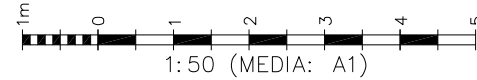



L	REFERENCE DRAWINGS	DRAWING No.	NOTES: 1. All dimensions are in mm unless otherwise stated. 2. Bottom of Platform is 3m from the highest tidal level. 3. The size of vent stack is assumed pending availability of date from process. 4. The Close drain tank and the open drain tank is located under of the platform deck with an access hatch. 5. OPUG Pig Receiver BBOU-A-001 is for future installation. 6. Plant Reference Coordinates EAST: 0.00, NORTH 0.00 Equivalent Coordinate 179052mE, 494217mN UTM ZONE 32 WGS 84 DATUM.	CONTRACTOR						BRASS FERTILIZER & PETROCHEMICAL COMPANY LIMITED							
										brass fertilizer GAS PROCESSING AND METHANOL COMPLEX PROJECT FEED FOR GAS GATHERING PIPELINES 							
				ENDORSEMENT						LOCATION BBOU MANFOLD PLATFORM PIPING GENERAL ARRANGEMENT DRAWING - BBOU							
									RELEASED FOR	DESIGN ENGR.	BFFC TECH REP	SPDC TECH REP	DATE				
M				A01	ISSUED FOR APPROVAL	CAN	ENW	ADR	11/12/2022						DRAWN: CAN	DATE: 11/12/2022	SHEET: 1 of 7
				R01	ISSUED FOR REVIEW	CAN	ENW	ADR	11/07/2022						CHECKED: ENW	DRAWING No. EA-BFFCL-GPMC-CGPL-FEED-MPP-DWG-014	REV.
				REV			DRAWN	CHK	END	DATE					ENDORSED: ADR	PROJECT No. 11998A	A01
				COPY RIGHT RESERVED											APP'D DATE: -	PROJECT No. -	

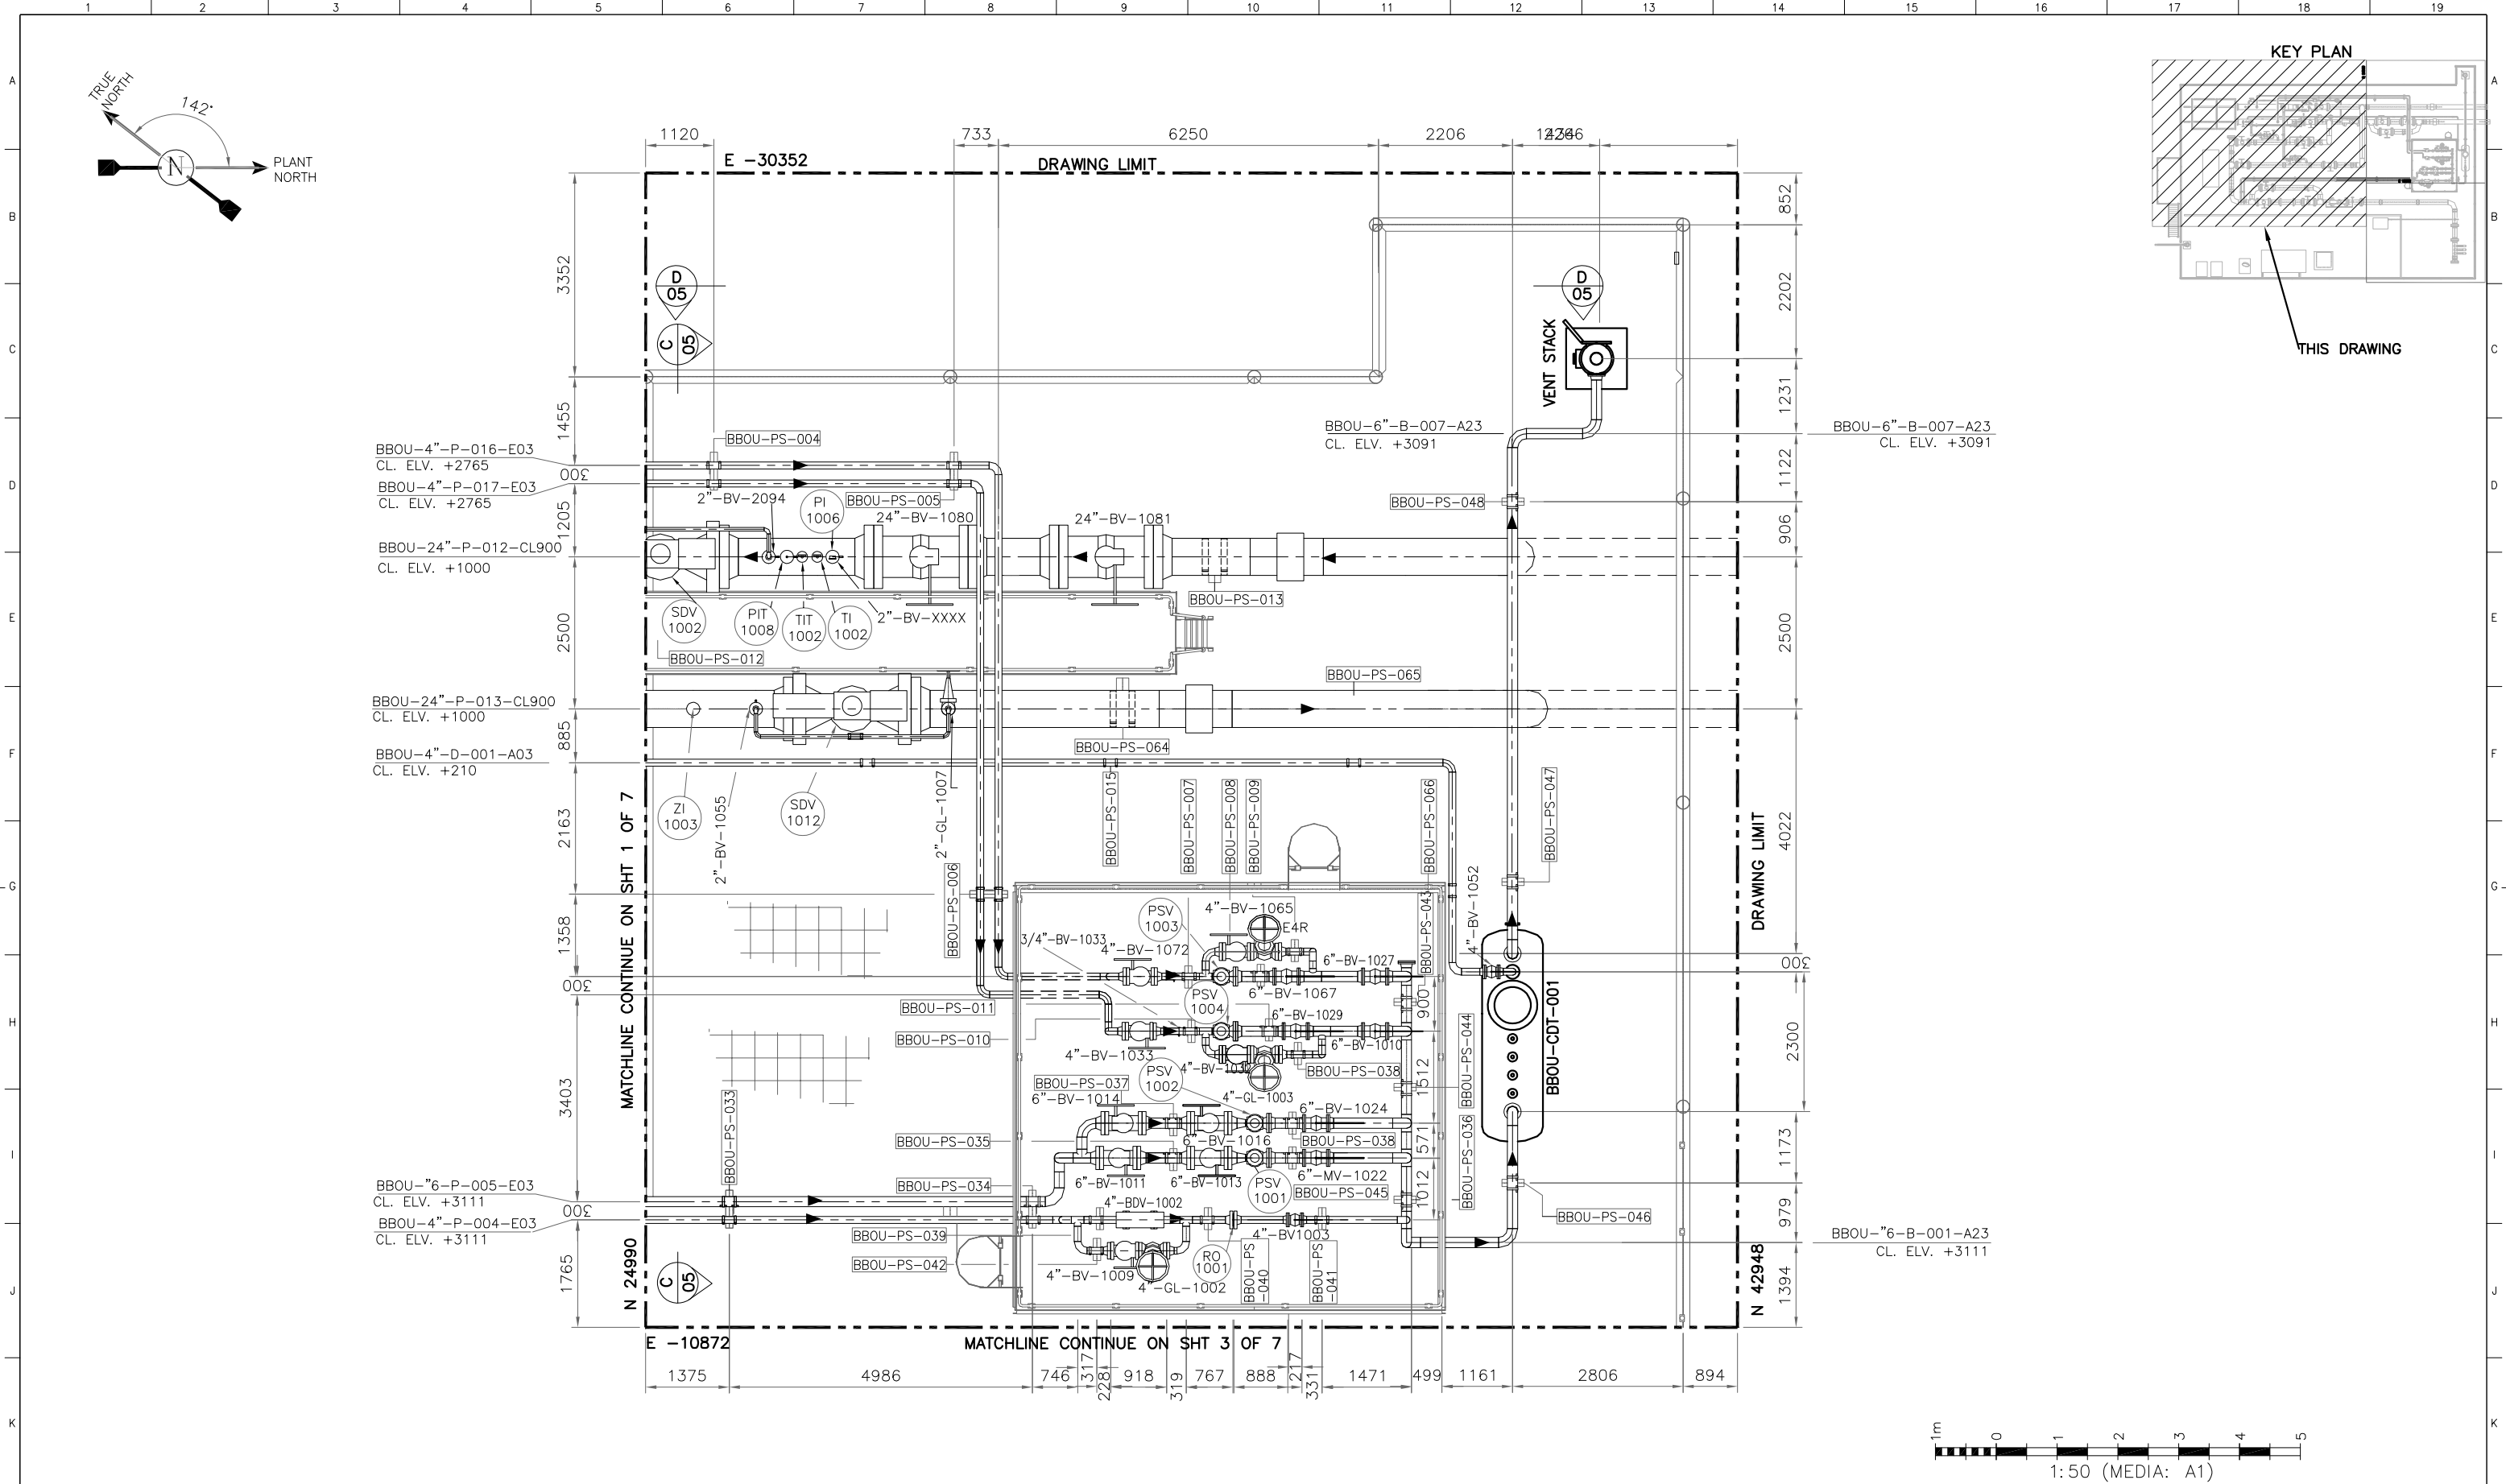


L	REFERENCE DRAWINGS		DRAWING No.		NOTES: 1. All dimensions are in mm unless otherwise stated. 2. Bottom of Platform is 3m from the highest tidal level. 3. The size of vent stack is assumed pending availability of date from process. 4. The Close drain tank and the open drain tank is located under of the platform deck with an access hatch. 5. OPUG Pig Receiver BBOU-A-001 is for future installation. 6. Plant Reference Coordinates EAST: 0.00, NORTH 0.00 Equivalent Coordinate 179052mE, 494217mN UTM ZONE 32 WGS 84 DATUM.							CONTRACTOR				BRASS FERTILIZER & PETROCHEMICAL COMPANY LIMITED																					
																 GAS PROCESSING AND METHANOL COMPLEX PROJECT  FEED FOR GAS GATHERING PIPELINES																					
												ENDORSEMENT				LOCATION BBOU MANFOLD PLATFORM PIPING GENERAL ARRANGEMENT DRAWING – BBOU																					
												RELEASED FOR		DESIGN ENGR.	BFPC TECH REP	SPDC TECH REP	DATE	DRAWN: CAN		DATE: 11/12/2022		SHEET: 2 OF 7															
M											A01 ISSUED FOR APPROVAL		CAN	ENW	ADR	11/12/2022							CHECKED: ENW		DRAWING No. EA-BFPCL-GPMC-CGPL-FEED-MPP-DWG-014		REV.										
											R01 ISSUED FOR REVIEW		CAN	ENW	ADR	11/07/2022							ENDORSED: ADR		PROJECT No. 11998A		A01										
											REV			DRAWN	CHK	END	DATE							APP'D DATE: –		PROJECT No. –											
											COPY RIGHT RESERVED																										
1		2		3		4		5		6		7		8		9		10		11		12		13		14		15		16		17		18		19	

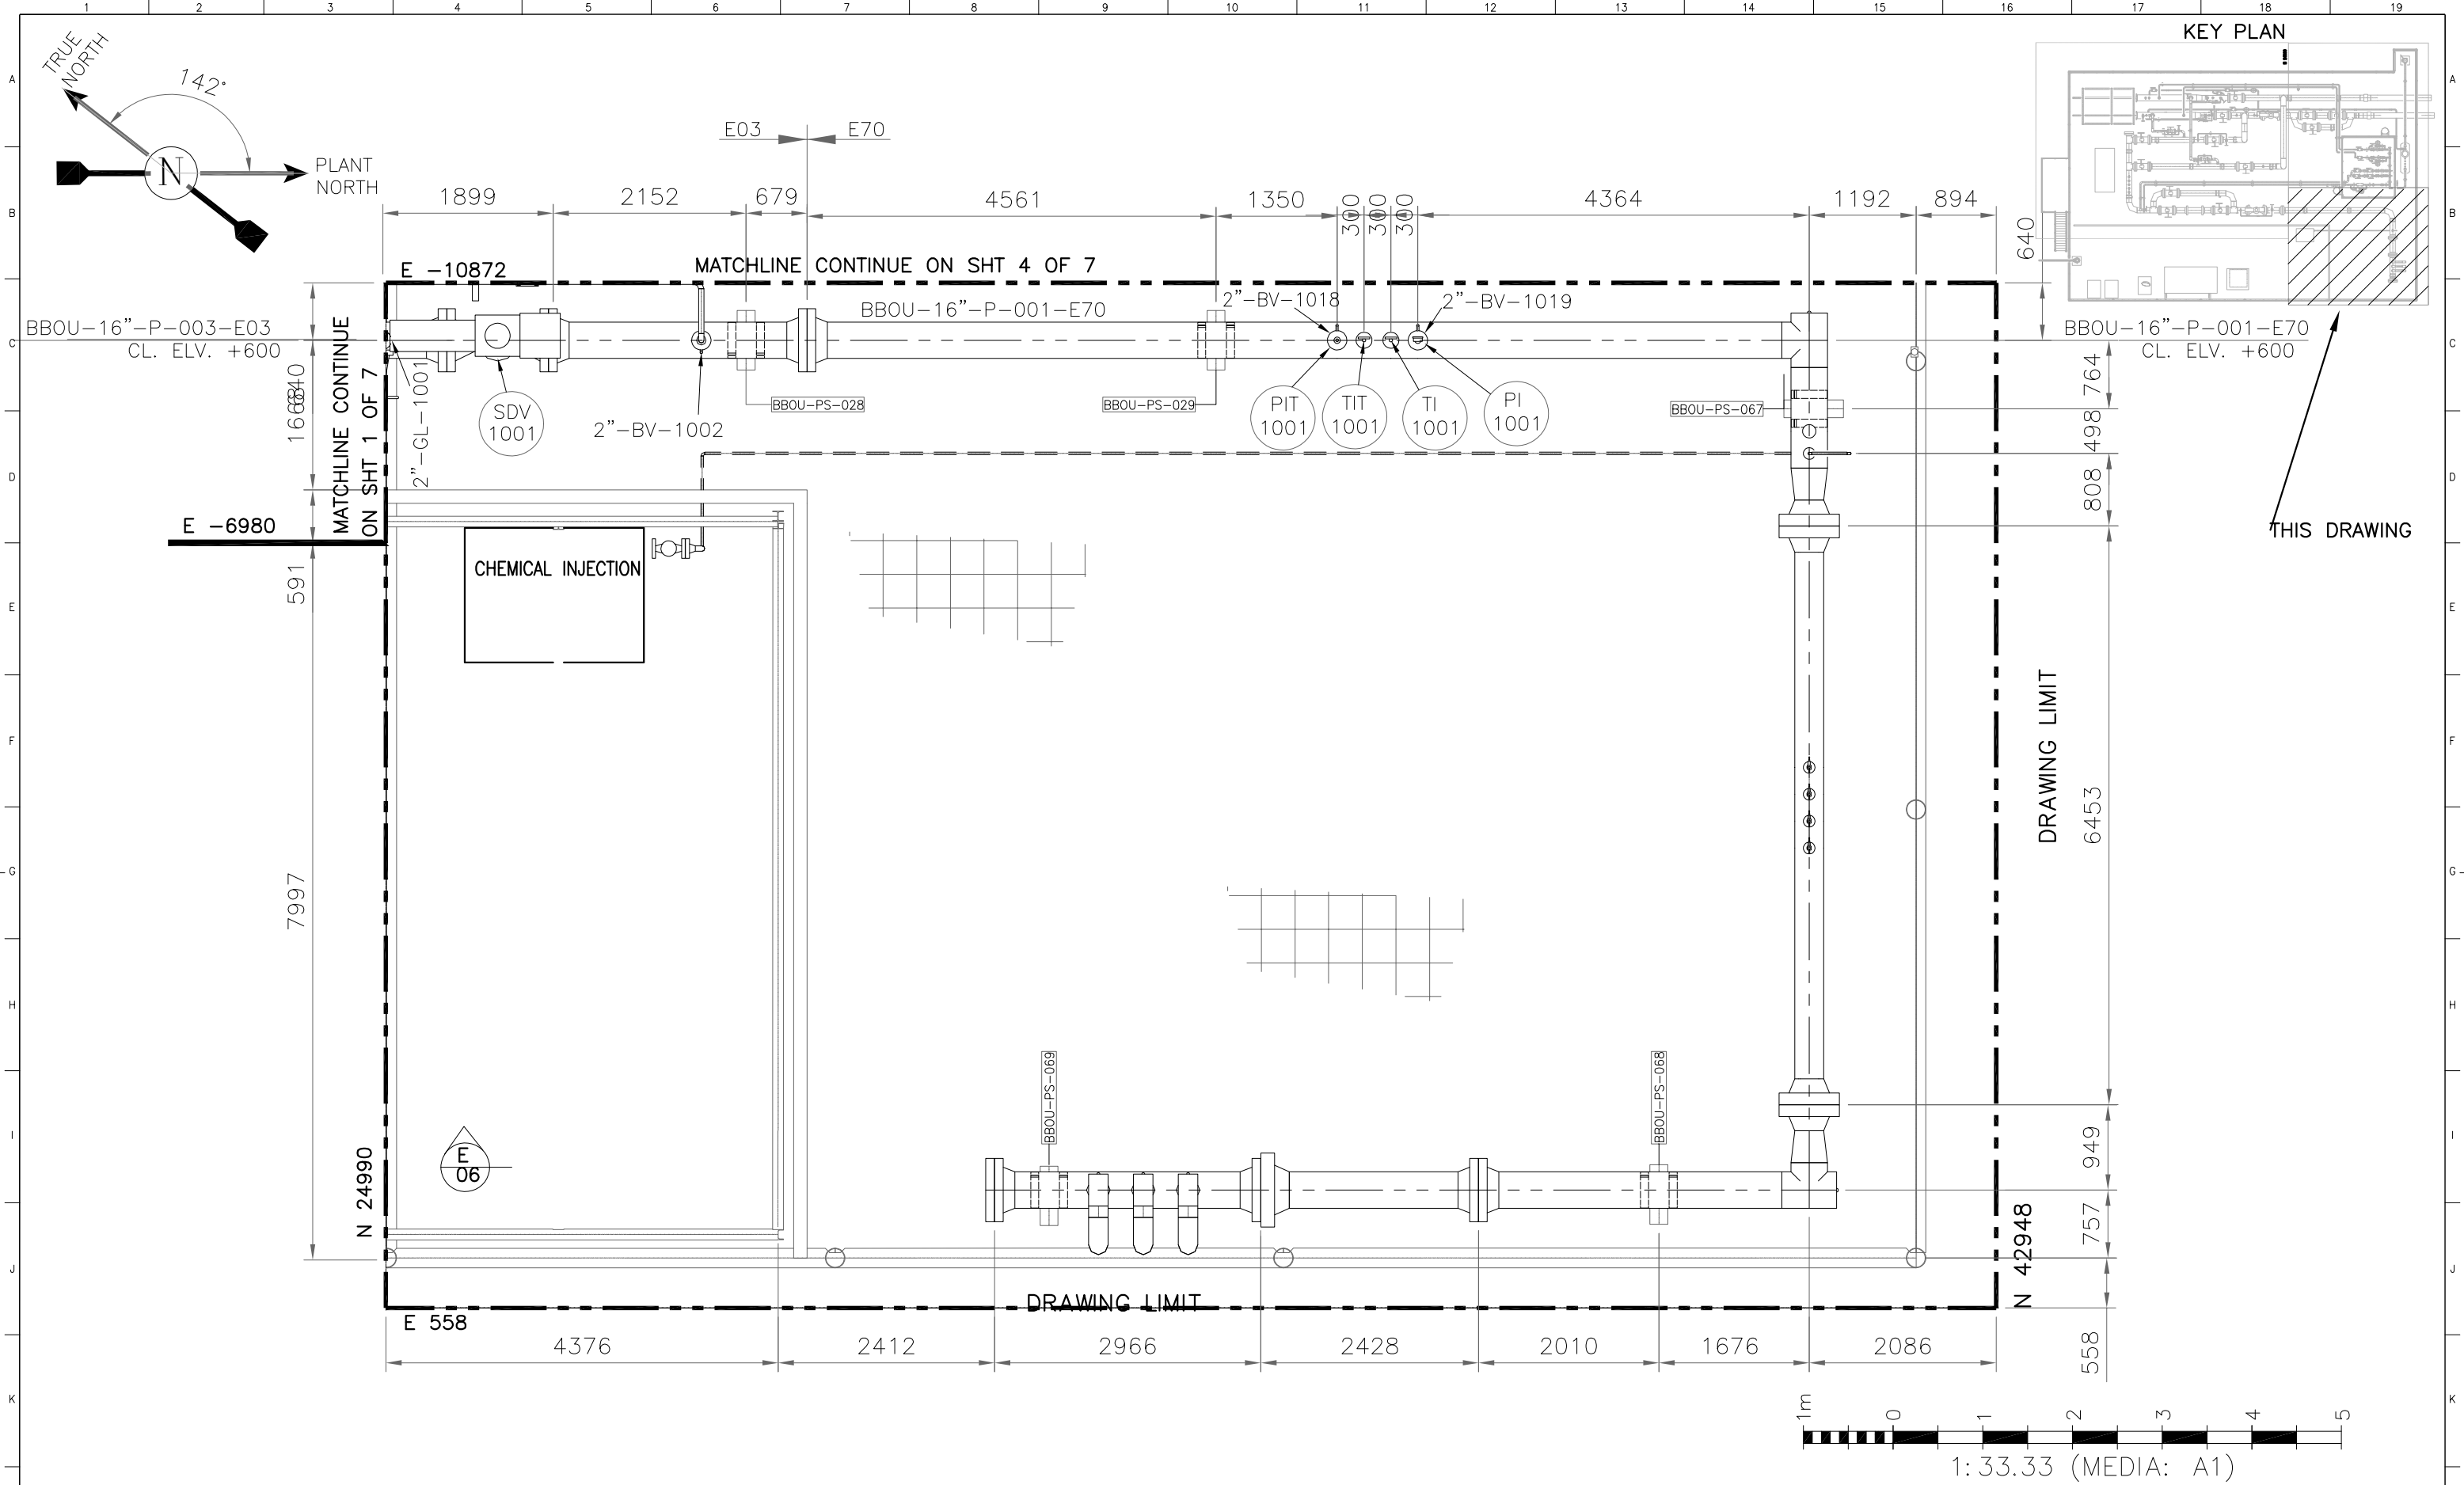

L	REFERENCE DRAWINGS		DRAWING No.		NOTES: 1. All dimensions are in mm unless otherwise stated. 2. Bottom of Platform is 3m from the highest tidal level. 3. The size of vent stack is assumed pending availability of date from process. 4. The Close drain tank and the open drain tank is located under of the platform deck with an access hatch. 5. OPUG Pig Receiver BBOU-A-001 is for future installation. 6. Plant Reference Coordinates EAST: 0.00, NORTH 0.00 Equivalent Coordinate 179052mE, 494217mN UTM ZONE 32 WGS 84 DATUM.																				CONTRACTOR				BRASS FERTILIZER & PETROCHEMICAL COMPANY LIMITED																								
																															 GAS PROCESSING AND METHANOL COMPLEX PROJECT FEED FOR GAS GATHERING PIPELINES																						
																															LOCATION BBOU MANFOLD PLATFORM PIPING GENERAL ARRANGEMENT DRAWING – BBOU																						
M															A01		ISSUED FOR APPROVAL		CAN		ENW		ADR		11/12/2022										DRAWN: CAN		DATE: 11/12/2022		SHEET: 3 OF 7														
															R01		ISSUED FOR REVIEW		CAN		ENW		ADR		11/07/2022										CHECKED: ENW		DRAWING No. EA-BFPCL-GPMC-CGPL-FEED-MPP-DWG-014		REV.														
															REV				DRAWN		CHK		END		DATE										ENDORSED: ADR		PROJECT No. 11998A																
																																			APP'D DATE: –		PROJECT No. –		A01														
																		COPY RIGHT RESERVED																																			
1		2		3		4		5		6		7		8		9		10		11		12		13		14		15		16		17		18		19																	

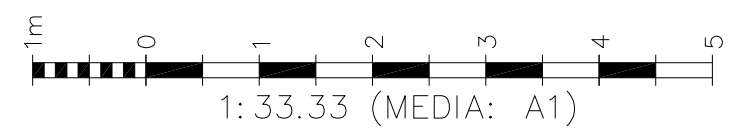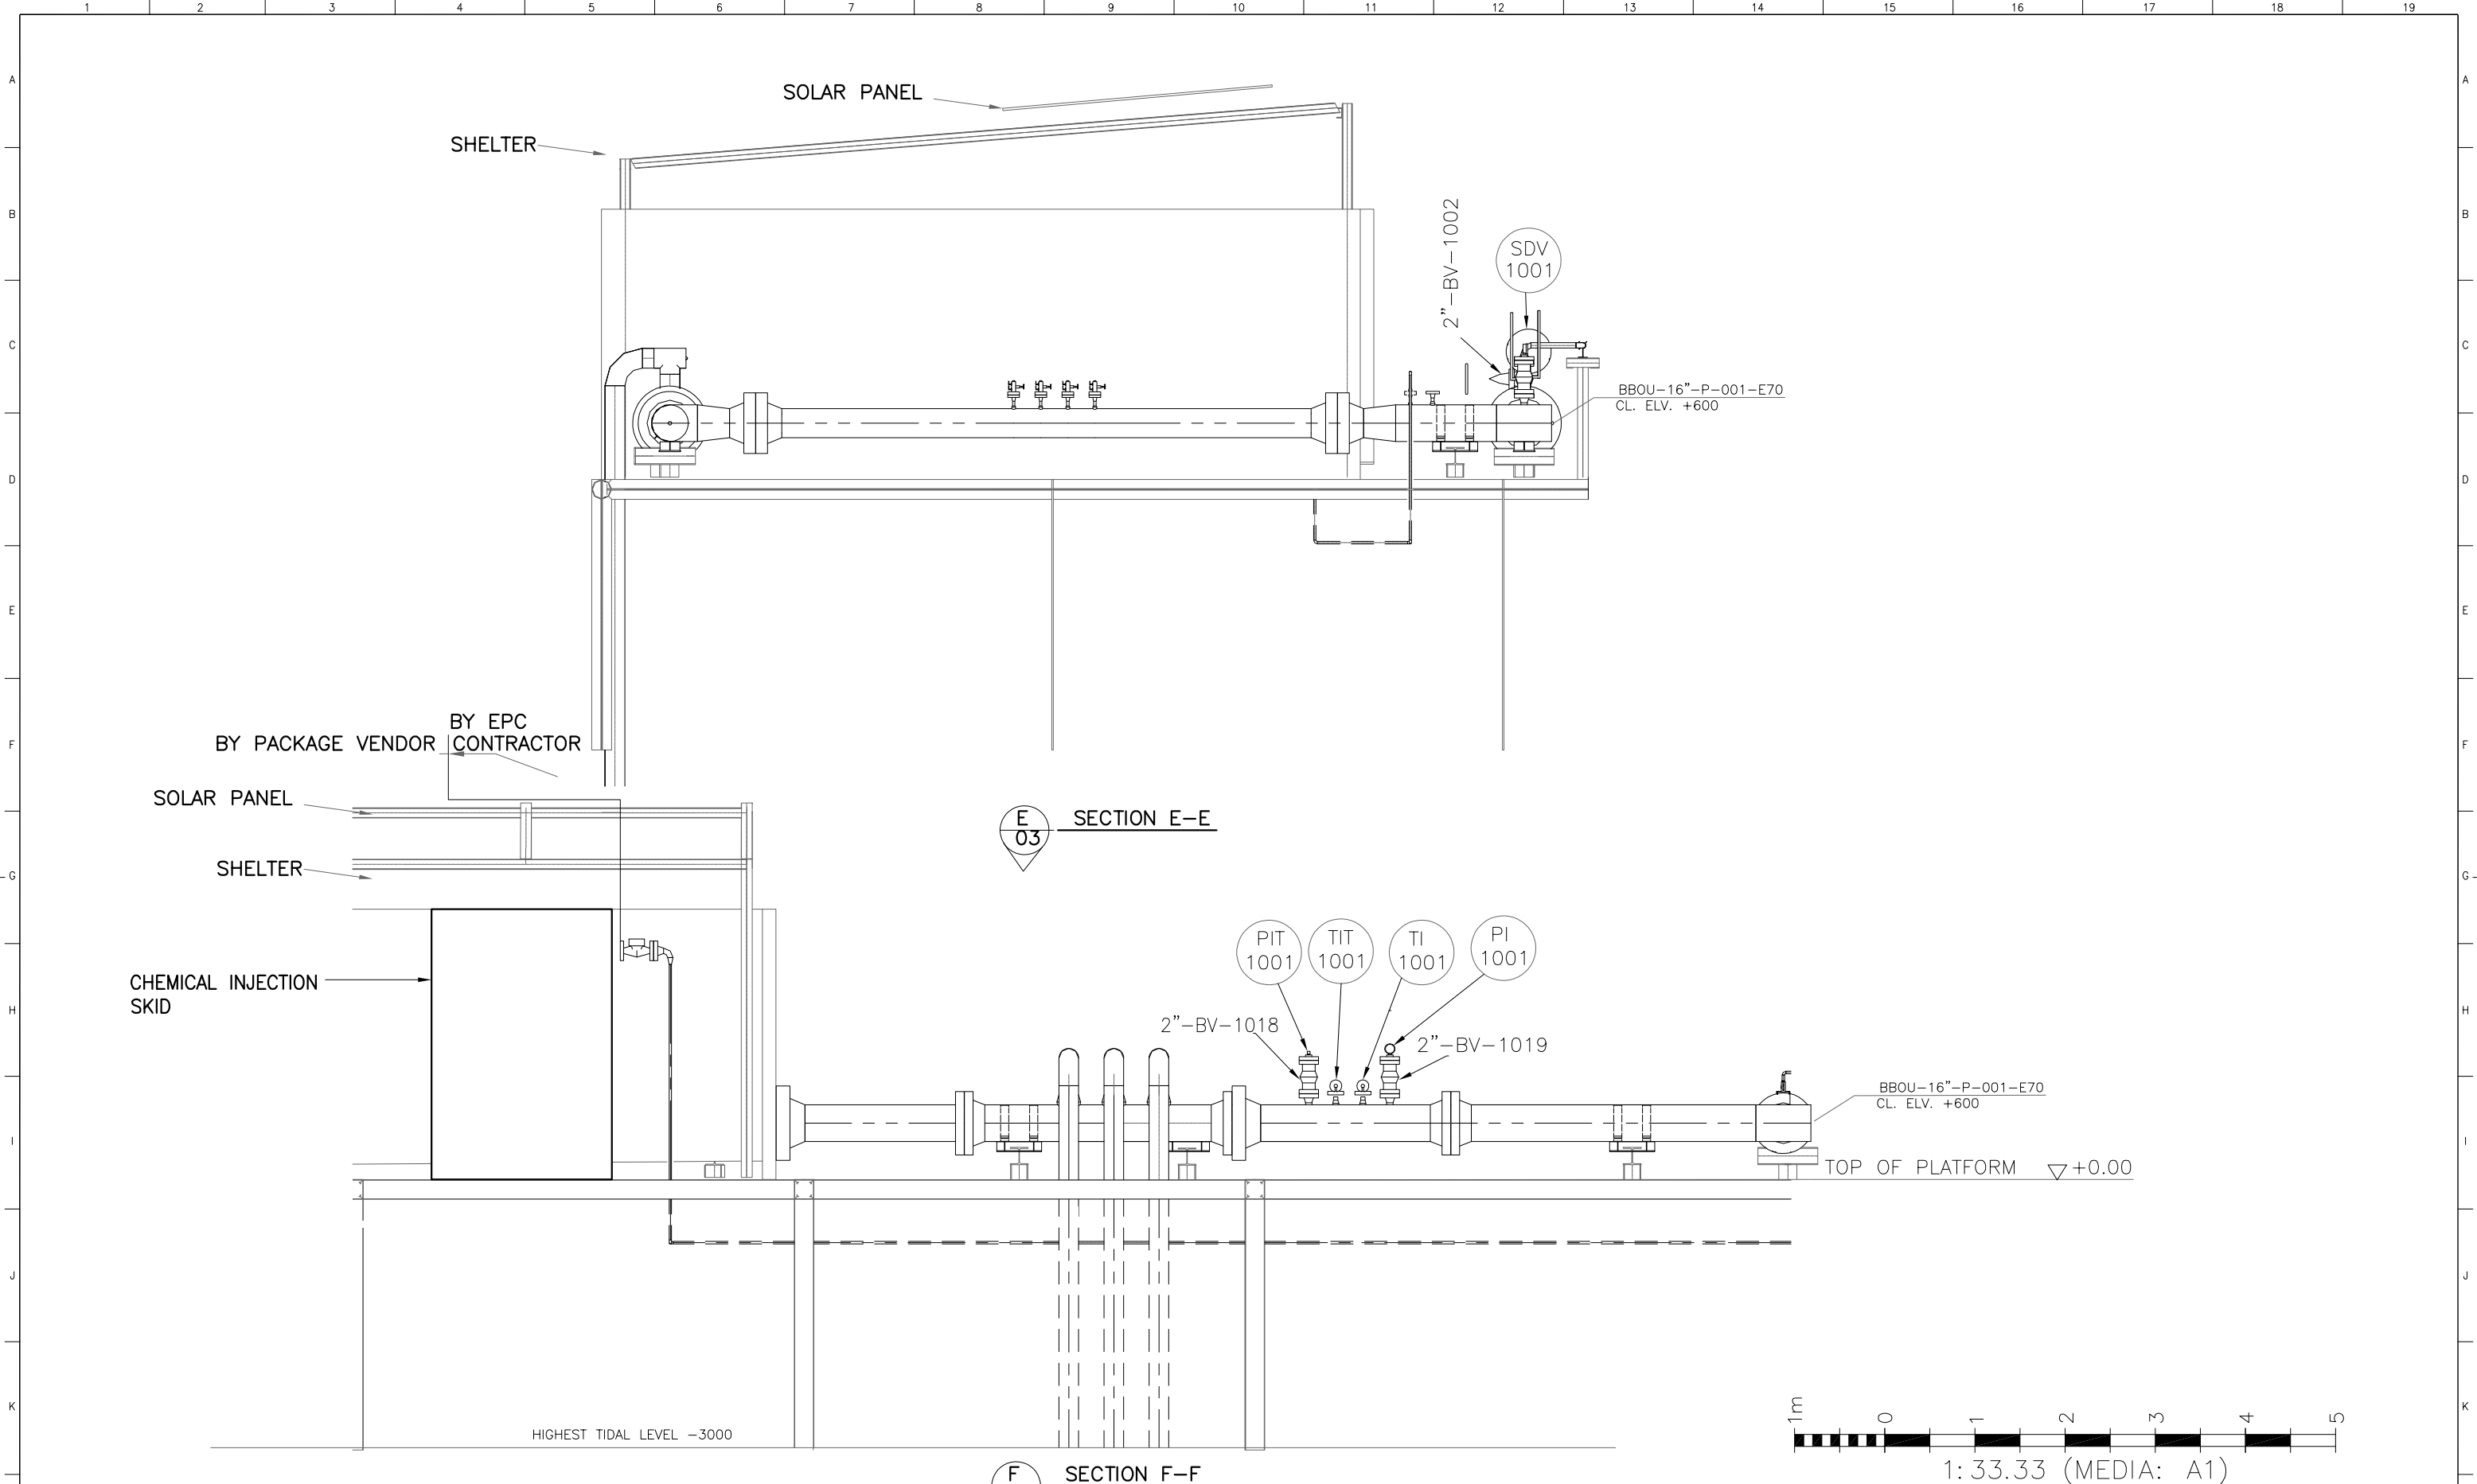

L	REFERENCE DRAWINGS		DRAWING No.		NOTES: 1. All dimensions are in mm unless otherwise stated. 2. Bottom of Platform is 3m from the highest tidal level. 3. The size of vent stack is assumed pending availability of date from process. 4. The Close drain tank and the open drain tank is located under of the platform deck with an access hatch. 5. OPUG Pig Receiver BBOU-A-001 is for future installation. 6. Plant Reference Coordinates EAST: 0.00, NORTH 0.00 Equivalent Coordinate 179052mE, 494217mN UTM ZONE 32 WGS 84 DATUM.							CONTRACTOR								BRASS FERTILIZER & PETROCHEMICAL COMPANY LIMITED								
																				GAS PROCESSING AND METHANOL COMPLEX PROJECT FEED FOR GAS GATHERING PIPELINES								
M																												

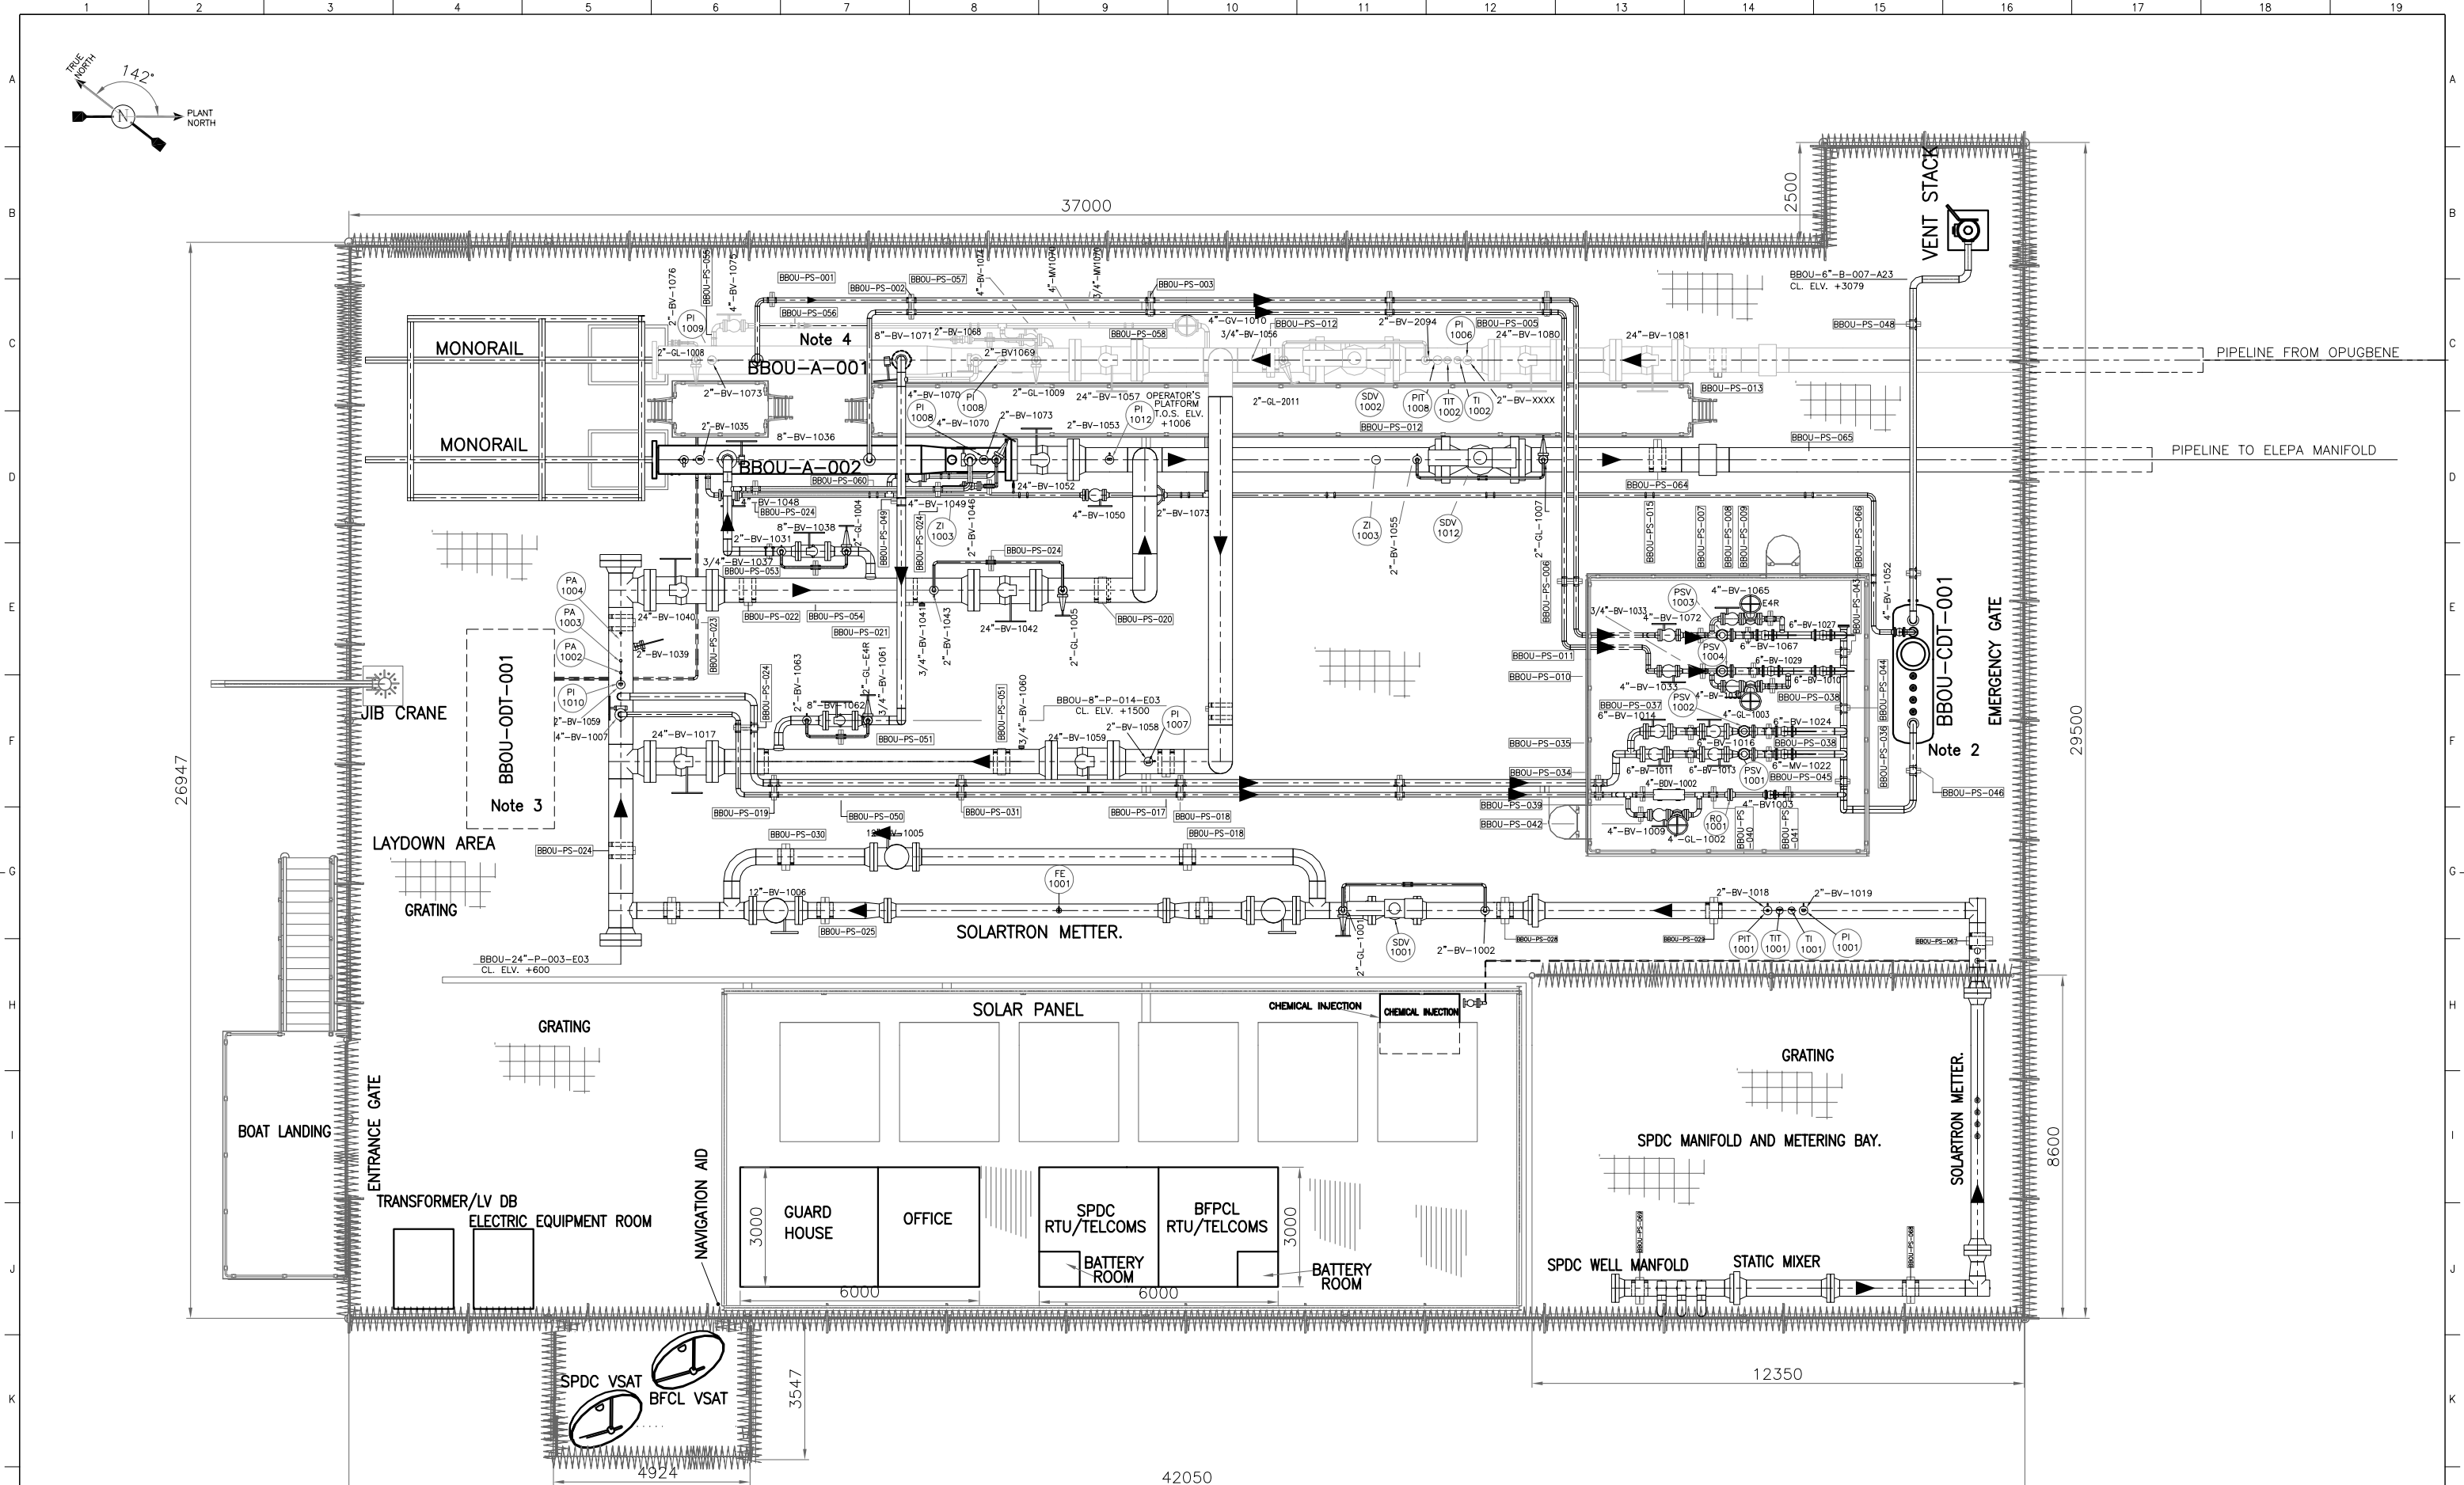

L	REFERENCE DRAWINGS	DRAWING No.	NOTES: 1. ALL DIMENSIONS ARE IN MM UNLESS OTHERWISE STATED. 2. CLOSE DRAIN TANK TO BE INSTALLED BELOW PLATFORM GRADE. 3. OPEN DRAIN TANK TO BE INSTALLED BELOW PLATFORM GRADE. 4. OPUG PIG RECEIVER BBOU-A-001/PIPING IS FOR FUTURE INSTALLATION. 5. PLANT REFERENCE COORDINATE EAST: 0.00, NORTH 0.00 EQUIVALENT COORDINATE 179052mE, 494217mN UTM ZONE 32 WGS 84 DATUM.	
---	--------------------	-------------	--	--	