

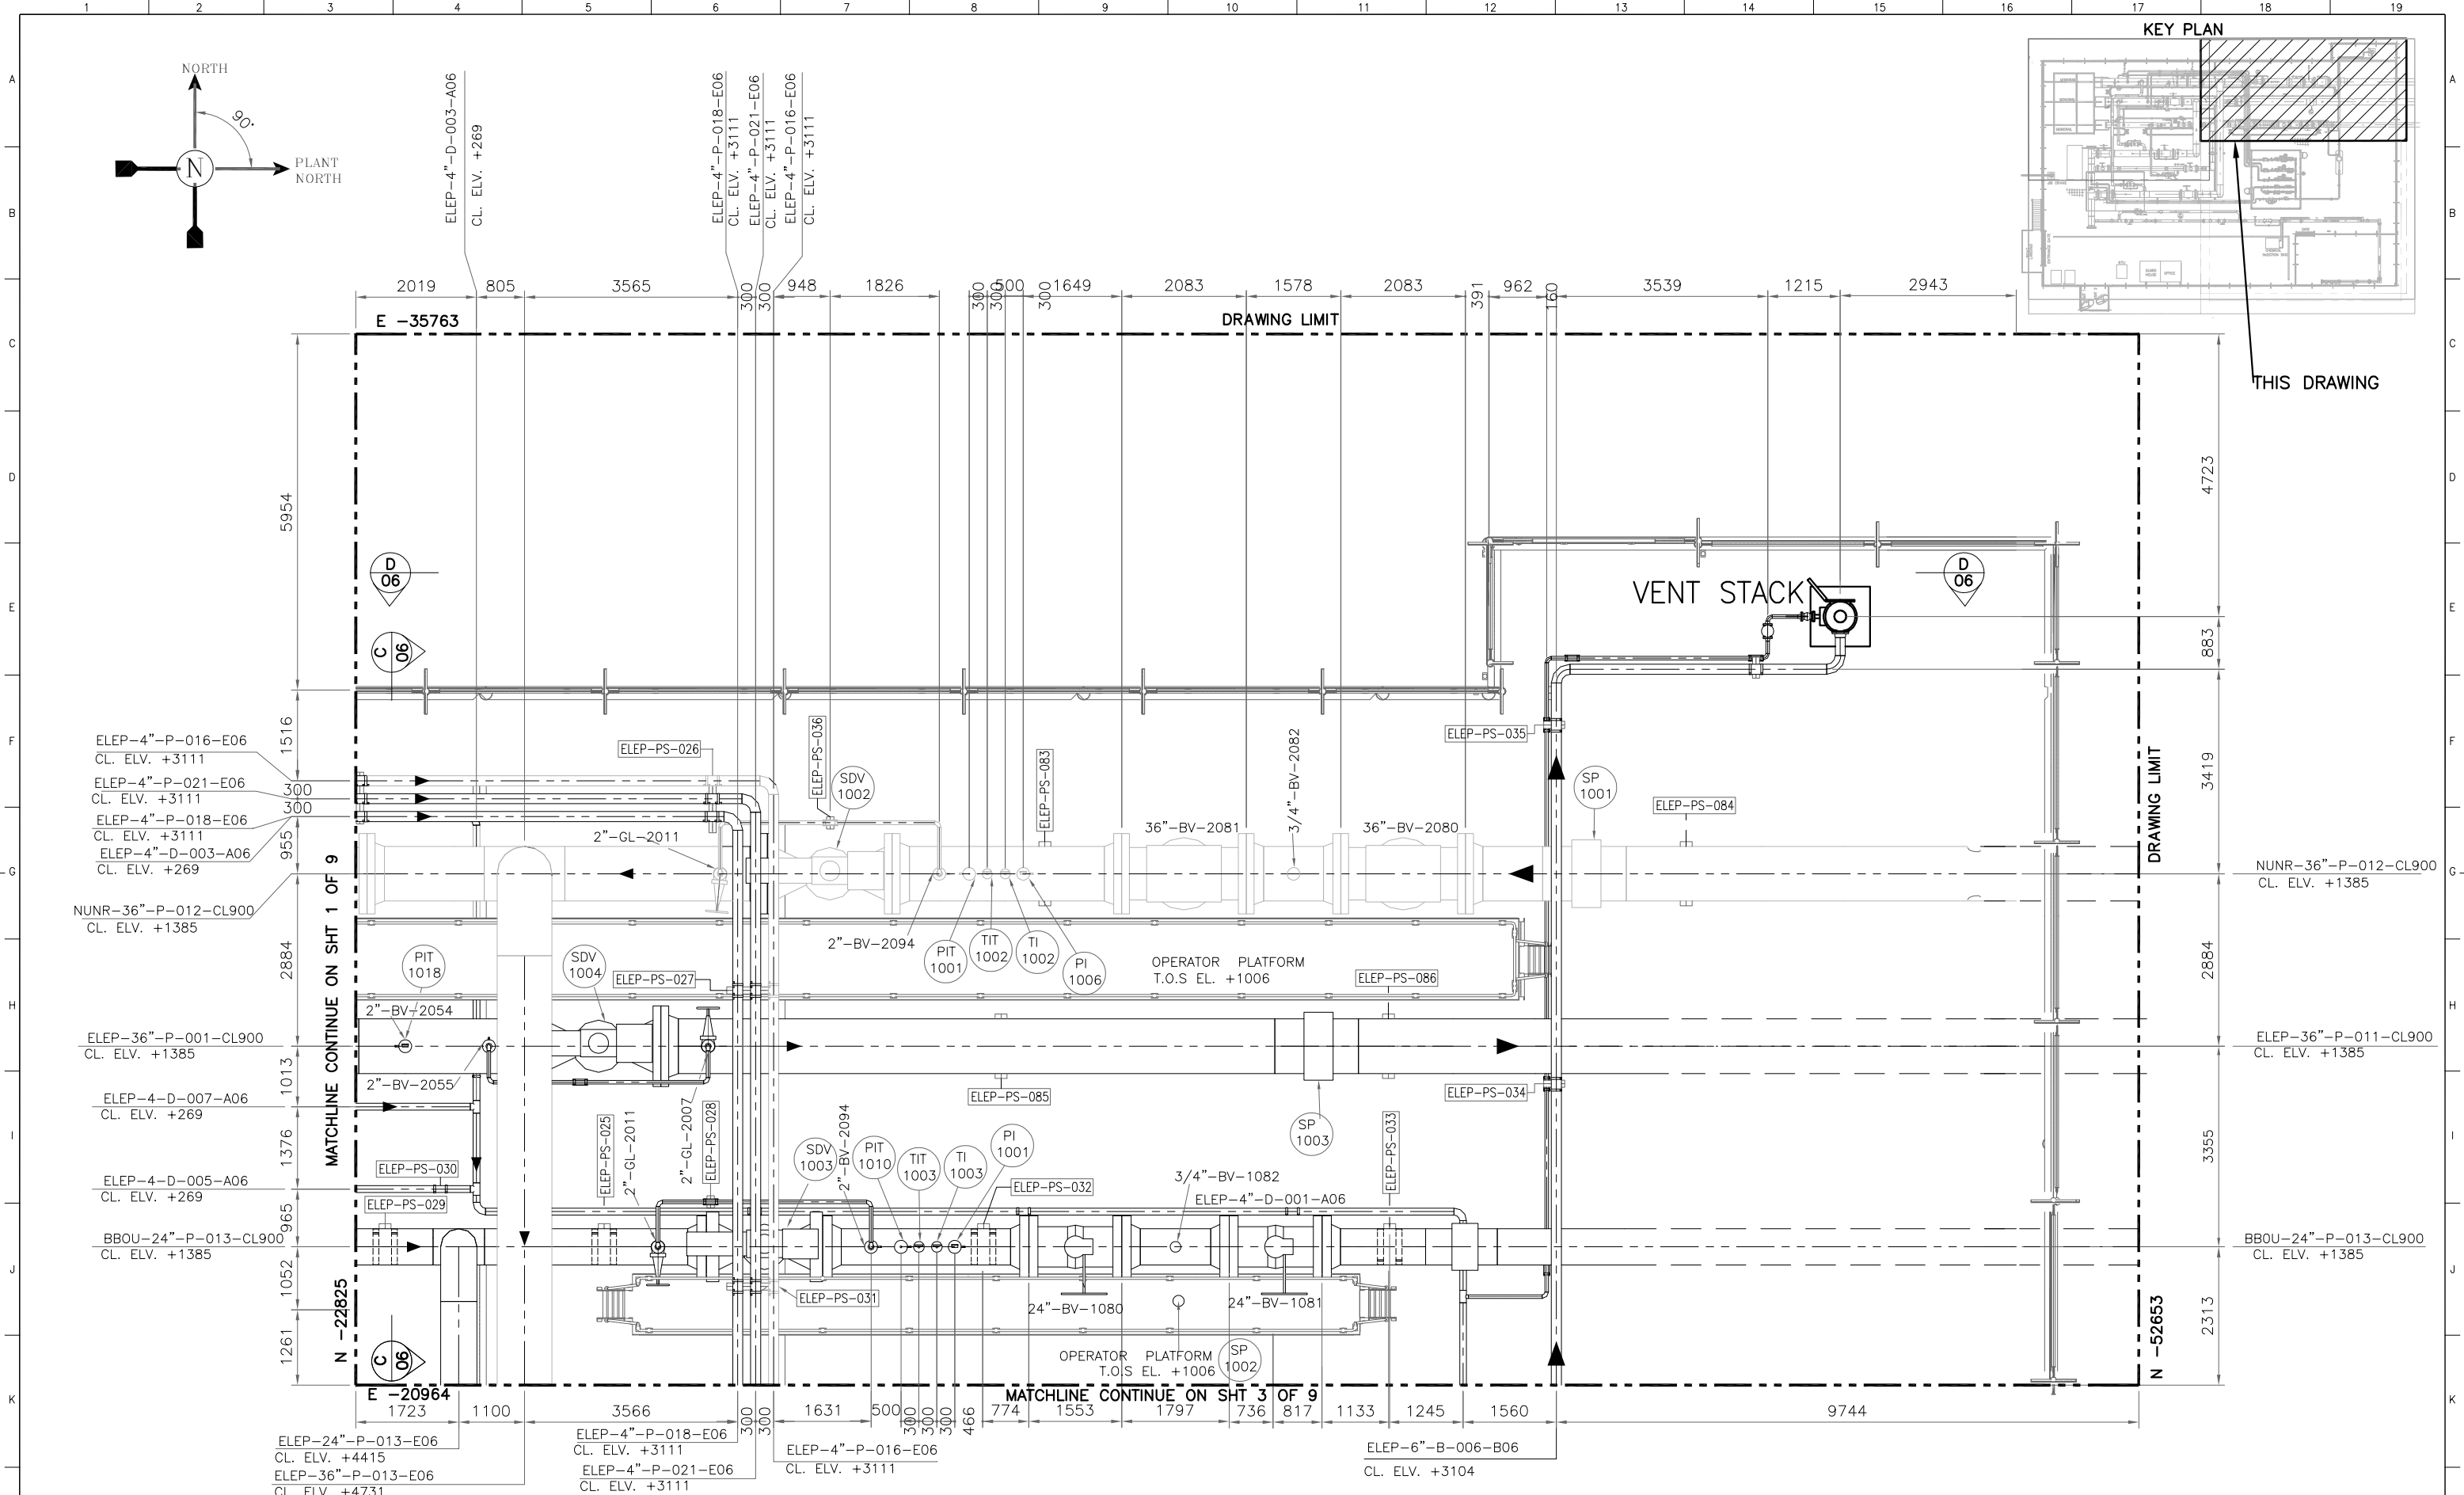
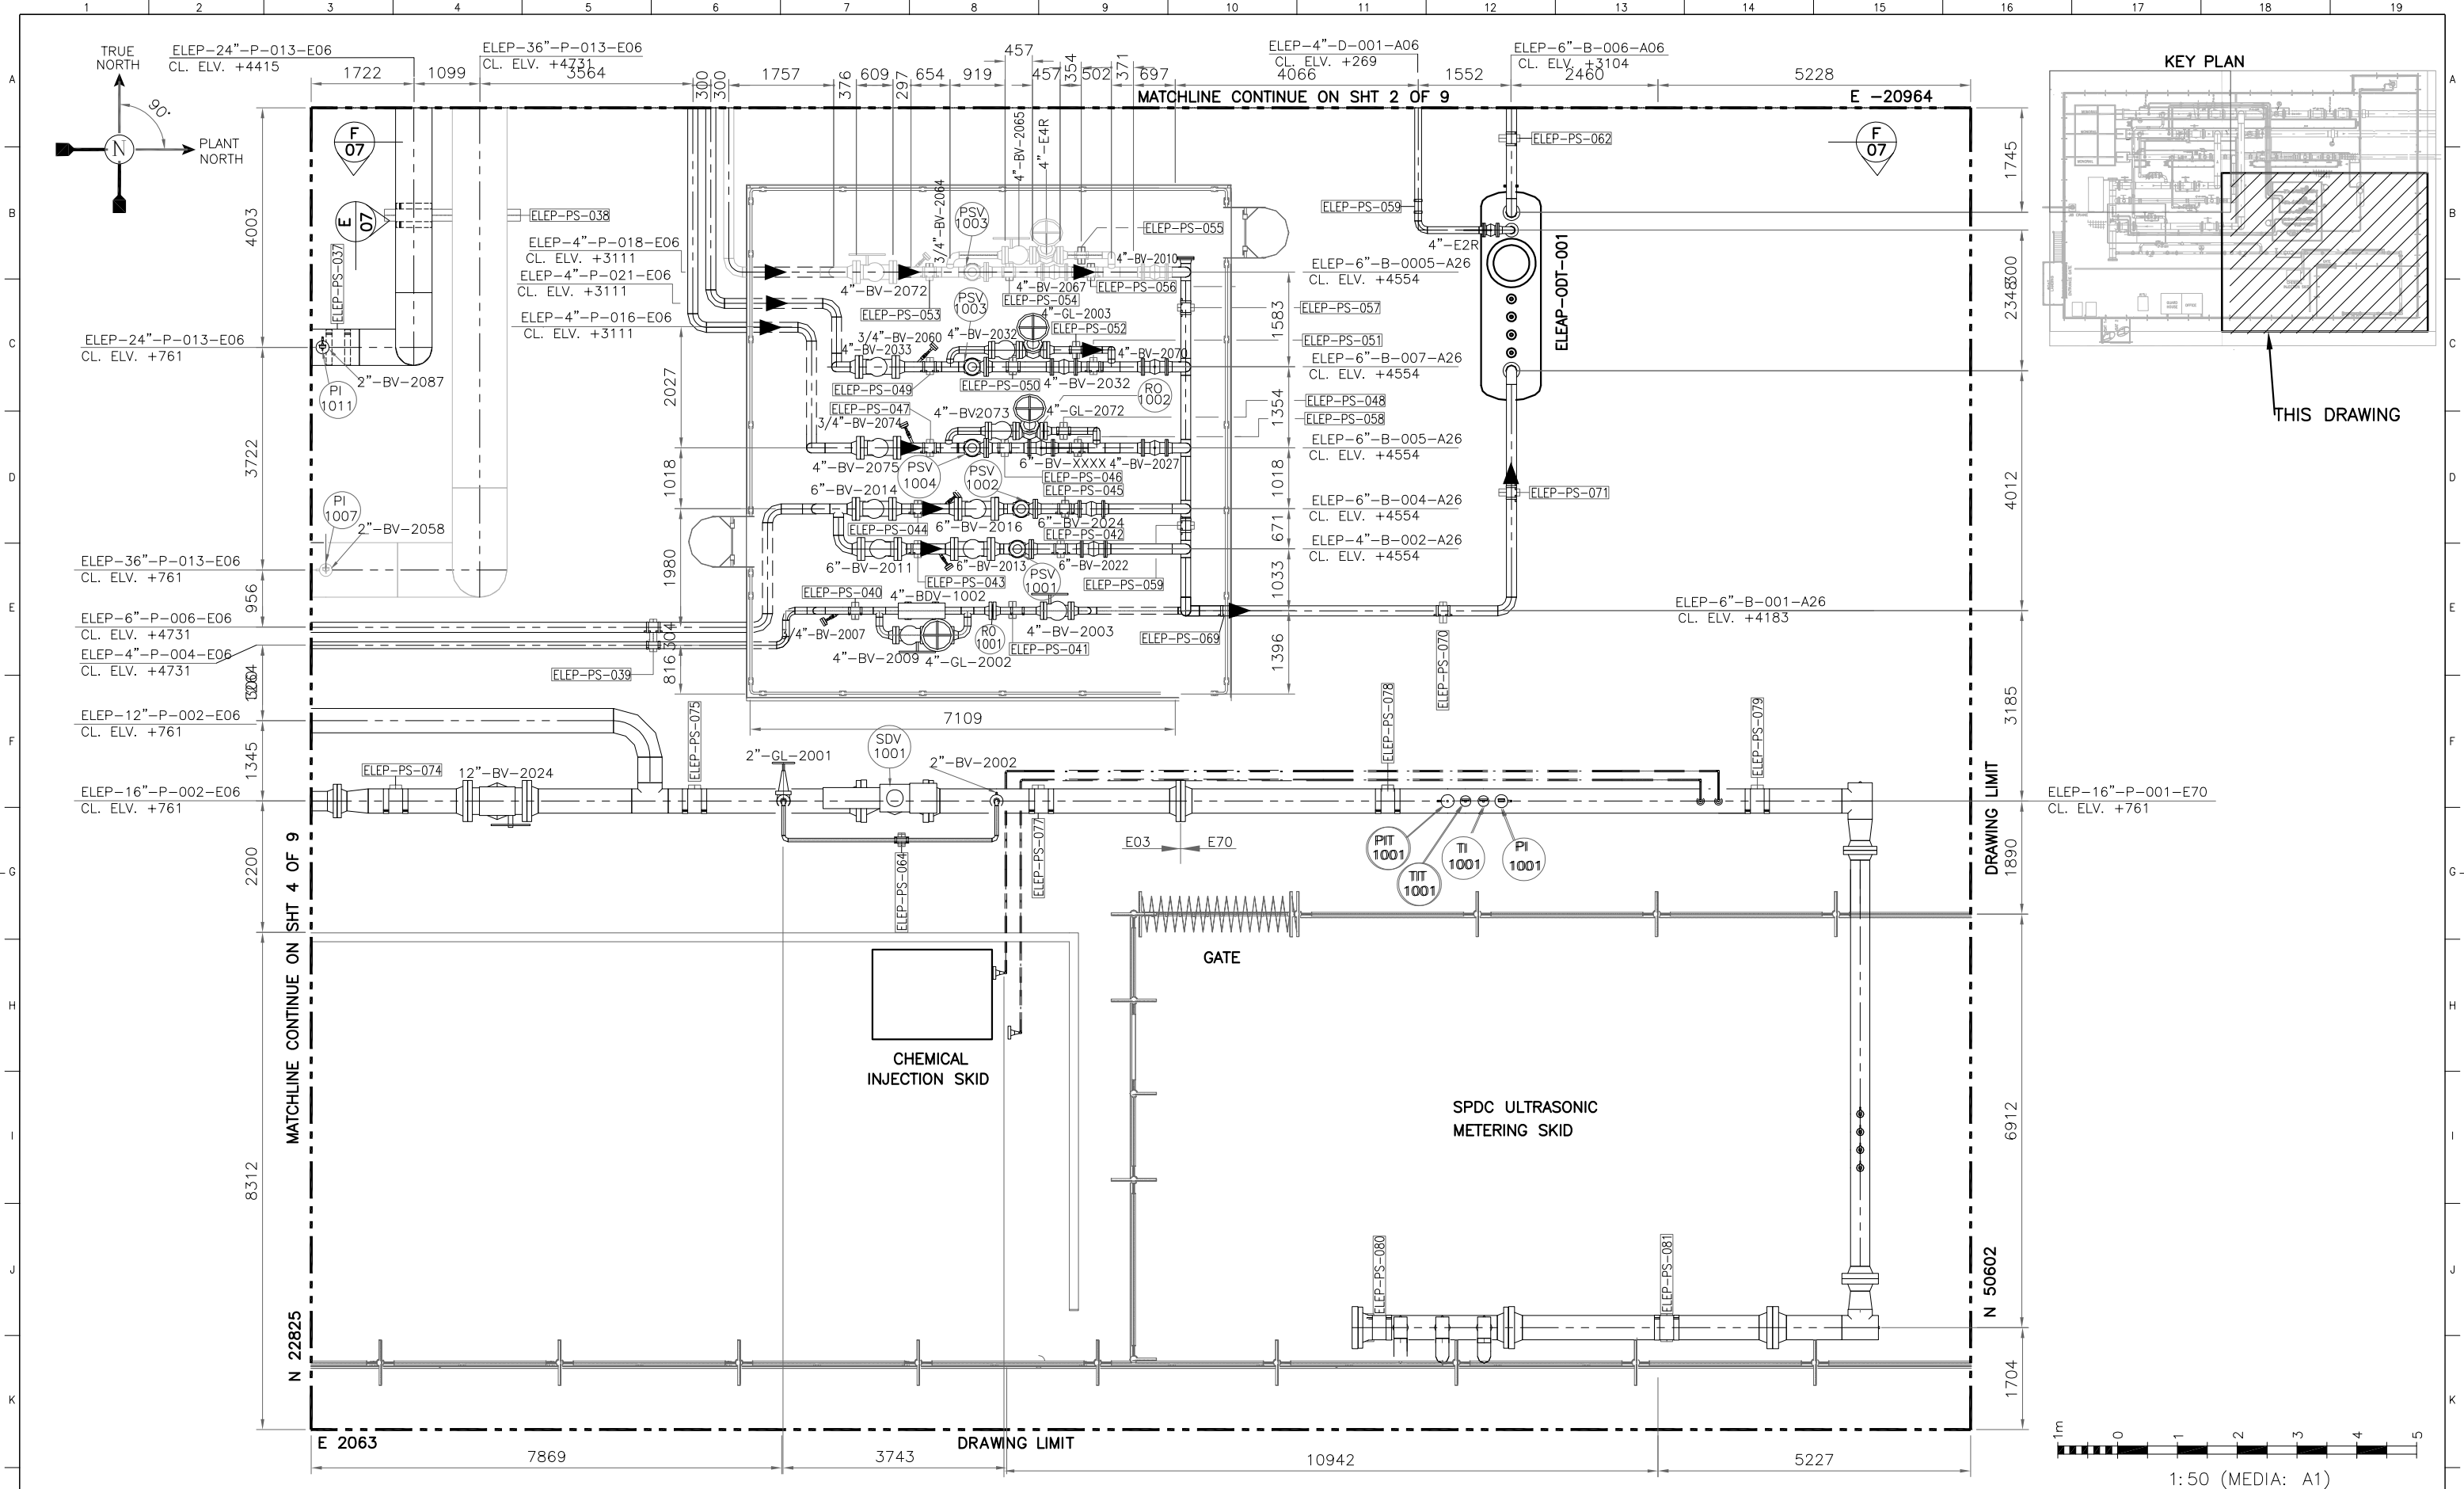


[illegible]


[illegible]

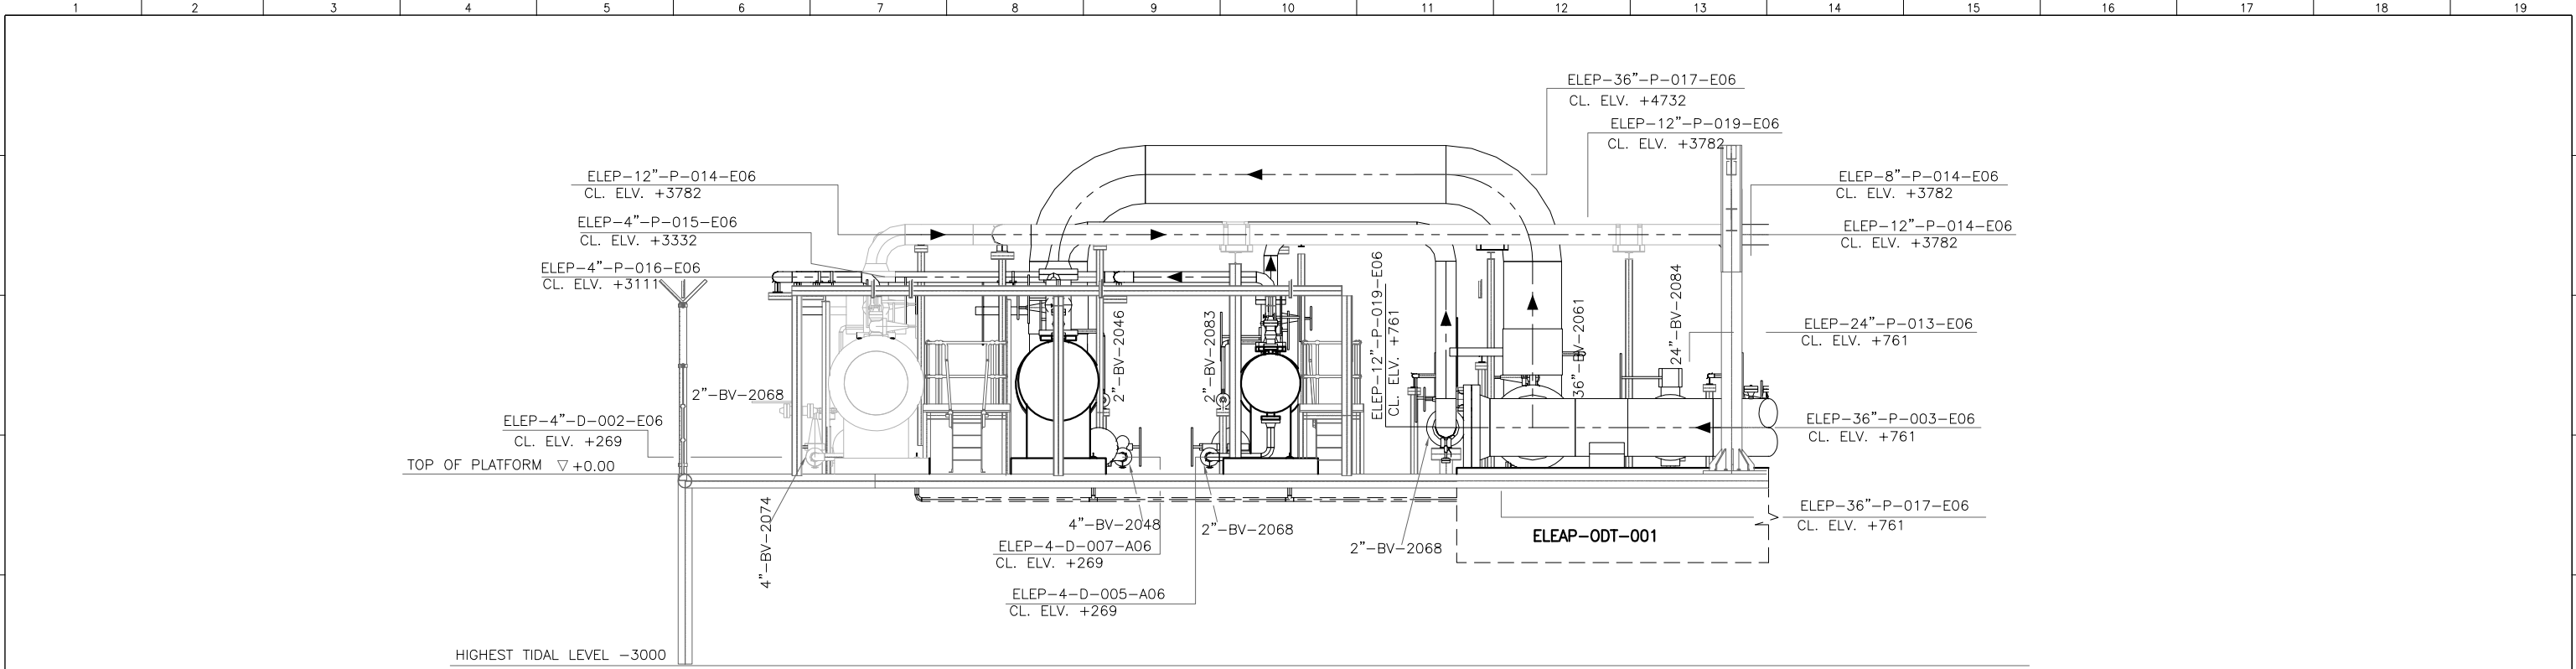


A
01 SECTION A-A

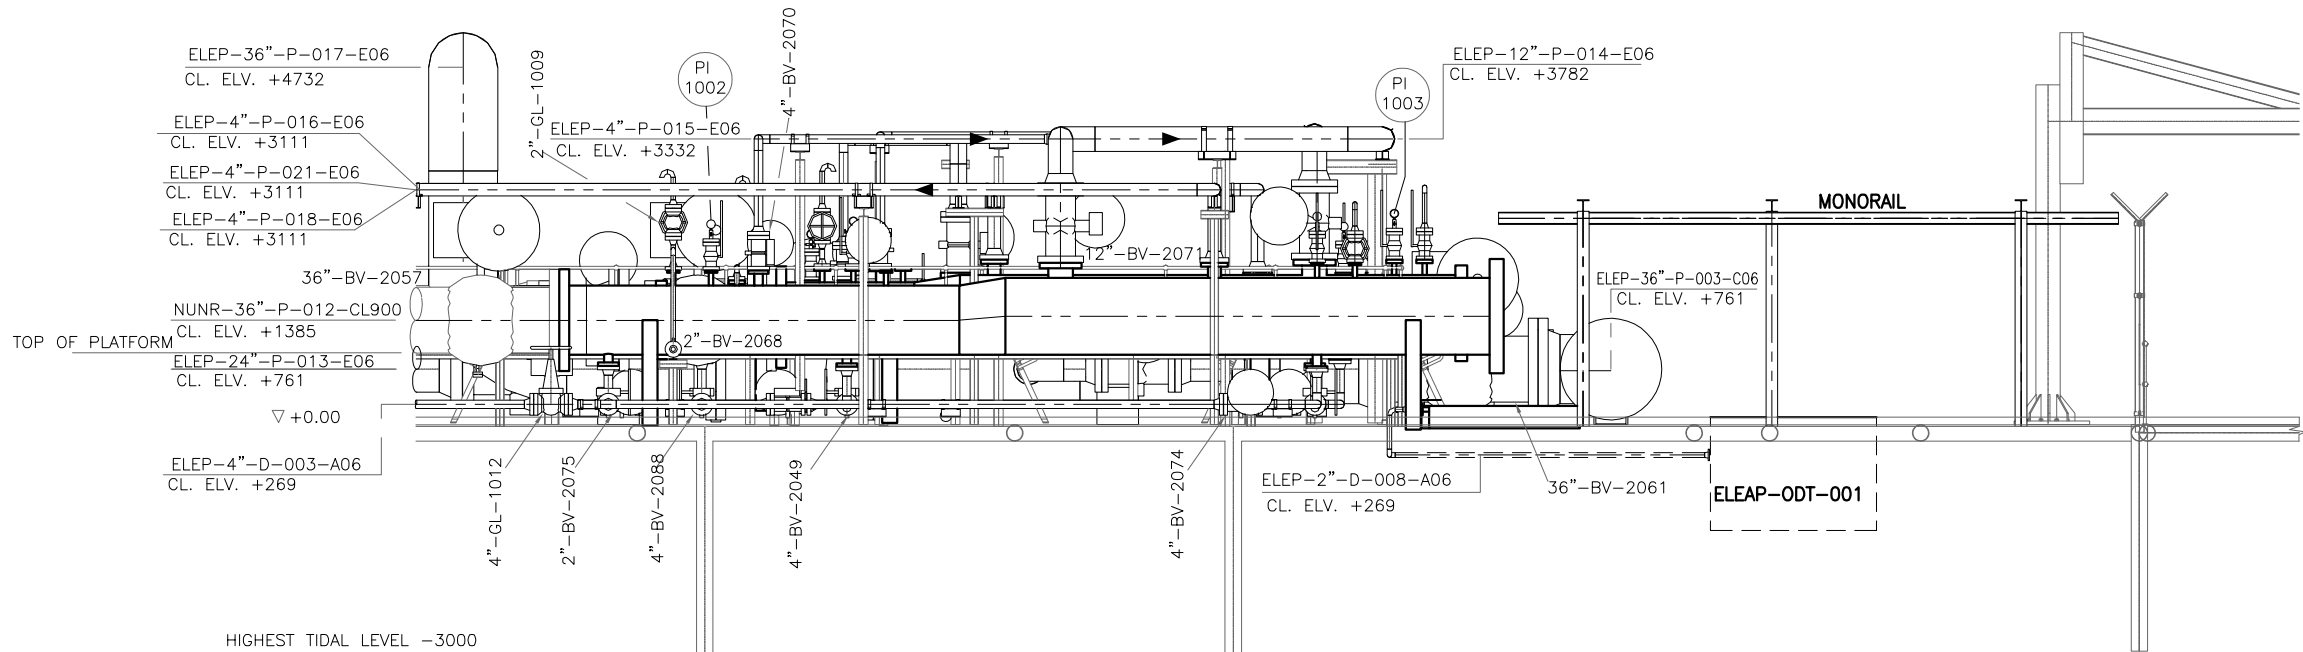


B
01 SECTION B-B

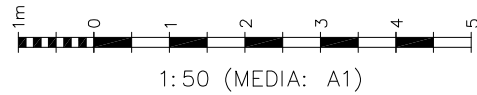


REFERENCE DRAWINGS	DRAWING No.	NOTES: 1. All dimensions are in mm unless otherwise stated. 2. Bottom of Platform is 3m from the highest tidal level. 3. The size of vent stack is assumed pending availability of date from process. 4. The Close drain tank and the open drain tank are located under of the platform deck with an access hatch. 5. Plant Reference Coordinate EAST:0.000, NORTH: 0.000	
--------------------	-------------	--	--	

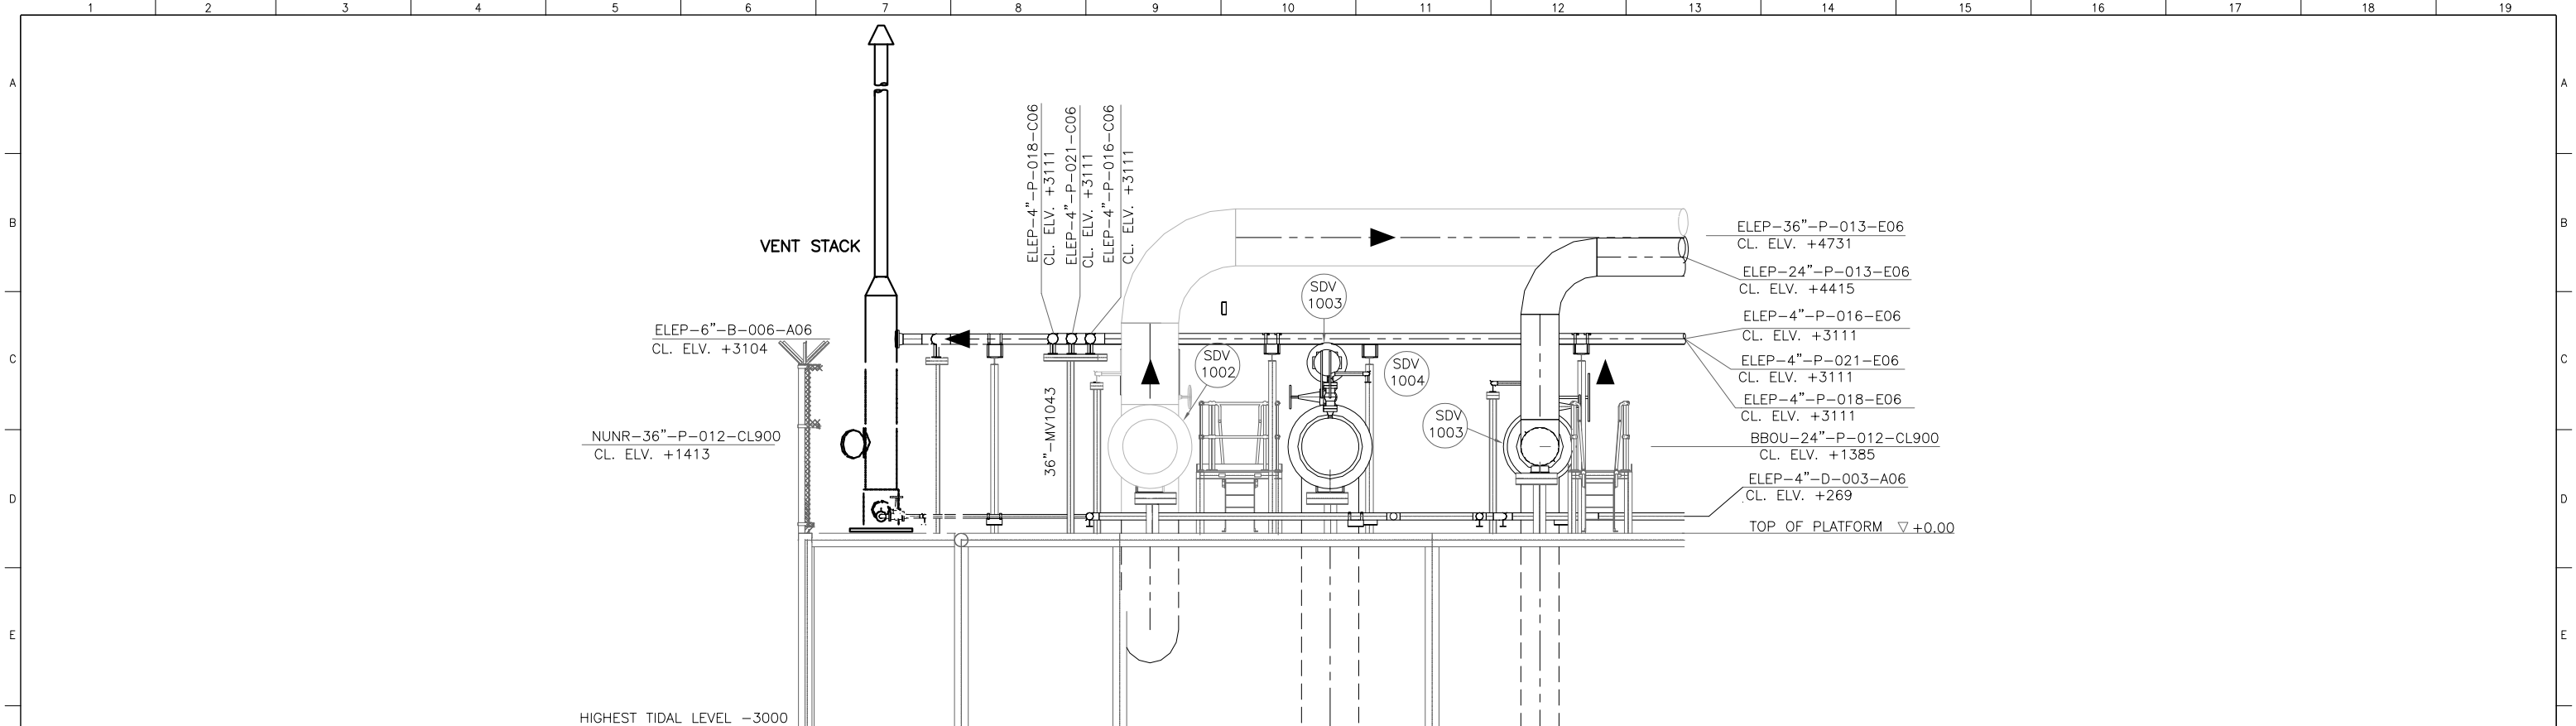

C
02 SECTION C-C

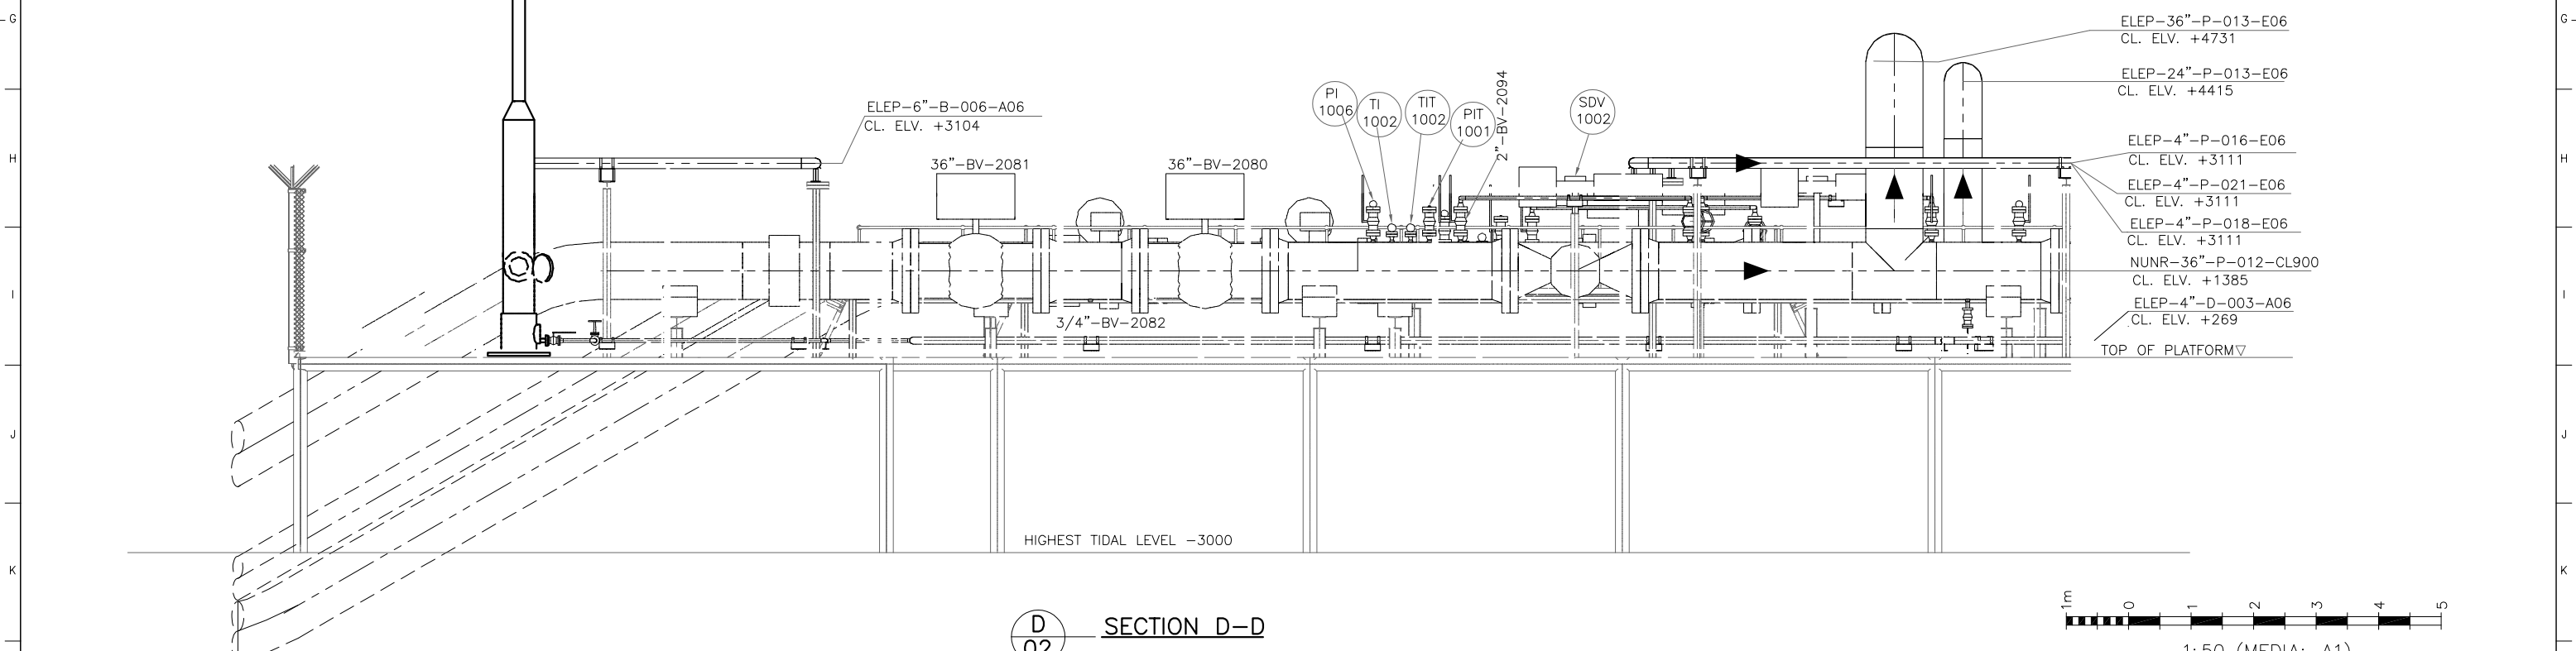

D
02 SECTION D-D

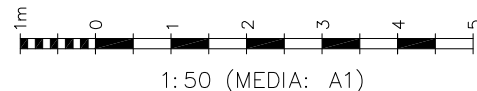

L	REFERENCE DRAWINGS		DRAWING No.		NOTES: 1. All dimensions are in mm unless otherwise stated. 2. Bottom of Platform is 3m from the highest tidal level. 3. The size of vent stack is assumed pending availability of date from process. 4. The Close drain tank and the open drain tank are located under of the platform deck with an access hatch. 5. Plant Reference Coordinate EAST:0.000, NORTH: 0.000							CONTRACTOR								BRASS FERTILIZER & PETROCHEMICAL COMPANY LIMITED																				
											 GAS PROCESSING AND METHANOL COMPLEX PROJECT FEED FOR GAS GATHERING PIPELINES 																													
													ENDORSEMENT				LOCATION ELEPA MANFOLD PLATFORM PIPING GENERAL ARRANGEMENT DRAWING – ELEPA																							
							RELEASED FOR		DESIGN ENGR.	BFPC TECH REP	SPDC TECH REP	DATE																												
							A01	ISSUED FOR APPROVAL		CAN	ENW	ADR	11/12/22					DRAWN: CAN		DATE: 11/12/2022		SHEET: 6 of 9																		
							R01	ISSUED FOR REVIEW		CAN	ENW	ADR	04/07/22					CHECKED: ENW		DRAWING No. EA-BFPCL-CPMC-CGPL-FEED-MPP-DWG-015		REV.																		
							REV			DRAWN	CHK	END	DATE					ENDORSED: ADR		PROJECT No. 11998A		01																		
							COPY RIGHT RESERVED																																	
M	
	1		2			3		4			5		6		7		8		9		10		11		12		13		14		15		16		17		18		19	

