




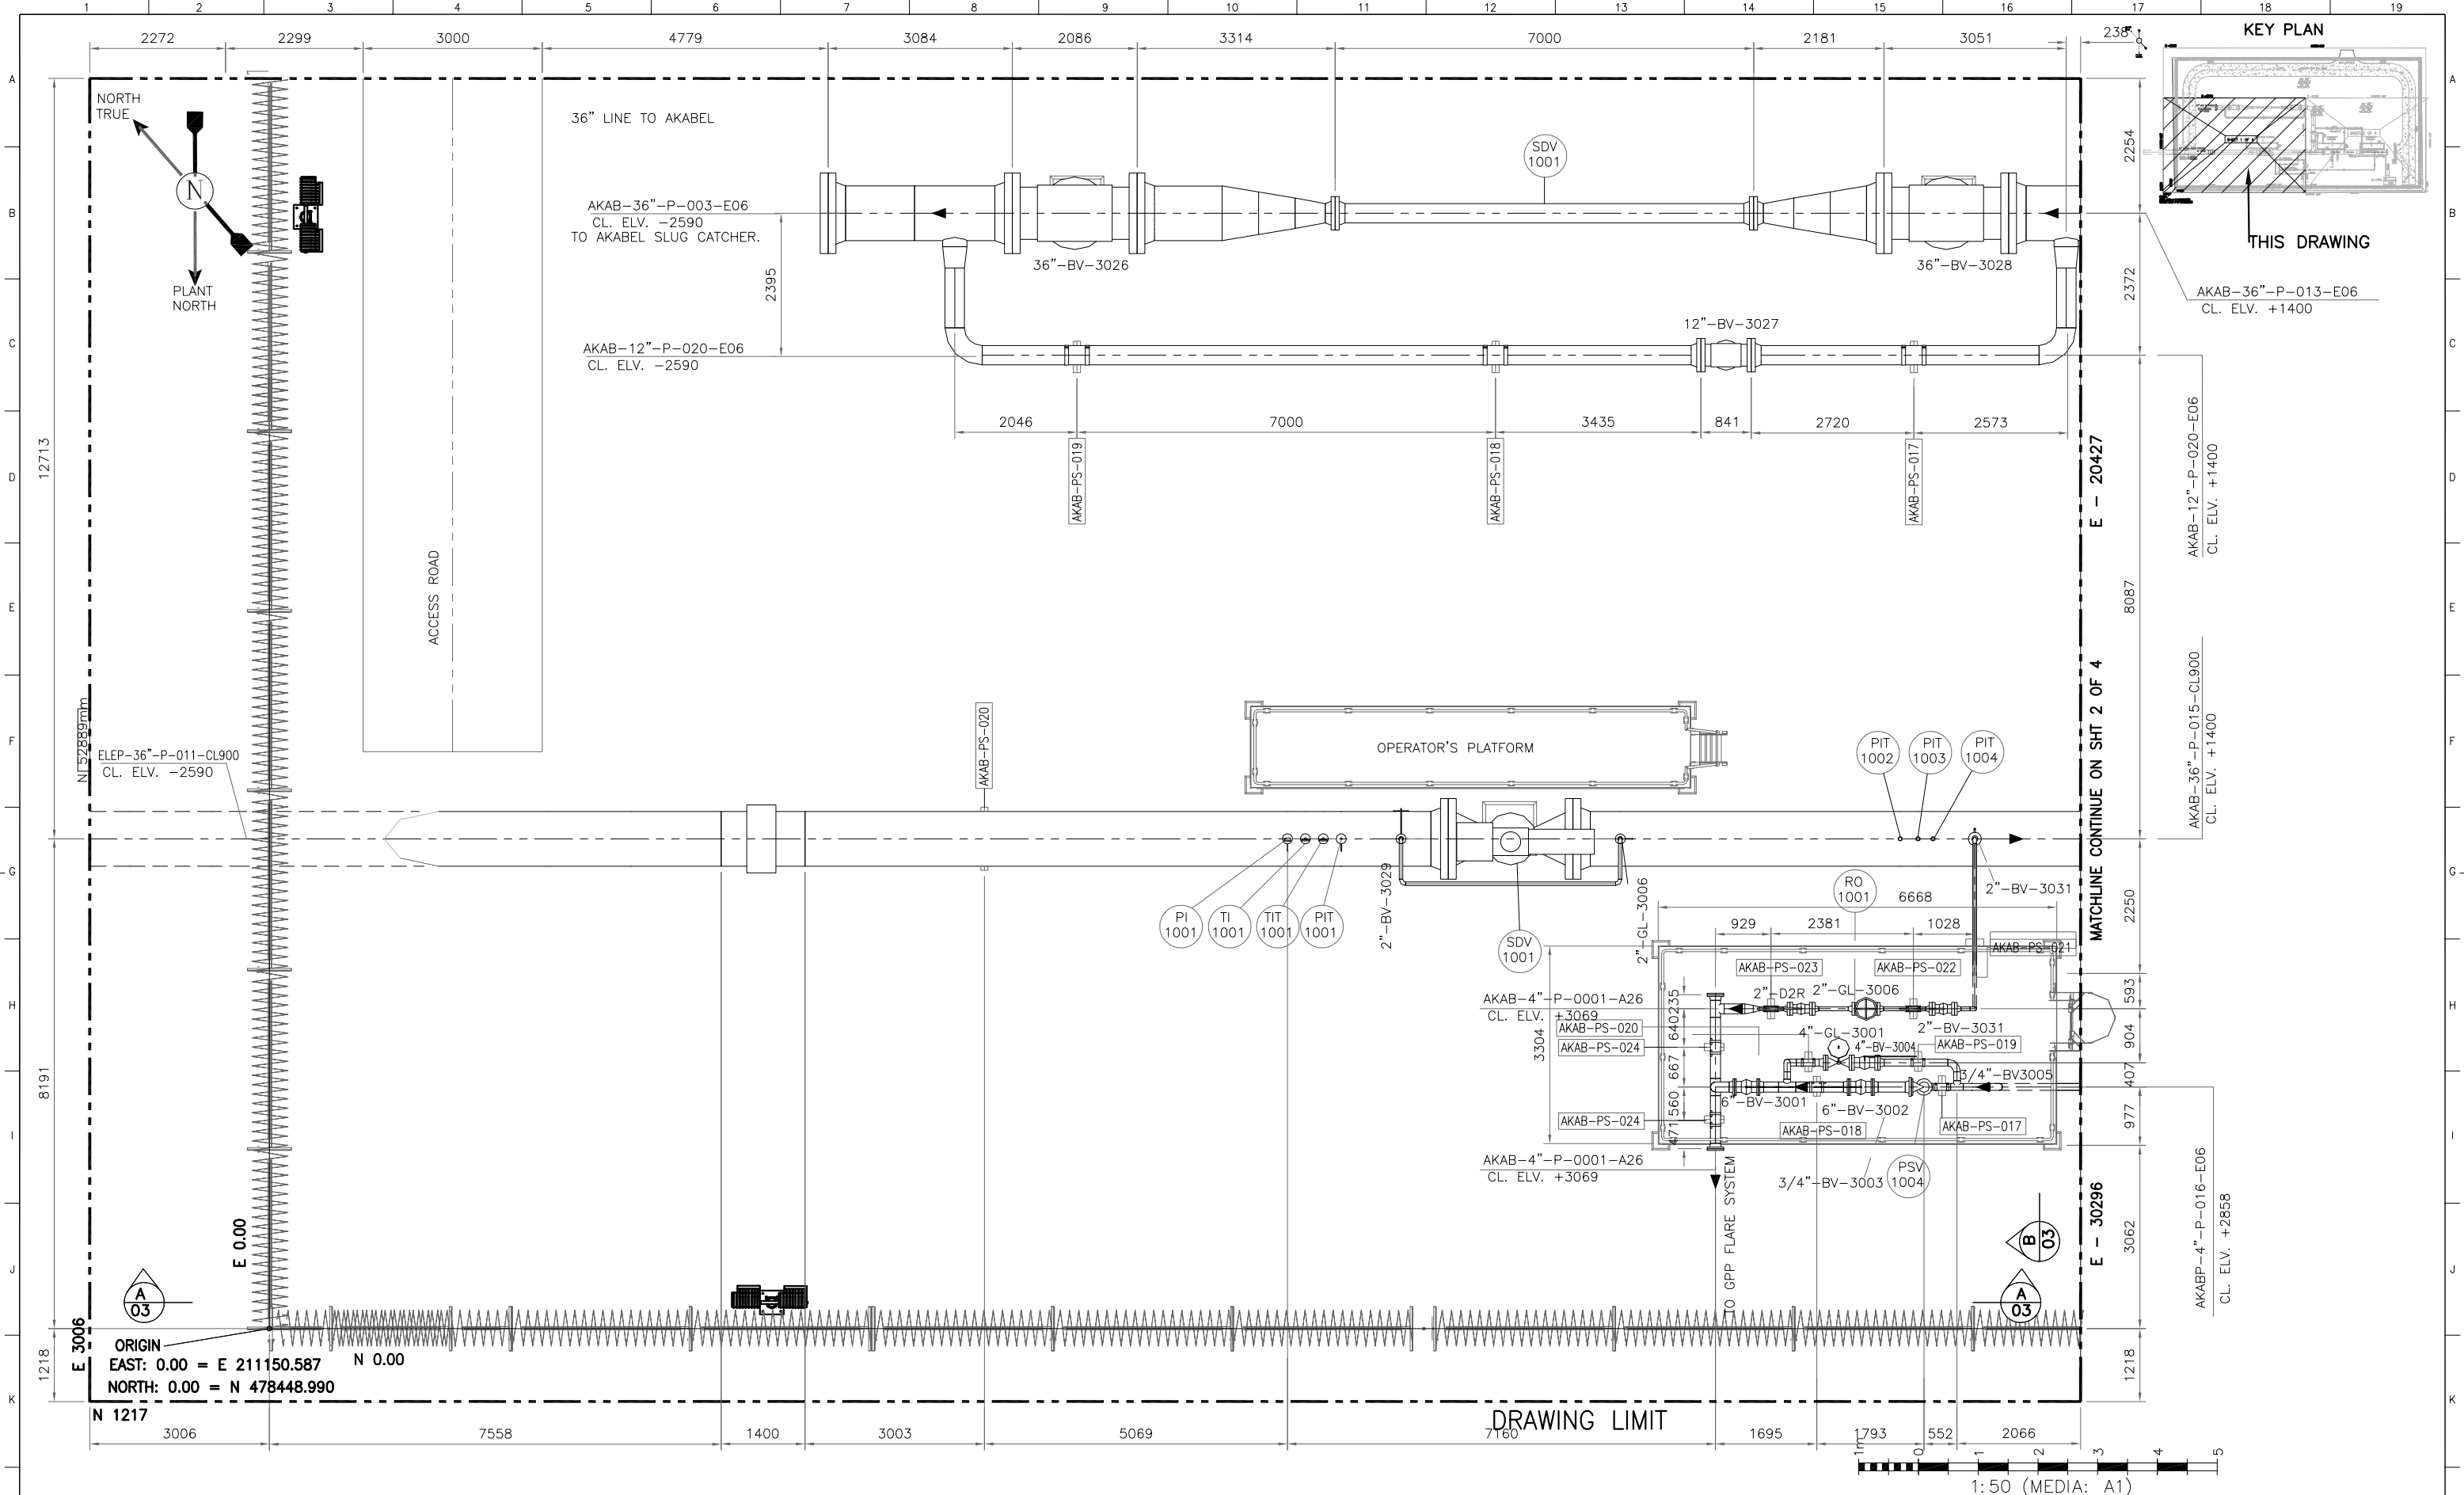


L	REFERENCE DRAWINGS	DRAWING No.	NOTES: 1. ALL DIMENSIONS ARE IN MM UNLESS OTHERWISE SPECIFIED 2. PLANT REFERENCE COORDINATE EAST: 0.00, NORTH 0.00 IS EQUIVALENT COORDINATE 211151mE, 478449mN UTM ZONE 32 WGS 84 DATUM.									CONTRACTOR			BRASS FERTILIZER & PETROCHEMICAL COMPANY LIMITED	
															GAS PROCESSING AND METHANOL COMPLEX PROJECT	
														LOCATION	
														AKABEL PIG RECEIVER	
														PIPING GENERAL ARRANGEMENT DRAWING – AKABEL	
M	

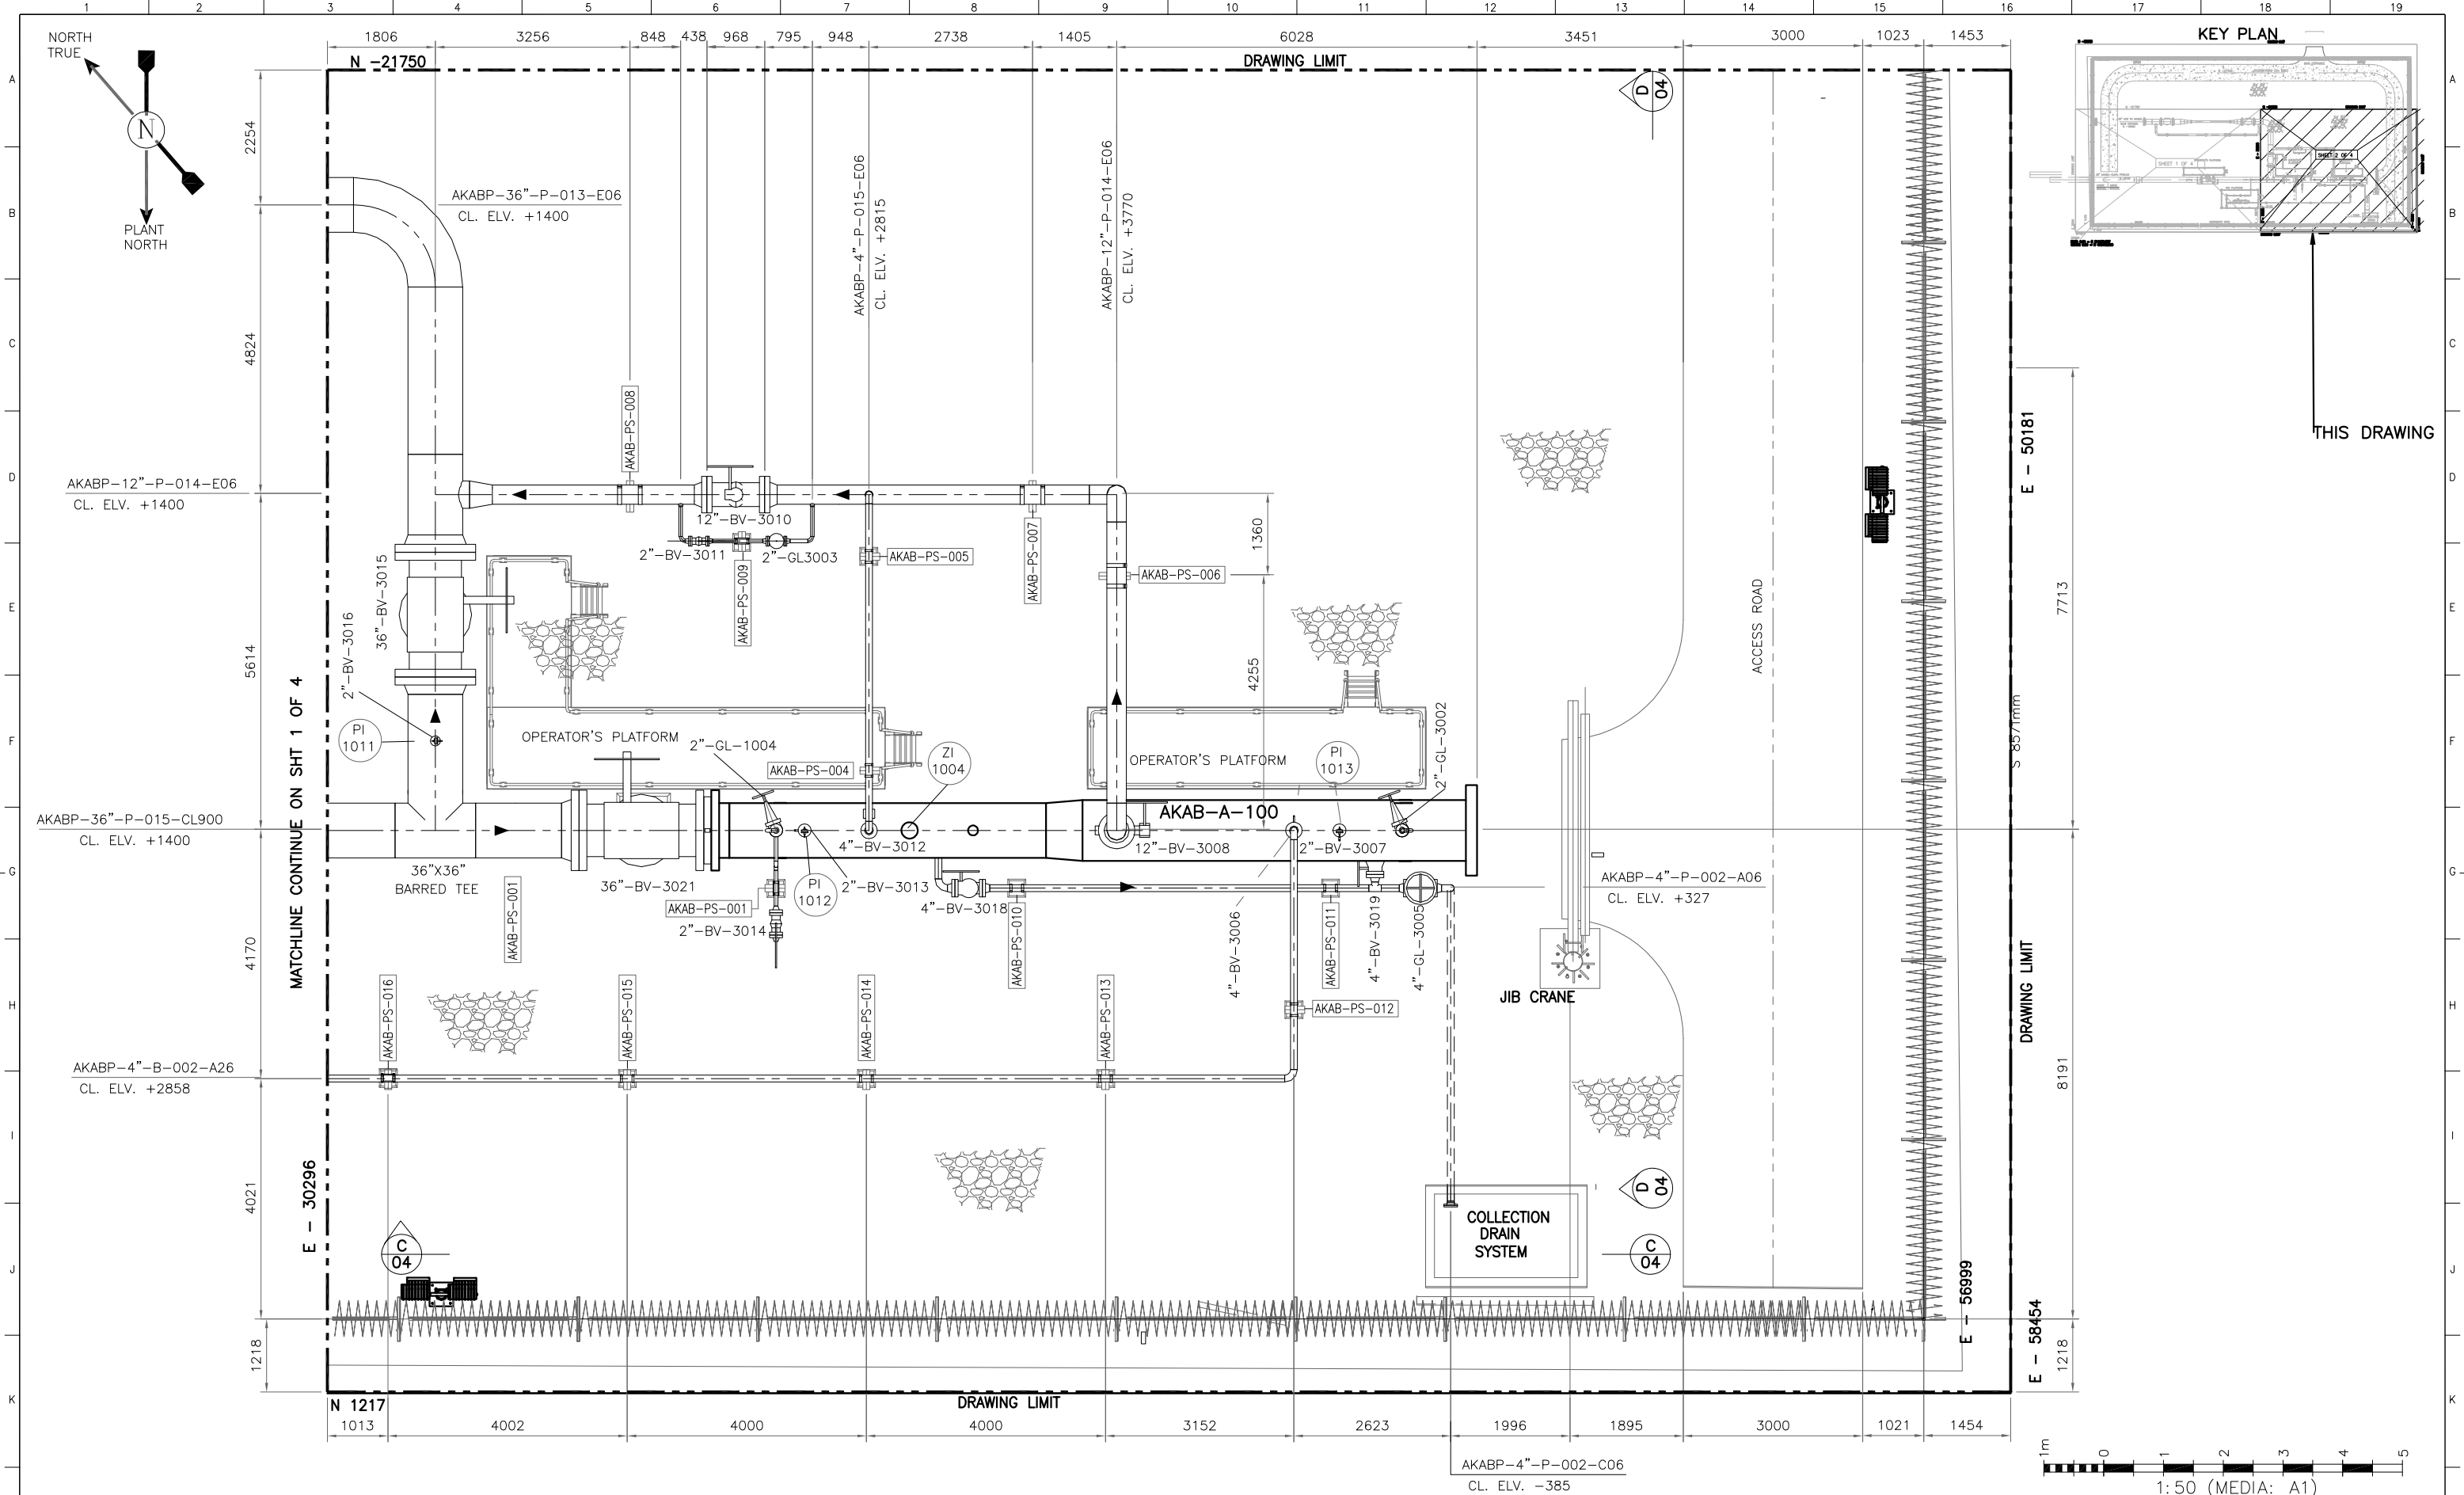


L	REFERENCE DRAWINGS	DRAWING No.	NOTES: 1. ALL DIMENSIONS ARE IN MM UNLESS OTHERWISE SPECIFIED 2. PLANT REFERENCE COORDINATE EAST: 0.00, NORTH 0.00 IS EQUIVALENT COORDINATE 211151mE, 478449mN UTM ZONE 32 WGS 84 DATUM.								CONTRACTOR			BRASS FERTILIZER & PETROCHEMICAL COMPANY LIMITED								
														GAS PROCESSING AND METHANOL COMPLEX PROJECT FEED FOR GAS GATHERING PIPELINES								
													ENDORSEMENT		LOCATION AKABEL PIG RECEIVER PIPING GENERAL ARRANGEMENT DRAWING – AKABEL							
													RELEASED FOR	DESIGN ENGR.	BFPC TECH REP	SPDC TECH REP	DATE					
M				A01	ISSUED FOR APPROVAL	CAN	ENW	ADR	22/12/22								DRAWN: CAN	DATE: 19/07/2022	SHEET: 2 of 4			
				R01	ISSUED FOR REVIEW	CAN	ENW	ADR	19/07/22								CHECKED: ENW	DRAWING No. EA-BFPCL-GPMC-CGPL-FEED-MPP-DWG-018	REV.			
				REV		DRAWN	CHK	END	DATE								ENDORSED: ADR	PROJECT No. 11998A		A01		
				COPY RIGHT RESERVED													APP'D DATE: –	PROJECT No. –				
	1	2	3	4	5	6	7	8	9	10	11	12	13	14	15	16	17	18	19			

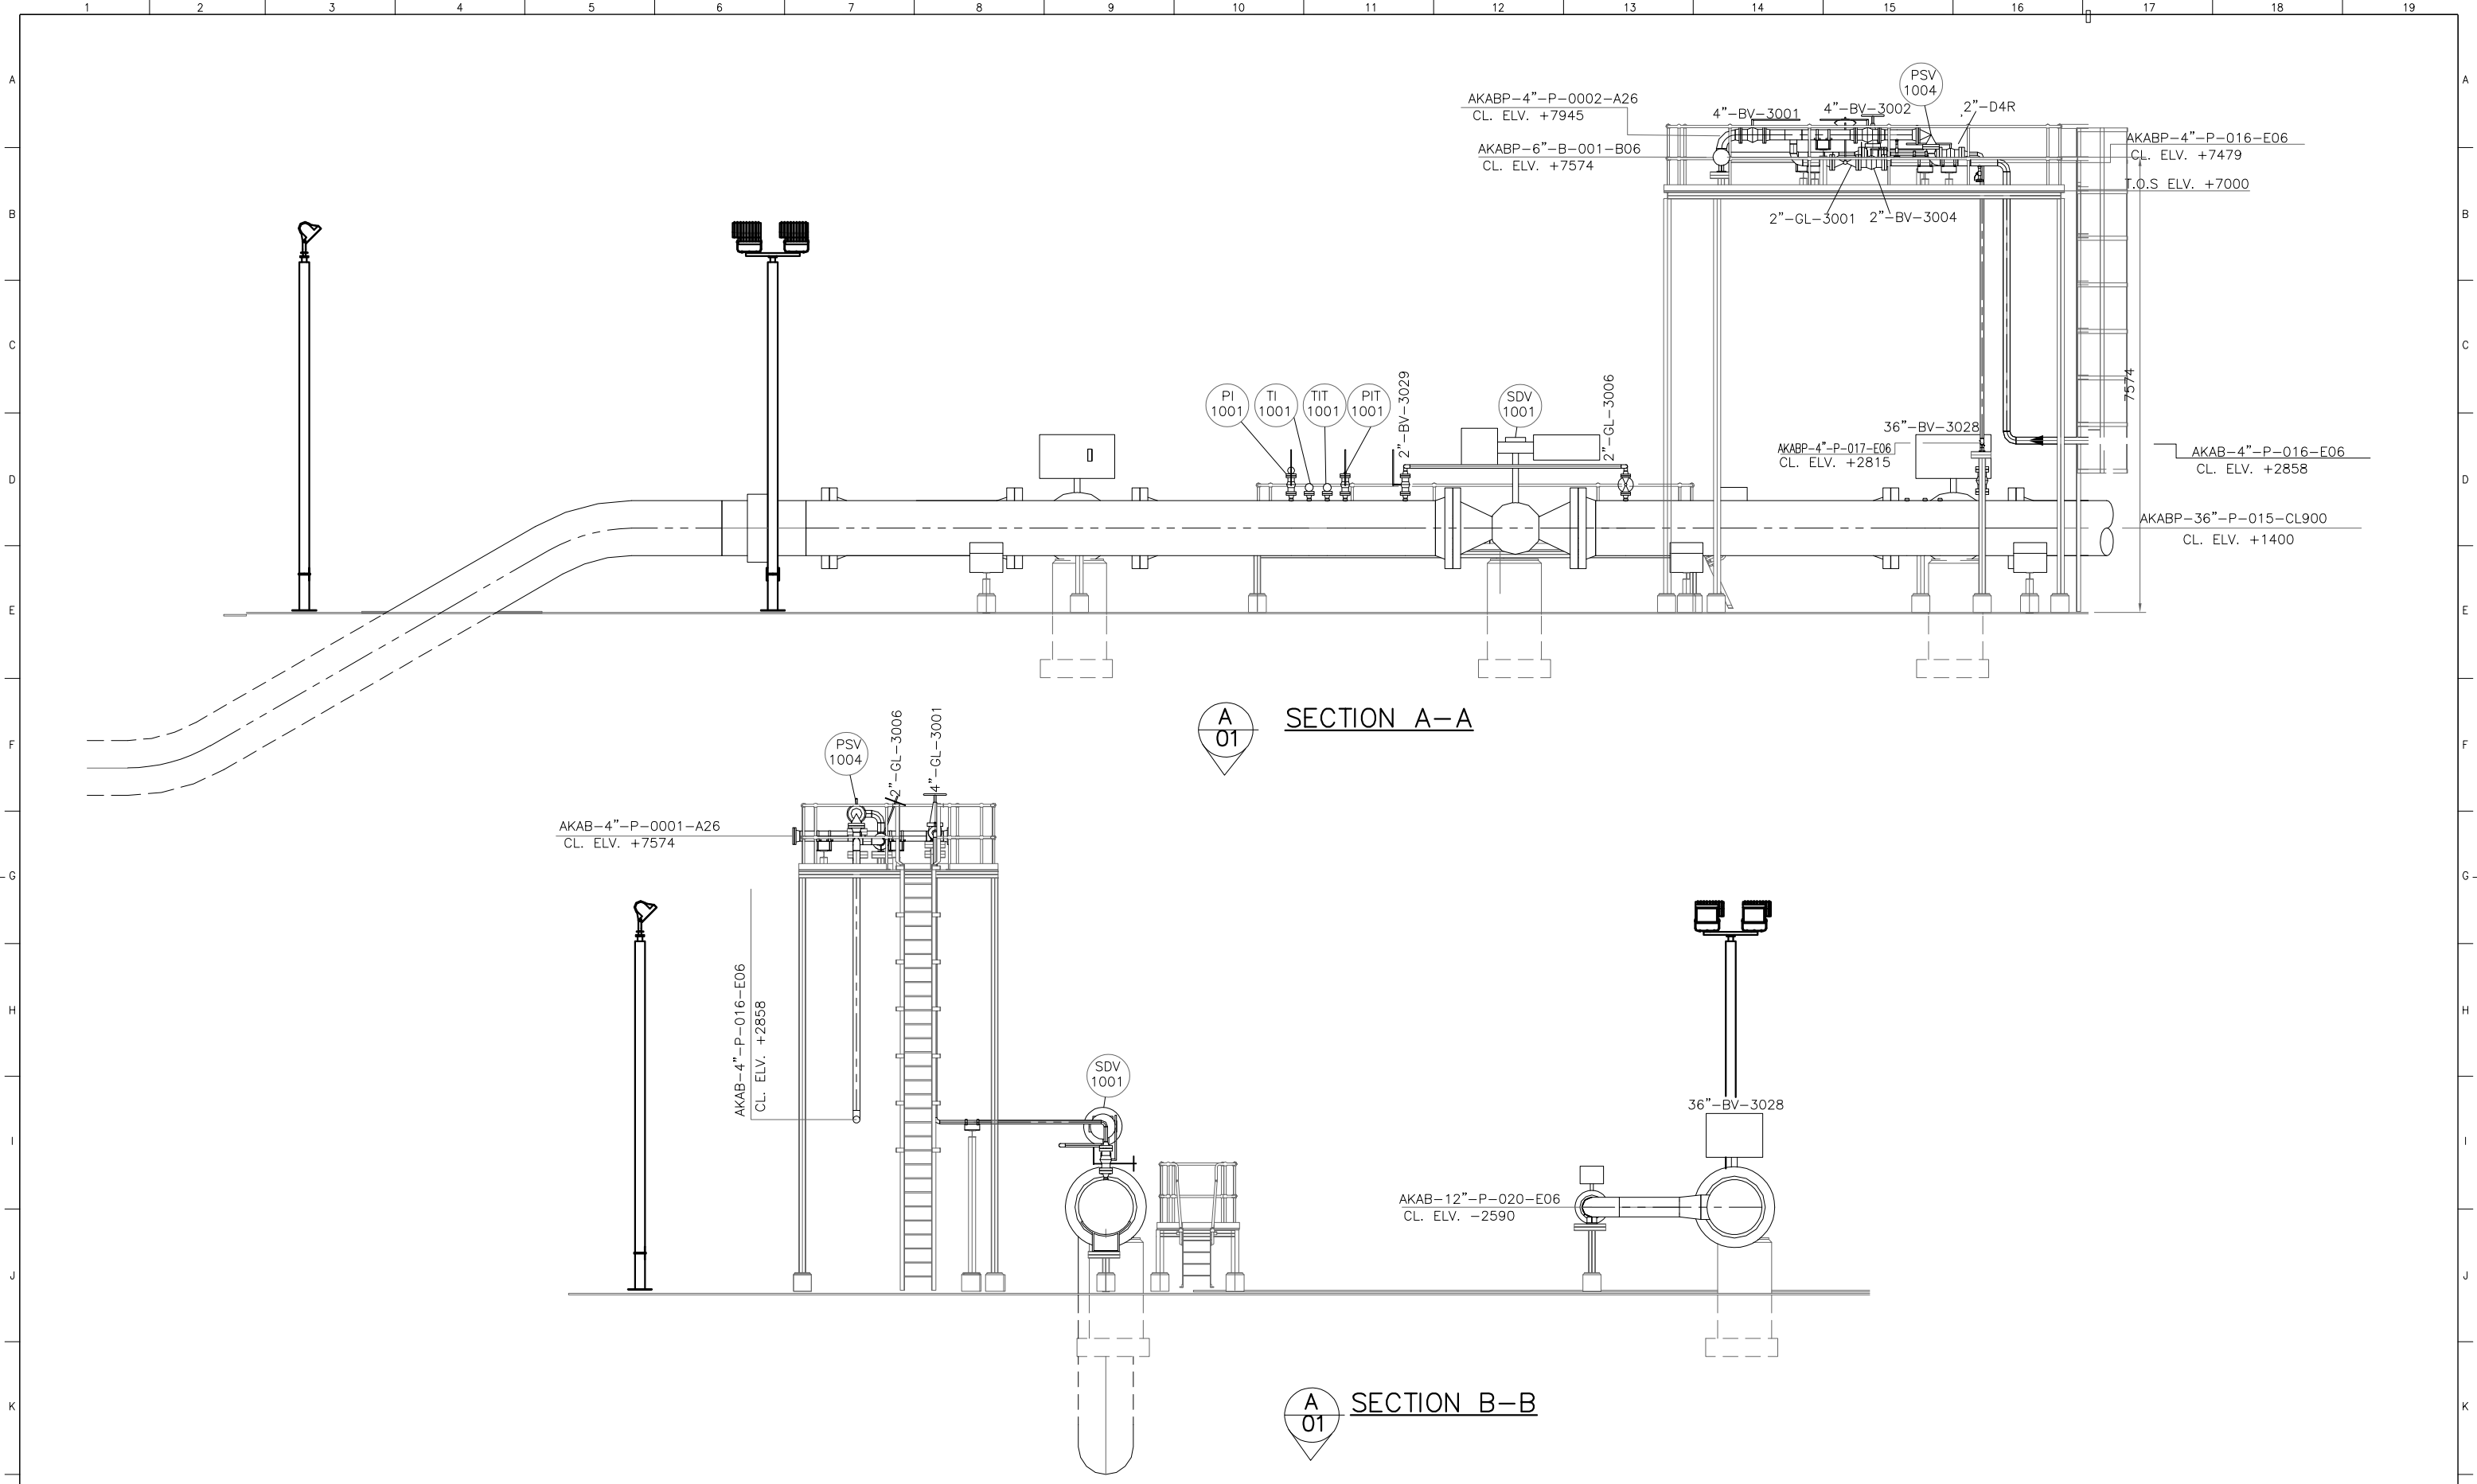

L	REFERENCE DRAWINGS		DRAWING No.		NOTES: 1. ALL DIMENSIONS ARE IN MM UNLESS OTHERWISE SPECIFIED 2. PLANT REFERENCE COORDINATE EAST: 0.00, NORTH 0.00 IS EQUIVALENT COORDINATE 211151mE, 478449mN UTM ZONE 32 WGS 84 DATUM.							CONTRACTOR				BRASS FERTILIZER & PETROCHEMICAL COMPANY LIMITED						
																 GAS PROCESSING AND METHANOL COMPLEX PROJECT FEED FOR GAS GATHERING PIPELINES 						
												ENDORSEMENT				LOCATION						
												RELEASED FOR				AKABEL PIG RECEIVER						
												DESIGN ENGR.				PIPING GENERAL ARRANGEMENT DRAWING — AKABEL						
												BFPC TECH REP				DATE						
												SPDC TECH REP										
M						A01	ISSUED FOR APPROVAL	CAN	ENW	ADR	22/12/22					DRAWN: CAN		DATE: 19/07/2022		SHEET: 3 of 4		
						R01	ISSUED FOR REVIEW	CAN	ENW	ADR	19/07/22					CHECKED: ENW		DRAWING No. EA-BFPCL-GPMC-CGPL-FEED-MPP-DWG-018		REV.		
						REV		DRAWN	CHK	END	DATE					ENDORSED: ADR		PROJECT No. 11998A		A01		
						COPY RIGHT RESERVED											APP'D DATE: —		PROJECT No. —			
1		2		3	4	5	6	7	8	9	10	11	12	13	14	15	16	17	18	19		

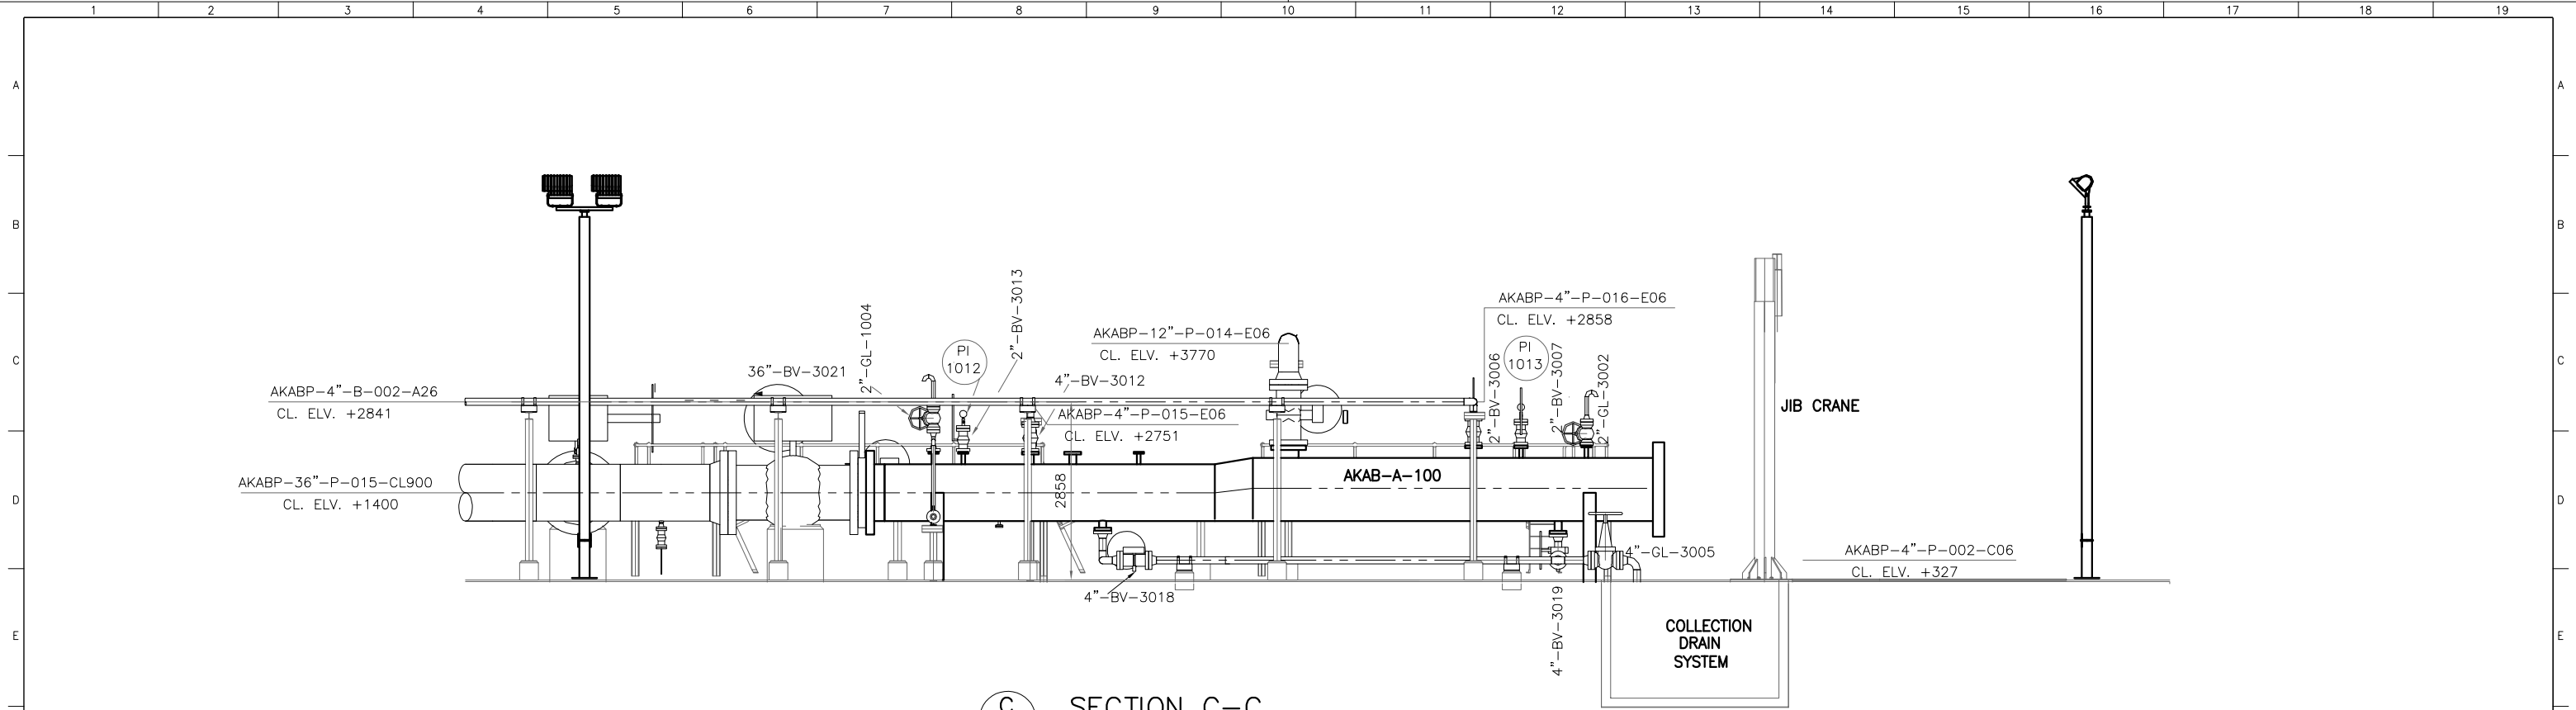

C
02 SECTION C-C

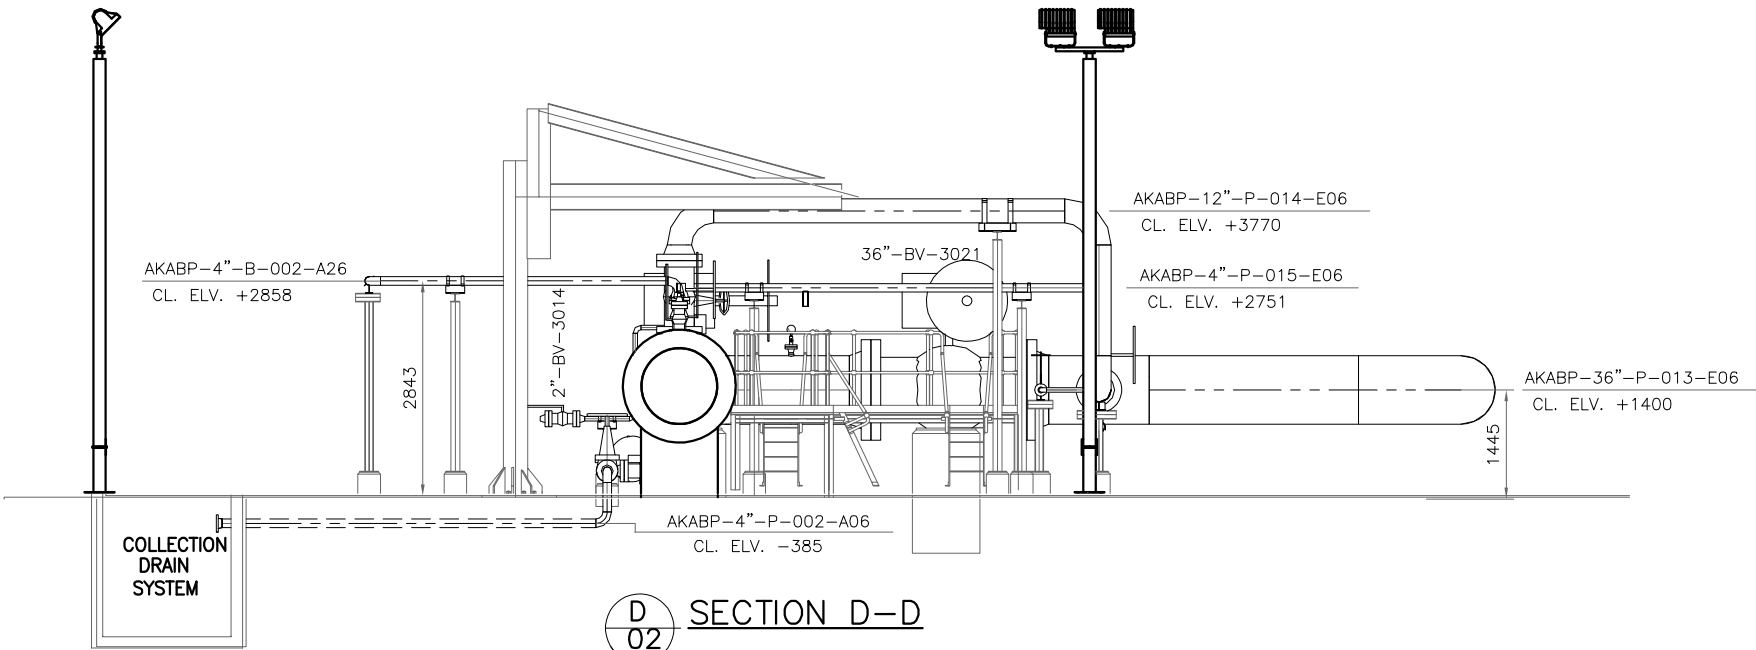

D
02 SECTION D-D

REFERENCE DRAWINGS	DRAWING No.	NOTES: 1. ALL DIMENSIONS ARE IN MM UNLESS OTHERWISE SPECIFIED 2. PLANT REFERENCE COORDINATE EAST: 0.00, NORTH 0.00 IS EQUIVALENT COORDINATE 211151mE, 478449mN UTM ZONE 32 WGS 84 DATUM.	
--------------------	-------------	--	--	