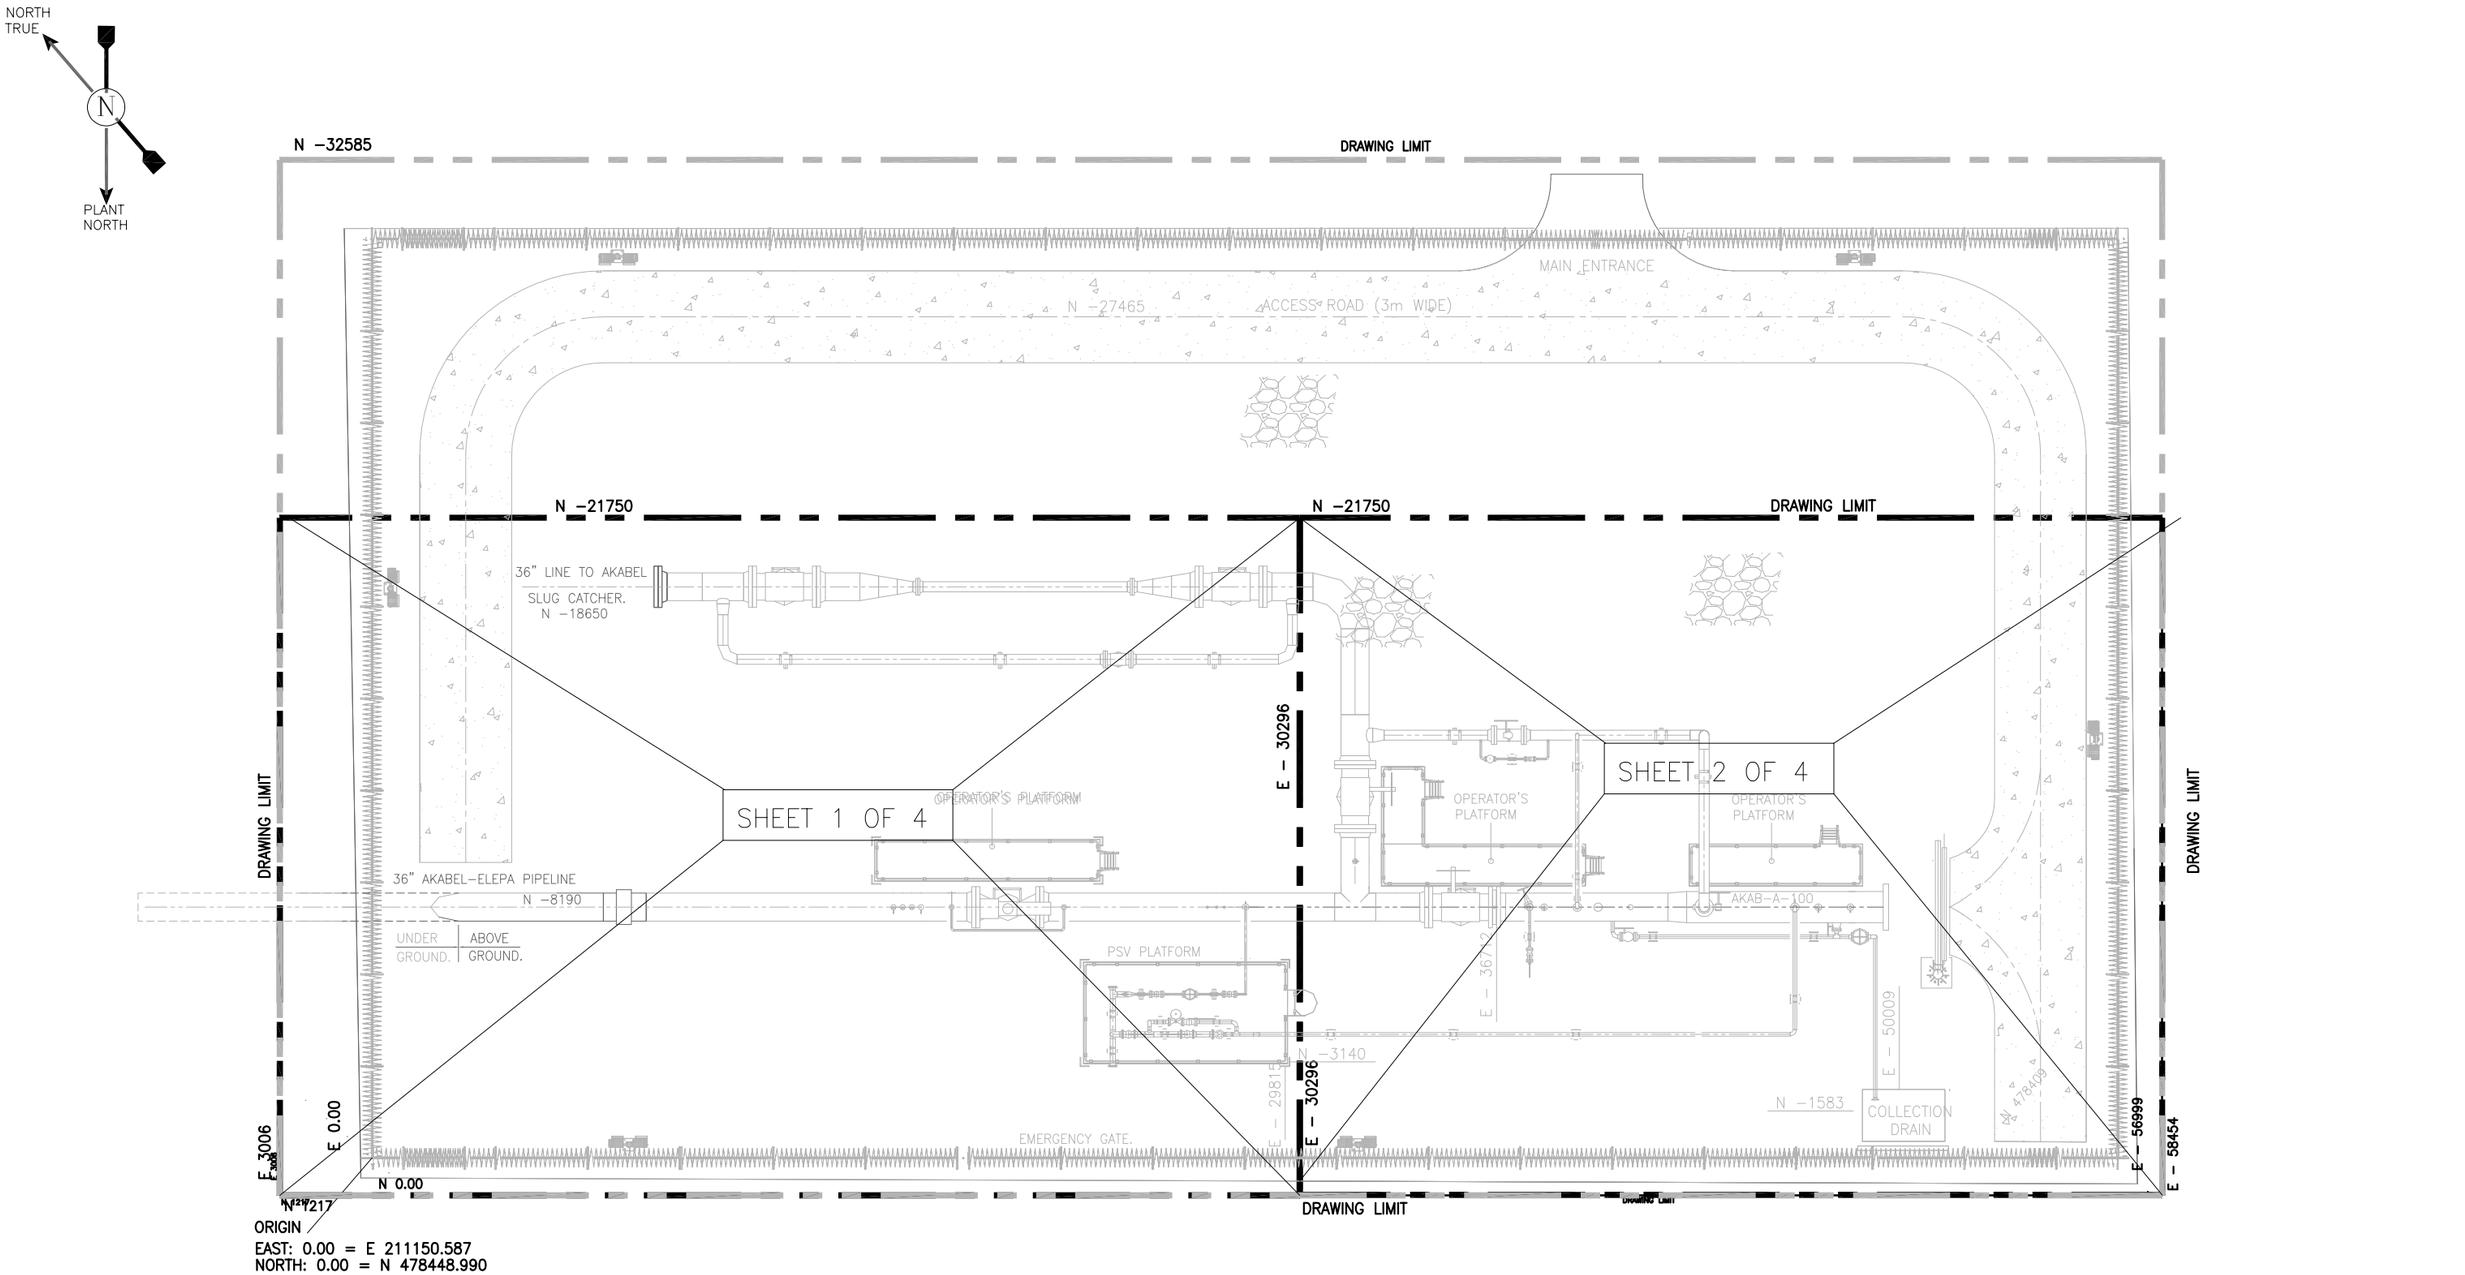

1m 0 1 2 3 4 5

1:100 (MEDIA: A1)

REFERENCE DRAWINGS	DRAWING No.

NOTES:
1. ALL DIMENSIONS ARE IN MM UNLESS OTHERWISE SPECIFIED
2. PLANT REFERENCE COORDINATE EAST: 0.00, NORTH 0.00 IS EQUIVALENT COORDINATE 211151mE, 478449mN UTM ZONE 32 WGS 84 DATUM.

REV					
A01	ISSUED FOR APPROVAL	CAN	ENW	ADR	14/01/23
R01	ISSUED FOR REVIEW	CAN	ENW	ADR	19/06/22
REV		DRAWN	CHK	END	DATE

COPY RIGHT RESERVED

CONTRACTOR epic ATLANTIC

ENDORSEMENT				
RELEASED FOR	DESIGN ENGR.	BFPC TECH REP	SPDC TECH REP	DATE

BRASS FERTILIZER & PETROCHEMICAL COMPANY LIMITED

brass fertilizer

GAS PROCESSING AND METHANOL COMPLEX PROJECT
FEED FOR GAS GATHERING PIPELINES

LOCATION
AKABEL PIG RECEIVER
KEY PLAN – AKABEL

DRAWN: CAN	DATE: 19/06/2022	SHEET: 1 of 1	
CHECKED: ENW	DRAWING No. EA-BFPCL-GPMC-GGPL-FEED-MPP-DWG-019	REV.	A01
ENDORSED: ADR	PROJECT No. 11998A		
APP'D DATE: –	PROJECT No. –		