


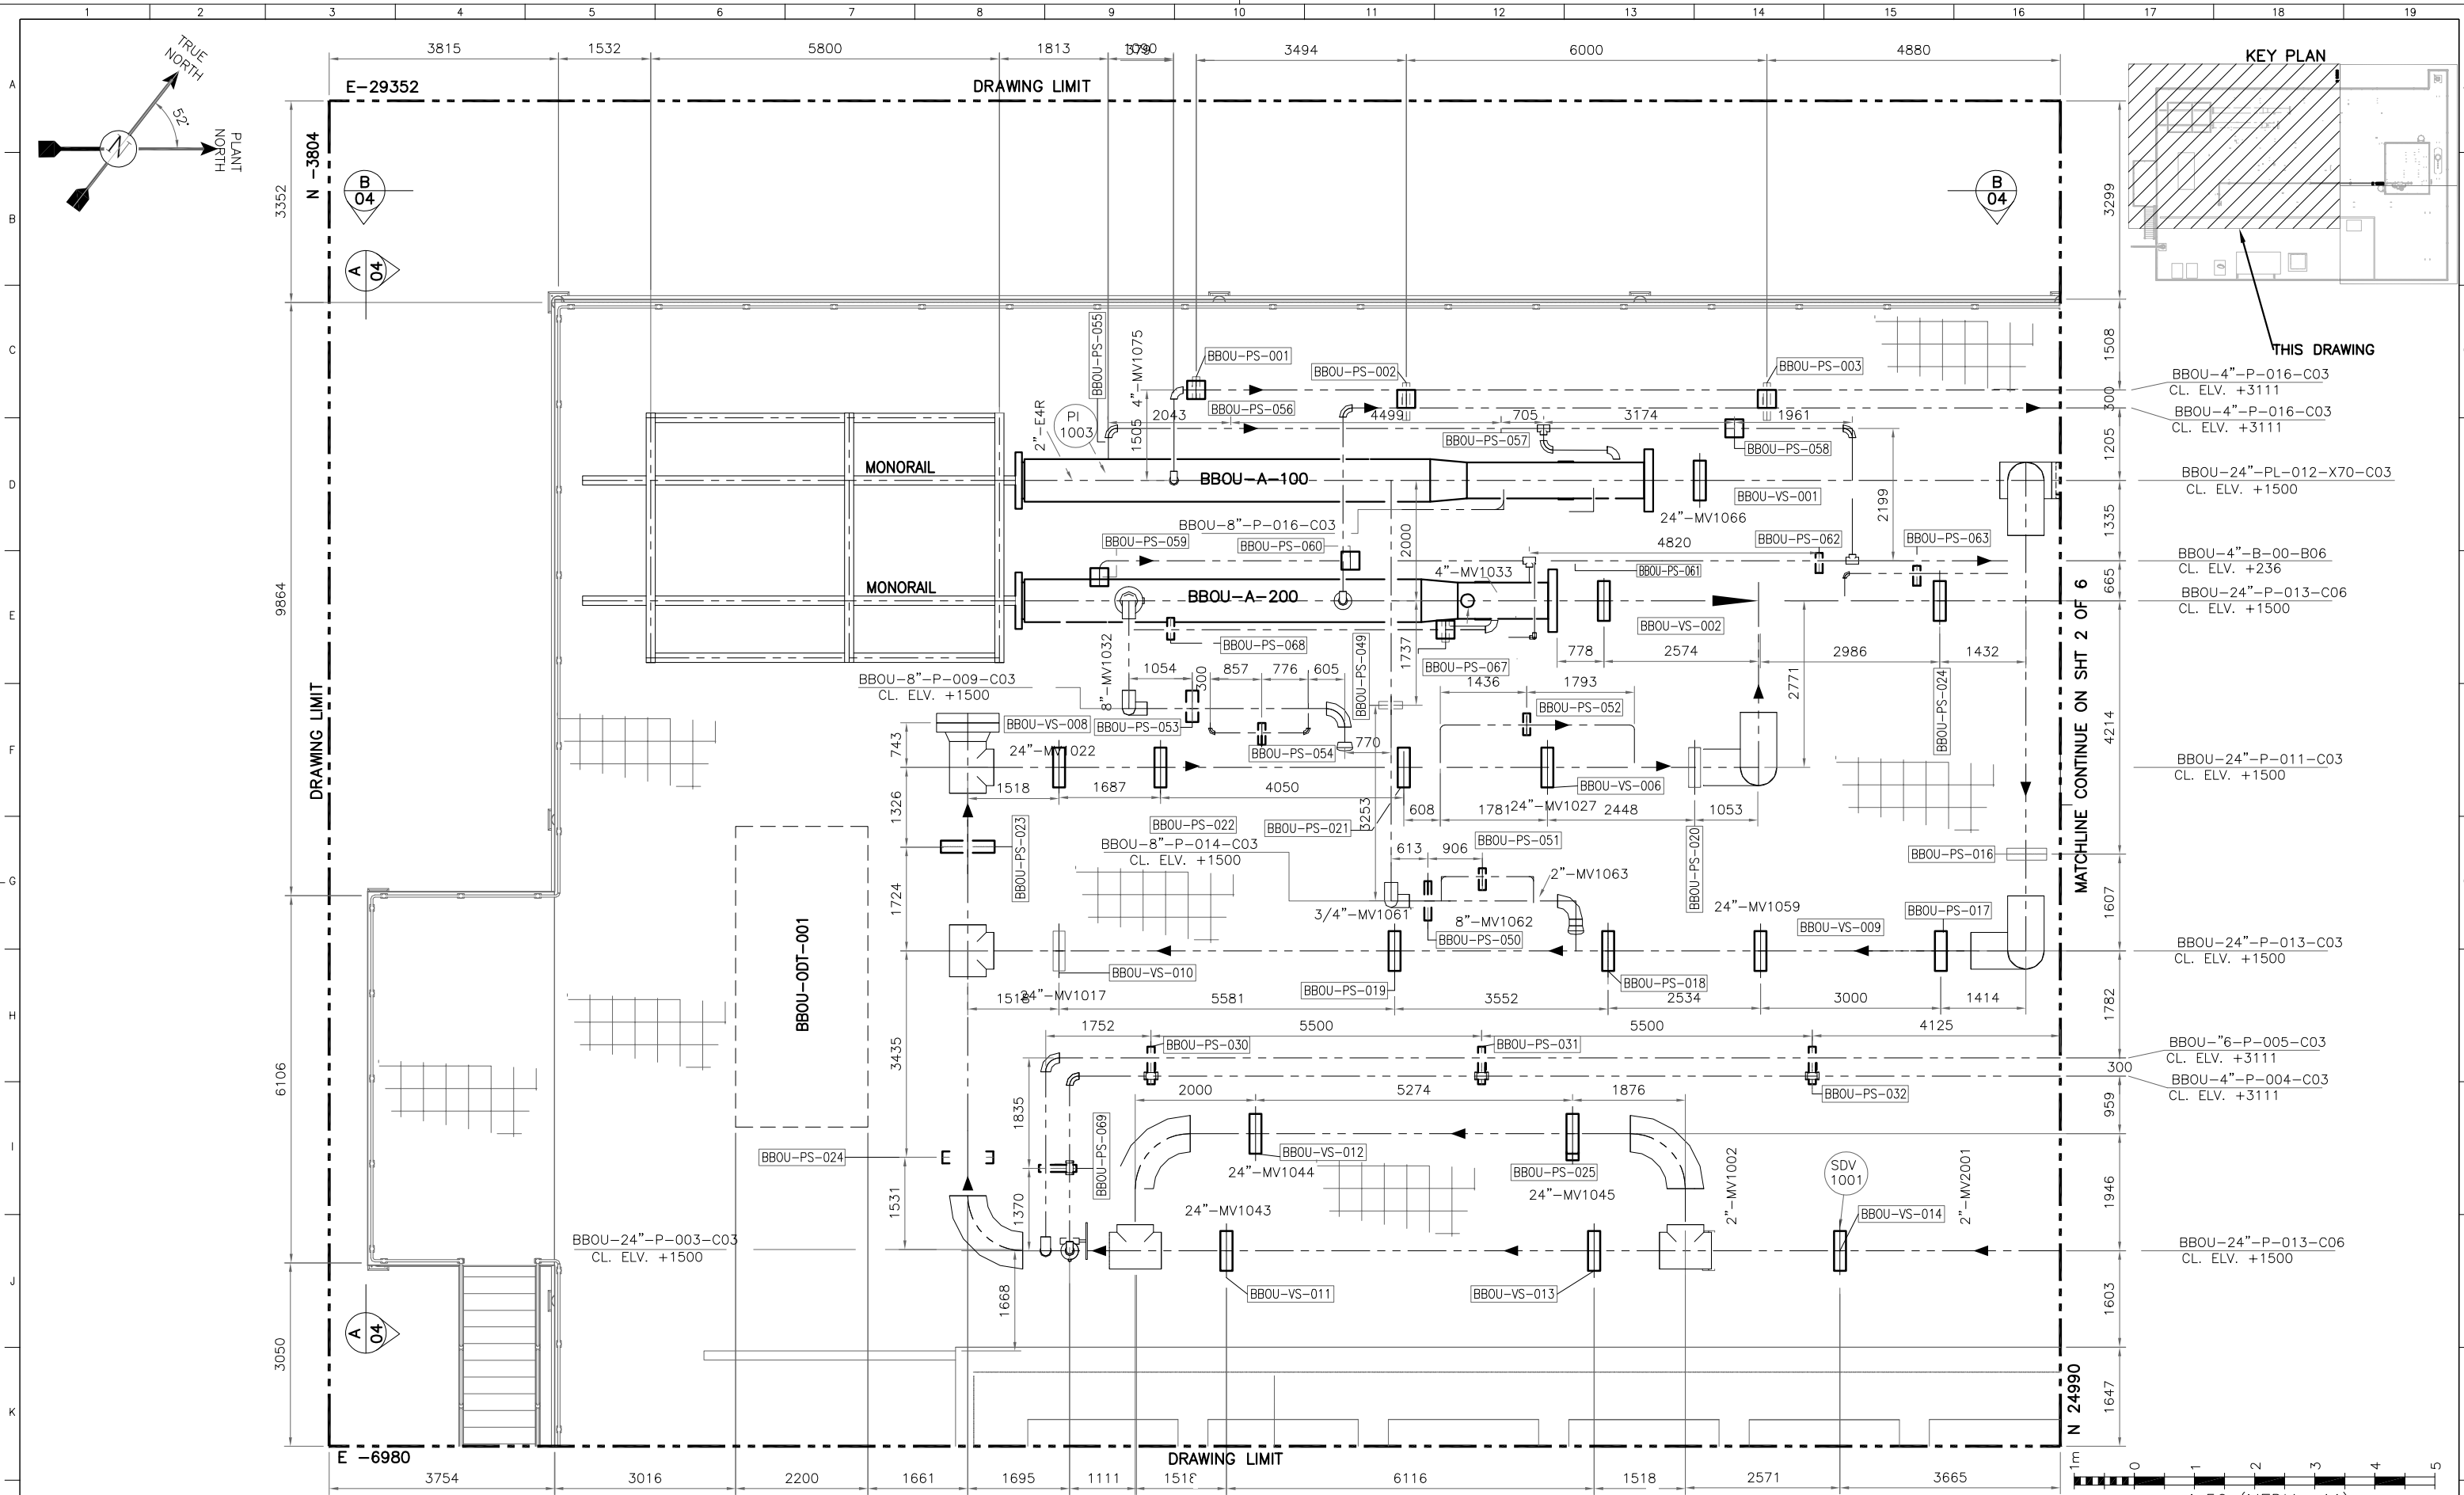
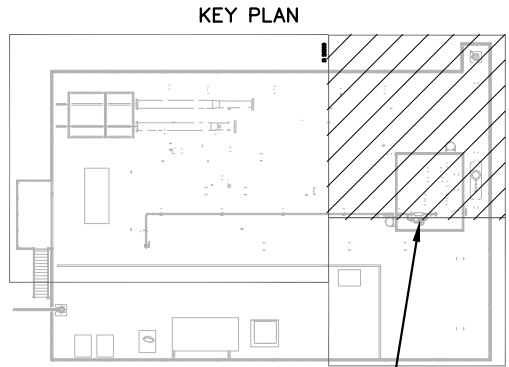


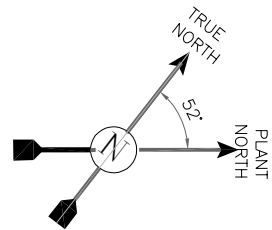



REFERENCE DRAWINGS	DRAWING No.	NOTES: 1. ALL DIMENSIONS ARE IN MILLIMETER UNLESS OTHER WISE SPECIFIED. 2. SUPPORT LOCATION SHALL BE FIRMED UP IN DETAILED ENGINEERING REFERENCE: 1. GENERAL PIPING ARRANGEMENT DRAWING – BBOU. EA-BFPCL–GPMC–GGPL–FEED–MPP–DWG–014								CONTRACTOR 	BRASS FERTILIZER & PETROCHEMICAL COMPANY LIMITED  GAS PROCESSING AND METHANOL COMPLEX PROJECT FEED FOR GAS GATHERING PIPELINES 	

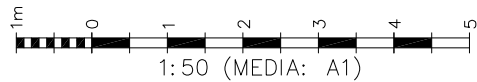

THIS DRAWING

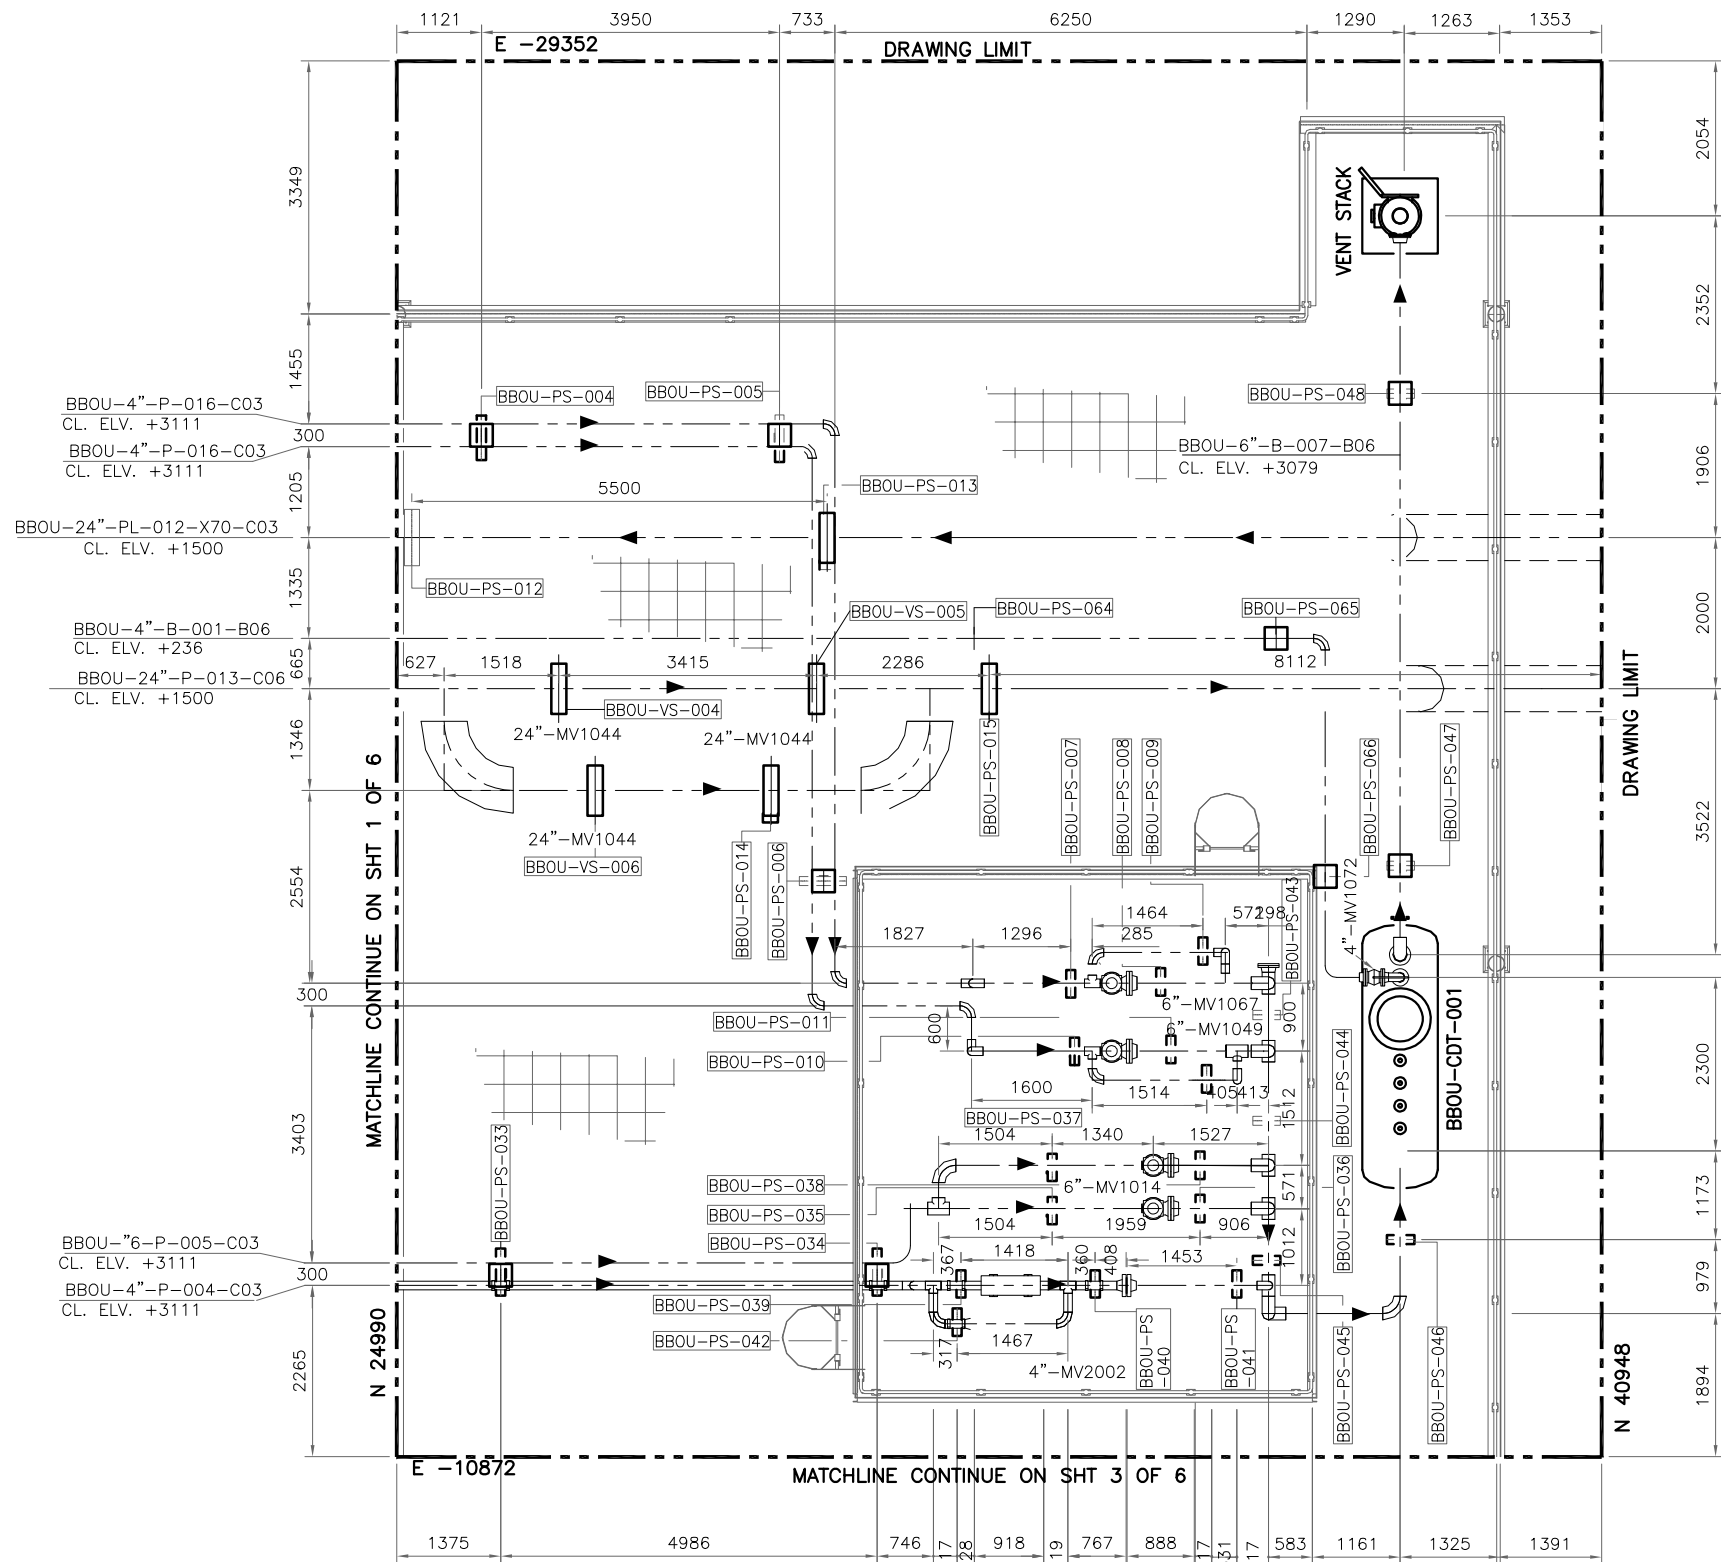

REFERENCE DRAWINGS	DRAWING No.	NOTES: 1. ALL DIMENSIONS ARE IN MILLIMETER UNLESS OTHER WISE SPECIFIED. 2. SUPPORT LOCATION SHALL BE FIRMED UP IN DETAILED ENGINEERING REFERENCE: 1. GENERAL PIPING ARRANGEMENT DRAWING – BBOU. EA–BFPCL–GPMC–GGPL–FEED–MPP–DWG–014	
--------------------	-------------	--	--	

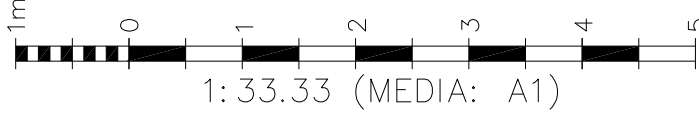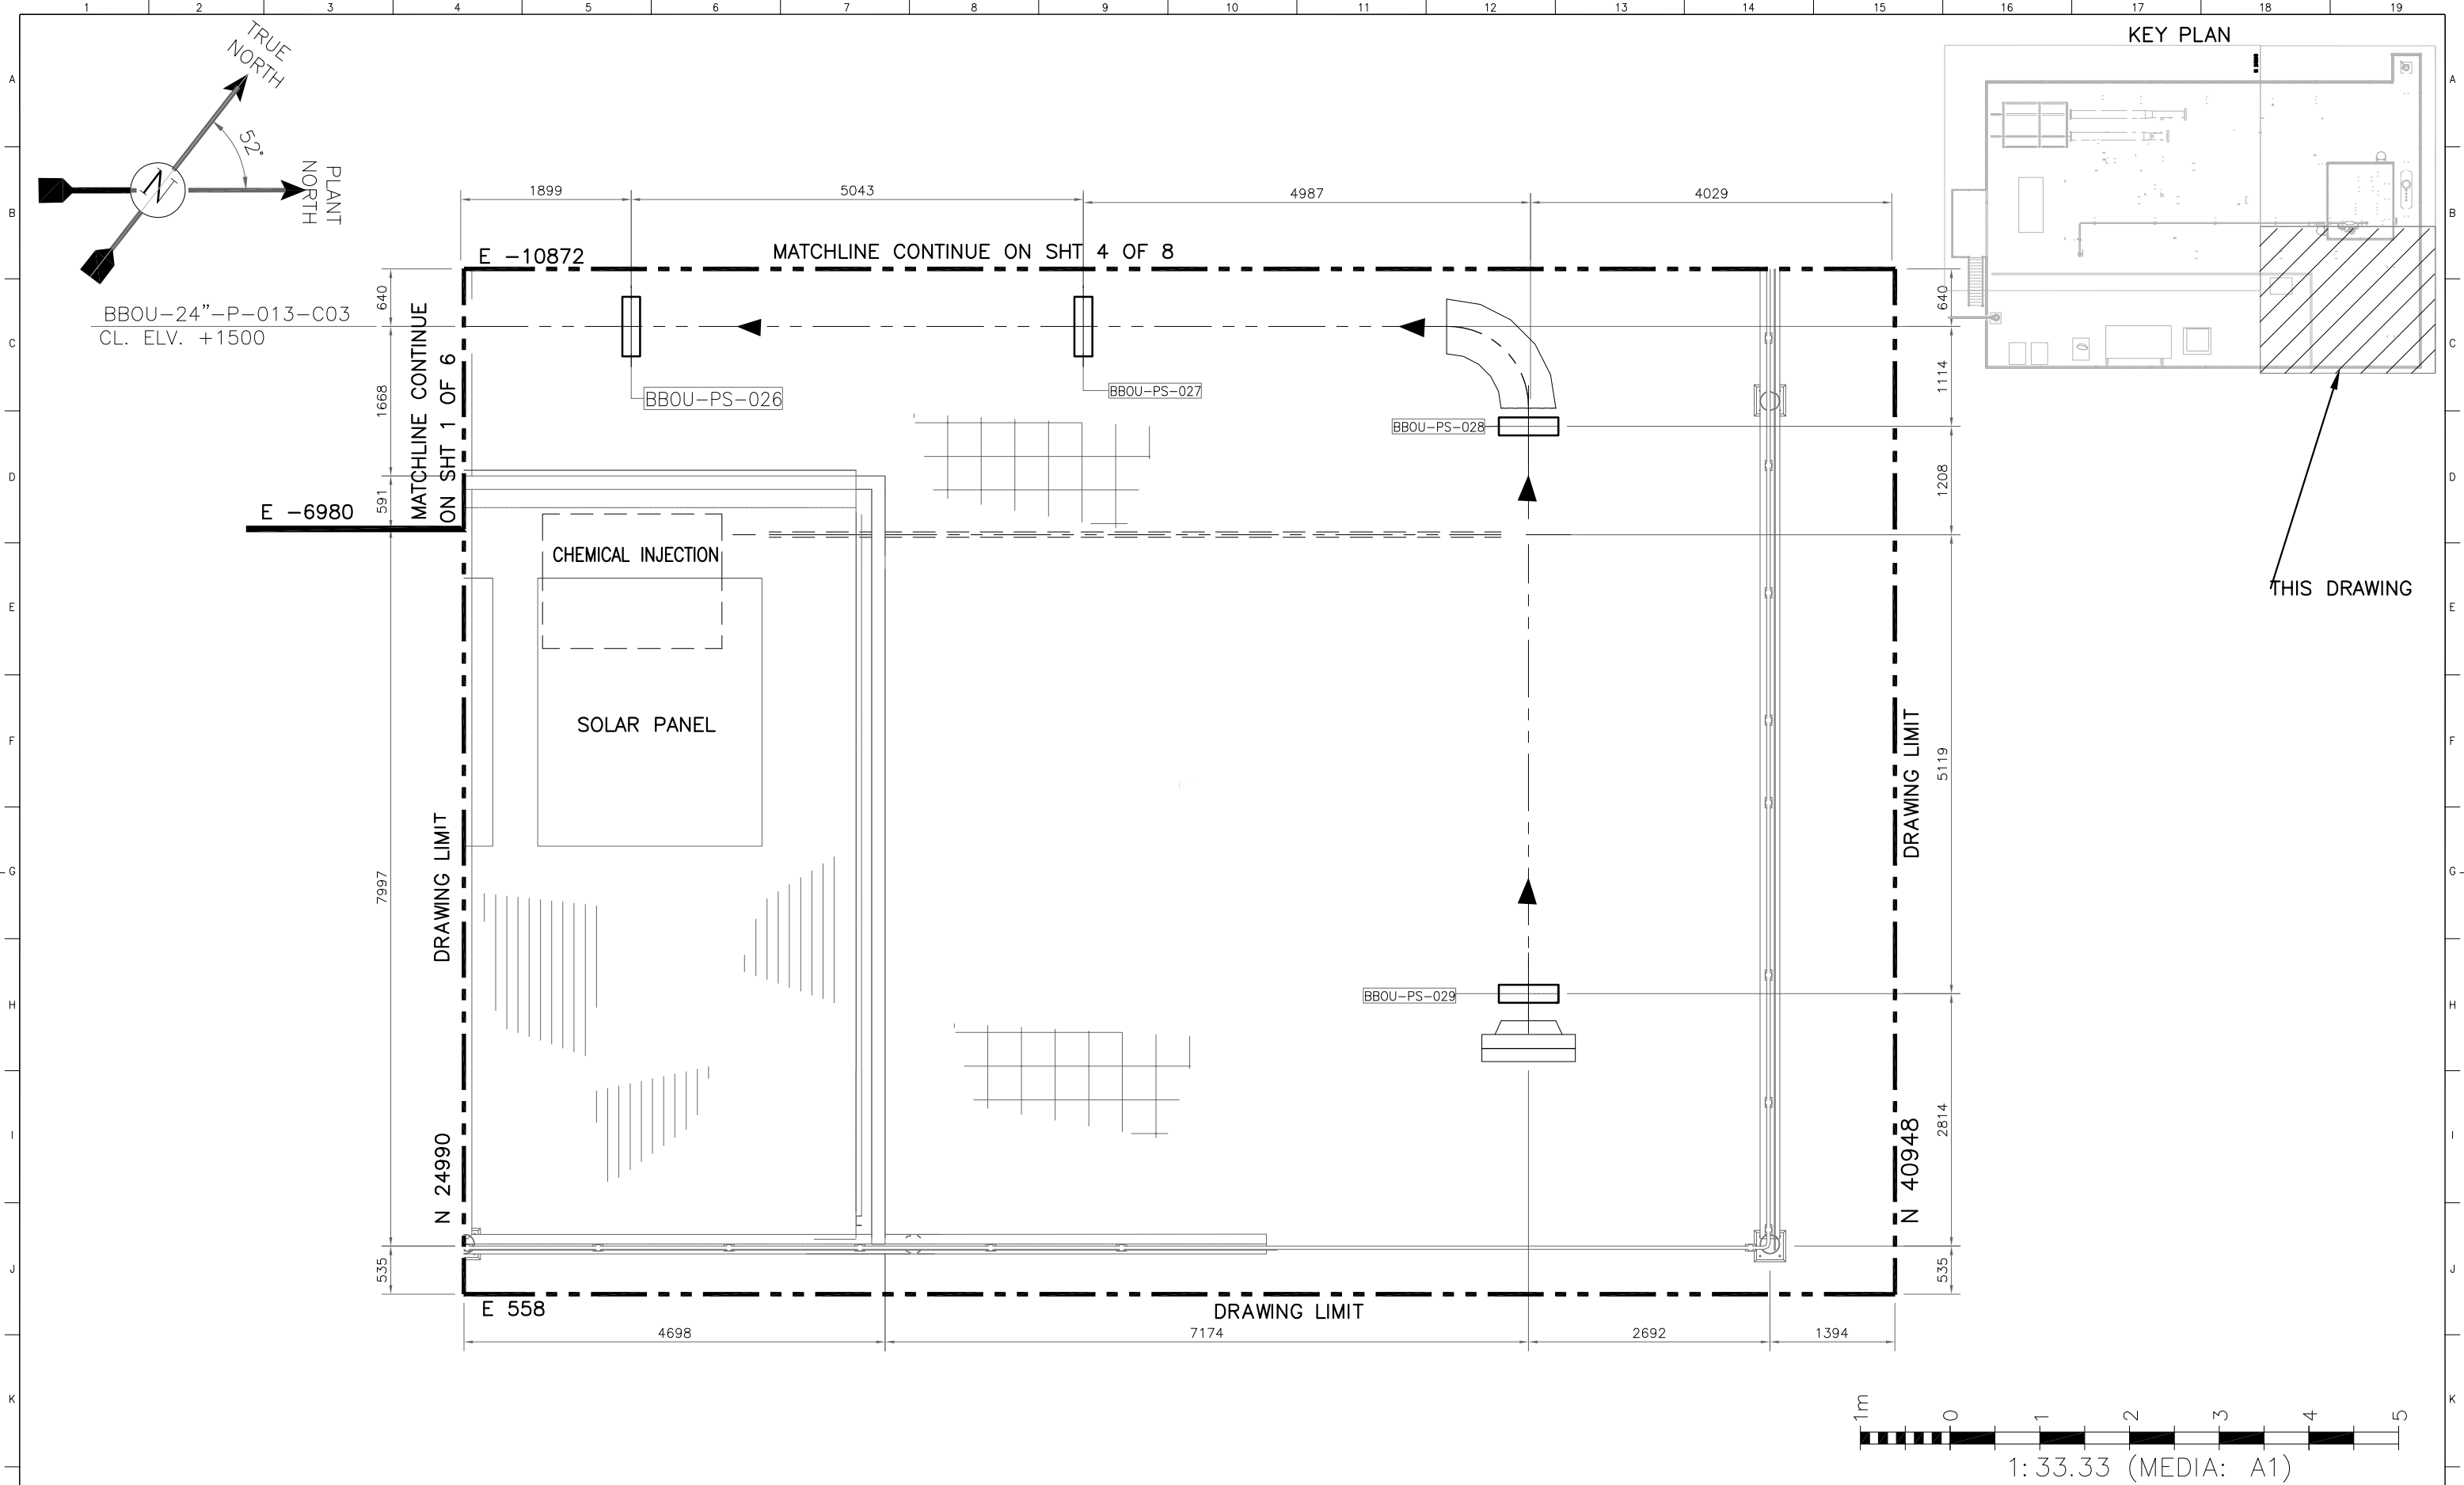

L	REFERENCE DRAWINGS		DRAWING No.		NOTES: 1. ALL DIMENSIONS ARE IN MILLIMETER UNLESS OTHER WISE SPECIFIED. 2. SUPPORT LOCATION SHALL BE FIRMED UP IN DETAILED ENGINEERING REFERENCE: 1. GENERAL PIPING ARRANGEMENT DRAWING – BBOU. EA–BFPCL–GPMC–GGPL–FEED–MPP–DWG–014							CONTRACTOR					BRASS FERTILIZER & PETROCHEMICAL COMPANY LIMITED																				
																	 GAS PROCESSING AND METHANOL COMPLEX PROJECT FEED FOR GAS GATHERING PIPELINES 																				
												ENDORSEMENT					LOCATION BBOU MANFOLD PLATFORM PIPE SUPPORT LOCATION DRAWING – BBOU																				
												RELEASED FOR		DESIGN ENGR.	BFPCL TECH REP	SPDC TECH REP	DATE																				
																		DRAWN: CAN																			
																		DATE: 31/07/2022																			
																		CHECKED: ENW																			
																		DRAWING No. EA-BFPCL-GPMC-GGPL-FEED-MPP-DWG-023																			
																		ENDORSED: ADR																			
																		PROJECT No. 11998A																			
M																	APP'D DATE: –																				
																	PROJECT No. –																				
																	R01																				
COPY RIGHT RESERVED																																					
1		2		3		4		5		6		7		8		9		10		11		12		13		14		15		16		17		18		19	