




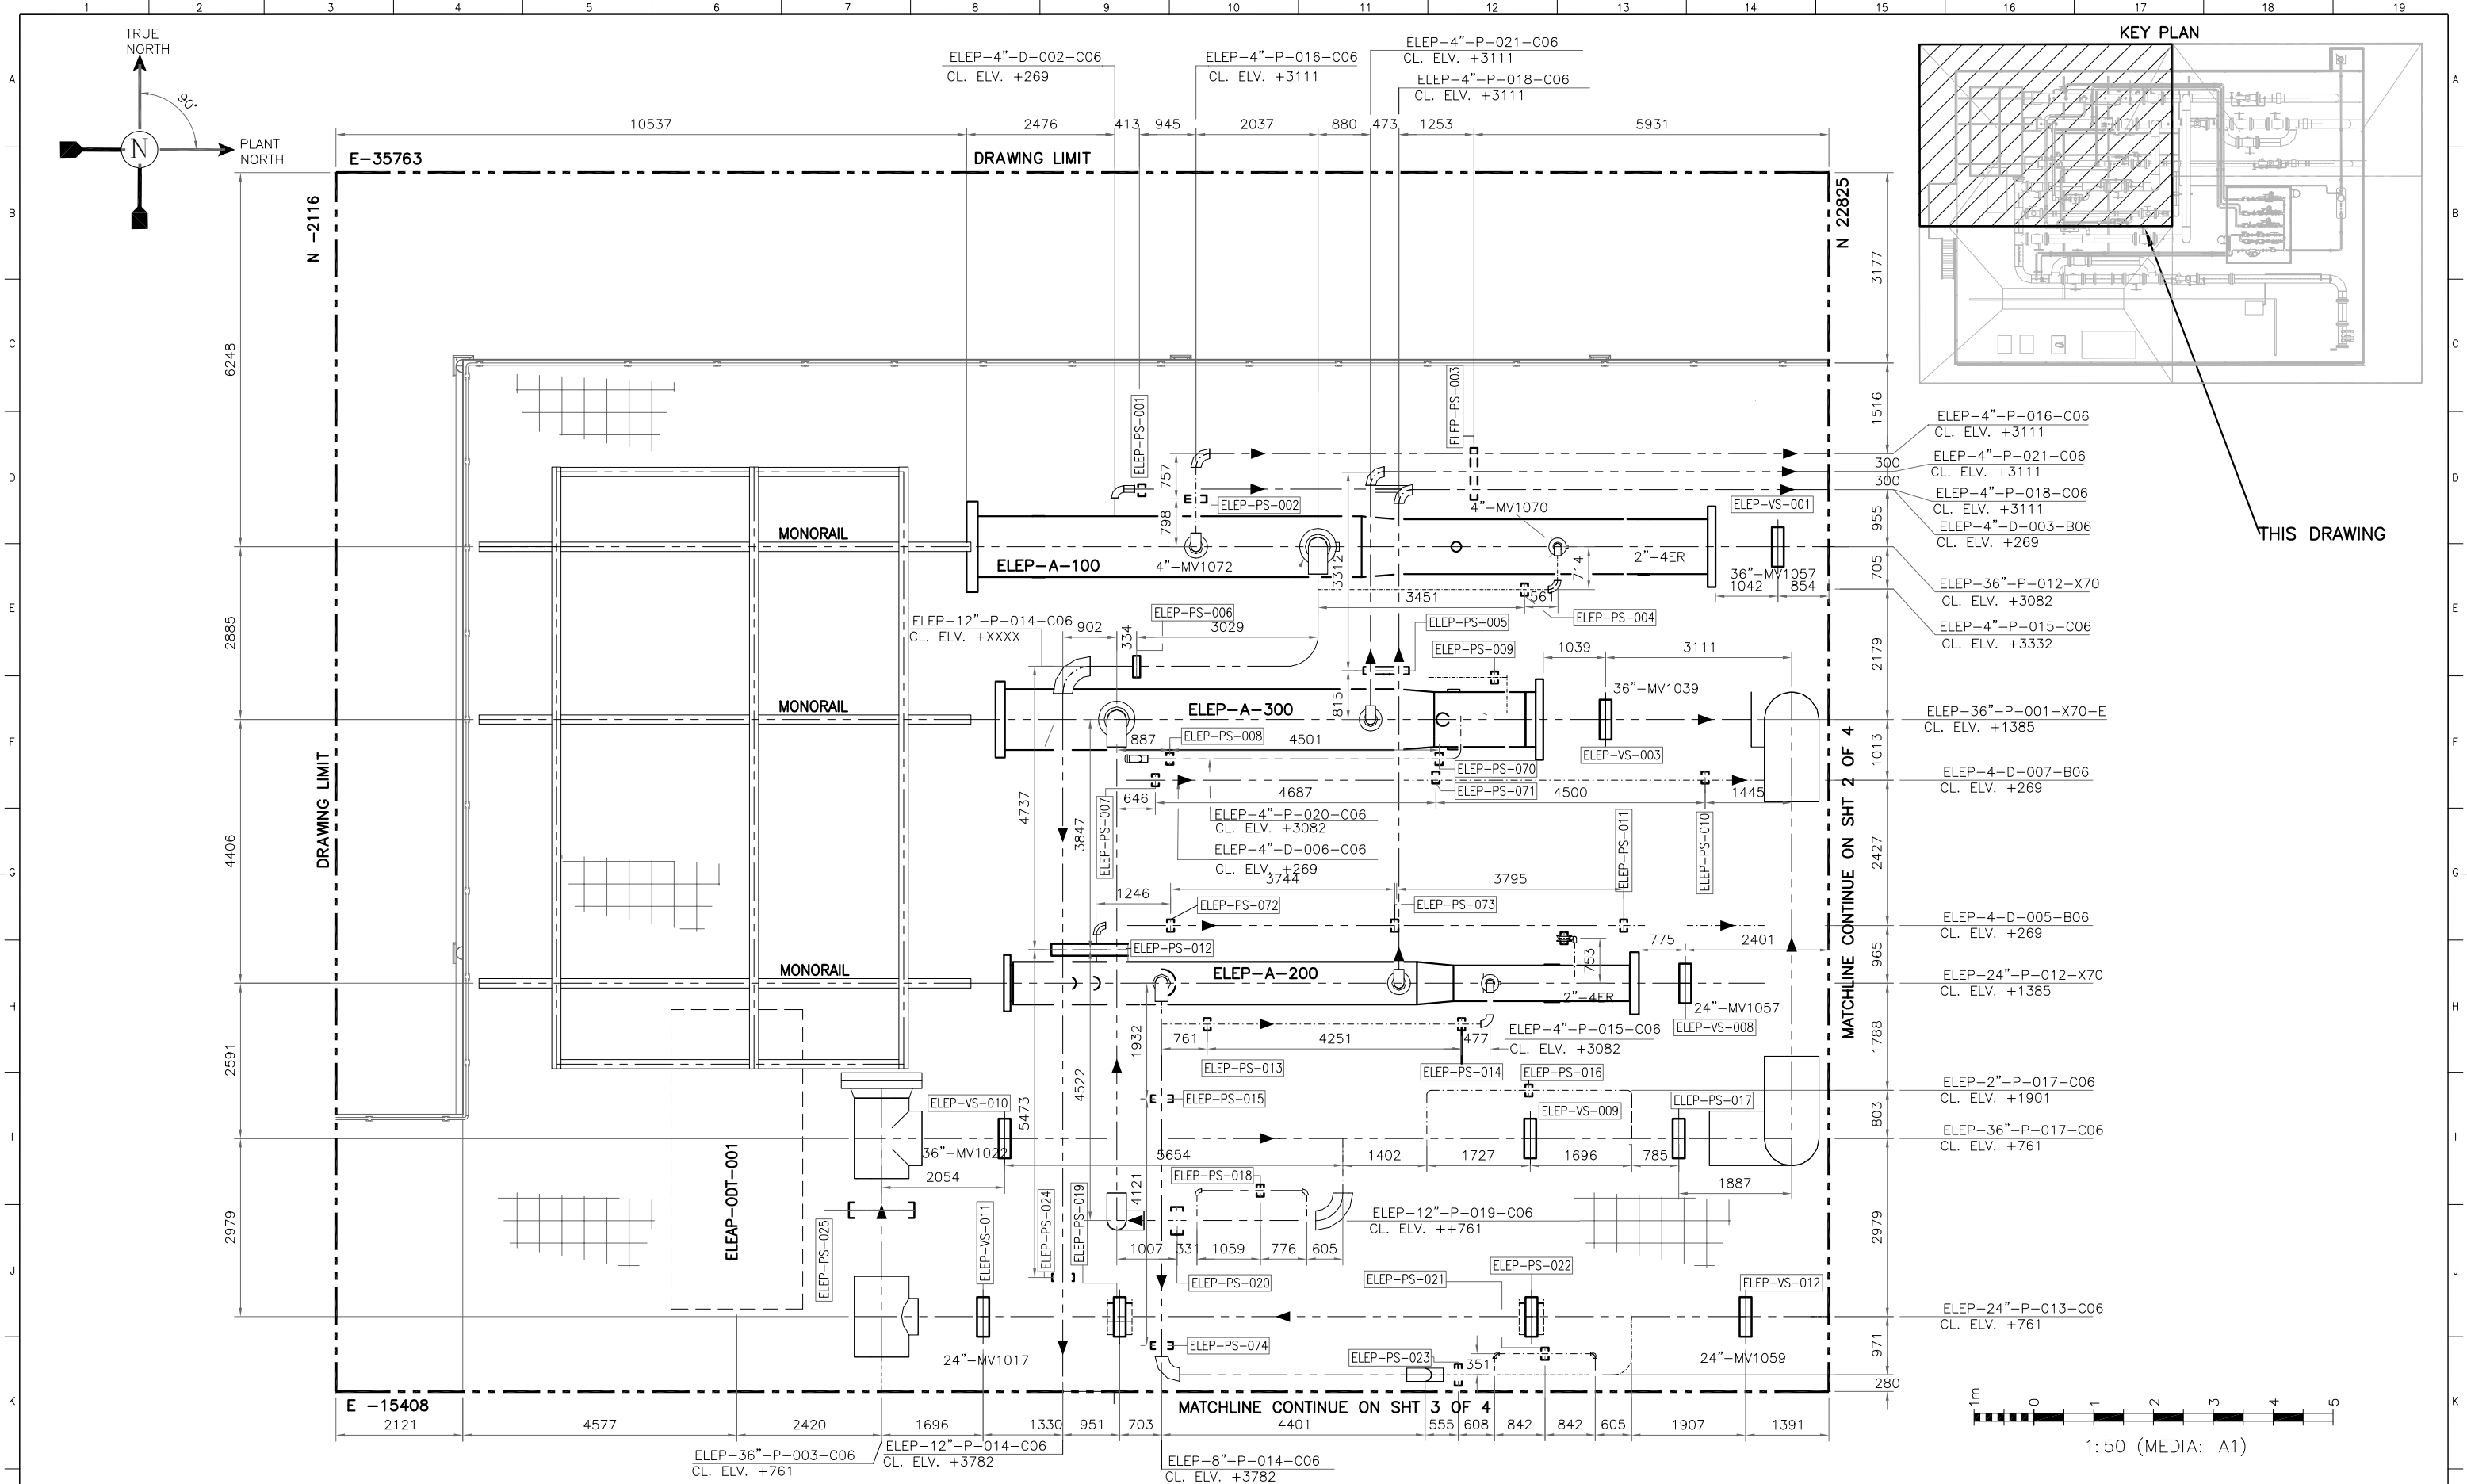

REFERENCE DRAWINGS		DRAWING No.		NOTES: 1. ALL DIMENSIONS ARE IN MILLIMETER UNLESS OTHER WISE SPECIFIED. 2. SUPPORT LOCATION SHALL BE FIRMED UP IN DETAILED ENGINEERING REFERENCE: 1. GENERAL PIPING ARRANGEMENT DRAWING – ELEPA EA–BFPCl–GPMC–GGPL–FEED–MPP–DWG–015						CONTRACTOR						BRASS FERTILIZER & PETROCHEMICAL COMPANY LIMITED																			
																						 GAS PROCESSING AND METHANOL COMPLEX PROJECT FEED FOR GAS GATHERING PIPELINES 													
																ENDORSEMENT						LOCATION ELEPA MANFOLD PLATFORM													
																RELEASED FOR						DESIGN ENGR.		BFPC TECH REP		SPDC TECH REP		DATE		PIPE SUPPORTS LOCATION DRAWING – ELEP					
																														DRAWN: CAN					
																														DATE: 31/07/2022					
										R01						ISSUED FOR REVIEW						CAN		ENW		ADR		–		CHECKED: ENW					
										REV												DRAWN		CHK		END		DATE		DRAWING No. EA-BFPCl-GPMC-GGPL-FEED-MPP-DWG-024					
																														PROJECT No. 11998A					
																														PROJECT No. –					
																														REV.					
																														R01					

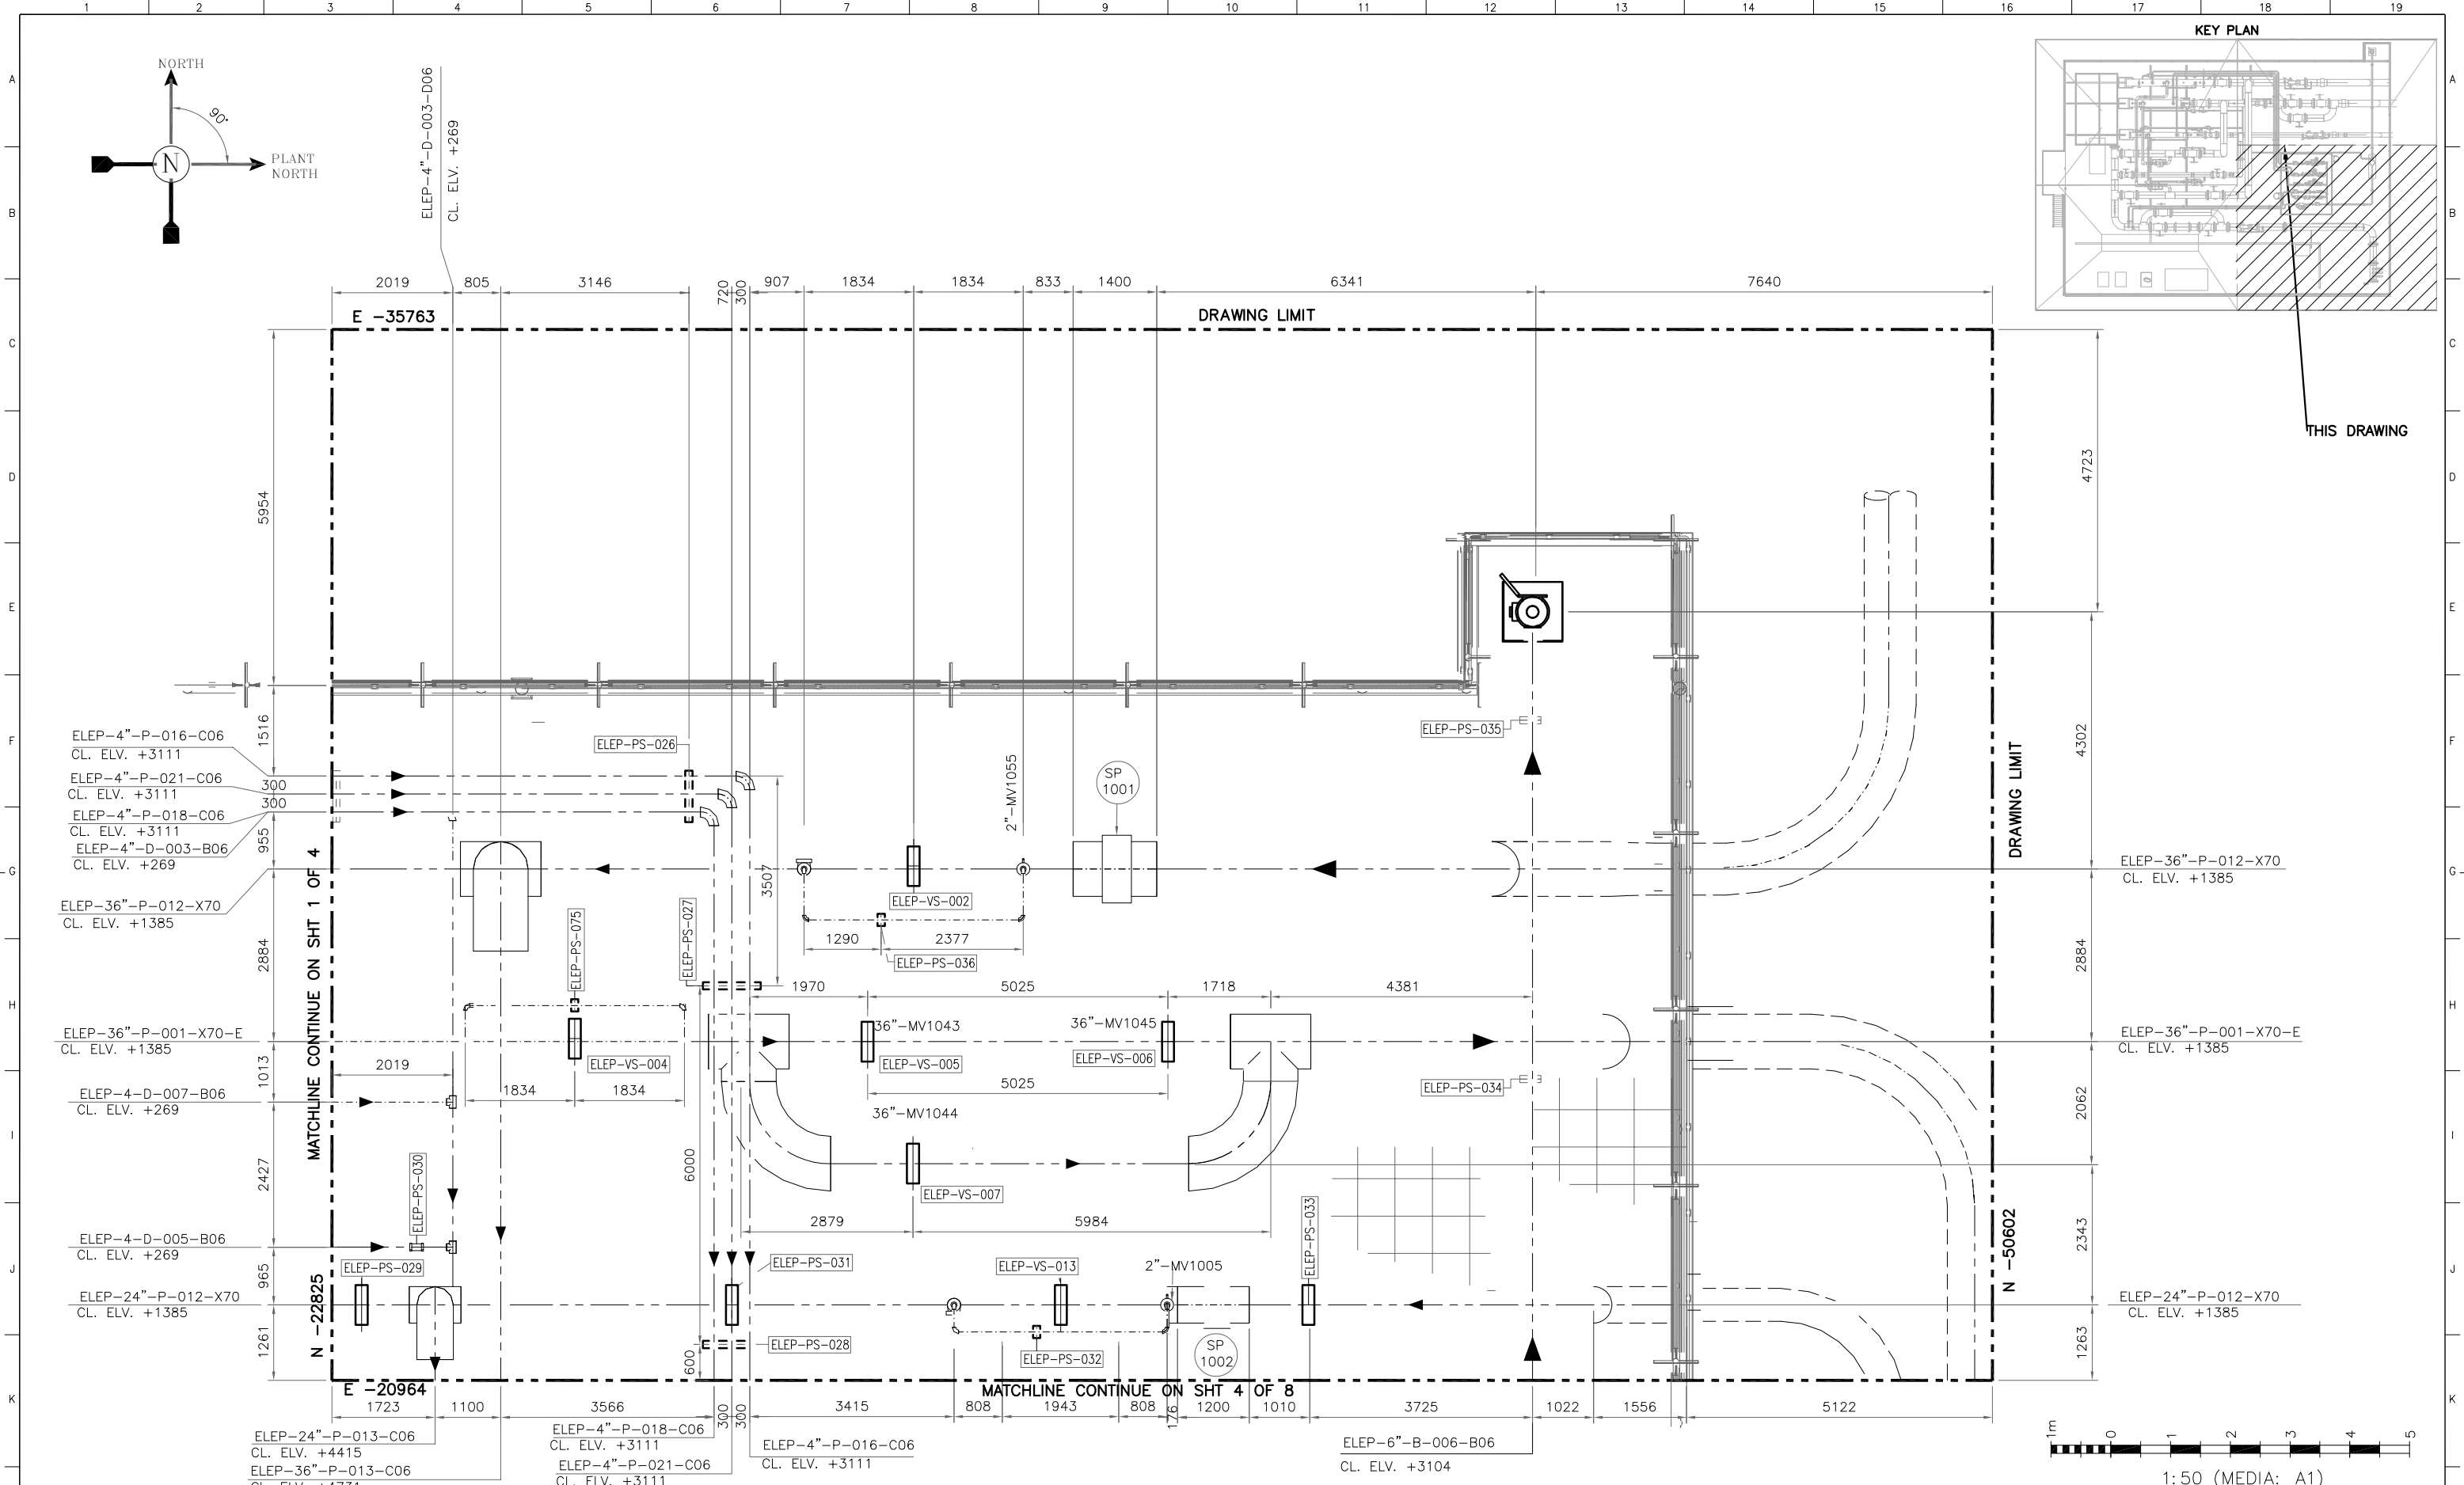

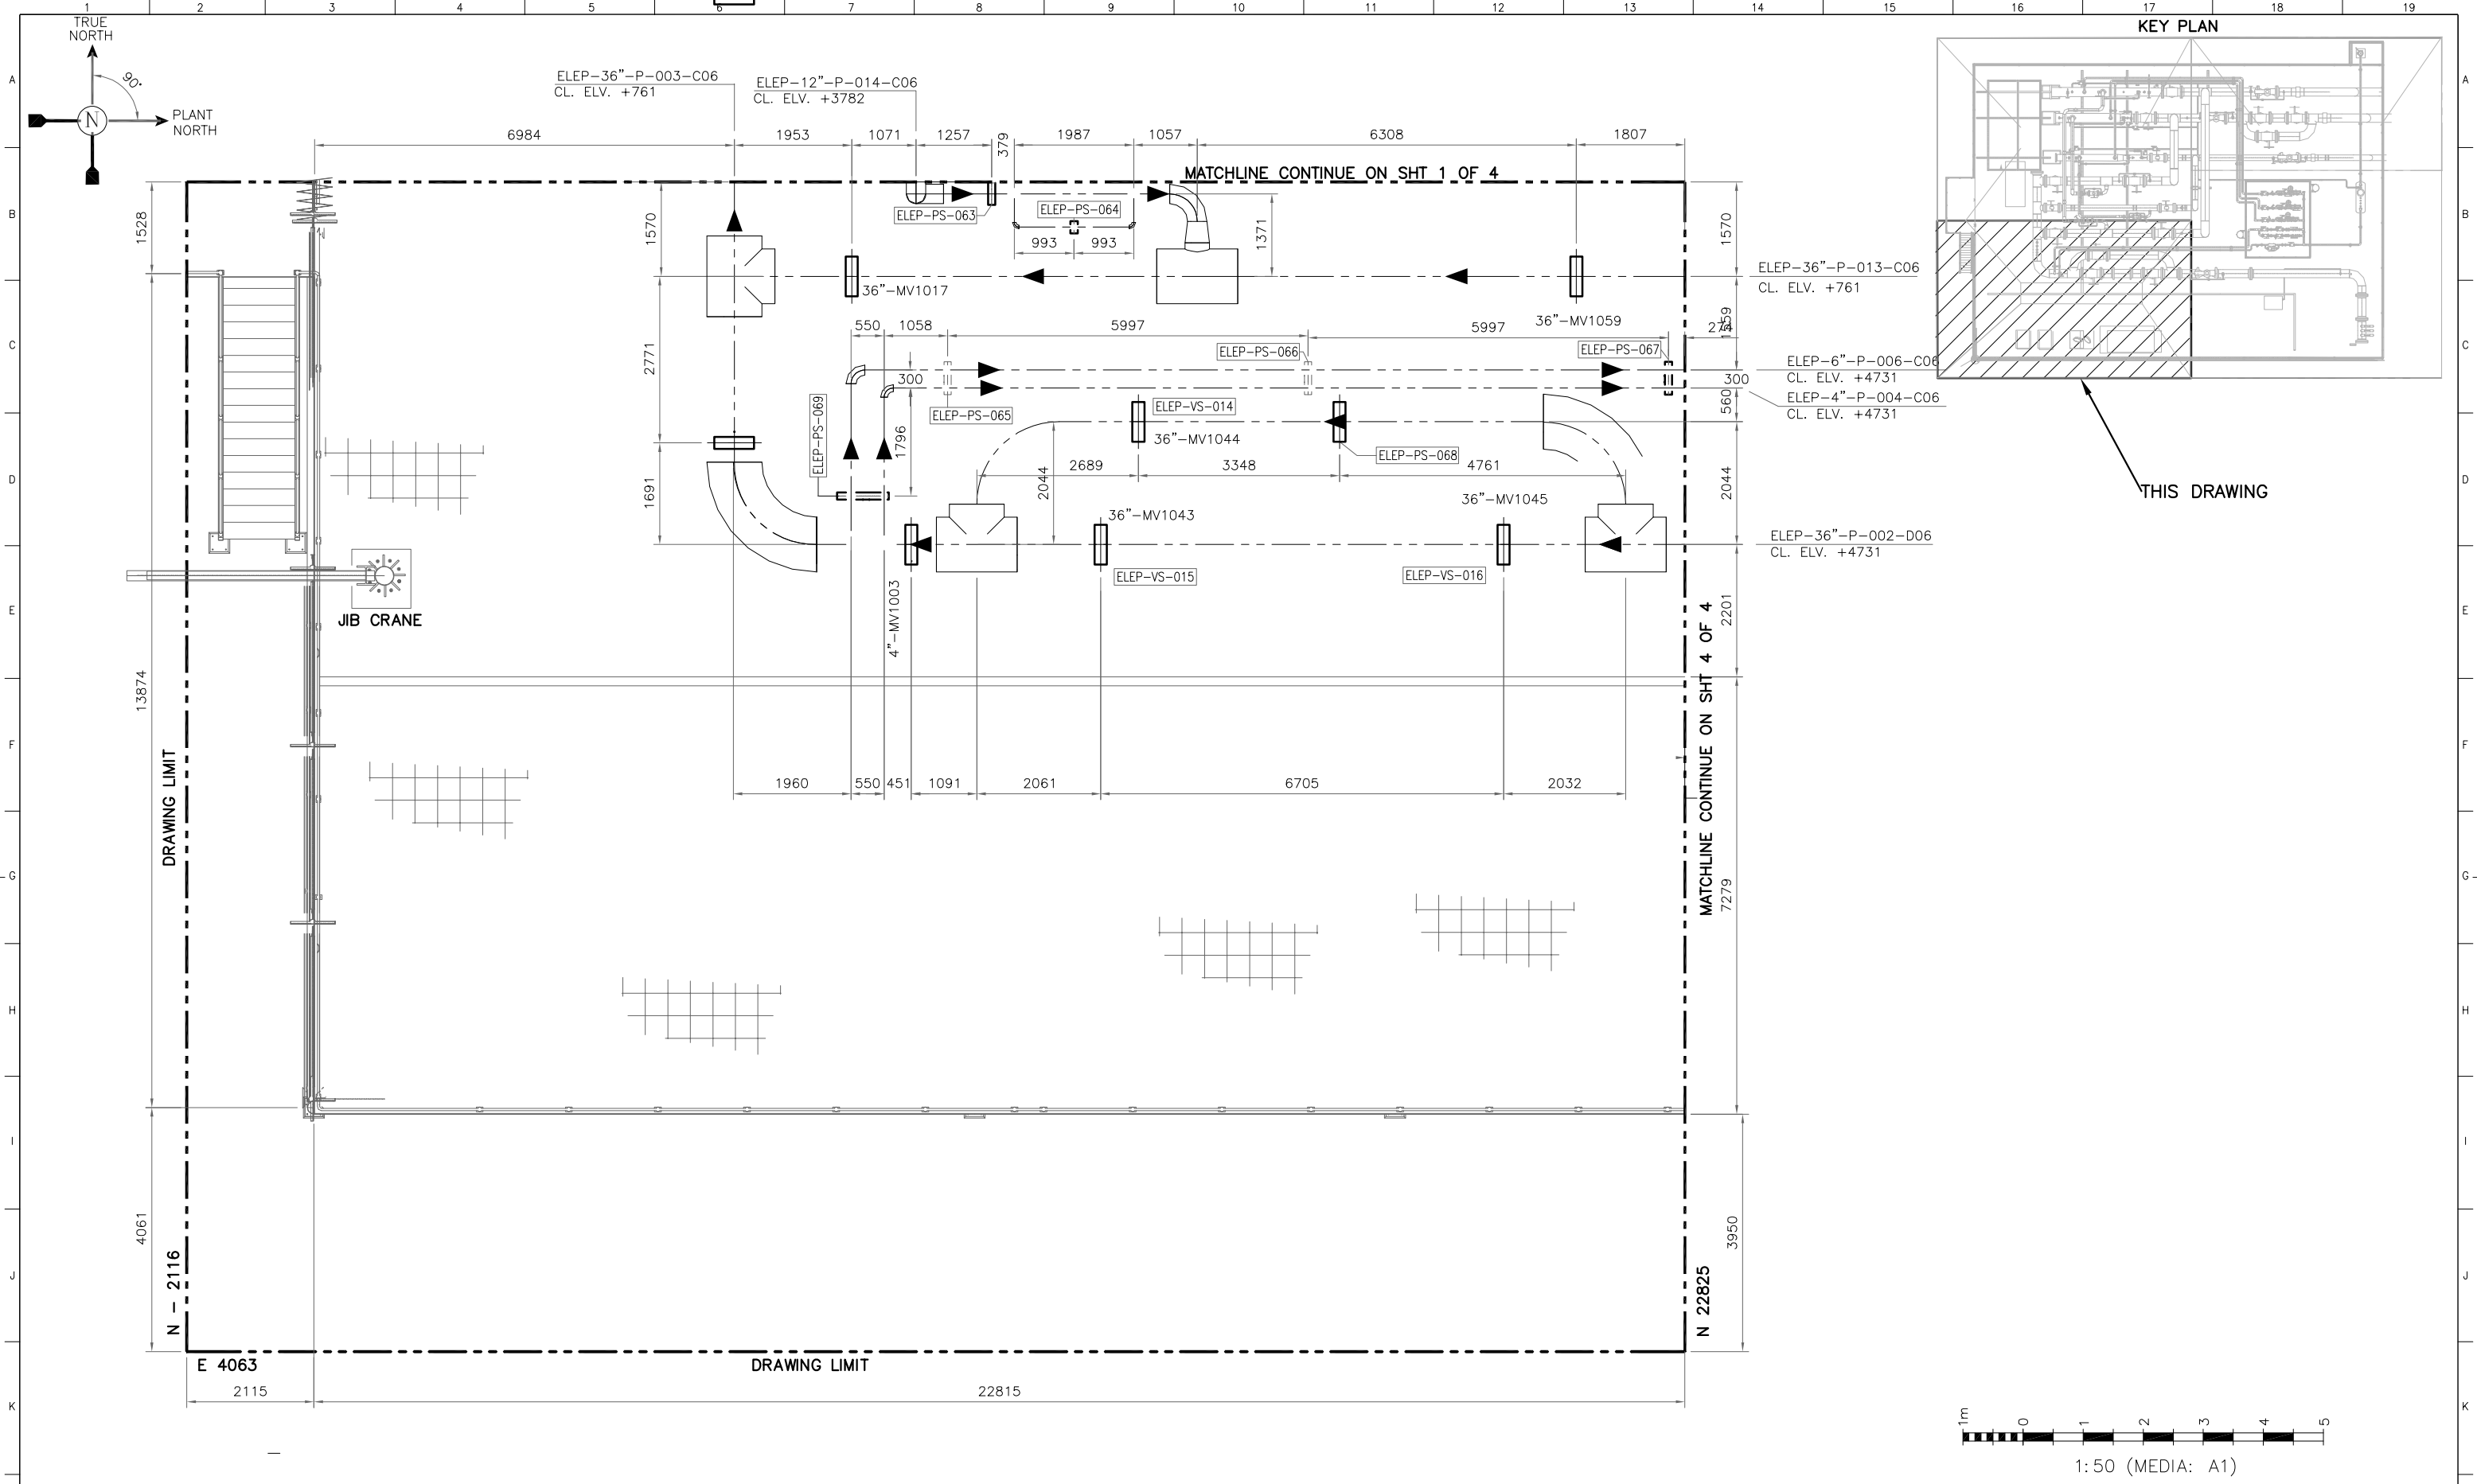

L	REFERENCE DRAWINGS		DRAWING No.		NOTES: 1. ALL DIMENSIONS ARE IN MILLIMETER UNLESS OTHER WISE SPECIFIED. 2. SUPPORT LOCATION SHALL BE FIRMED UP IN DETAILED ENGINEERING REFERENCE: 1. GENERAL PIPING ARRANGEMENT DRAWING – ELEPA EA-BFPCL-GPMC-GGPL-FEED-MPP-DWG-015										CONTRACTOR						BRASS FERTILIZER & PETROCHEMICAL COMPANY LIMITED											
	epic ATLANTIC														brass fertilizer						GAS PROCESSING AND METHANOL COMPLEX PROJECT FEED FOR GAS GATHERING PIPELINES											
	ENDORSEMENT														LOCATION ELEPA MANFOLD PLATFORM PIPE SUPPORTS LOCATION DRAWING – ELEP																	
	RELEASED FOR		DESIGN ENGR.												BFPCL TECH REP		SPDC TECH REP		DATE		DRAWN: CAN					DATE: 31/07/2022					SHEET: 4 of 4	
	R01 ISSUED FOR REVIEW		CAN												ENW		ADR		–		CHECKED: ENW					DRAWING No. EA-BFPCL-GPMC-GGPL-FEED-MPP-DWG-024					REV.	
	REV		DRAWN												CHK		END		DATE		ENDORSED: ADR					PROJECT No. 11998A					R01	
																					APP'D DATE: –					PROJECT No. –						
	COPY RIGHT RESERVED																															