



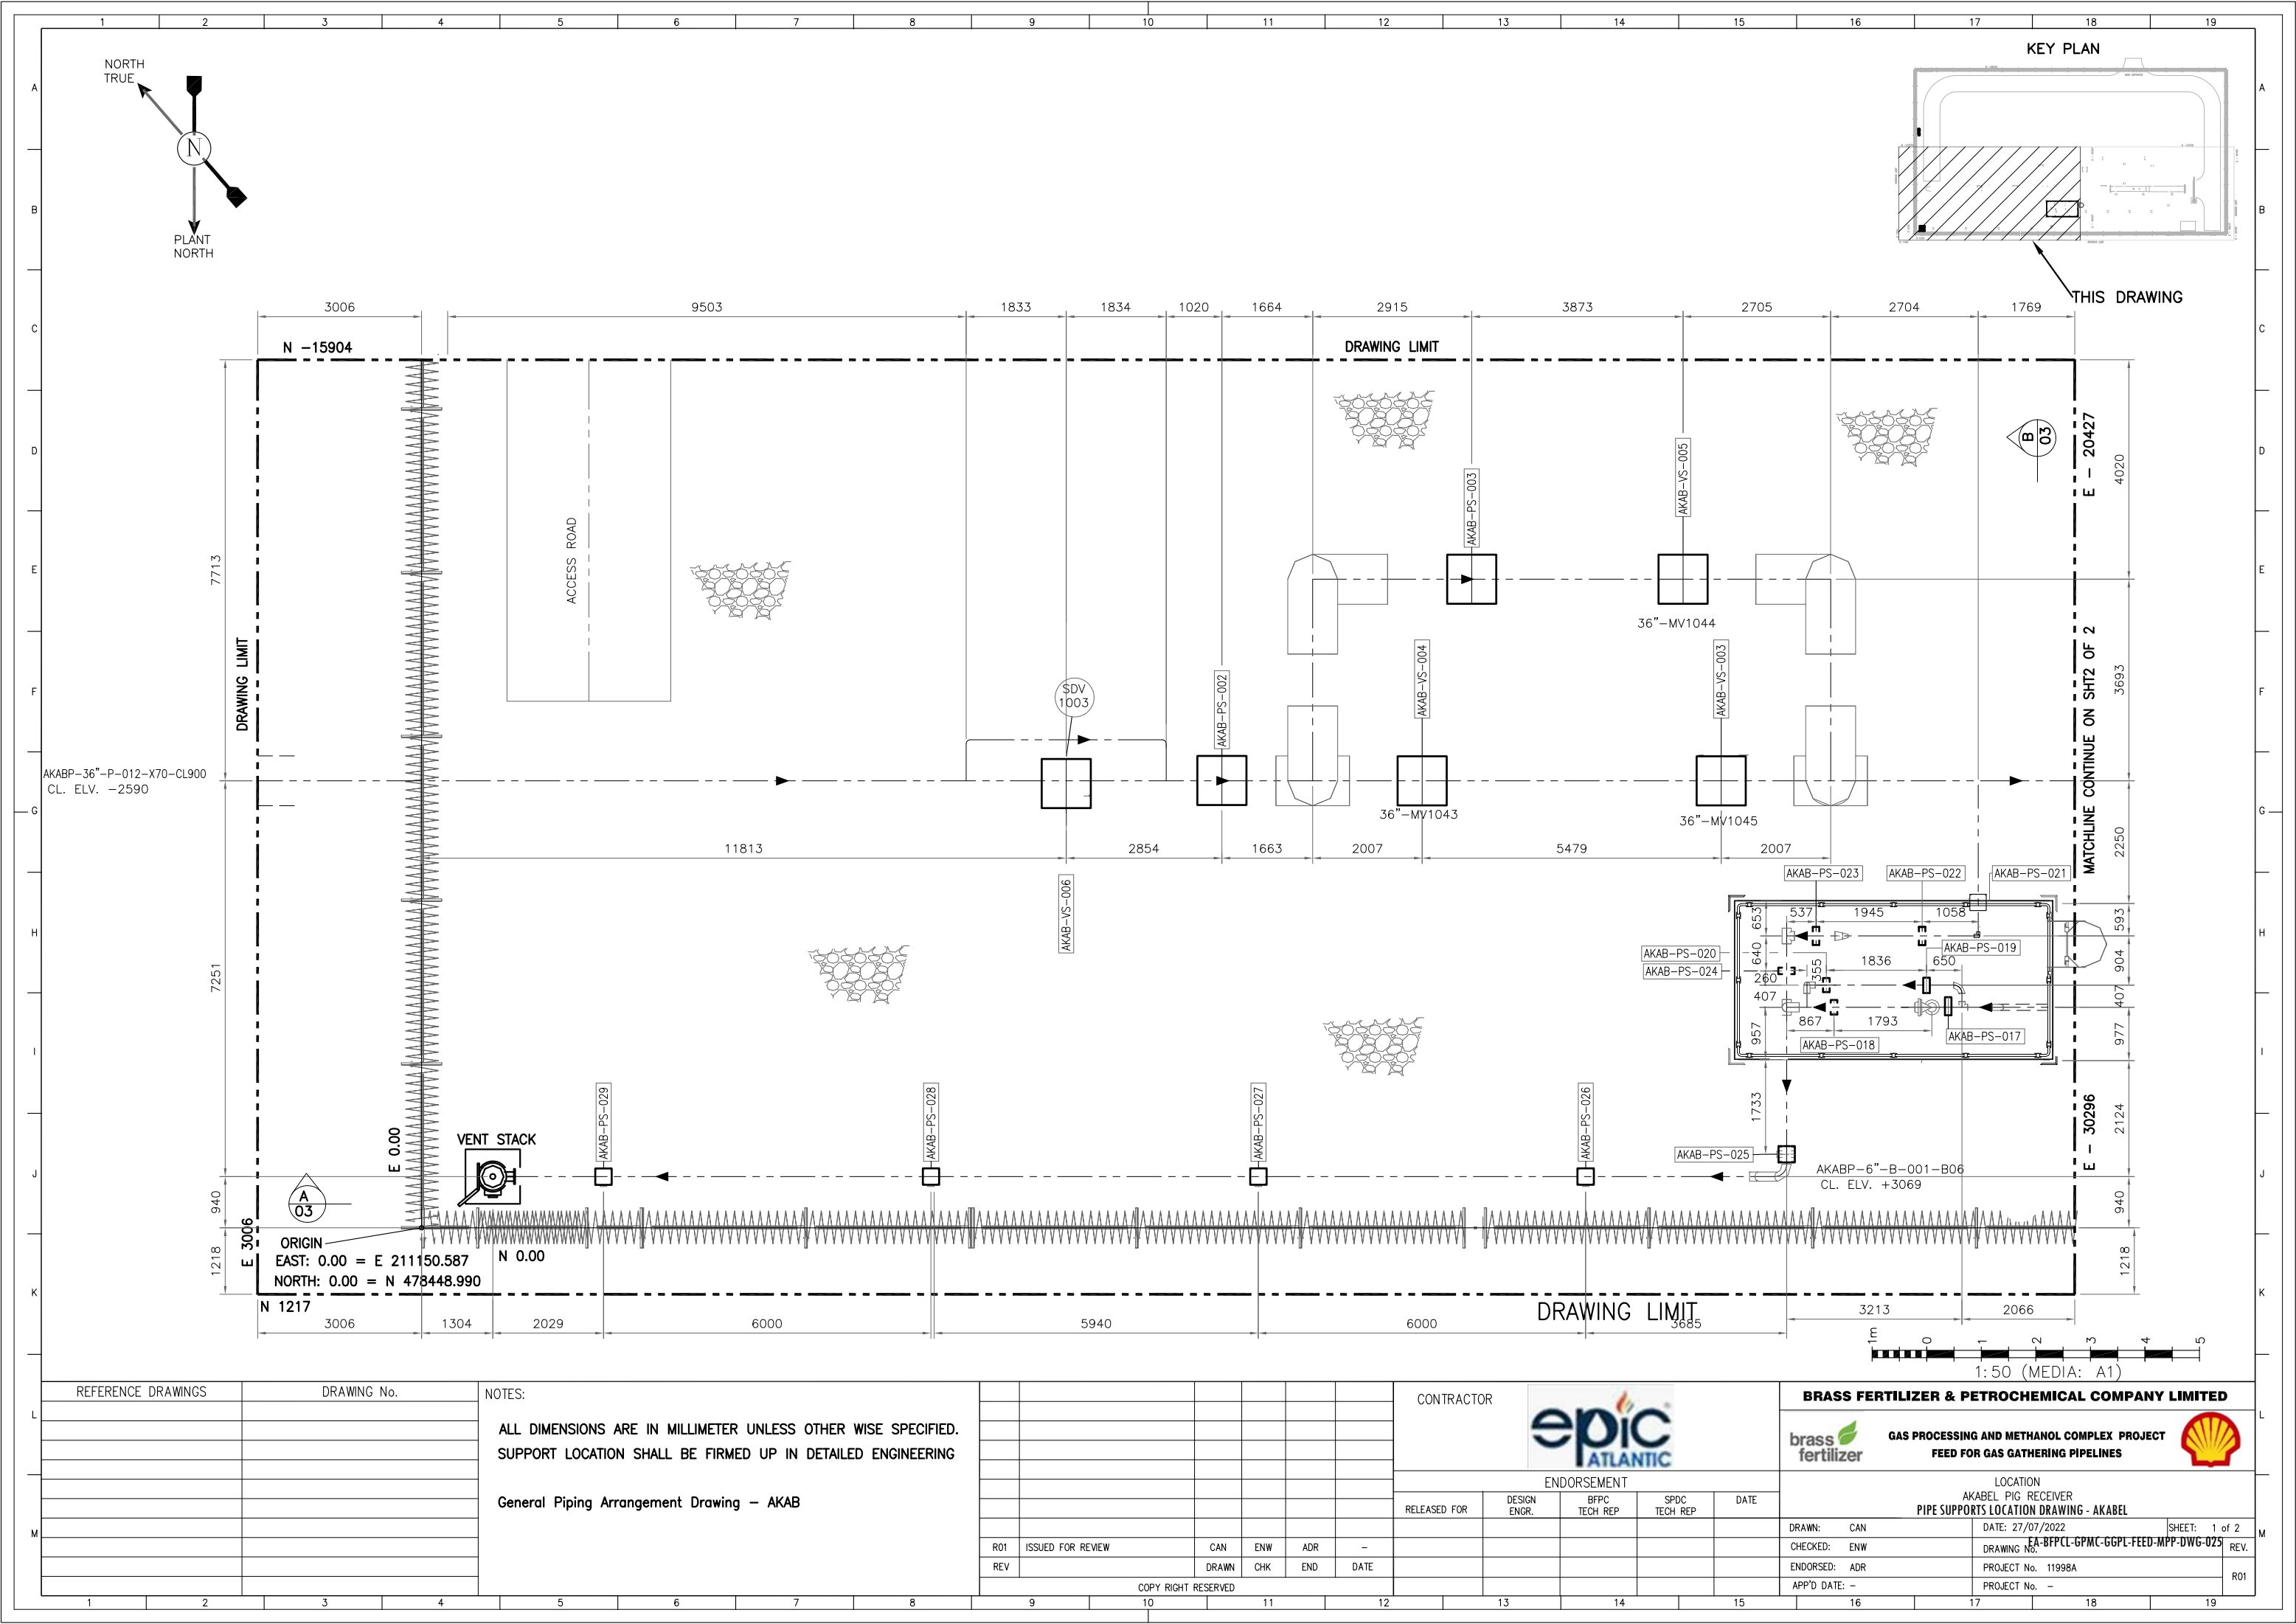

REFERENCE DRAWINGS	DRAWING No.	NOTES: ALL DIMENSIONS ARE IN MILLIMETER UNLESS OTHER WISE SPECIFIED. SUPPORT LOCATION SHALL BE FIRMED UP IN DETAILED ENGINEERING General Piping Arrangement Drawing – AKAB								CONTRACTOR 	BRASS FERTILIZER & PETROCHEMICAL COMPANY LIMITED				
												 GAS PROCESSING AND METHANOL COMPLEX PROJECT FEED FOR GAS GATHERING PIPELINES			
												LOCATION AKABEL PIG RECEIVER PIPE SUPPORTS LOCATION DRAWING - AKABEL			
											ENDORSEMENT				
											RELEASED FOR	DESIGN ENGR.	BFPC TECH REP	SPDC TECH REP	DATE
R01	ISSUED FOR REVIEW			CAN	ENW	ADR	–								
REV				DRAWN	CHK	END	DATE								
				COPY RIGHT RESERVED											

DRAWN: CAN	DATE: 27/07/2022	SHEET: 1 of 2
CHECKED: ENW	DRAWING No. EA-BFPCL-GPMC-GGPL-FEED-MPP-DWG-025	REV.
ENDORSED: ADR	PROJECT No. 11998A	
APP'D DATE: –	PROJECT No. –	R01

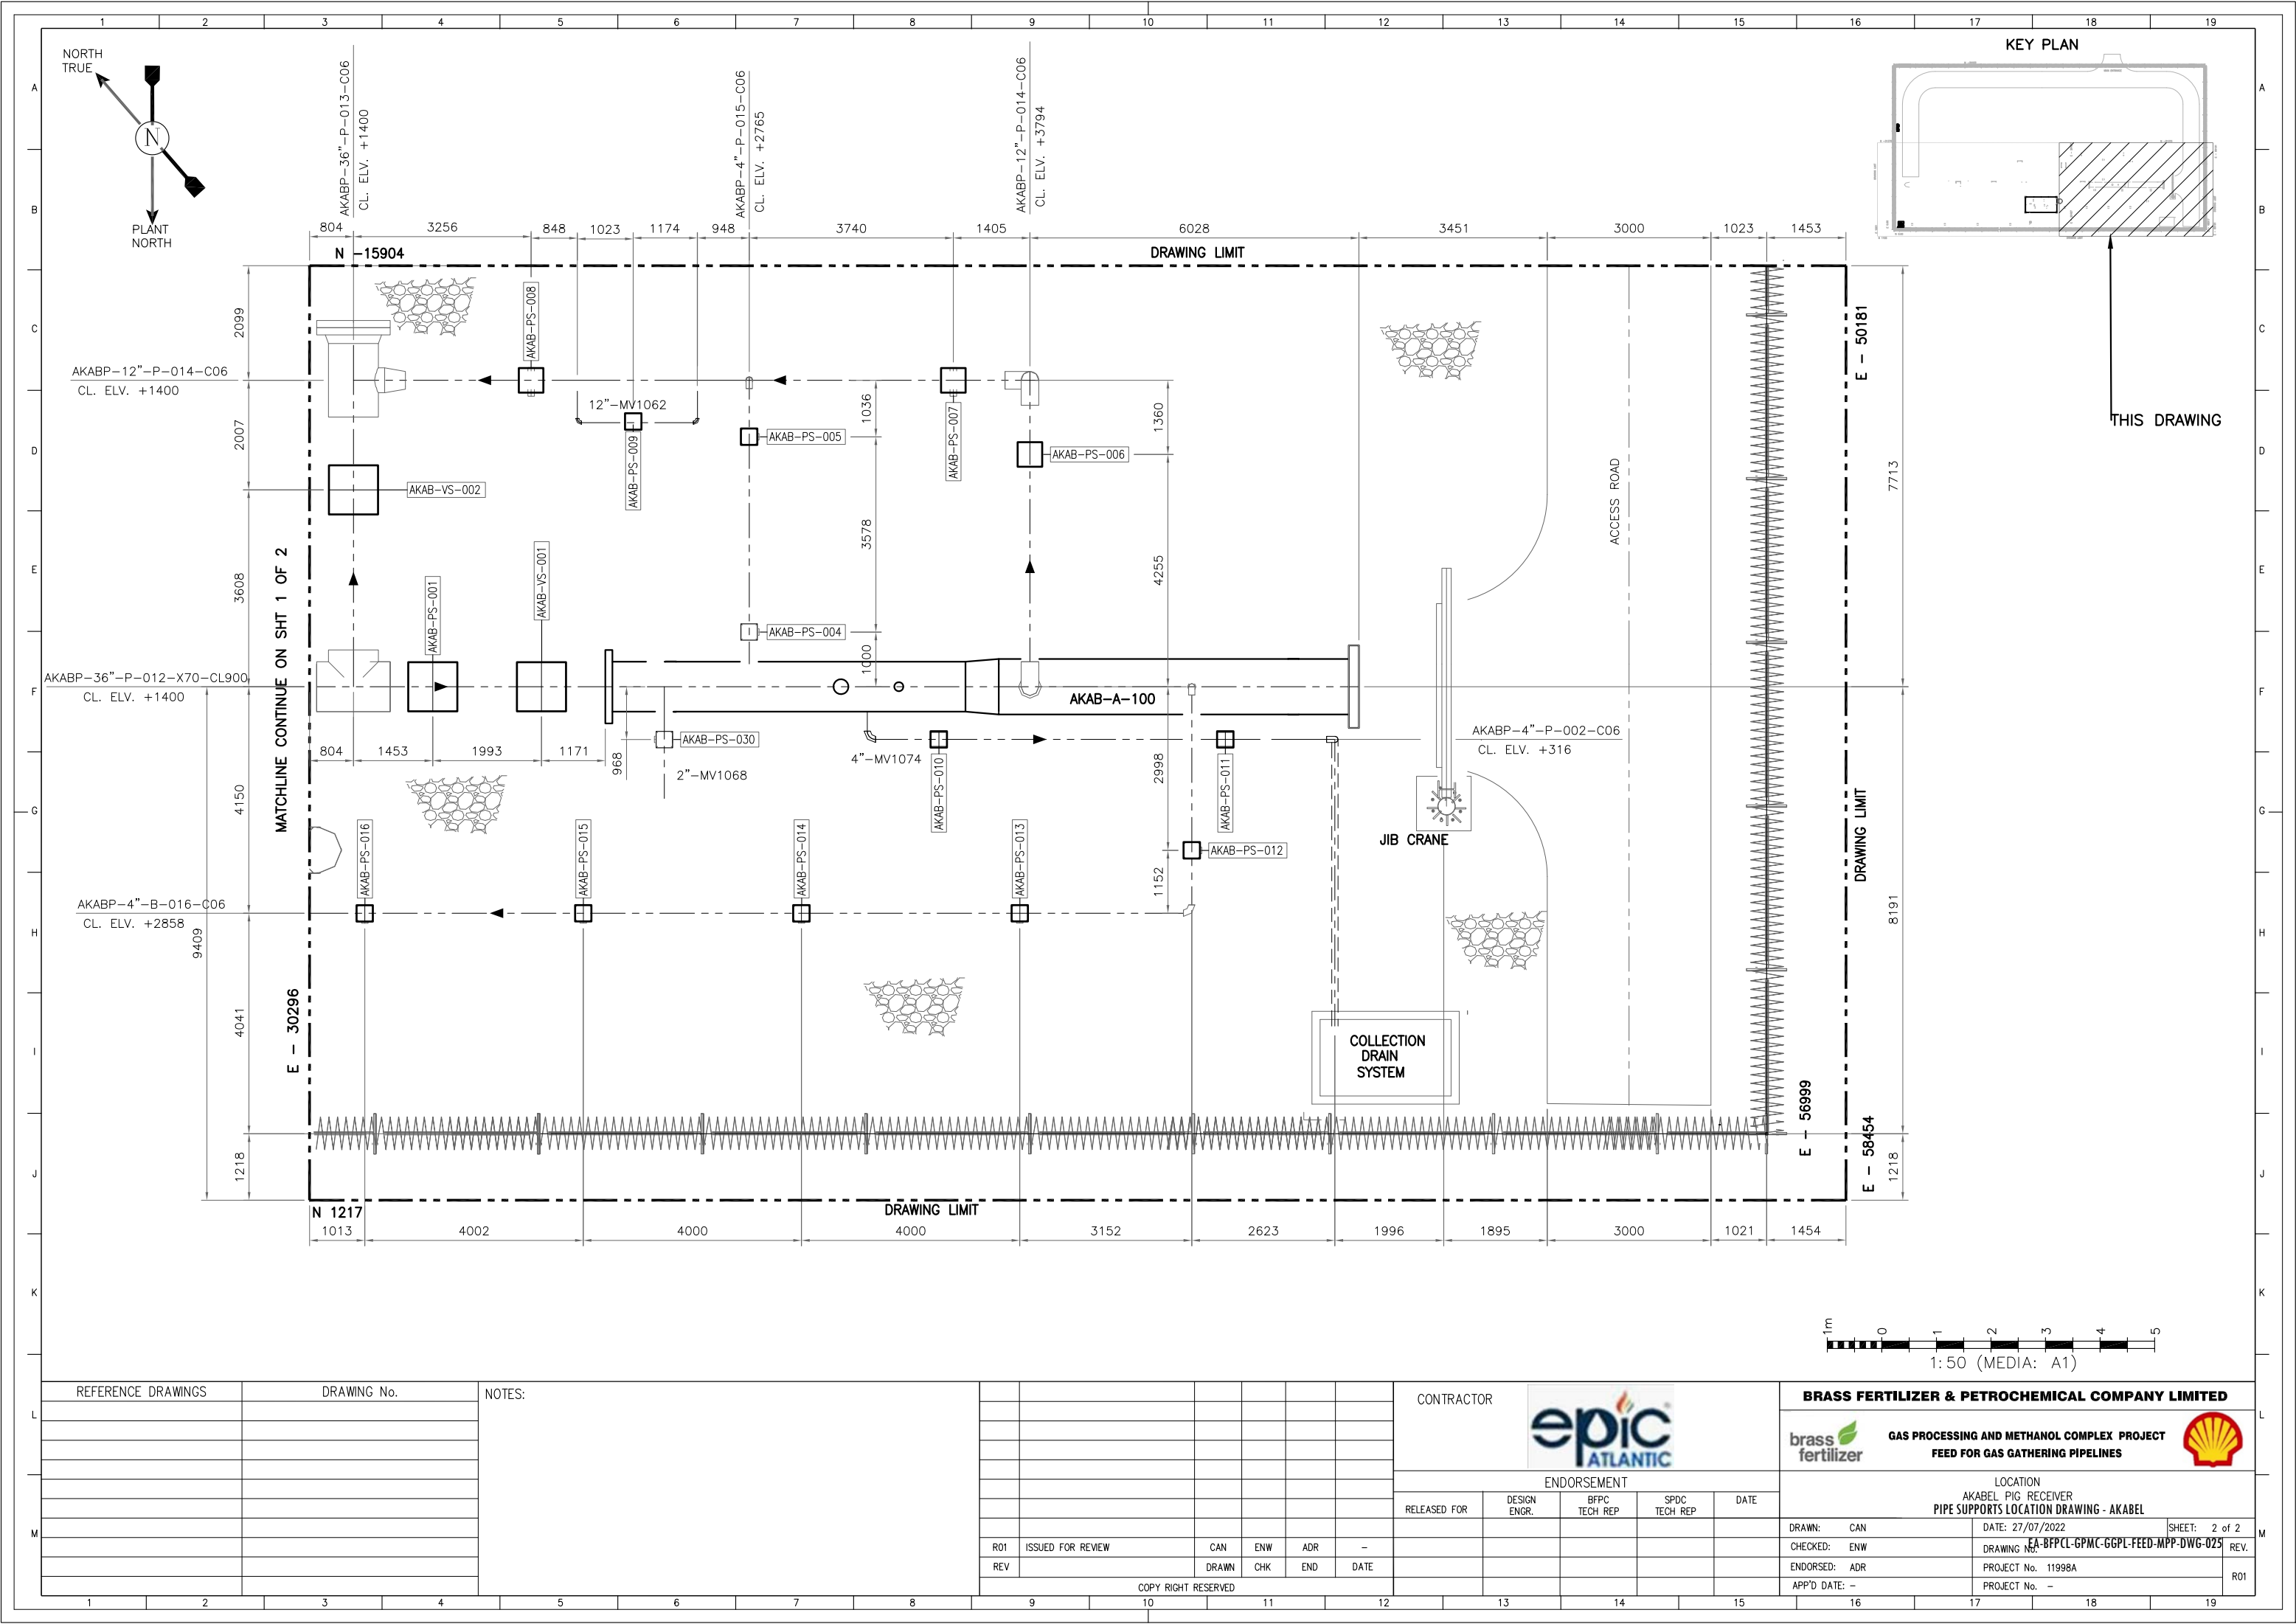

REFERENCE DRAWINGS		DRAWING No.	NOTES:							CONTRACTOR		ENDORSEMENT					BRASS FERTILIZER & PETROCHEMICAL COMPANY LIMITED		
												brass fertilizer GAS PROCESSING AND METHANOL COMPLEX PROJECT FEED FOR GAS GATHERING PIPELINES					LOCATION AKABEL PIG RECEIVER PIPE SUPPORTS LOCATION DRAWING - AKABEL		
										RELEASED FOR	DESIGN ENGR.	BFPC TECH REP	SPDC TECH REP	DATE	DRAWN: CAN		DATE: 27/07/2022	SHEET: 2 of 2	REV.
															CHECKED: ENW		DRAWING No. EA-BFPCL-GPMC-GGPL-FEED-MPP-DWG-025		
															ENDORSED: ADR		PROJECT No. 11998A		
															APP'D DATE: -		PROJECT No. -		
										COPY RIGHT RESERVED									R01