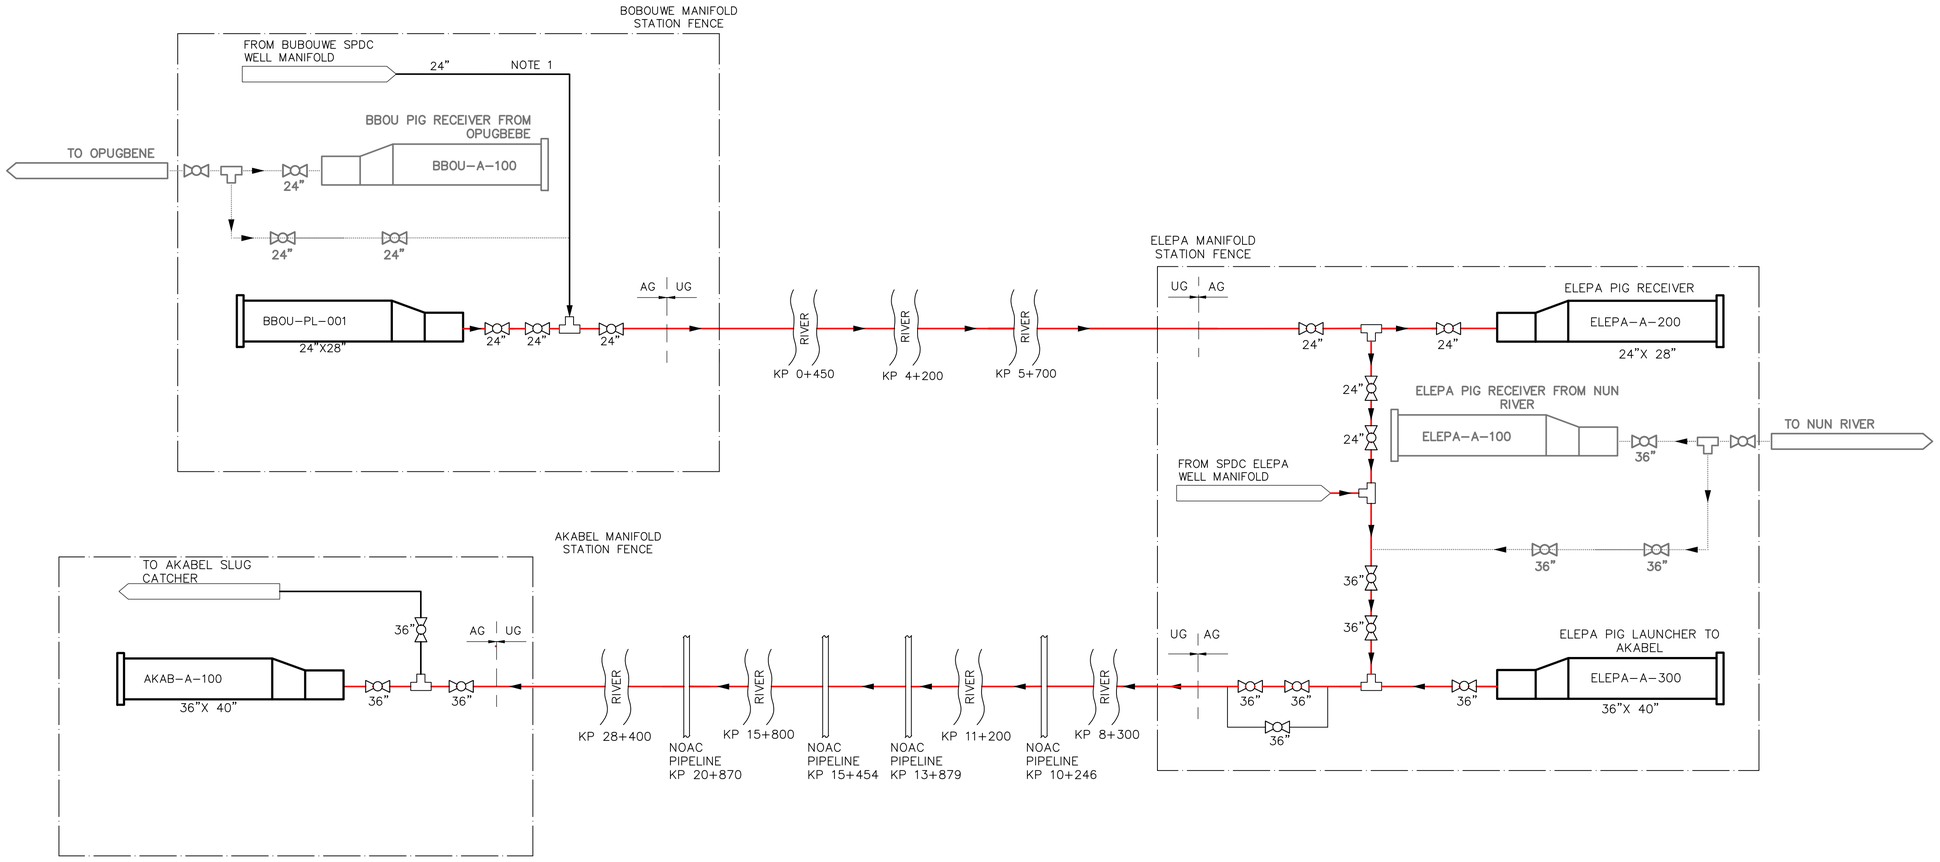

NOTE:

1. THE RIVERS CAPTURED ARE THOSE WITH WIDTH ABOVE 100m.

REFERENCE DRAWINGS		
S/N	TITLE	DRAWING NO.
1	PIPELINE ALIGNMENT SHEETS KP0:00 TO KP 38:00	EA-BFPCL-GPMC-GGPL-FEED-PPL-ALS-001 TO 038
2	TYPICAL ROW INSTALLATION- NEW ROUTE	EA-BFPCL-GPMC-GGPL-FEED-PPL-DWG-010
3	OVERALL LOCATION PLAN MAP / SATELLITE IMAGERY	EA-BFPCL-GPMC-GGPL-FEED-PPL-DWG-001
5	SPECIFICATIONS FOR LINE PIPES	EA-BFPCL-GPMC-GGPL-FEED-PPL-SPC-001
6	TYPICAL RIVER CROSSING	EA-BFPCL-GPMC-GGPL-FEED-PPL-DWG-009
7	TYPICAL GAS PIPELINE MARKER	EA-BFPCL-GPMC-GGPL-FEED-PPL-DWG-012

REFERENCE DRAWINGS	DRAWING No.

NOTES:

REV		DRAWN	CHK	END	DATE
R01	ISSUED FOR REVIEW	SIE	EN	AB	21/07/22

COPY RIGHT RESERVED

CONTRACTOR

epic ATLANTIC

ENDORSEMENT

RELEASED FOR	DESIGN ENGR.	BFPC TECH REP	SPDC TECH REP	DATE

BRASS FERTILIZER & PETROCHEMICAL COMPANY LIMITED

brass fertilizer

GAS PROCESSING AND METHANOL COMPLEX PROJECT
FEED FOR GAS GATHERING PIPELINES

LOCATION
BUBOUWE MANIFOLD STATION TO ELEPA MANIFOLD STATION TO AKABEL MANIFOLD STATION RIGHT OF WAY SCHEMATICS

DRAWN: SIE	DATE: 21/07/22	SHEET: 1 of 1	
CHECKED: EN	DRAWING No. EA-BFPCL-GPMC-GGPL-FEED-PPL-DWG-002	REV.	R01
ENDORSED: AB	PROJECT No. 11998A		
APP'D DATE: –	PROJECT No. 11998A		