
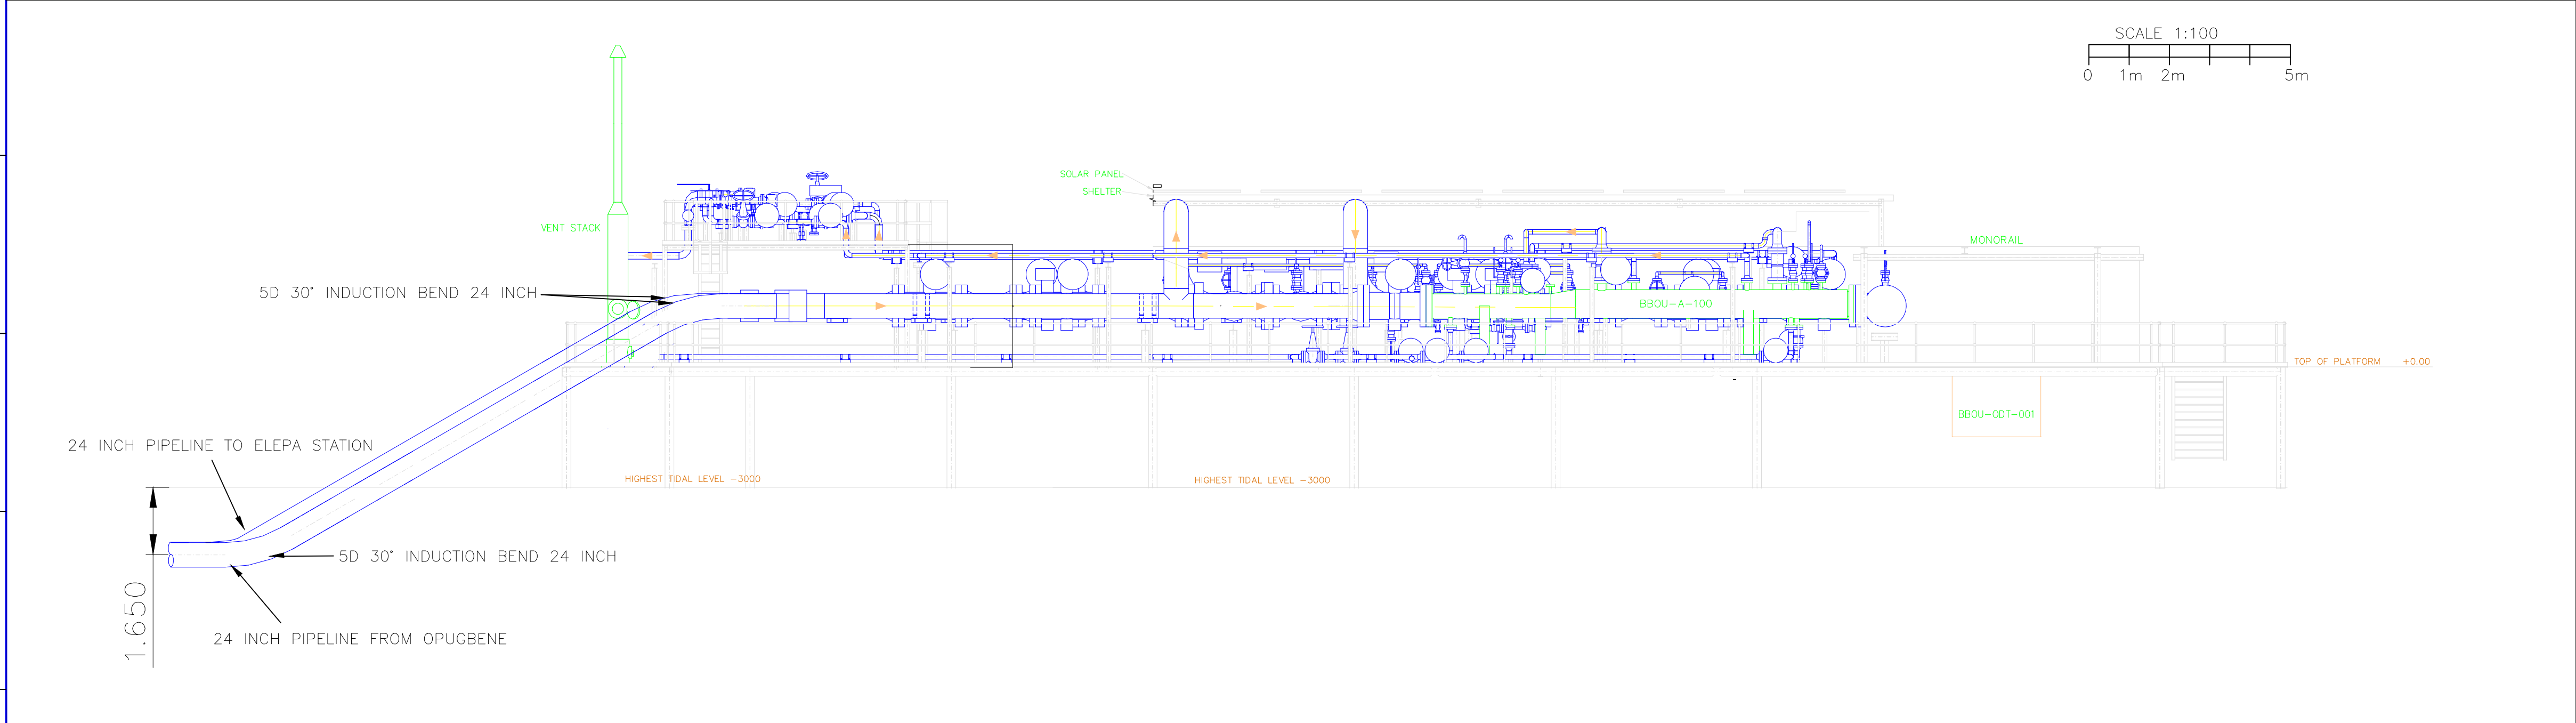
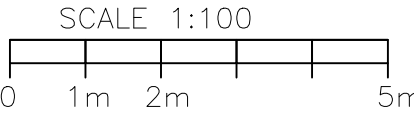
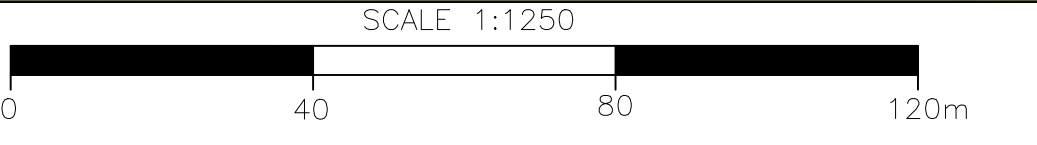
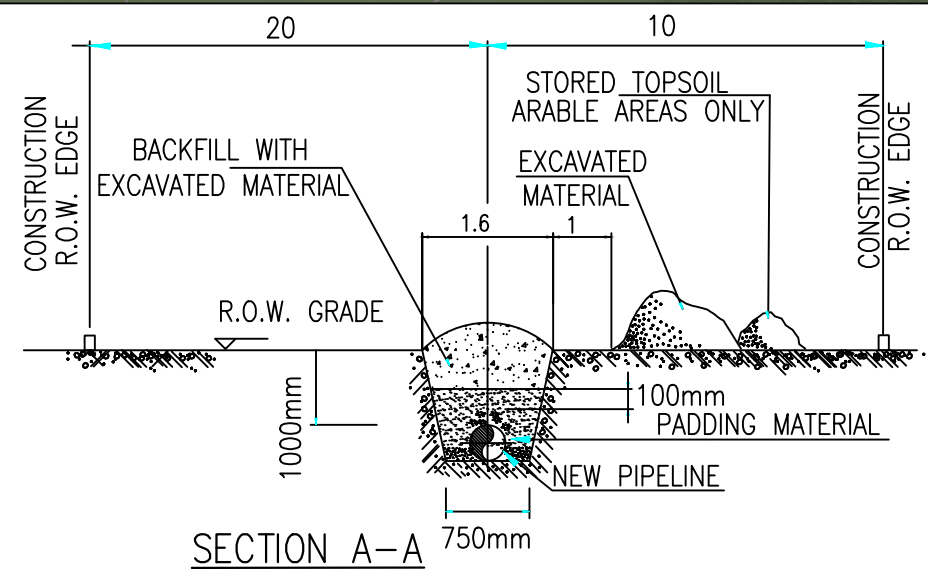


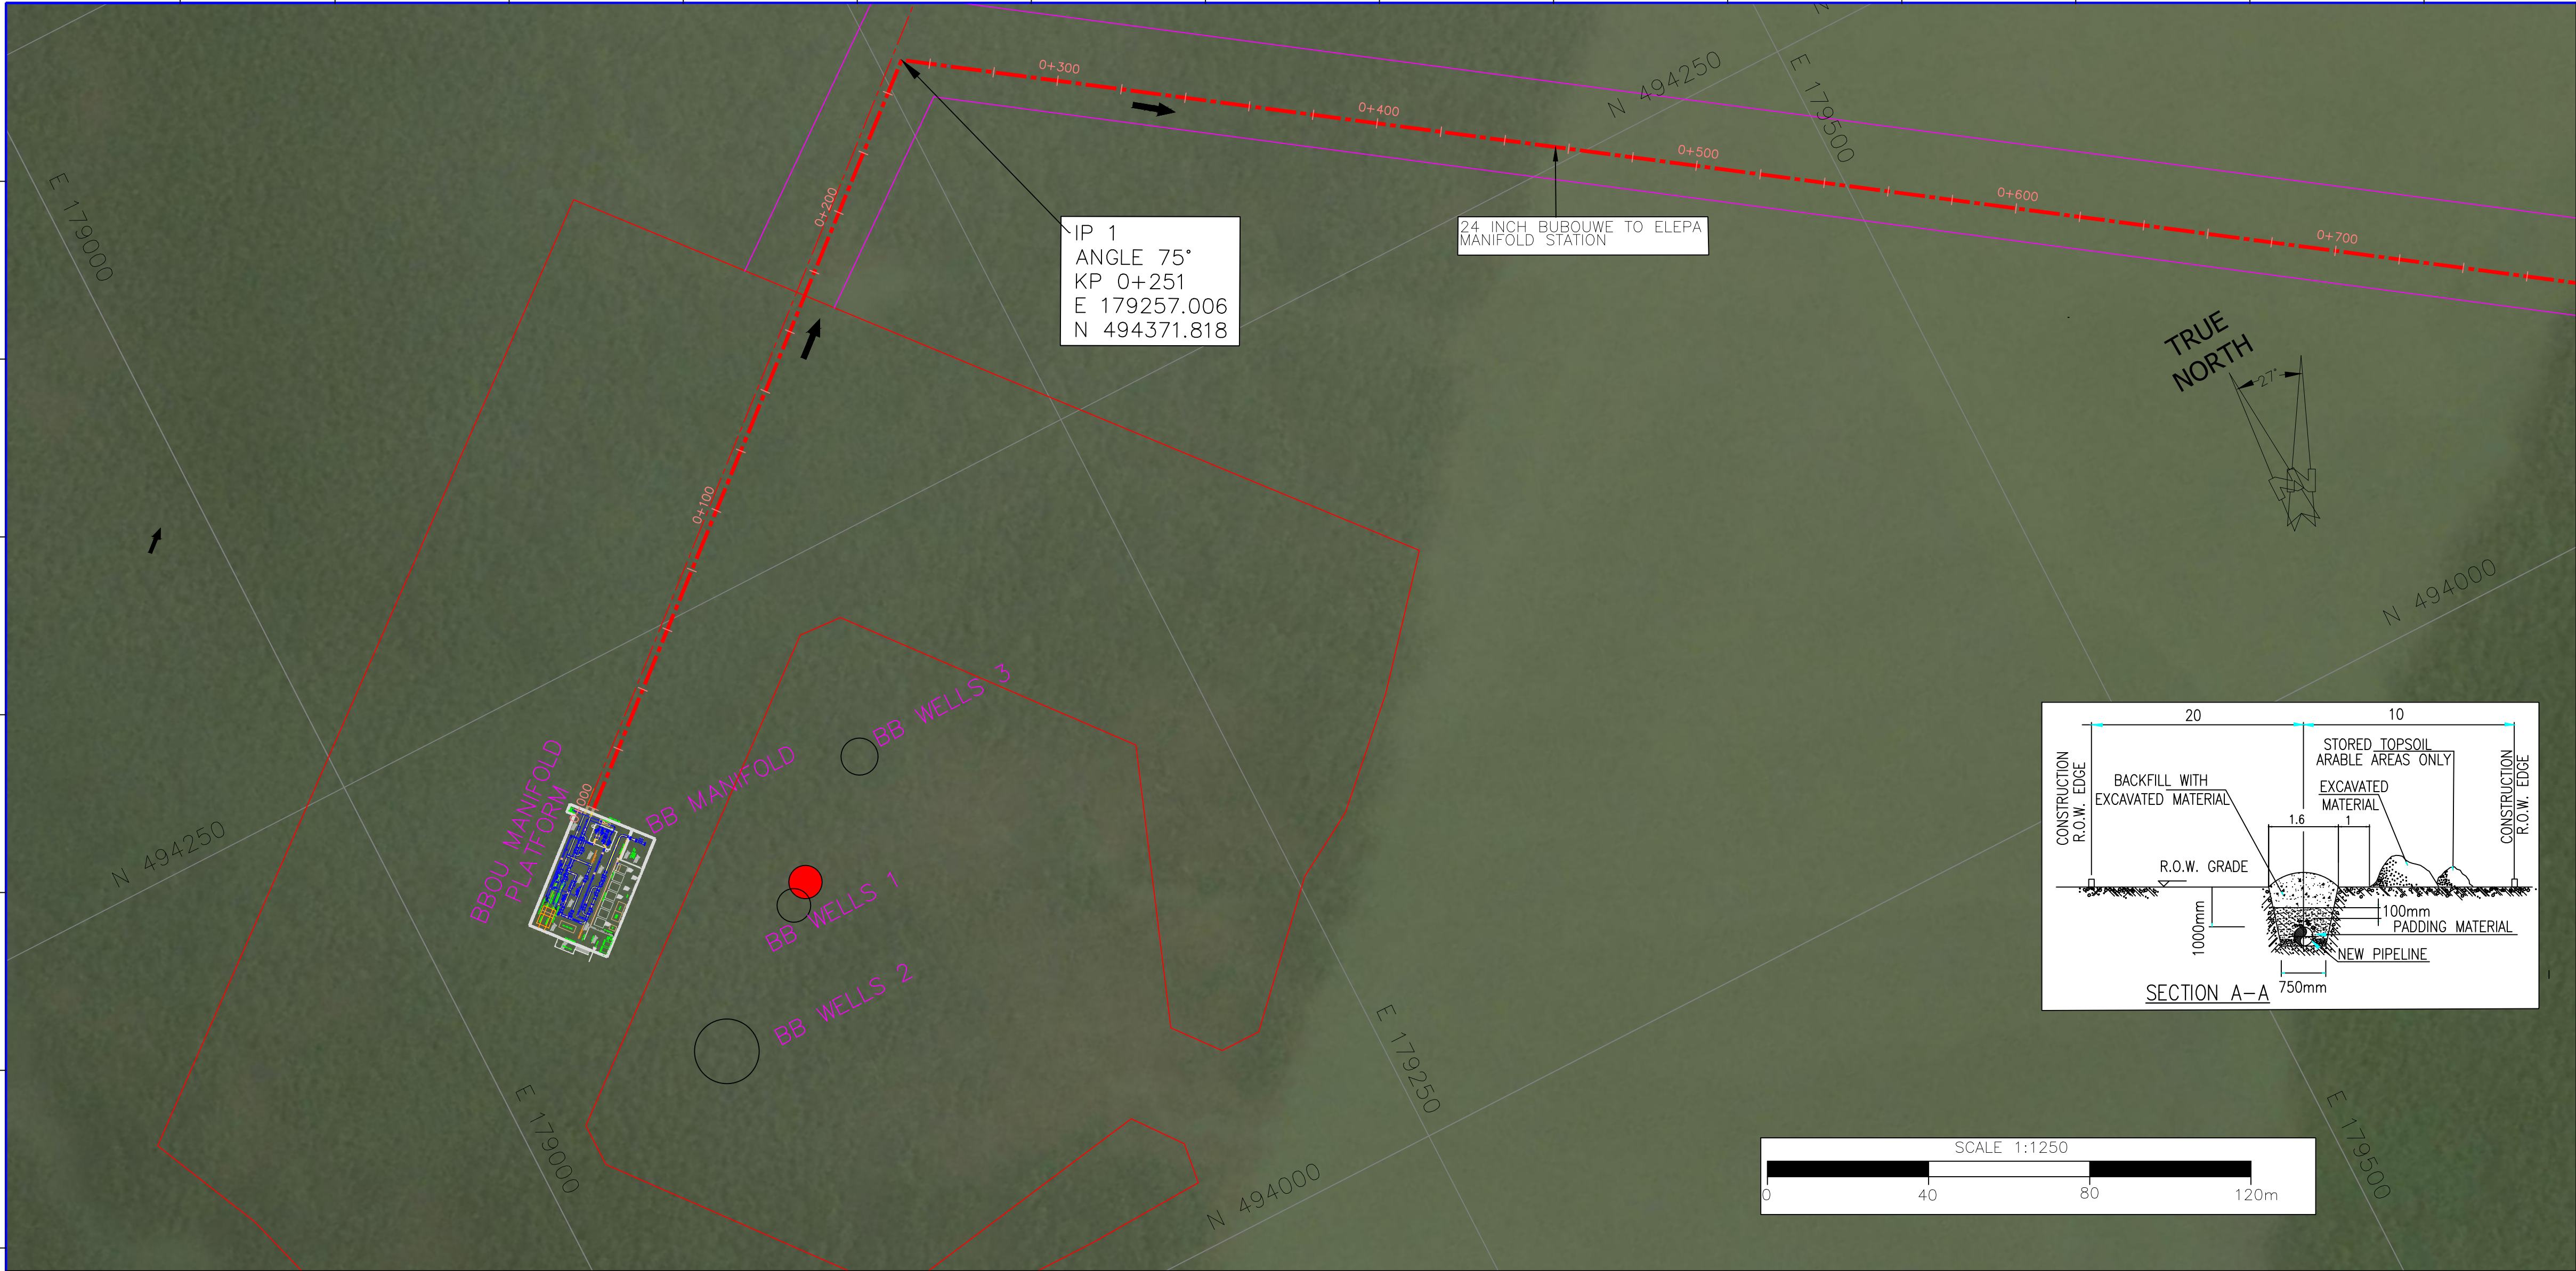

GEODATA

PROJECTION: UNIVERSAL TRANSVERSE MERCATOR (UTM)
ZONE: 32N
PARAMETERS:
CENTRAL MERIDIAN: 9°E
LATITUDE OF ORIGIN: 0.0
FALSE EASTING: 500,000
FALSE NORTHING: 0
DATUM: WGS 84

LEGEND

- NEW PIPELINE
- SPOT HEIGHT
- SURVEY PILLAR
- RECTANGULAR GRID
- GPS CONTROL
- BEARING & DISTANCE
- BOREHOLE(5.0M)
- KILOPOST (KP)
- RIVER/CREEK EDGE
- DUMP SITE
- FLOW DIRECTION
- GEOGRAPHIC GRID
- ROW LIMIT
- VEGETATION BOUNDARY
- SOUNDING
- BOREHOLE
- SOIL RESISTIVITY
- CONCRETE COATING

- NOTES
- ALL DIMENSIONS ARE IN METERS UNLESS STATED OTHERWISE..
 - FIELD JOINT COATING SHALL BE AS PER REFERENCED FJC SPECIFICATION.
 - CUT AND FILL TO BE CARRIED OUT TO REDUCE TRENCHING AND MAINTAIN LEVEL OF COVER AS SPECIFIED..
 - ALL DIMENSIONS AND COORDINATES ON THIS DRAWING SHOULD BE SITE VERIFIED PRIOR TO INSTALLATION.
 - THE SIZE OF VENT STACK IS ASSUMED PENDING AVAILABILITY OF DATE FROM PROCESS.

KEYMAP



REFERENCE DRAWINGS

S/N	TITLE	DRAWING NO.
1	EQUIPMENT LAYOUT - BUBOUWE	EA-BFPCL-GPMC-GGPL-FEED-MPP-DWG-006
2	PIPING GENERAL ARRANGEMENT DRAWING - BUBOUWE	EA-BFPCL-GPMC-GGPL-FEED-MPP-DWG-015
3	TYPICAL ROW INSTALLATION- NEW ROUTE	EA-BFPCL-GPMC-GGPL-FEED-PPL-DWG-010
4	OVERALL LOCATION PLAN MAP / SATELLITE IMAGERY	EA-BFPCL-GPMC-GGPL-FEED-PPL-DWG-001
5	PIPELINE CONSTRUCTION AND HDD INSTALLATION SPECIFICATION.	EA-BFPCL-GPMC-GGPL-FEED-PPL-SPC-009
6	KEY PLAN - BUBOUWE	EA-BFPCL-GPMC-GGPL-FEED-MPP-DWG-018
7	BASIS OF DESIGN DOCUMENT	EA-BFPCL-GPMC-GGPL-FEED-GEN-RPT-002
8	PIPELINE ALIGNMENT SHEET KP 0:00 TO KP 1:00	EA-BFPCL-GPMC-GGPL-FEED-PPL-ALS-001
9	PROCESS ENGINEERING FLOW SHEETS 1 TO 8	EA-BFPCL-GPMC-GGPL-FEED-PSE-DWG-003

REFERENCE DRAWINGS	DRAWING No.	NOTES:	CONTRACTOR	ENDORSEMENT	BRASS FERTILIZER & PETROCHEMICAL COMPANY LIMITED
			epic ATLANTIC		GAS PROCESSING AND METHANOL COMPLEX PROJECT FEED FOR GAS GATHERING PIPELINES
				RELEASED FOR	LOCATION BUBOUWE MANIFOLD STATION PIPELINE DEPARTURE DRAWING-BUBOUWE
				DESIGN ENGR.	DRAWN: SIE
				BFPC TECH REP	DATE: 26/07/22
				SPDC TECH REP	SHEET: 1 of 1
				DATE	CHECKED: EN
					DRAWING No. EA-BFPCL-GPMC-GGPL-FEED-PPL-DWG-003
					PROJECT No. 11998A
					APP'D DATE: -
					PROJECT No. 11998A
					REV. R01