
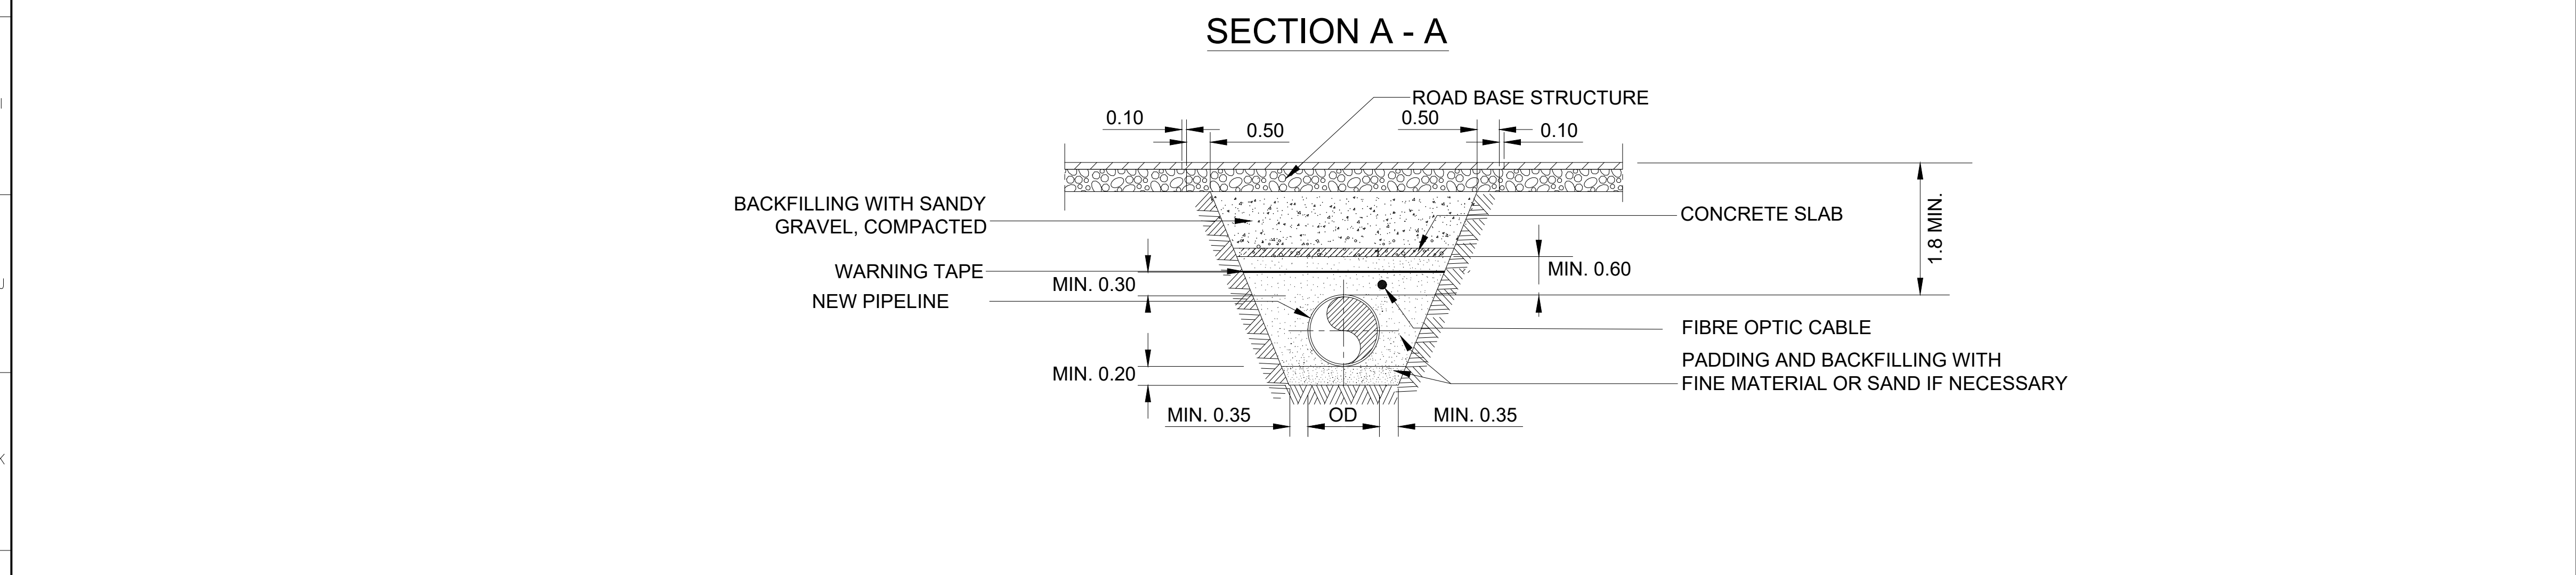
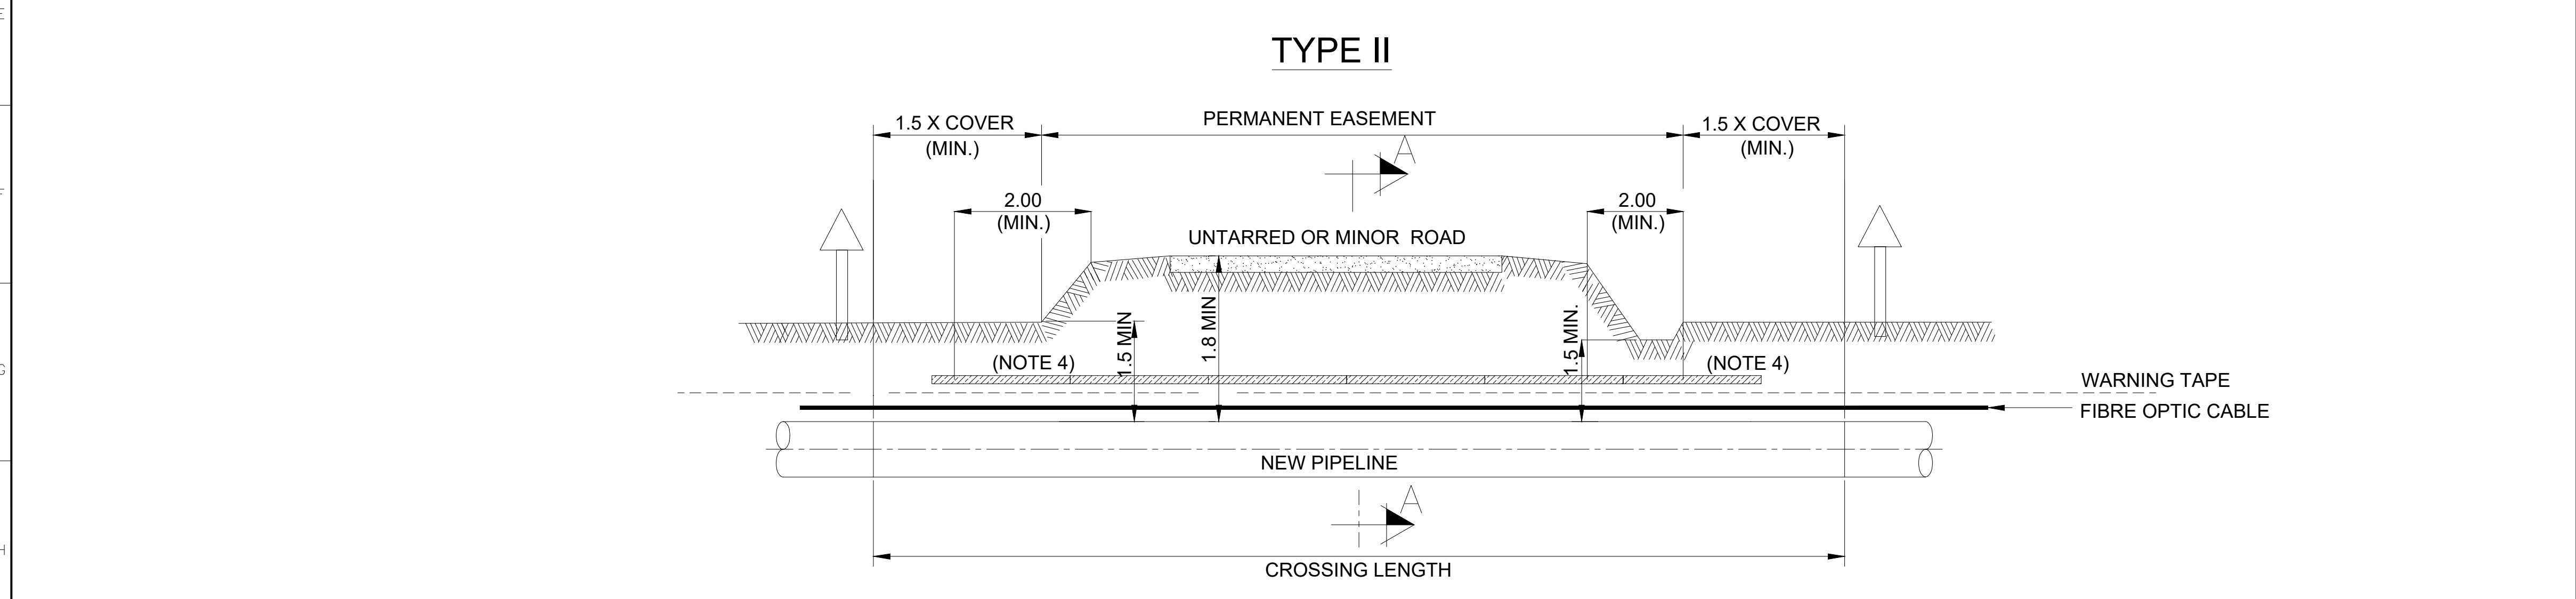
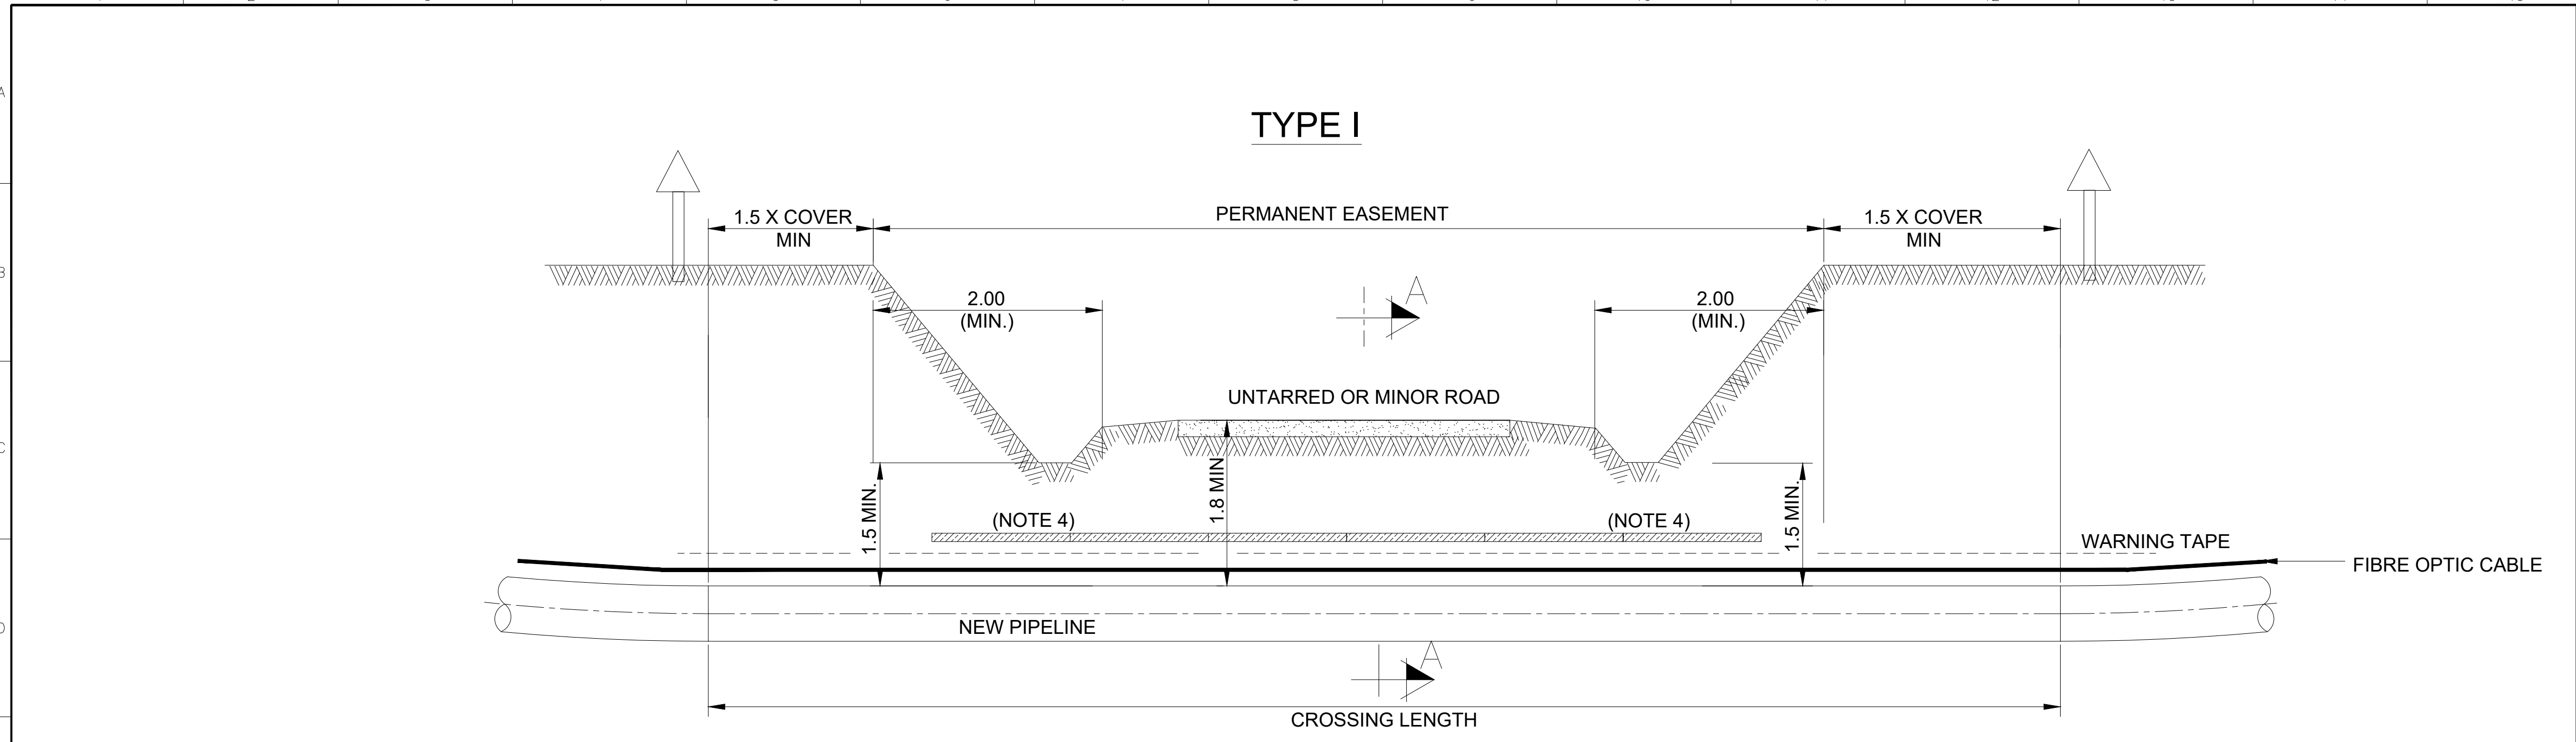


 

- NOTES:**
- ALL DIMENSIONS IN METERS, UNLESS OTHERWISE NOTED.
 - BACKFILLING AND COMPACTION OF THE MATERIAL MUST BE CARRIED OUT IN LAYERS OF 20 cm EACH. THE UPPER EDGE OF TRENCH IS TO BE CUT BACK BEFORE RE-INSTATEMENT. RE-INSTATEMENT IS DONE BY BACKFILLING TO THE FULL HEIGHT. AFTER THE FINAL TOP LAYER IS CONSTRUCTED.
 - ROADS AND SURROUNDING AREA TO BE RETURNED TO ITS ORIGINAL CONDITION.
 - PROTECTION WITH CONCRETE SLAB AS REQUIRED.
 - CROSSING ANGLE SHOULD IDEALLY BE 90° BUT IN NO CASE SHALL IT BE LESS THAN 45°.
 - PIPELINE MARKER TO BE INSTALLED ON BOTH SIDE OF THE ROAD.
 - THE ROAD BASE STRUCTURE MAY VARY FOR DIFFERENT LOCATIONS. TO BE REINSTATED TO THE ORIGINAL CONDITION.
 - THE SLOPE OF THE TRENCH SHALL BE ADJUSTED ACCORDING TO THE SOIL CHARACTERISTICS AND THE RELEVANT STABILITY BEHAVIOR.
 - BACKFILLING AND COMPACTION OF THE TRENCHES SHALL BE CARRIED OUT USING THE OPTIMUM MOISTURE CONTENT (OMC) AND RELATIVE DENSITY OF THE SOIL.

REFERENCE DRAWINGS		DRAWING No.	NOTES:							CONTRACTOR					BRASS FERTILIZER & PETROCHEMICAL COMPANY LIMITED				
															 GAS PROCESSING AND METHANOL COMPLEX PROJECT  FEED FOR GAS GATHERING PIPELINES				
										ENDORSEMENT					LOCATION				
										RELEASED FOR					BOU MANIFOLD, ELEPA MANIFOLD STATION AND AKABEL STATION TYPICAL MINOR AND UNTARRED ROAD CROSSING				
										DESIGN ENGR.									
										BFPC TECH REP									
										SPDC TECH REP									
										DATE									
										-					DRAWN: SIE				
										-					DATE: 28/05/22				
									-					SHEET: 1 of 1					
									R01 ISSUED FOR REVIEW					DRAWING No. EA-BFPCL-GPMC-GGPL-FEED-PPL-DWG-005					
									SIE EN AB 28/05/22					CHECKED: EN					
									REV					PROJECT No. 11998A					
									DRAWN CHK END DATE					ENDORSED: AB					
														PROJECT No. 11998A					
									COPY RIGHT RESERVED					APP'D DATE: -					
														PROJECT No. 11998A					
														0					