



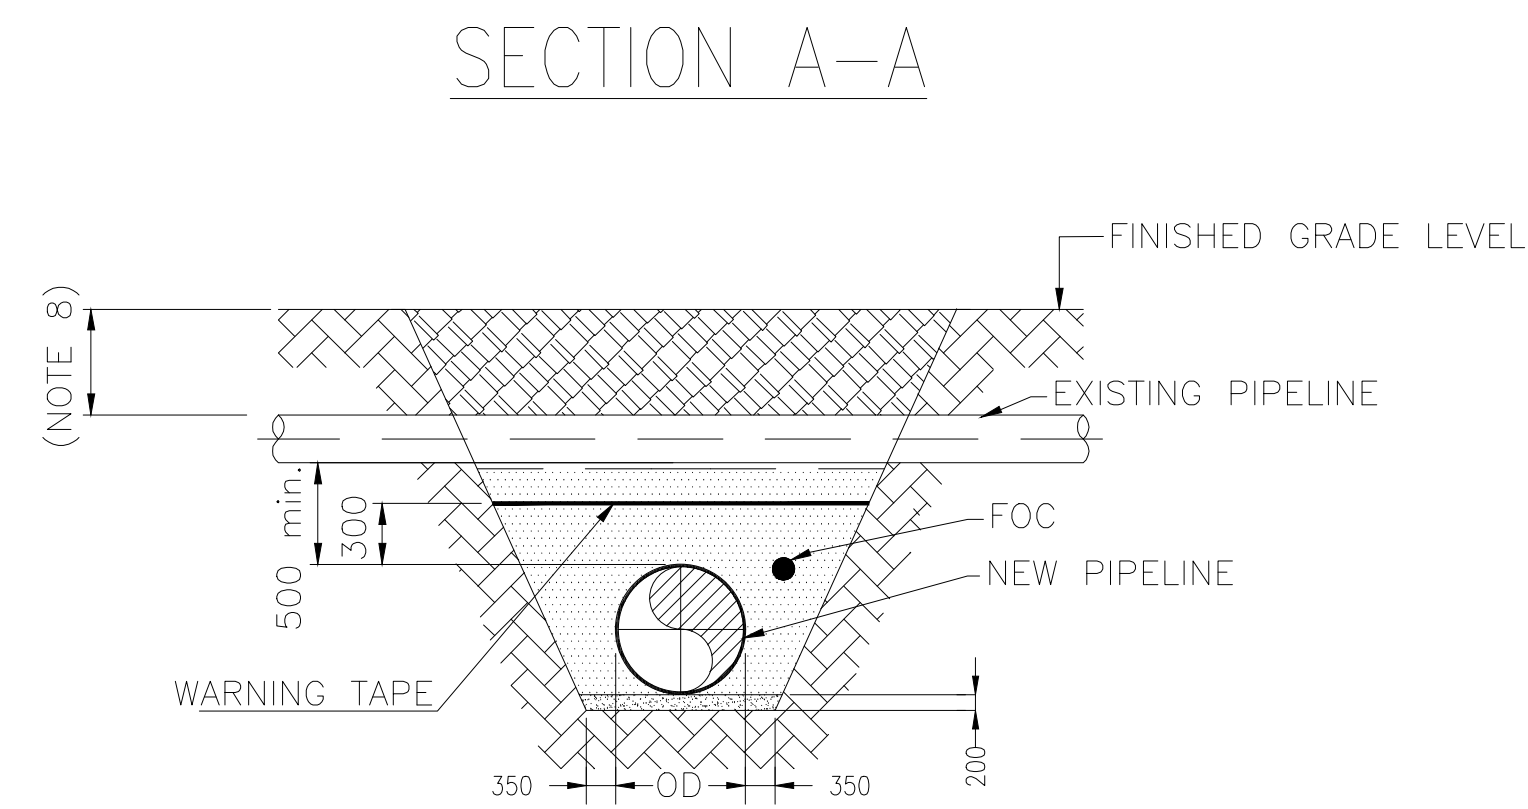

SECTION B-B

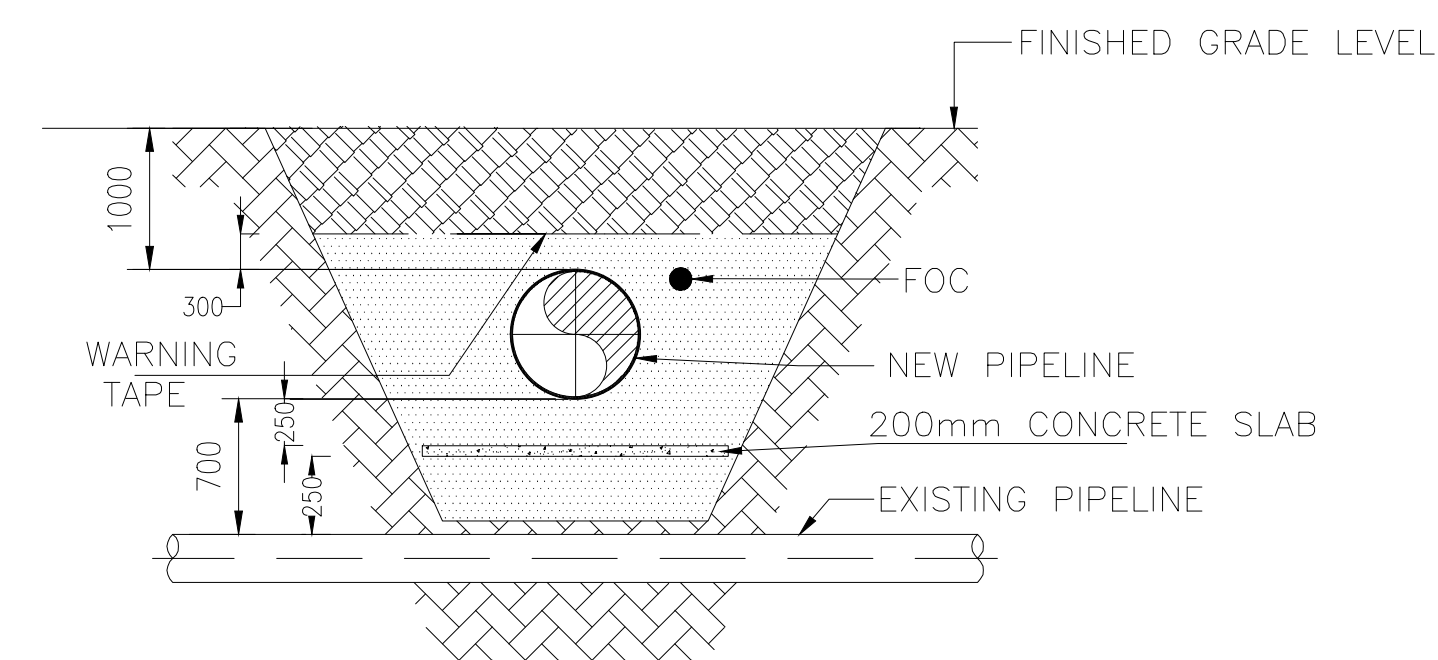

NEW PIPELINE CROSSING OVER A EXISTING PIPELINE

[illegible]