



LONGITUDINAL SECTION

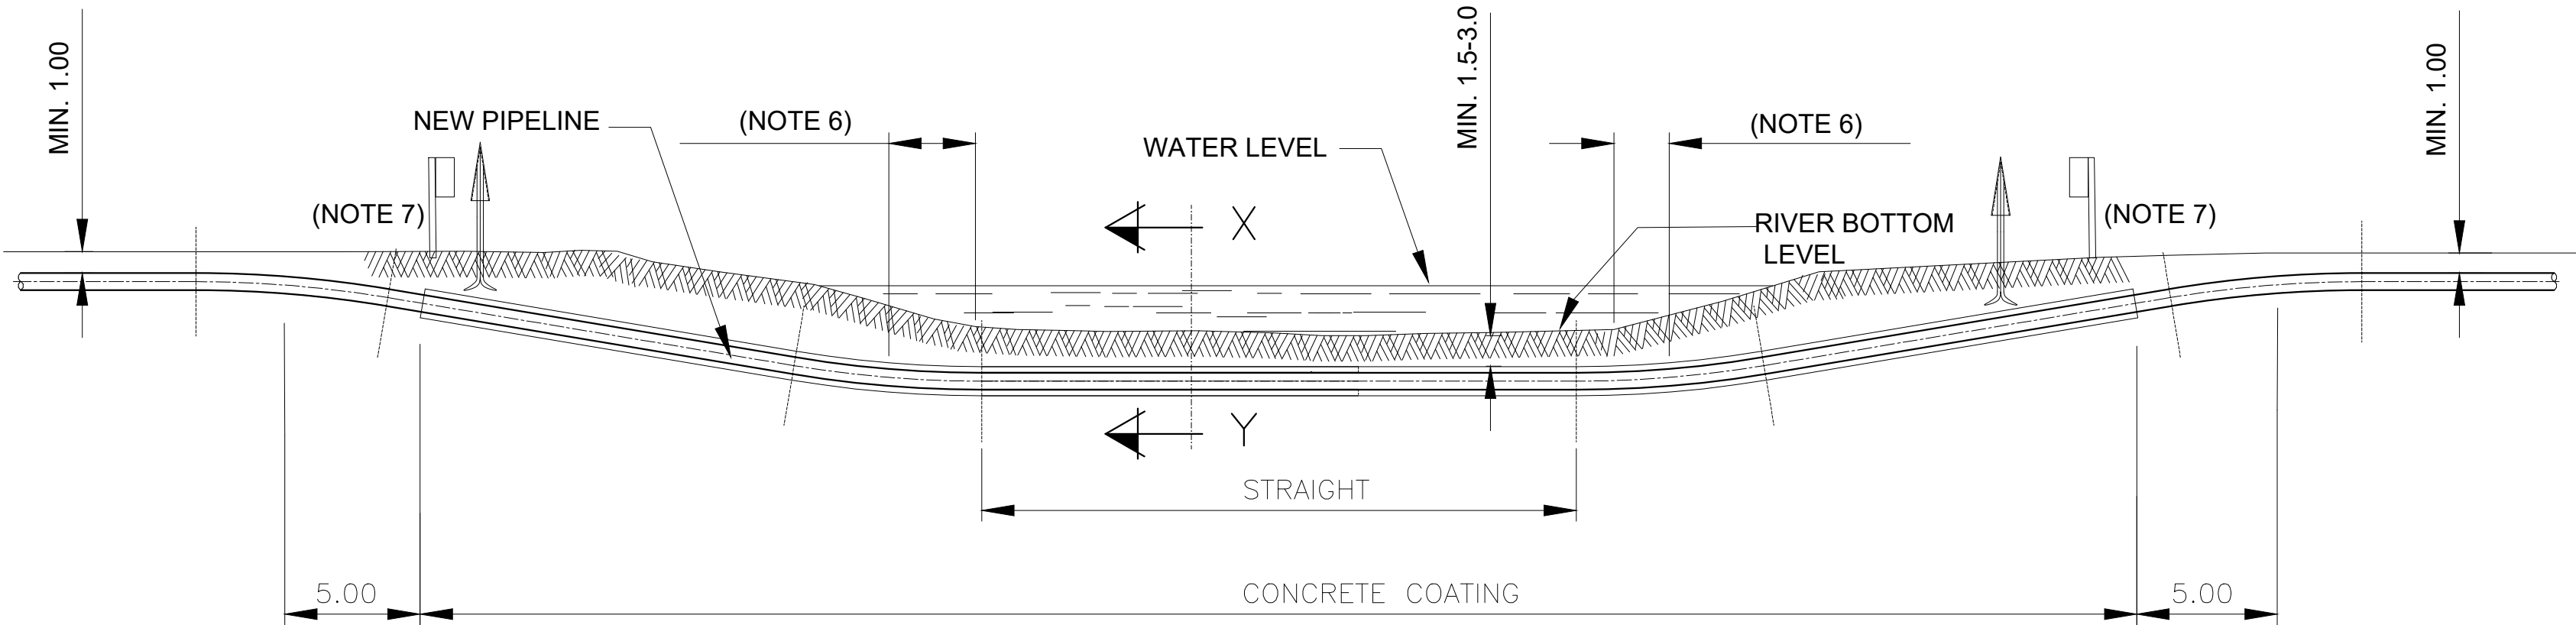


CROSS SECTION X - Y

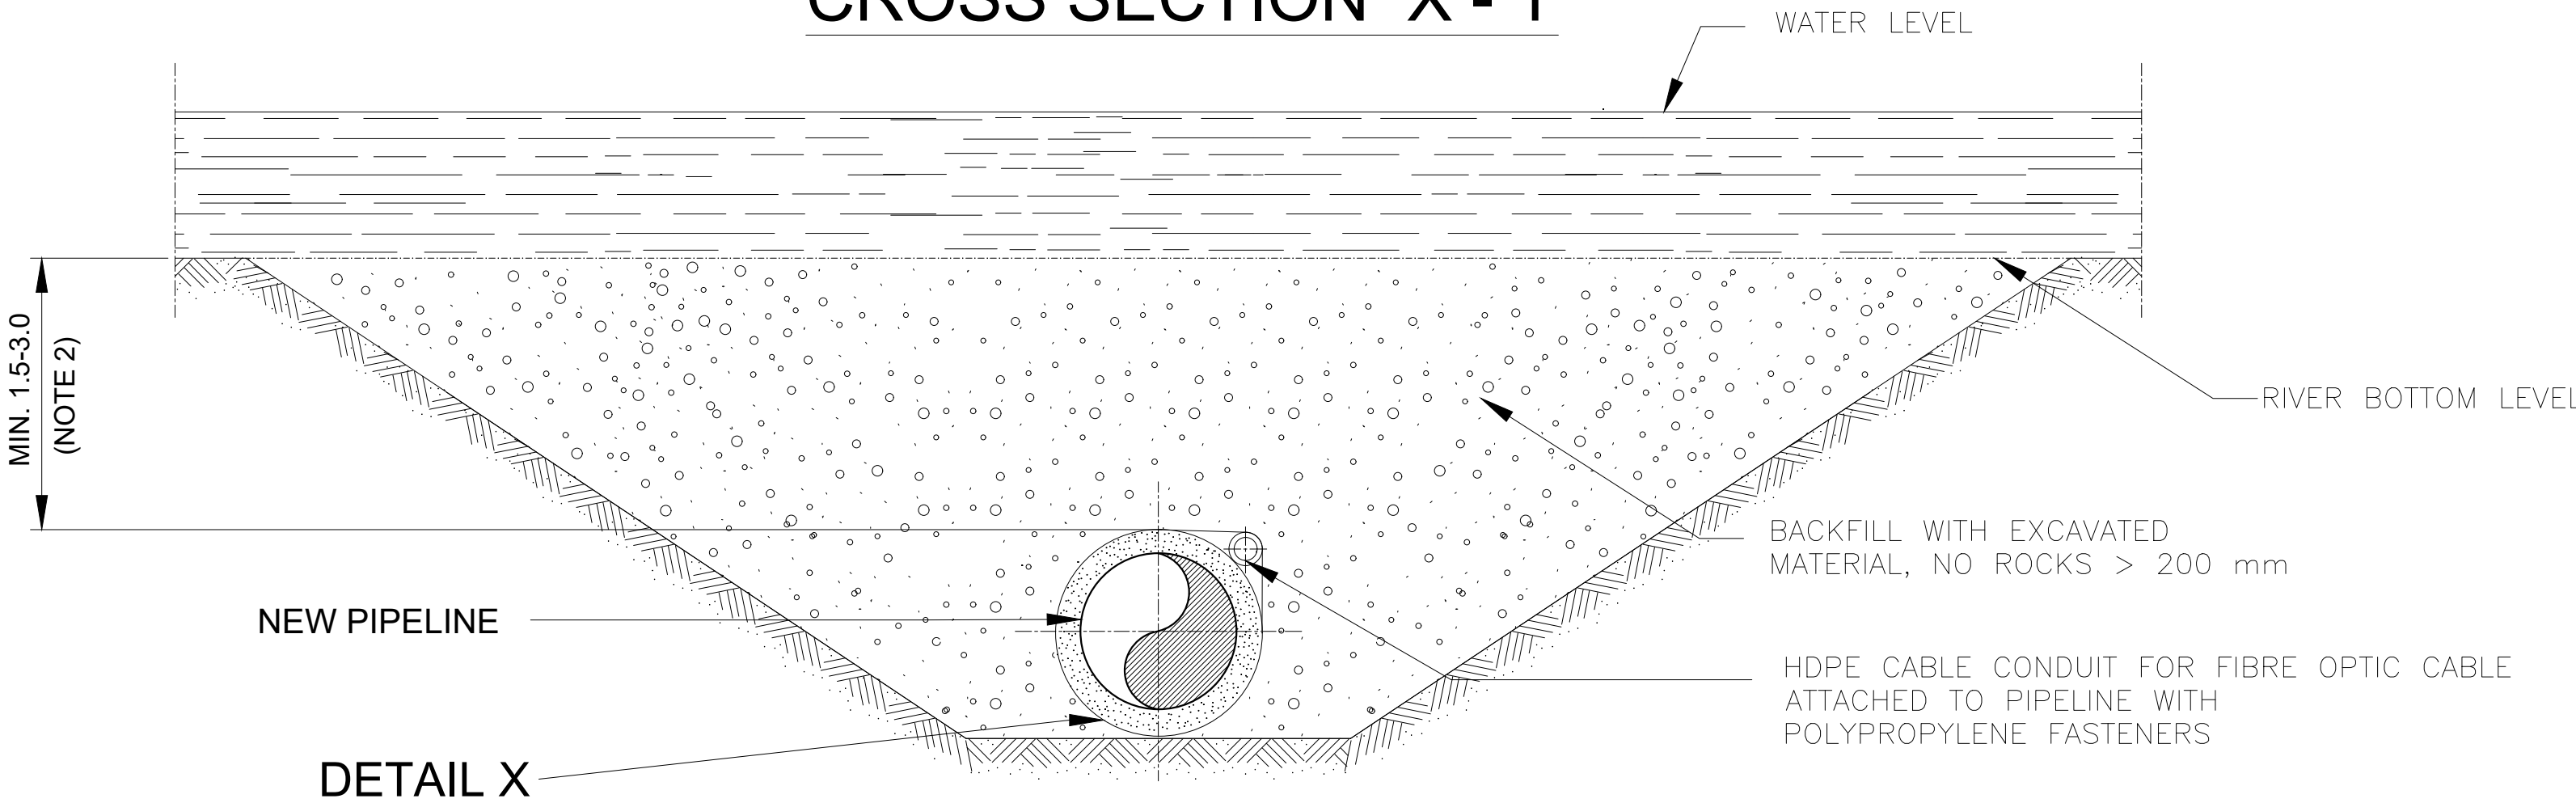

DETAIL X

CONCRETE COATING

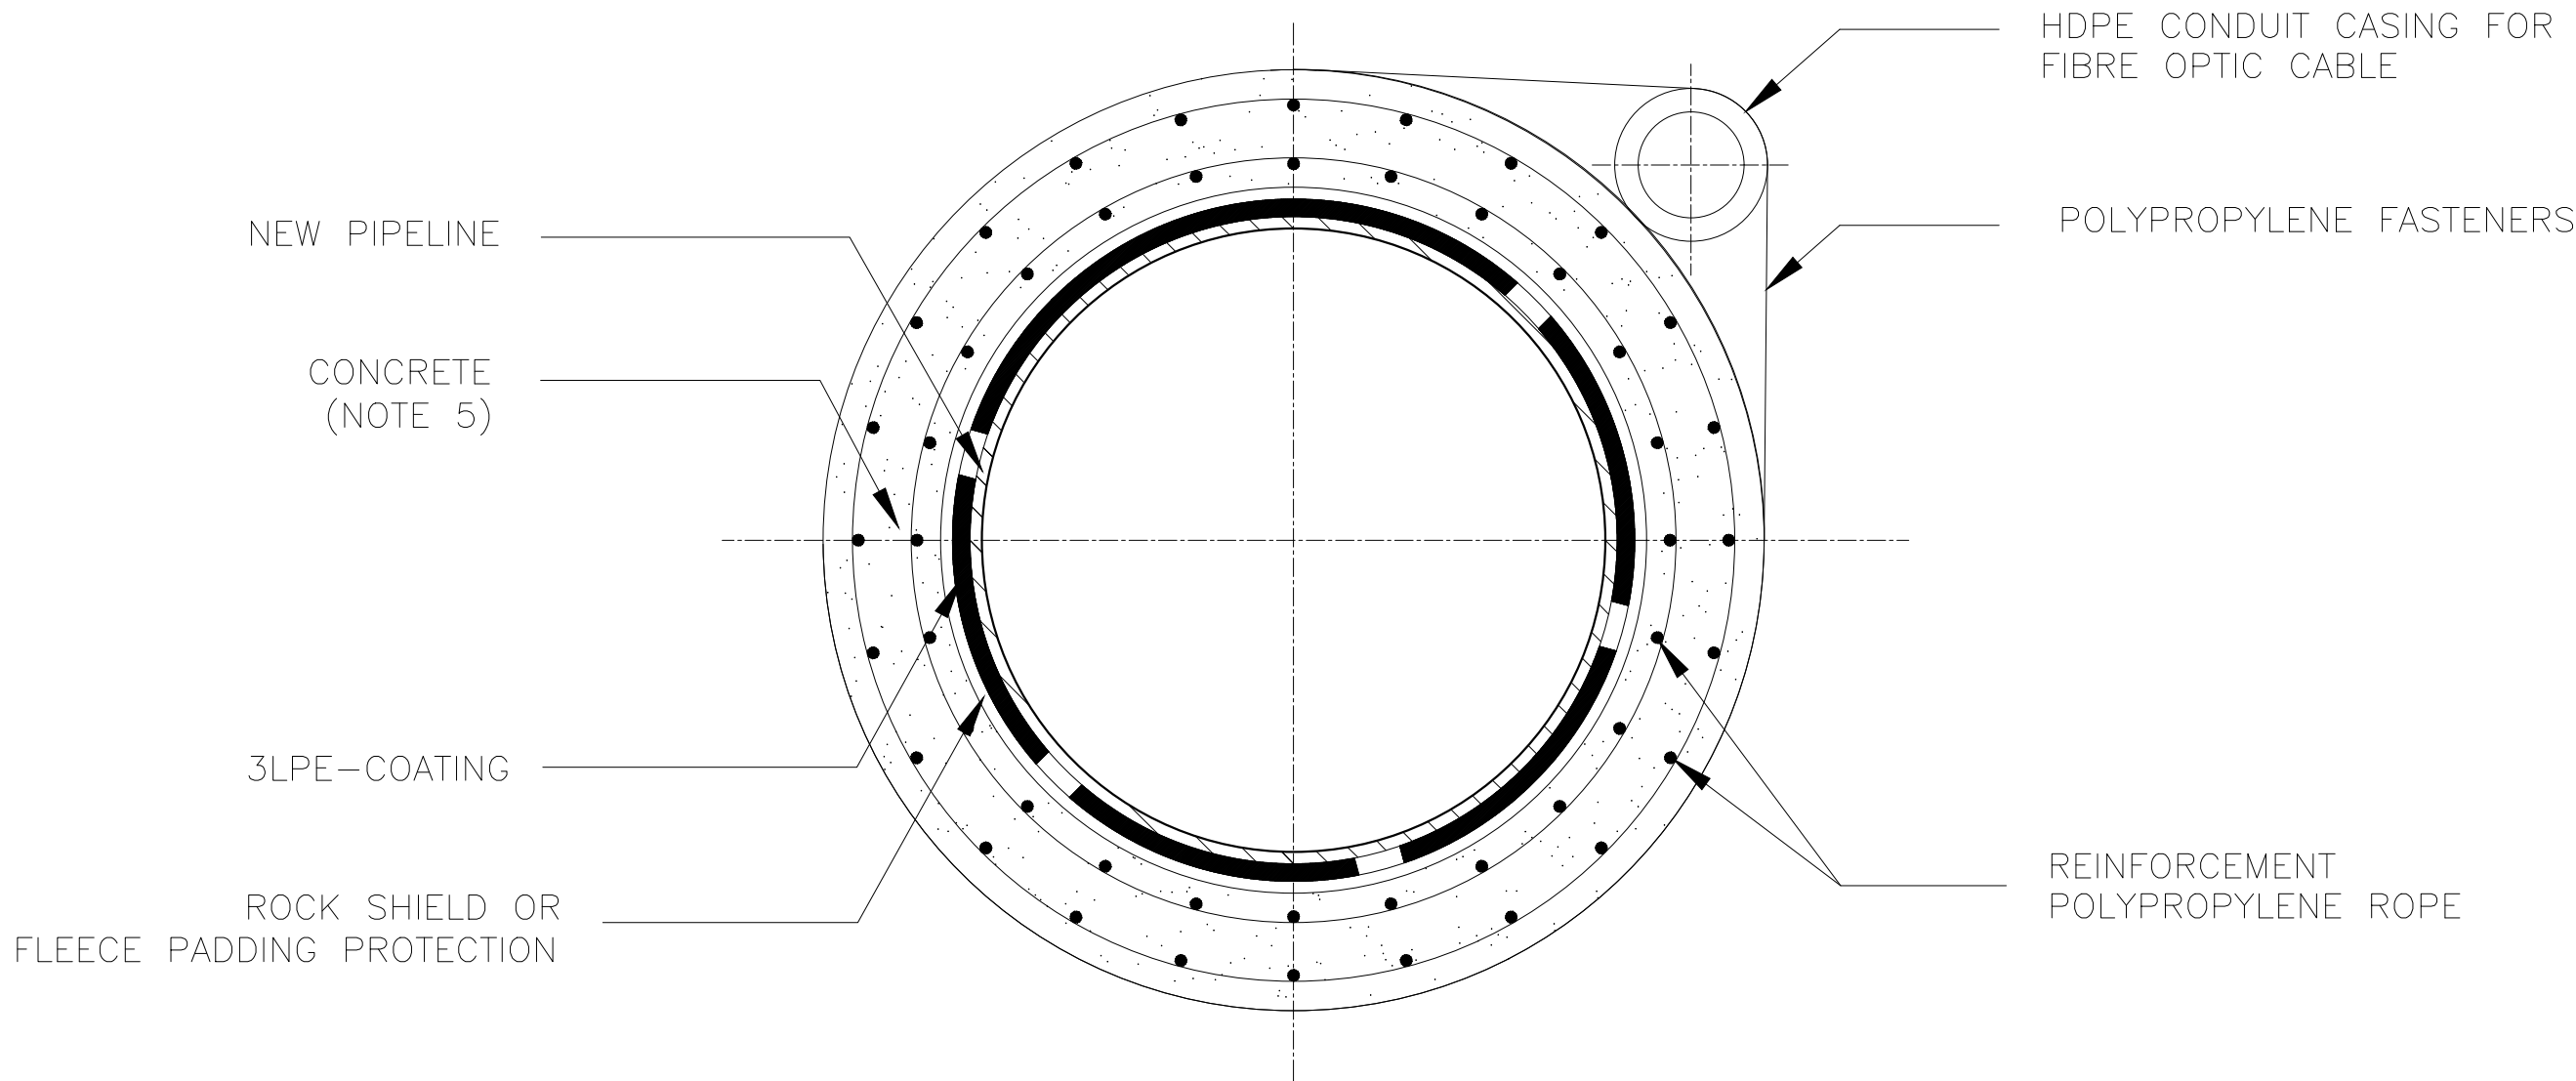

NOTES:

1. ALL DIMENSIONS ARE IN METERS UNLESS STATED OTHERWISE.
2. MINIMUM COVER IN ACCORDANCE WITH RIVER CLASSIFICATION 1.5 – 3.0 m.
3. THE RE-INSTATEMENT OF THE EMBANKMENTS AND THE RIVER BED HAS TO TAKE PLACE IN SUCH A MANNER THAT THE UNHINDERED DISCHARGE OF THE WATER AND STABILITY OF THE EMBANKMENT ARE ENSURED.
4. THE ENTIRE BANK AREA AFFECTED BY THE WORKING STRIP IS TO BE RE-INSTATED APPROPRIATELY. PROTECTION UPSTREAM AND DOWNSTREAM OF THE AFFECTED EMBANKMENT SHALL BE DONE AT LEAST ON THE ENTIRE WIDTH OF THE WORKING STRIP.
5. THICKNESS AND REINFORCEMENT ACCORDING TO CONCRETE COATING SPECIFICATION.
6. CONCRETE COATING TO EXTEND FULL WIDTH OF FLOOD PLAIN.
7. PIPELINE MARKER AND CP TEST POST TO BE INSTALLED ON BOTH SIDE OF RIVER CROSSING.
8. CROSSING ANGLE SHALL BE IDEALLY RECTANGULAR AND SHALL USUALLY NOT BE LESSER THAN 60°.

[illegible]