


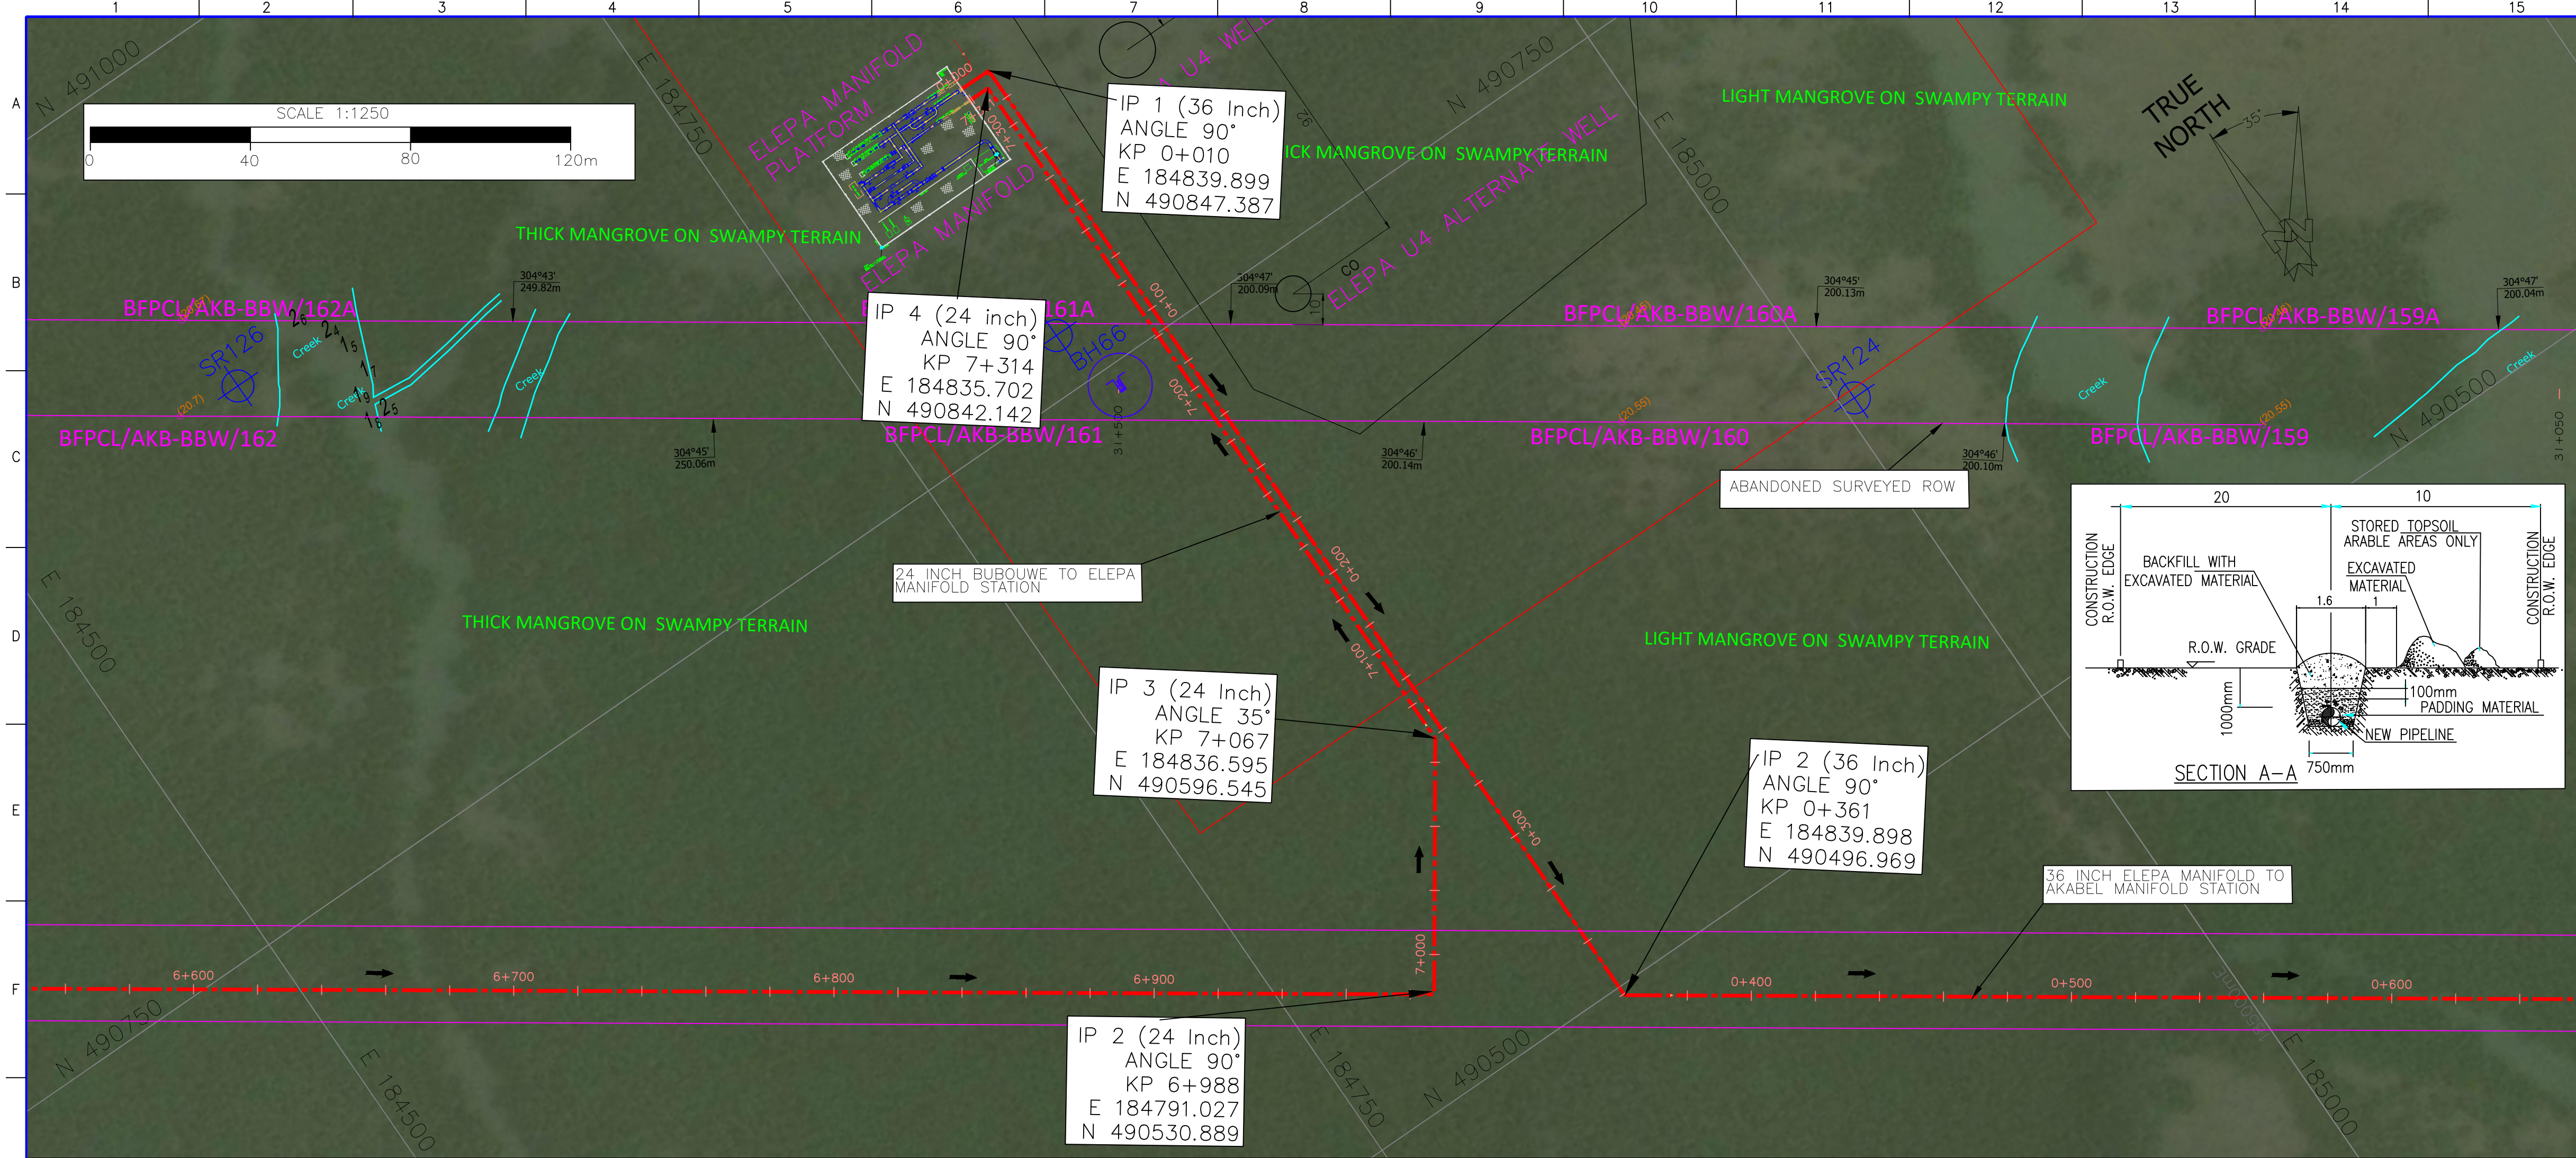

GEODATA

PROJECTION: UNIVERSAL TRANSVERSE MERCATOR (UTM)
ZONE: 32N
PARAMETERS:
CENTRAL MERIDIAN: 9°E
LATITUDE OF ORIGIN: 0.0
FALSE EASTING: 500,000
FALSE NORTHING: 0
DATUM: WGS 84

LEGEND

NEW PIPELINE

SPOT HEIGHT

SURVEY PILLAR

RECTANGULAR GRID

GPS CONTROL

BEARING & DISTANCE

BOREHOLE(5.0M)

KILOPOST (KP)

RIVER/CREEK EDGE

DUMP SITE

FLOW DIRECTION

GEOGRAPHIC GRID

ROW LIMIT

VEGETATION BOUNDARY

SOUNDING

BOREHOLE


SOIL RESISTIVITY

CONCRETE COATING

NOTES

1. ALL DIMENSIONS ARE IN METERS UNLESS STATED OTHERWISE..
2. FIELD JOINT COATING SHALL BE AS PER REFERENCED FUC SPECIFICATION.
3. CUT AND FILL TO BE CARRIED OUT TO REDUCE TRENCHING AND MAINTAIN LEVEL OF COVER AS SPECIFIED..
4. ALL DIMENSIONS AND COORDINATES ON THIS DRAWING SHOULD BE SITE VERIFIED PRIOR TO INSTALLATION.
5. THE SIZE OF VENT STACK IS ASSUMED PENDING AVAILABILITY OF DATE FROM PROCESS.

KEYMAP

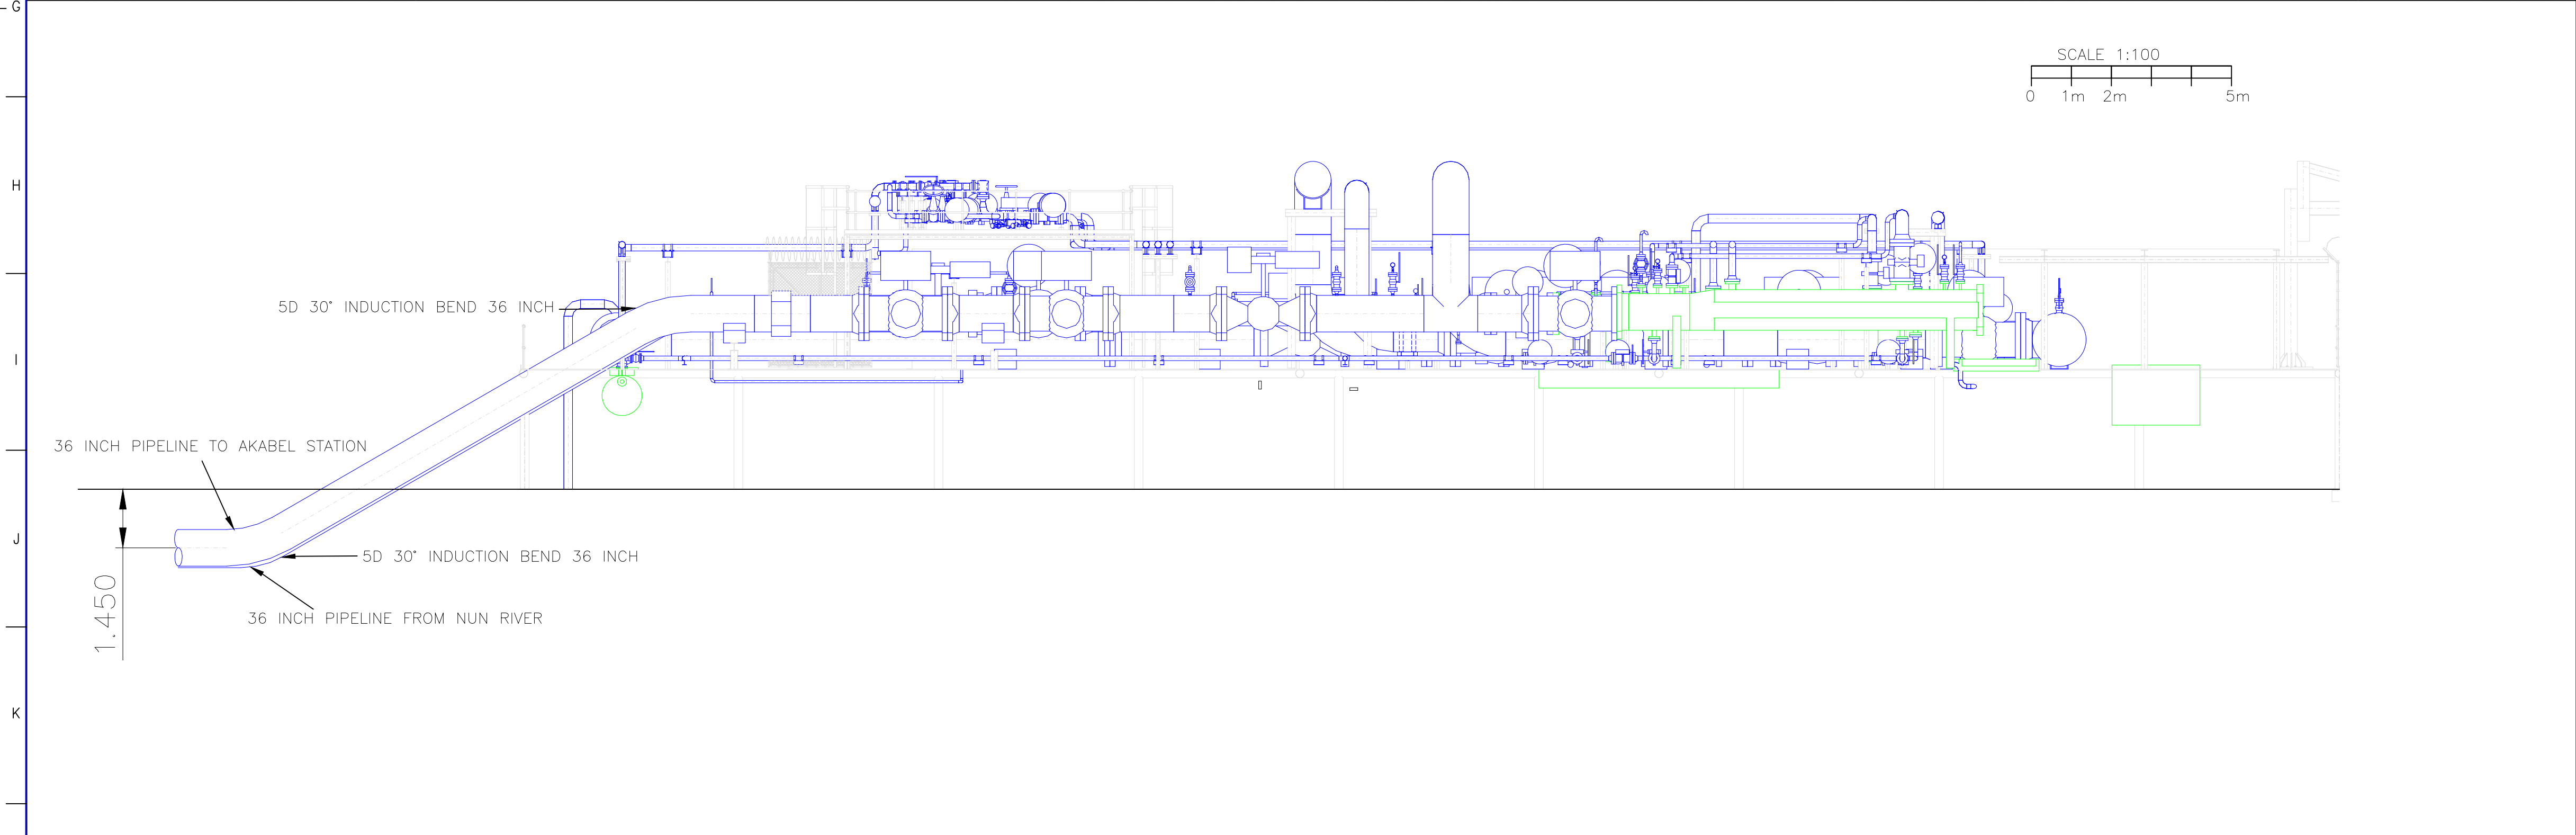

L	REFERENCE DRAWINGS		DRAWING No.		NOTES:							CONTRACTOR 					BRASS FERTILIZER & PETROCHEMICAL COMPANY LIMITED	
																	 GAS PROCESSING AND METHANOL COMPLEX PROJECT FEED FOR GAS GATHERING PIPELINES	
												ENDORSEMENT					LOCATION	
												RELEASED FOR		DESIGN ENGR.	BFPC TECH REP	SPDC TECH REP	DATE	ELEPA MANIFOLD STATION PIPELINE ARRIVAL AND DEPARTURE DRAWING_ELEPA	
M																		DRAWN: SIE					DATE: 26/07/22		SHEET: 1 of 1																																		
												R01		ISSUED FOR REVIEW				SIE	EN	AB	26/07/22					CHECKED: EN		DRAWING No. EA-BFPCL-GPMC-GGPL-FEED-PPL-DWG-011		REV.																													
												REV						DRAWN	CHK	END	DATE					ENDORSED: AB		PROJECT No. 11998A		R01																													
																										APP'D DATE: -		PROJECT No. 11998A																															
												COPY RIGHT RESERVED	
1		2		3		4		5		6		7		8		9		10		11		12		13		14		15		16		17		18		19																							