


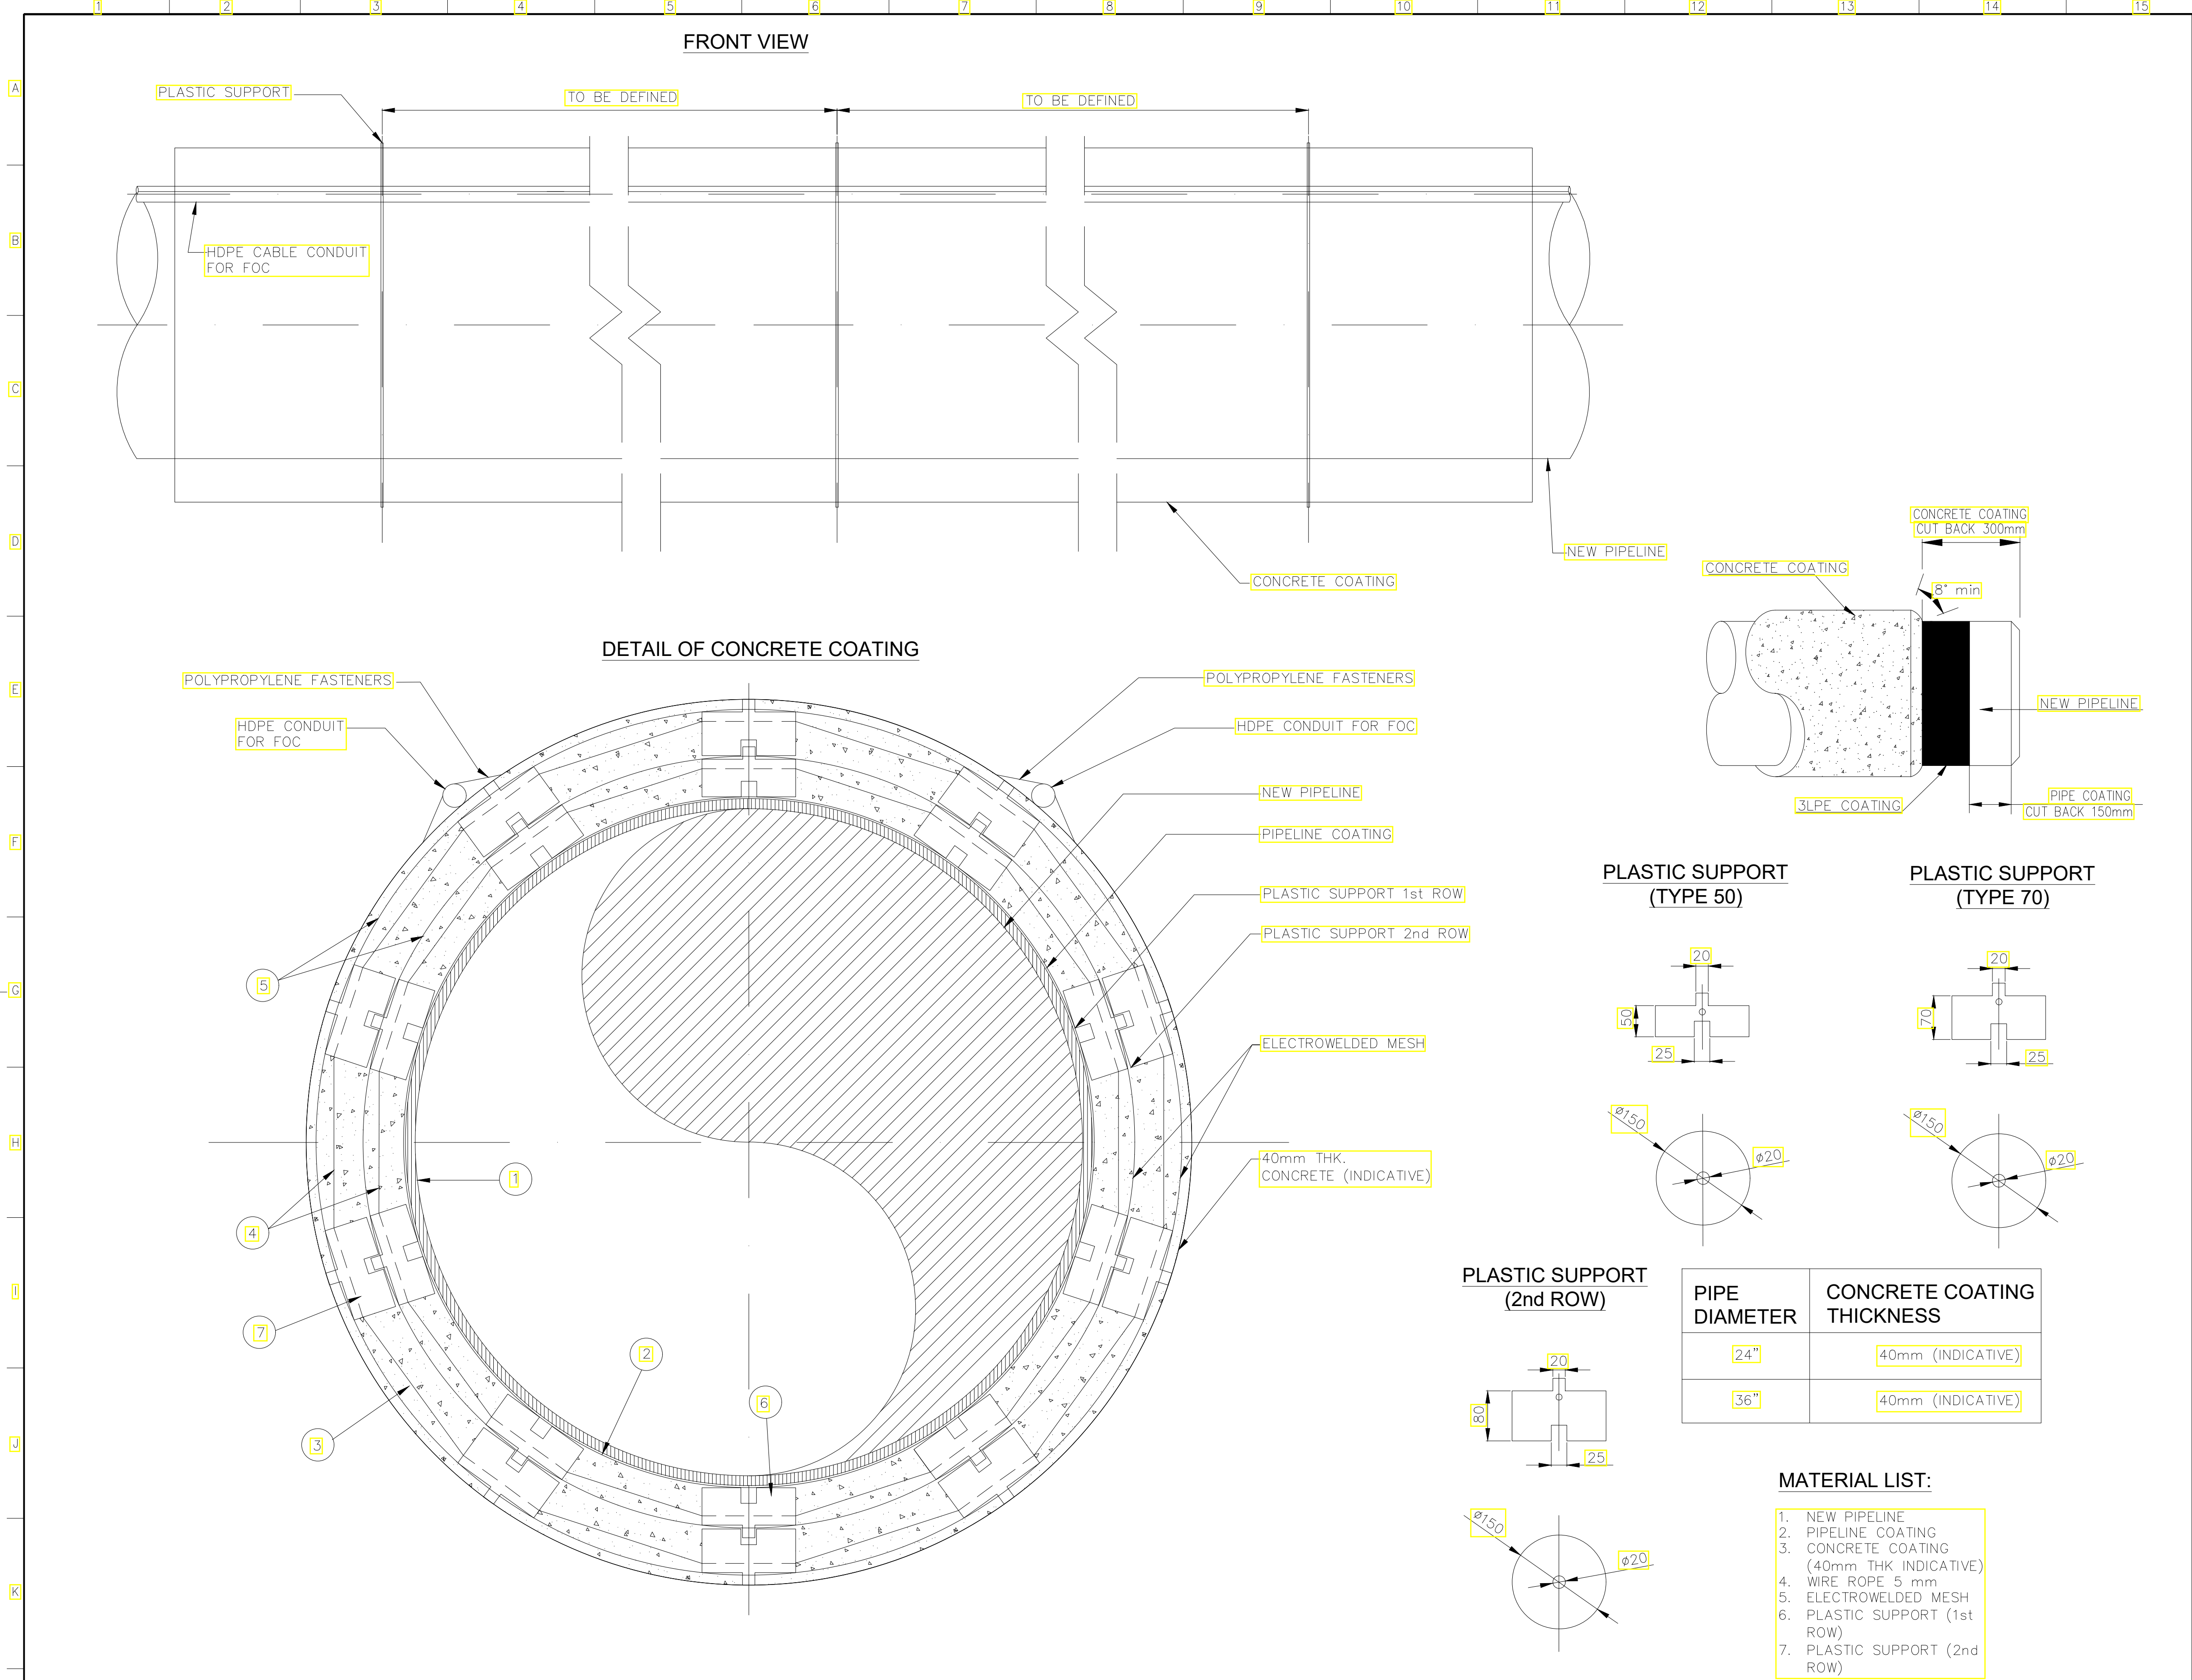

- NOTES:**
- ALL DIMENSIONS ARE IN MILLIMETERS, UNLESS STATED OTHERWISE.
 - PLASTIC SUPPORTS SHALL BE PREPARED IN PVC OR HDPE.
 - THE EXTREMITIES OF ELECTROWELDED MESH AND WIRE ROPE MUST BE CUTTED IN CORRESPONDENCE OF BARE PIPE ENDS.
 - THE CONCRETE MUST BE ADHERENT WITH CONTINUITY TO THE PIPELINE AND MUST HAVE A CONSTANT THICKNESS.
 - AT LEAST 150mm FROM THE PIPE COATING ENDS MUST BE LEFT WITHOUT CONCRETE.
 - THE PIPELINE COATING MUST BE TESTED WITH HOLIDAY DETECTOR BEFORE THE APPLICATION OF CONCRETE.
 - ALL CONCRETE SHOULD BE 4000 PSI (28 MPA) CYLINDER STRENGTH AT 28 DAYS.
 - ORDINARY PORTLAND CEMENT, CONFORMING TO BS-12/PS-232 SHALL BE USED IN ALL CONCRETE WORKS EXCEPT WHERE AS SPECIFIED BY THE ENGINEER.
 - SAND FROM APPROVED QUARRIES/SOURCES SHALL BE USED.
 - WELL GRADED CRUSHED STONE FROM APPROVED QUARRIES/SOURCES SHALL BE USED AS COARSE AGGREGATE. MAXIMUM NOMINAL SIZE OF THE COARSE AGGREGATE SHALL BE 3/4" (20 MM).
 - POTABLE WATER SHALL BE USED FOR CONCRETE AND SHALL BE FREE OF ORGANIC AND OTHER IMPURITIES.
 - THE THICKNESS OF CONCRETE WEIGHT COATING SHALL BE AS INDICATED IN RELEVANT ALIGNMENT SHEET.
 - ELECTROWELDED MESH WITH SQUARE MESH 10x10mm WIRE $\phi 6$ mm.

REFERENCE DRAWINGS		DRAWING No.	NOTES:		CONTRACTOR					BRASS FERTILIZER & PETROCHEMICAL COMPANY LIMITED				
					epic ATLANTIC					brass fertilizer GAS PROCESSING AND METHANOL COMPLEX PROJECT FEED FOR GAS GATHERING PIPELINES				
					ENDORSEMENT					LOCATION BOBOUWE BOU MANIFOLD, ELEPA MANIFOLD STATION AND AKABEL STATION				
					RELEASED FOR DESIGN ENGR. BFPC TECH REP SPDC TECH REP DATE					TYPICAL CONCRETE WEIGHT COATING DRAWING				
					R01 ISSUED FOR REVIEW SIE EN AB 01/06/22					DRAWN: SIE DATE: 01/06/22 SHEET: 1 of 1				
					REV DRAWN CHK END DATE					CHECKED: EN DRAWING No. EA-BFCL-GPMC-GGPL-FEED-PPL-DWG-015 REV.				
					COPY RIGHT RESERVED					ENDORSED: AB PROJECT No. 11998A				
										APP'D. DATE: PROJECT No. 11998A R01				