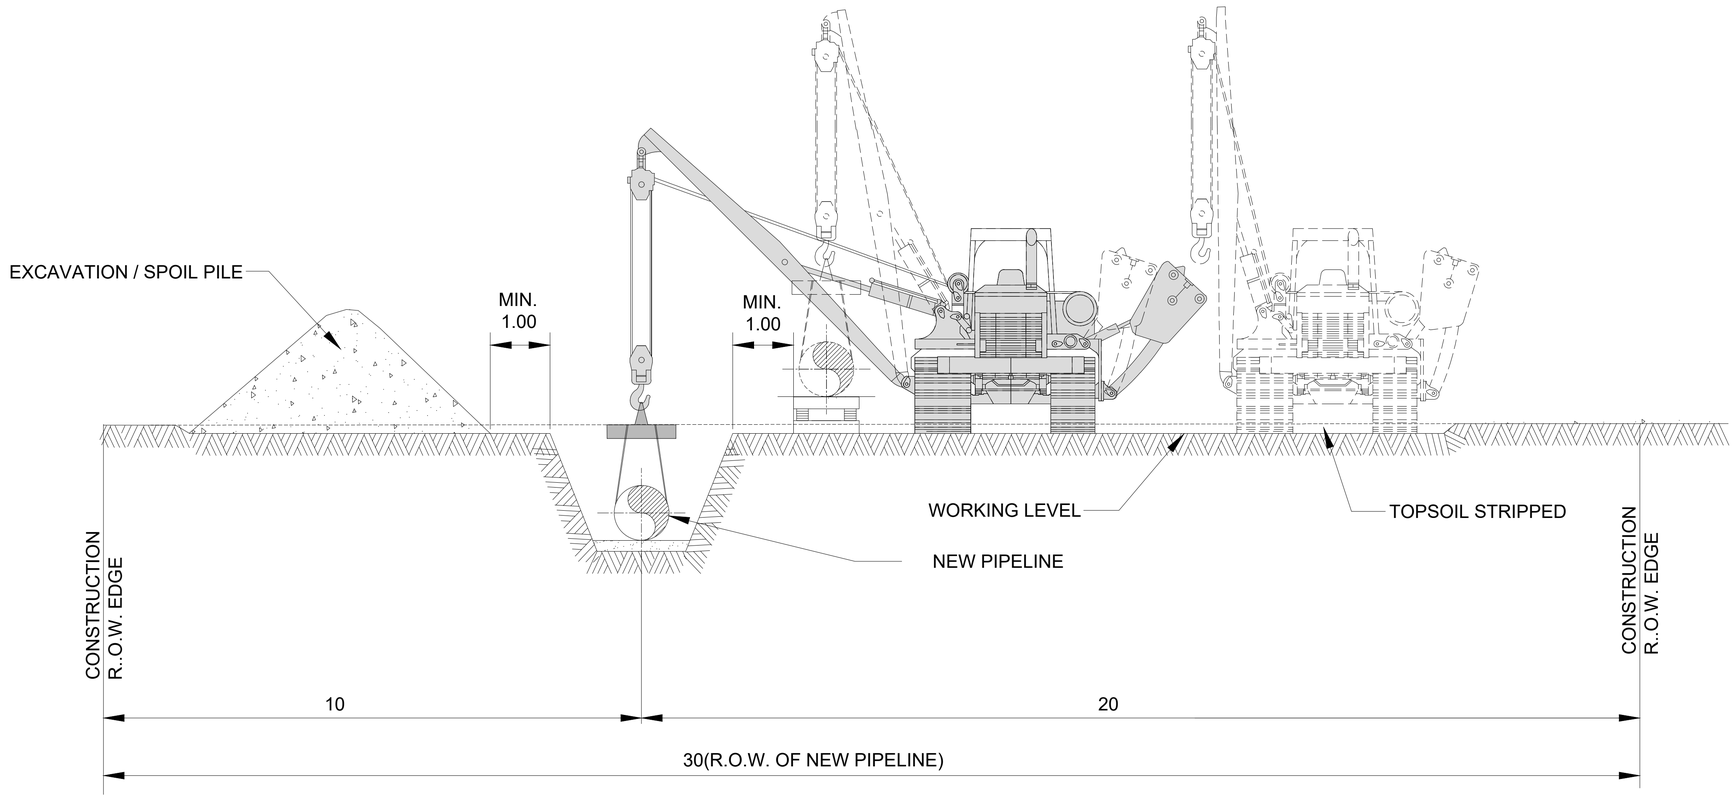


NOTES:

1. ALL DIMENSIONS IN METERS, UNLESS STATED OTHERWISE.
2. TOPSOIL SHALL BE STRIPPED TO ENTIRE DEPTH (DEPENDING ON LOCAL CONDITIONS).
3. PRIOR TO INSTALLATION, ALL DIMENSIONS SHOULD BE SITE VERIFIED BY THE INSTALLATION CONTRACTOR.

WORKING STRIP OF NEW PIPELINE R.O.W.

REFERENCE DRAWINGS	DRAWING No.	NOTES:

REV		DRAWN	CHK	END	DATE
R01	ISSUED FOR REVIEW	SIE	EN	AB	25/05/22

COPY RIGHT RESERVED

CONTRACTOR

ENDORSEMENT

RELEASED FOR	DESIGN ENGR.	BFPC TECH REP	SPDC TECH REP	DATE
–	–	–	–	–

BRASS FERTILIZER & PETROCHEMICAL COMPANY LIMITED

GAS PROCESSING AND METHANOL COMPLEX PROJECT
FEED FOR GAS GATHERING PIPELINES

LOCATION
BOBOUWE BOU MANIFOLD, ELEPA MANIFOLD STATION AND AKABEL STATION
TYPICAL ROW INSTALLATION–NEW ROUTE

DRAWN: SIE	DATE: 25/05/22	SHEET: 1 of 1	
CHECKED: EN	DRAWING No. EA-BFPCL-GPMC-GGPL-FEED-PPL-DWG-008		REV.
ENDORSED: AB	PROJECT No. 11998A		0
APP'D DATE: –	PROJECT No. 11998A		